


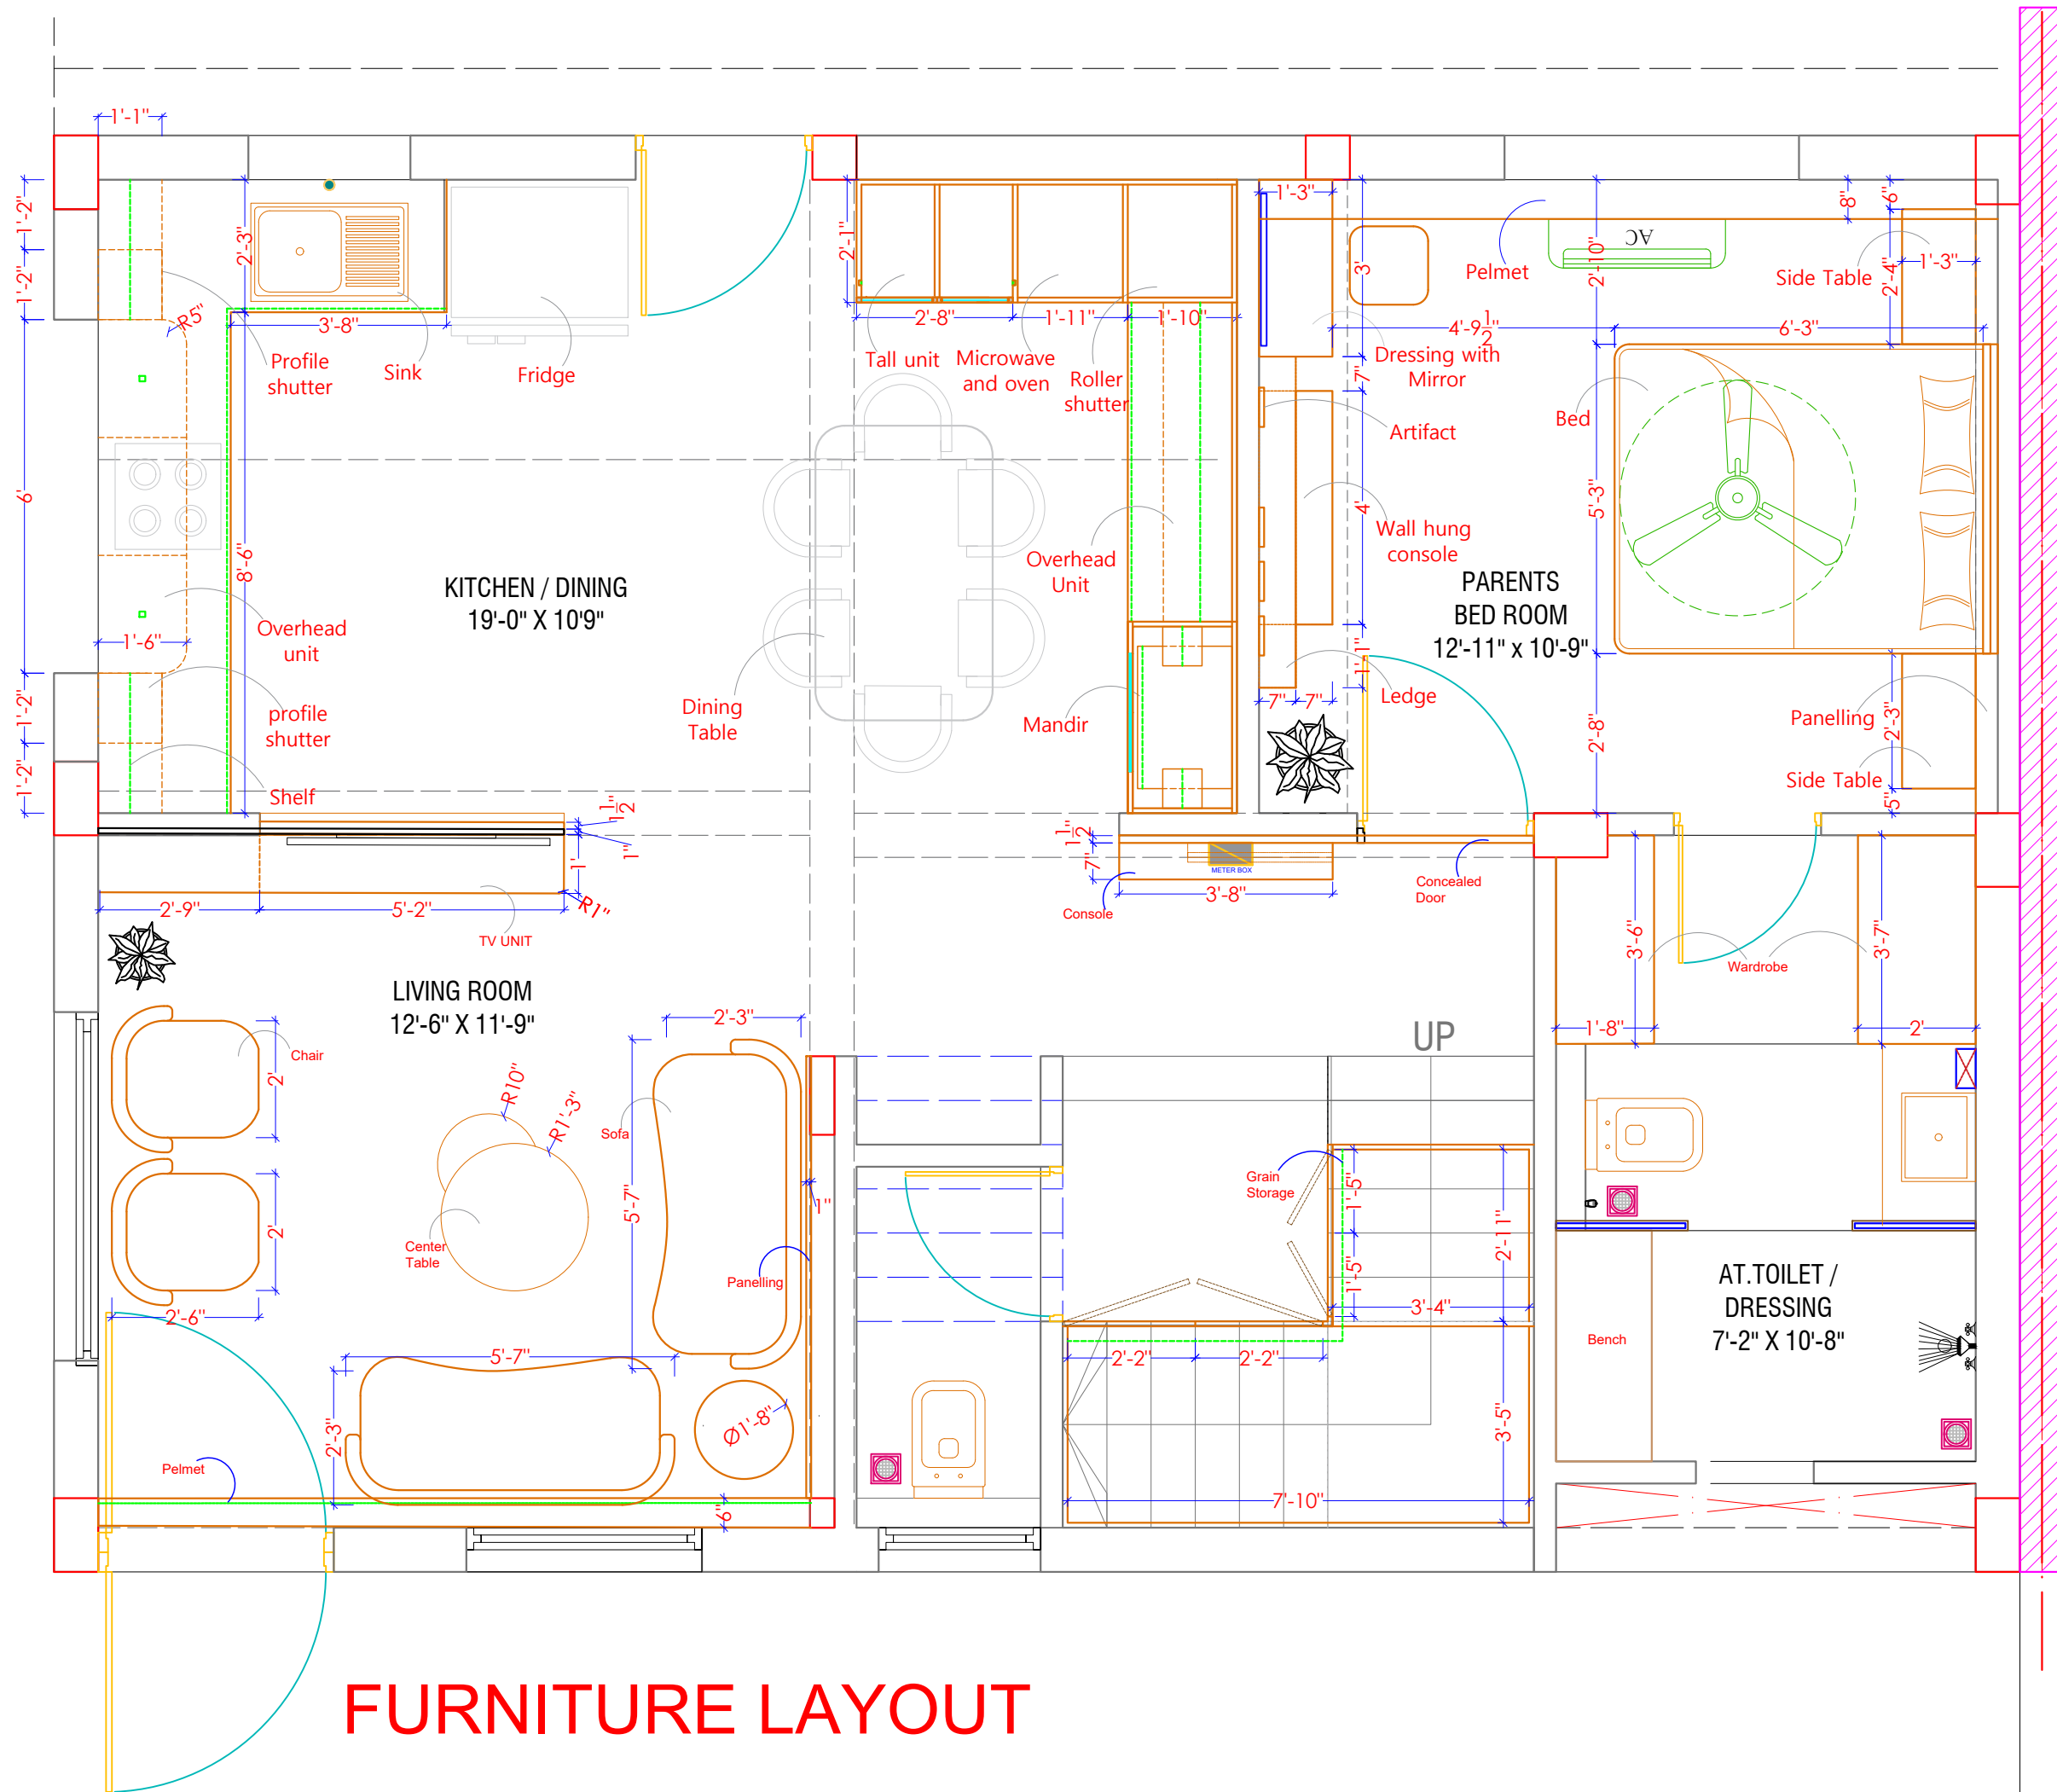

FURNITURE LAYOUT

NOTES:

- * DO NOT SCALE THE DRAWING.
- * ALL DIMENSIONS ARE IN FEET \ INCHES.
- * ANY DISCREPANCY IN THE DRAWING TO BE BROUGHT IN THE DESIGNER'S NOTICE BEFORE IMPLEMENTATION ON SITE.

DRAWING TITLE :
LIVING ROOM
FURNITURE LAYOUT

SITE ADDRESS:

SAVAD
VADODARA

CLIENT NAME:

RONAK PANCHOLI

DATE:

02-06-2025

NORTH:




DRAWING DETAIL

REVISION NO.	R1	R2	R3
REVISED DATE:	12/02/26		
SCALE:	N.T.S		
DRAWN BY:	ARCHANA		
CHECKED BY:	MITTAL		

	www.mayaspace.studio
	mayaspace.studio@gmail.com
	+918980144077
	@mayaspace.studio



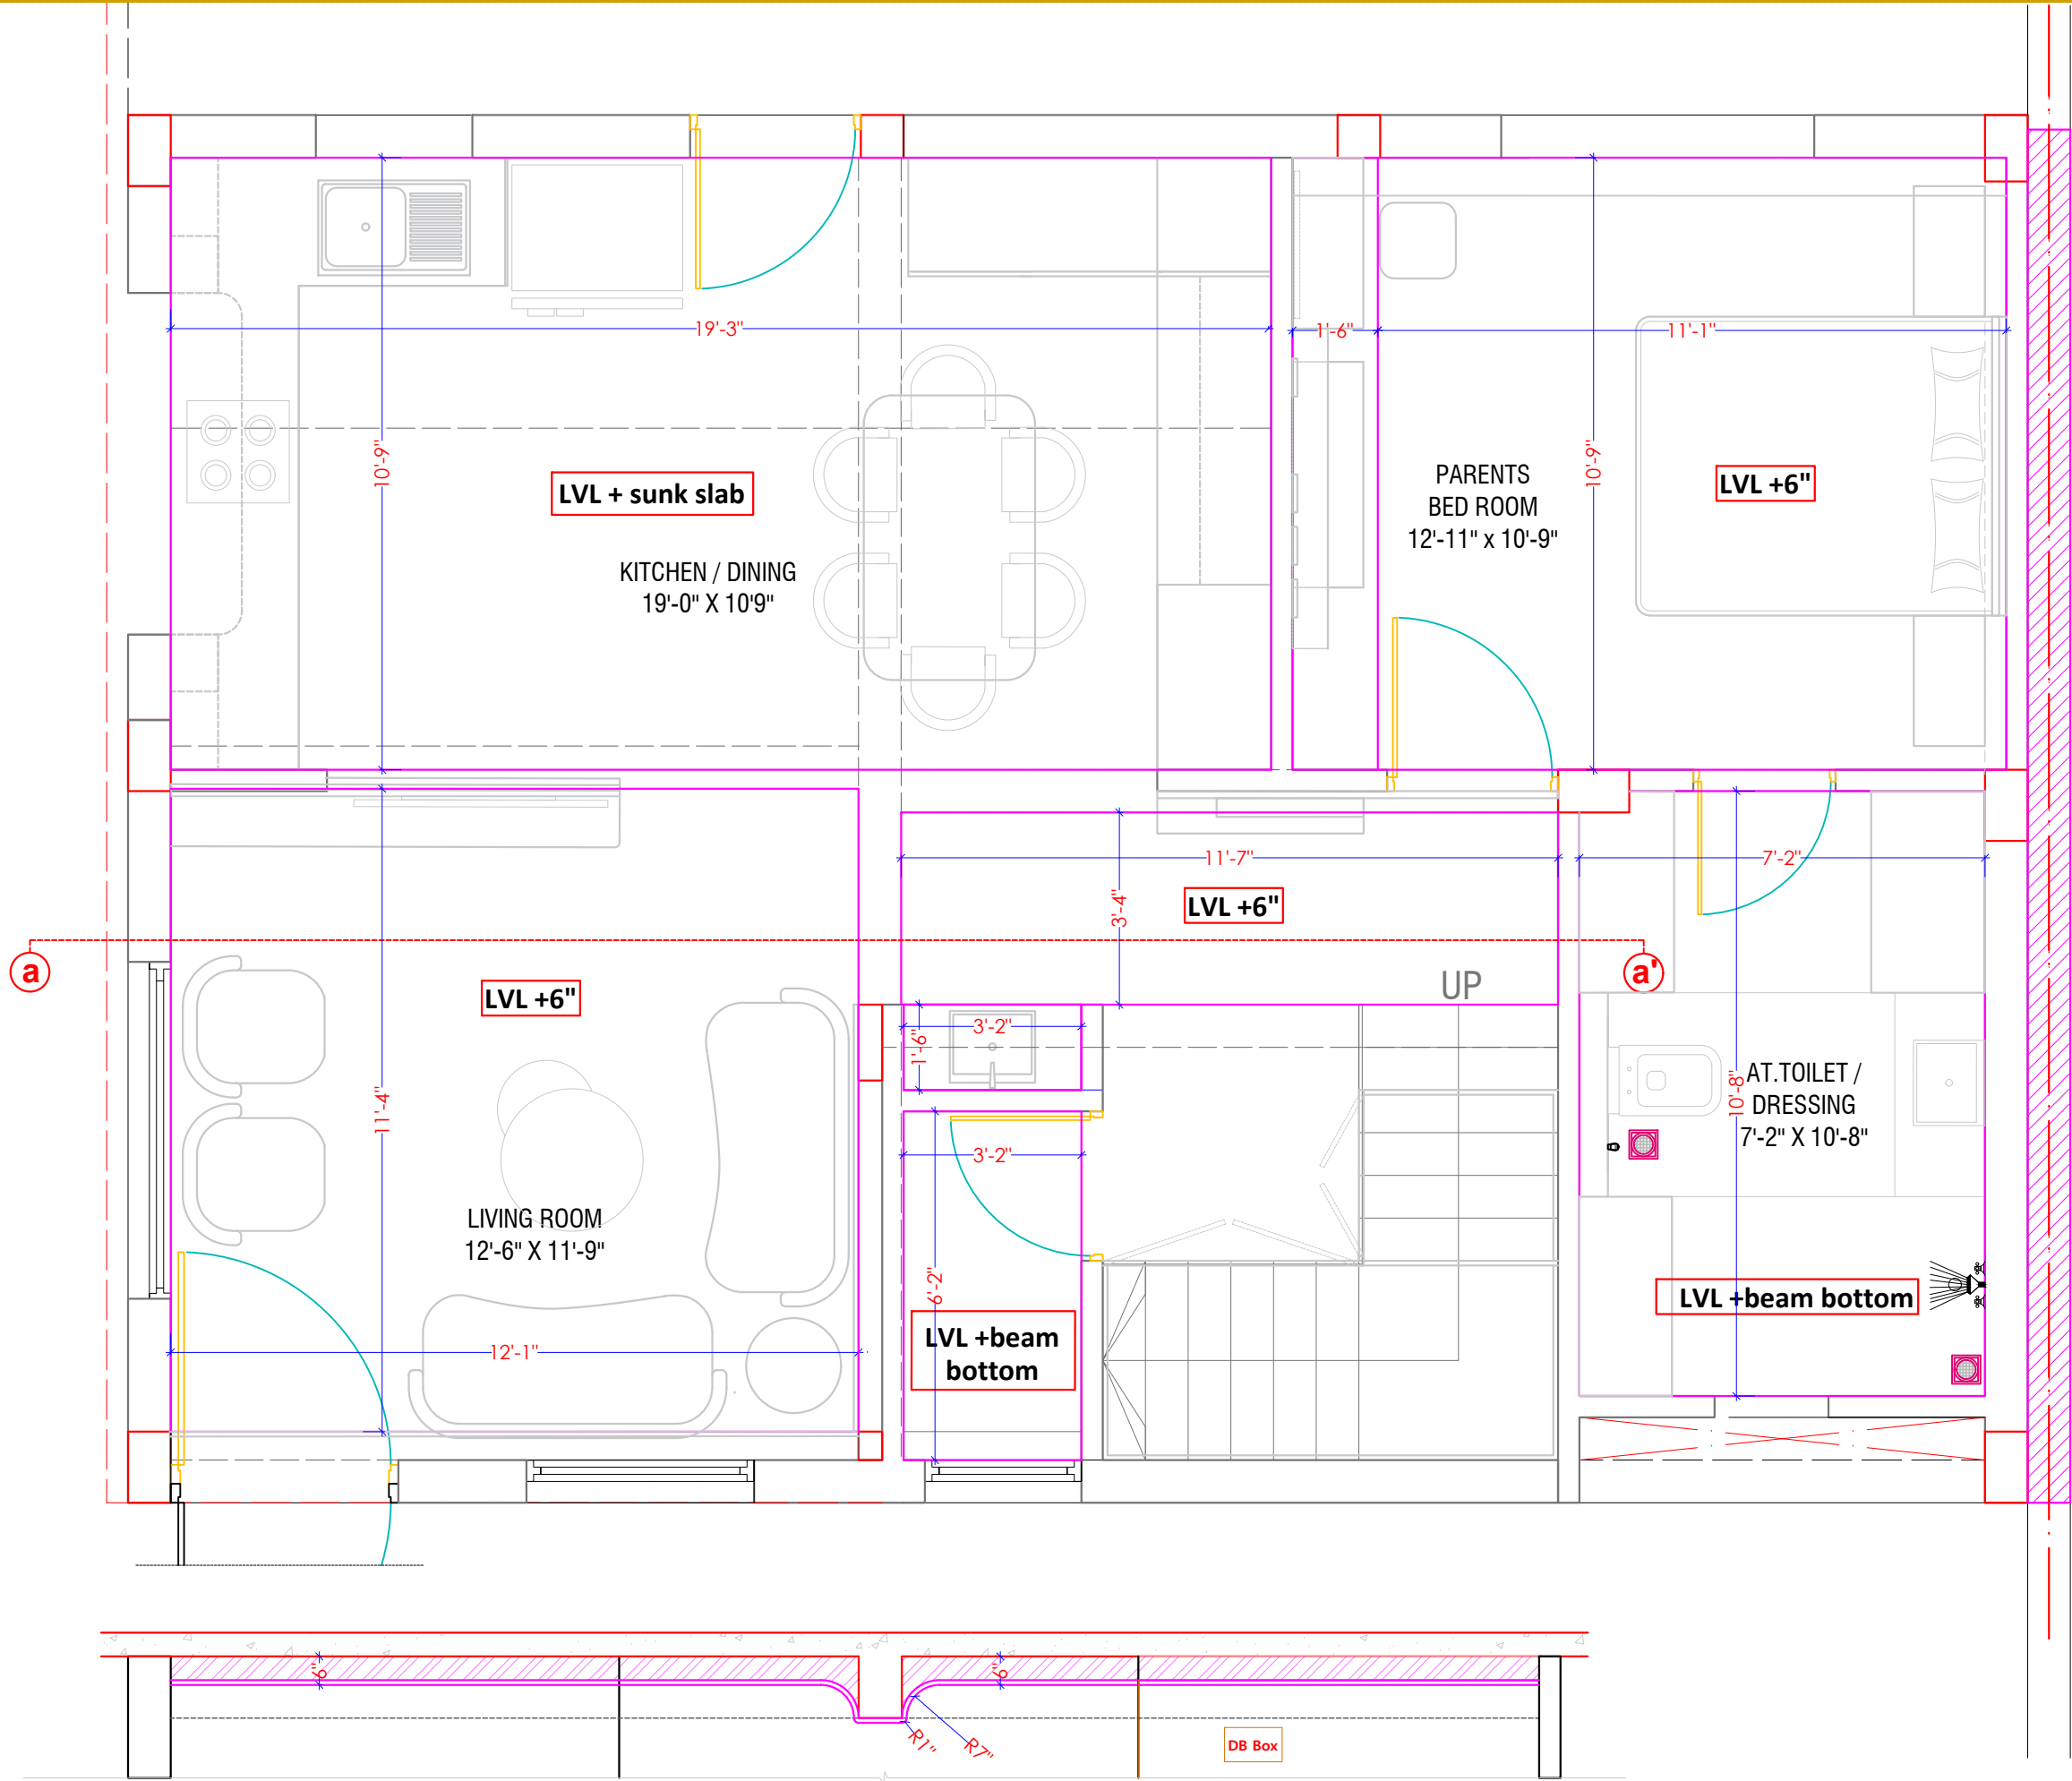

FALSE CEILING LAYOUT

DRAWING TITLE :

LIVING ROOM
FALSE CEILING LAYOUT

NOTES:

- * DO NOT SCALE THE DRAWING.
- * ALL DIMENSIONS ARE IN FEET \ INCHES.
- * ANY DISCREPANCY IN THE DRAWING TO BE BROUGHT IN THE DESIGNER'S NOTICE BEFORE IMPLEMENTATION ON SITE.

SITE ADDRESS:

SAVAD
VADODARA

CLIENT NAME:

RONAK PANCHOLI

DATE: 02-06-2025


NORTH:

DRAWING DETAIL

REVISION NO.	R1	R2	R3
REVISED DATE:	12/02/26		
SCALE:	N.T.S		
DRAWN BY:	ARCHANA		
CHECKED BY:	MITTAL		

- www.mayaspace.studio
- mayaspace.studio@gmail.com
- +918980144077
- @mayaspace.studio



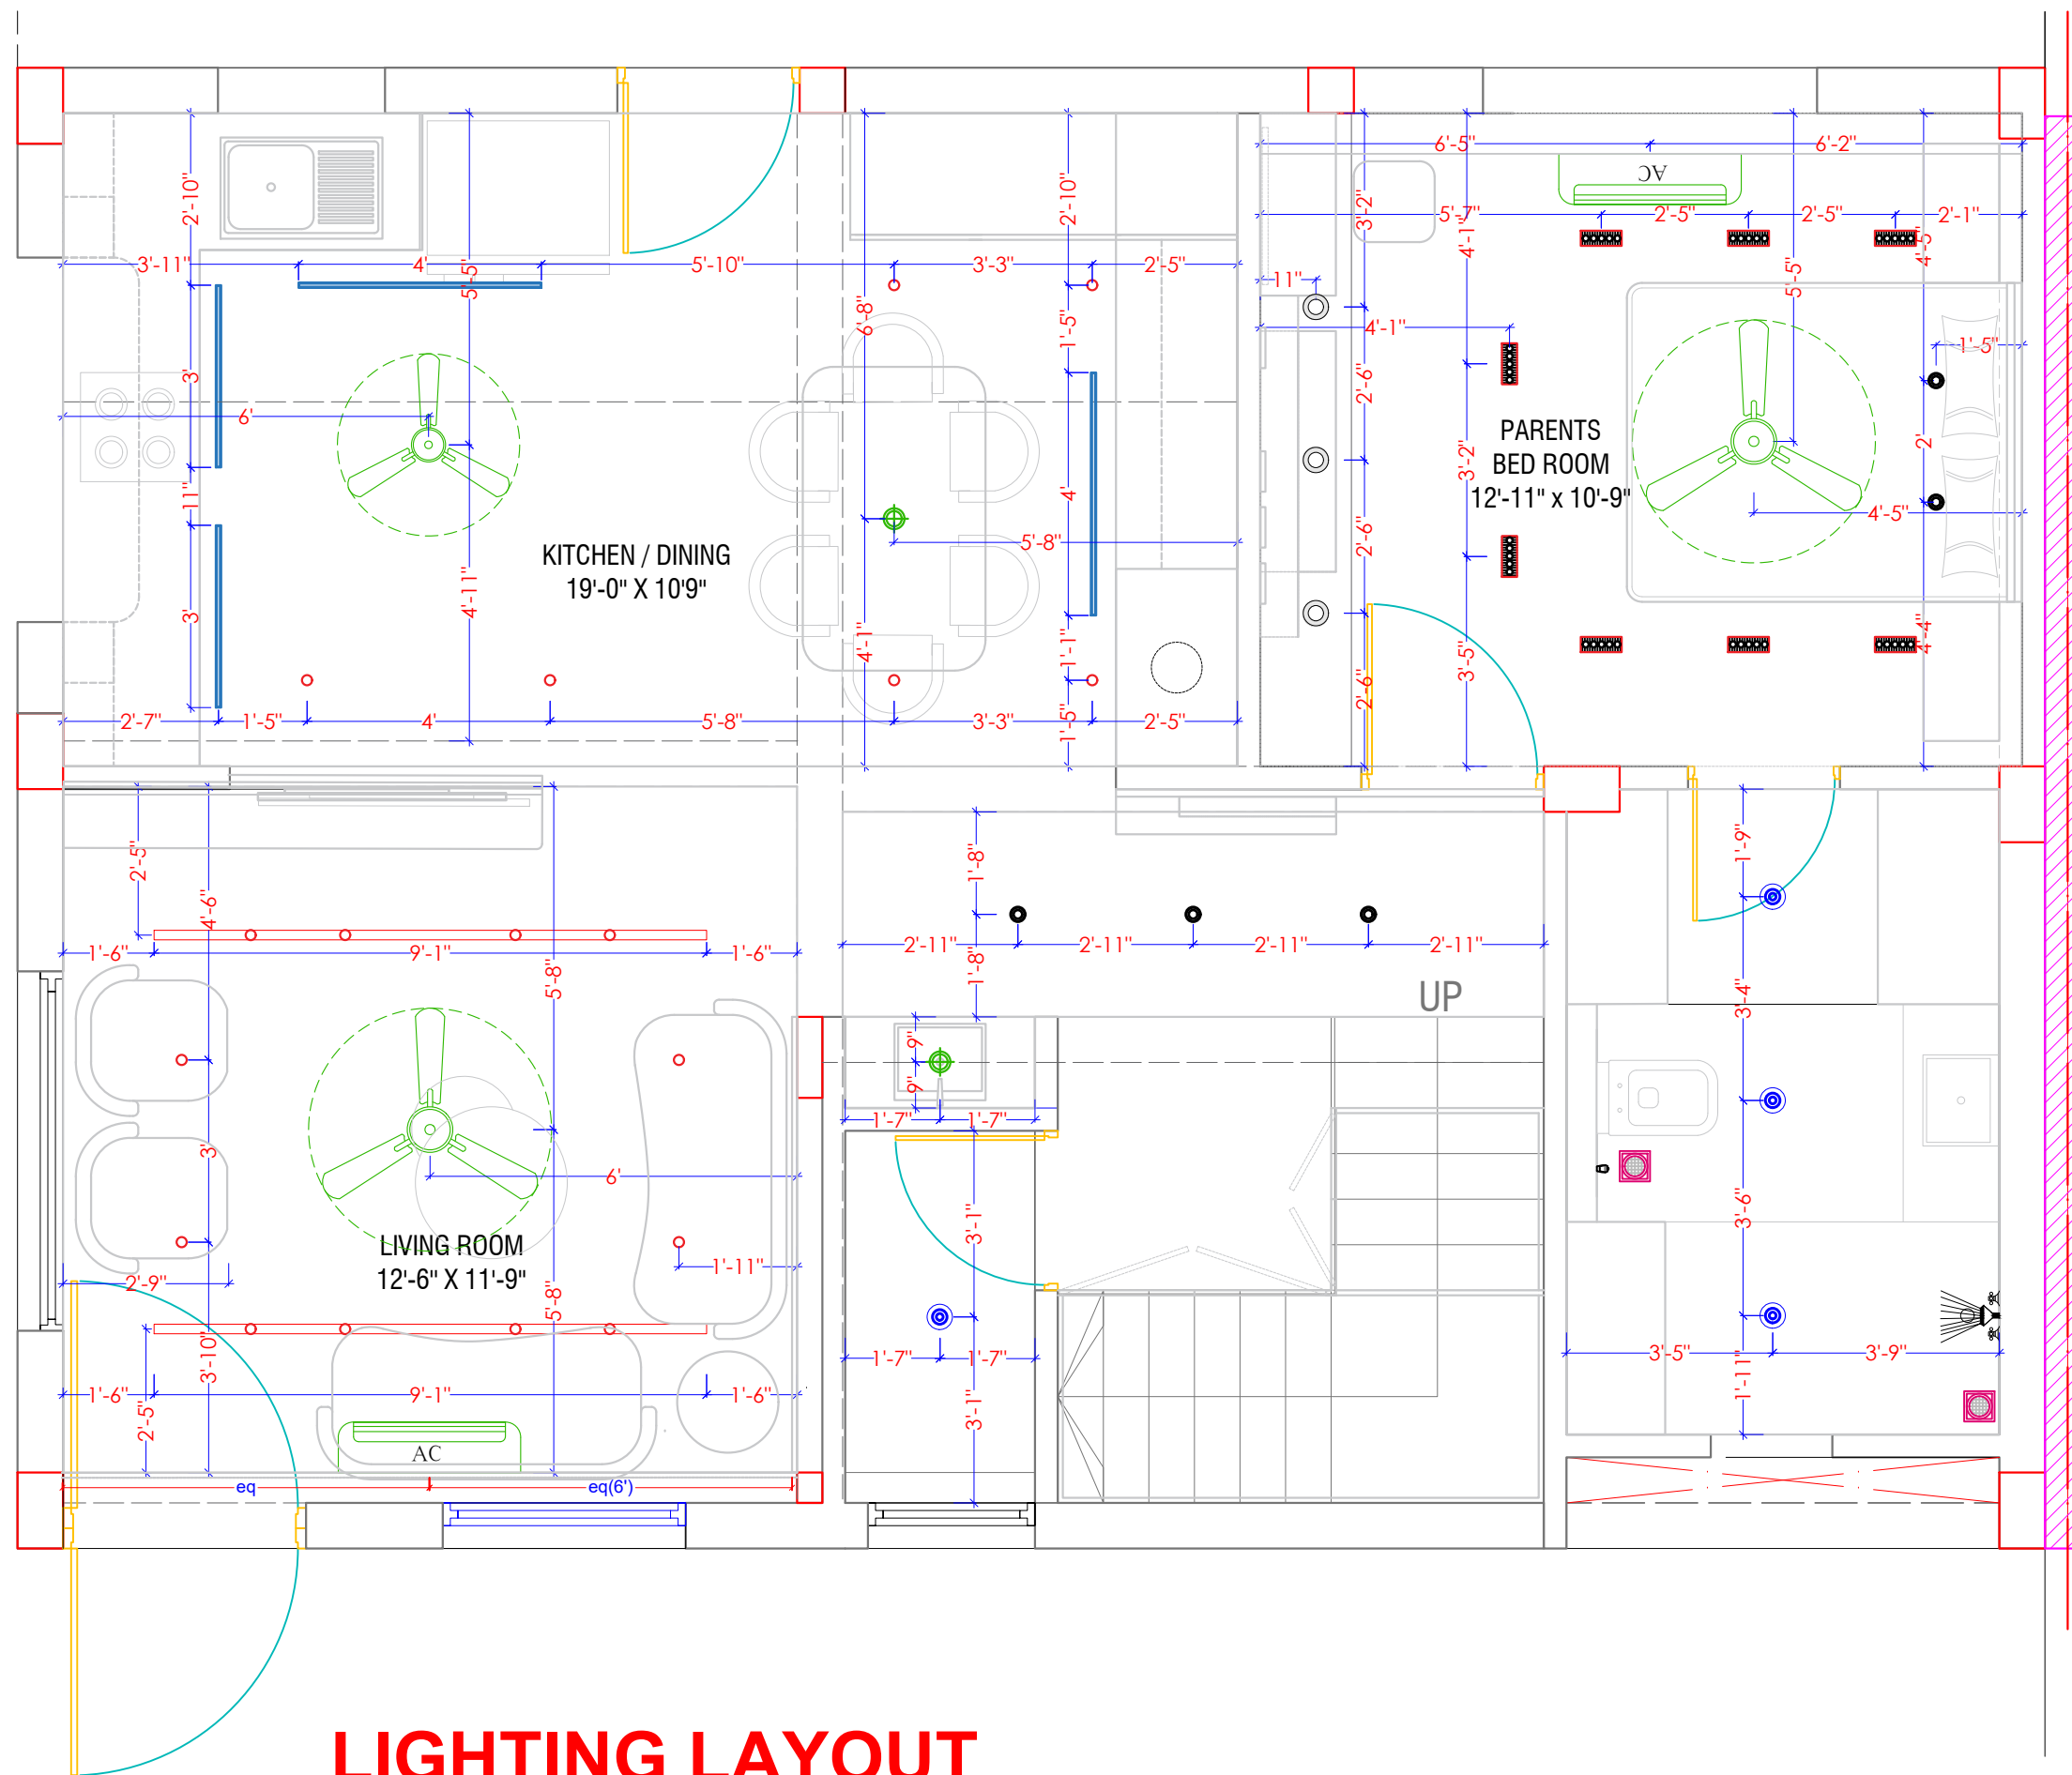

LIGHTING LAYOUT

LEGENDS	
	pin lights 10 WATT
	pop-outs 5 WATT
	Indirect light
	Laser blade 10 WATT
	SPOT light
	Hanging light
	Profile light 17 mm
	cylinder
	Foot lamp
	Switch board
	Wall point
	A/C
	Wi-Fi point
	FAN
	COB

DRAWING TITLE :

LIVING ROOM
LIGHTING LAYOUT

NOTES:

* DO NOT SCALE THE DRAWING.
* ALL DIMENSIONS ARE IN FEET \ INCHES.
* ANY DISCREPENCY IN THE DRAWING
TO BE BROUGHT IN THE DESIGNER'S
NOTICE BEFORE IMPLEMENTATION
ON SITE.

SITE ADDRESS:

SAVAD
VADODARA

CLIENT NAME:

RONAK PANCHOLI

DATE: 02-06-2025


NORTH:

DRAWING DETAIL

REVISION NO.	R1 R2 R3
REVISED DATE:	12/02/26
SCALE:	N.T.S
DRAWN BY:	ARCHANA
CHECKED BY:	MITTAL

www.mayaspace.studio
 mayaspace.studio@gmail.com
 +918980144077
 @mayaspace.studio



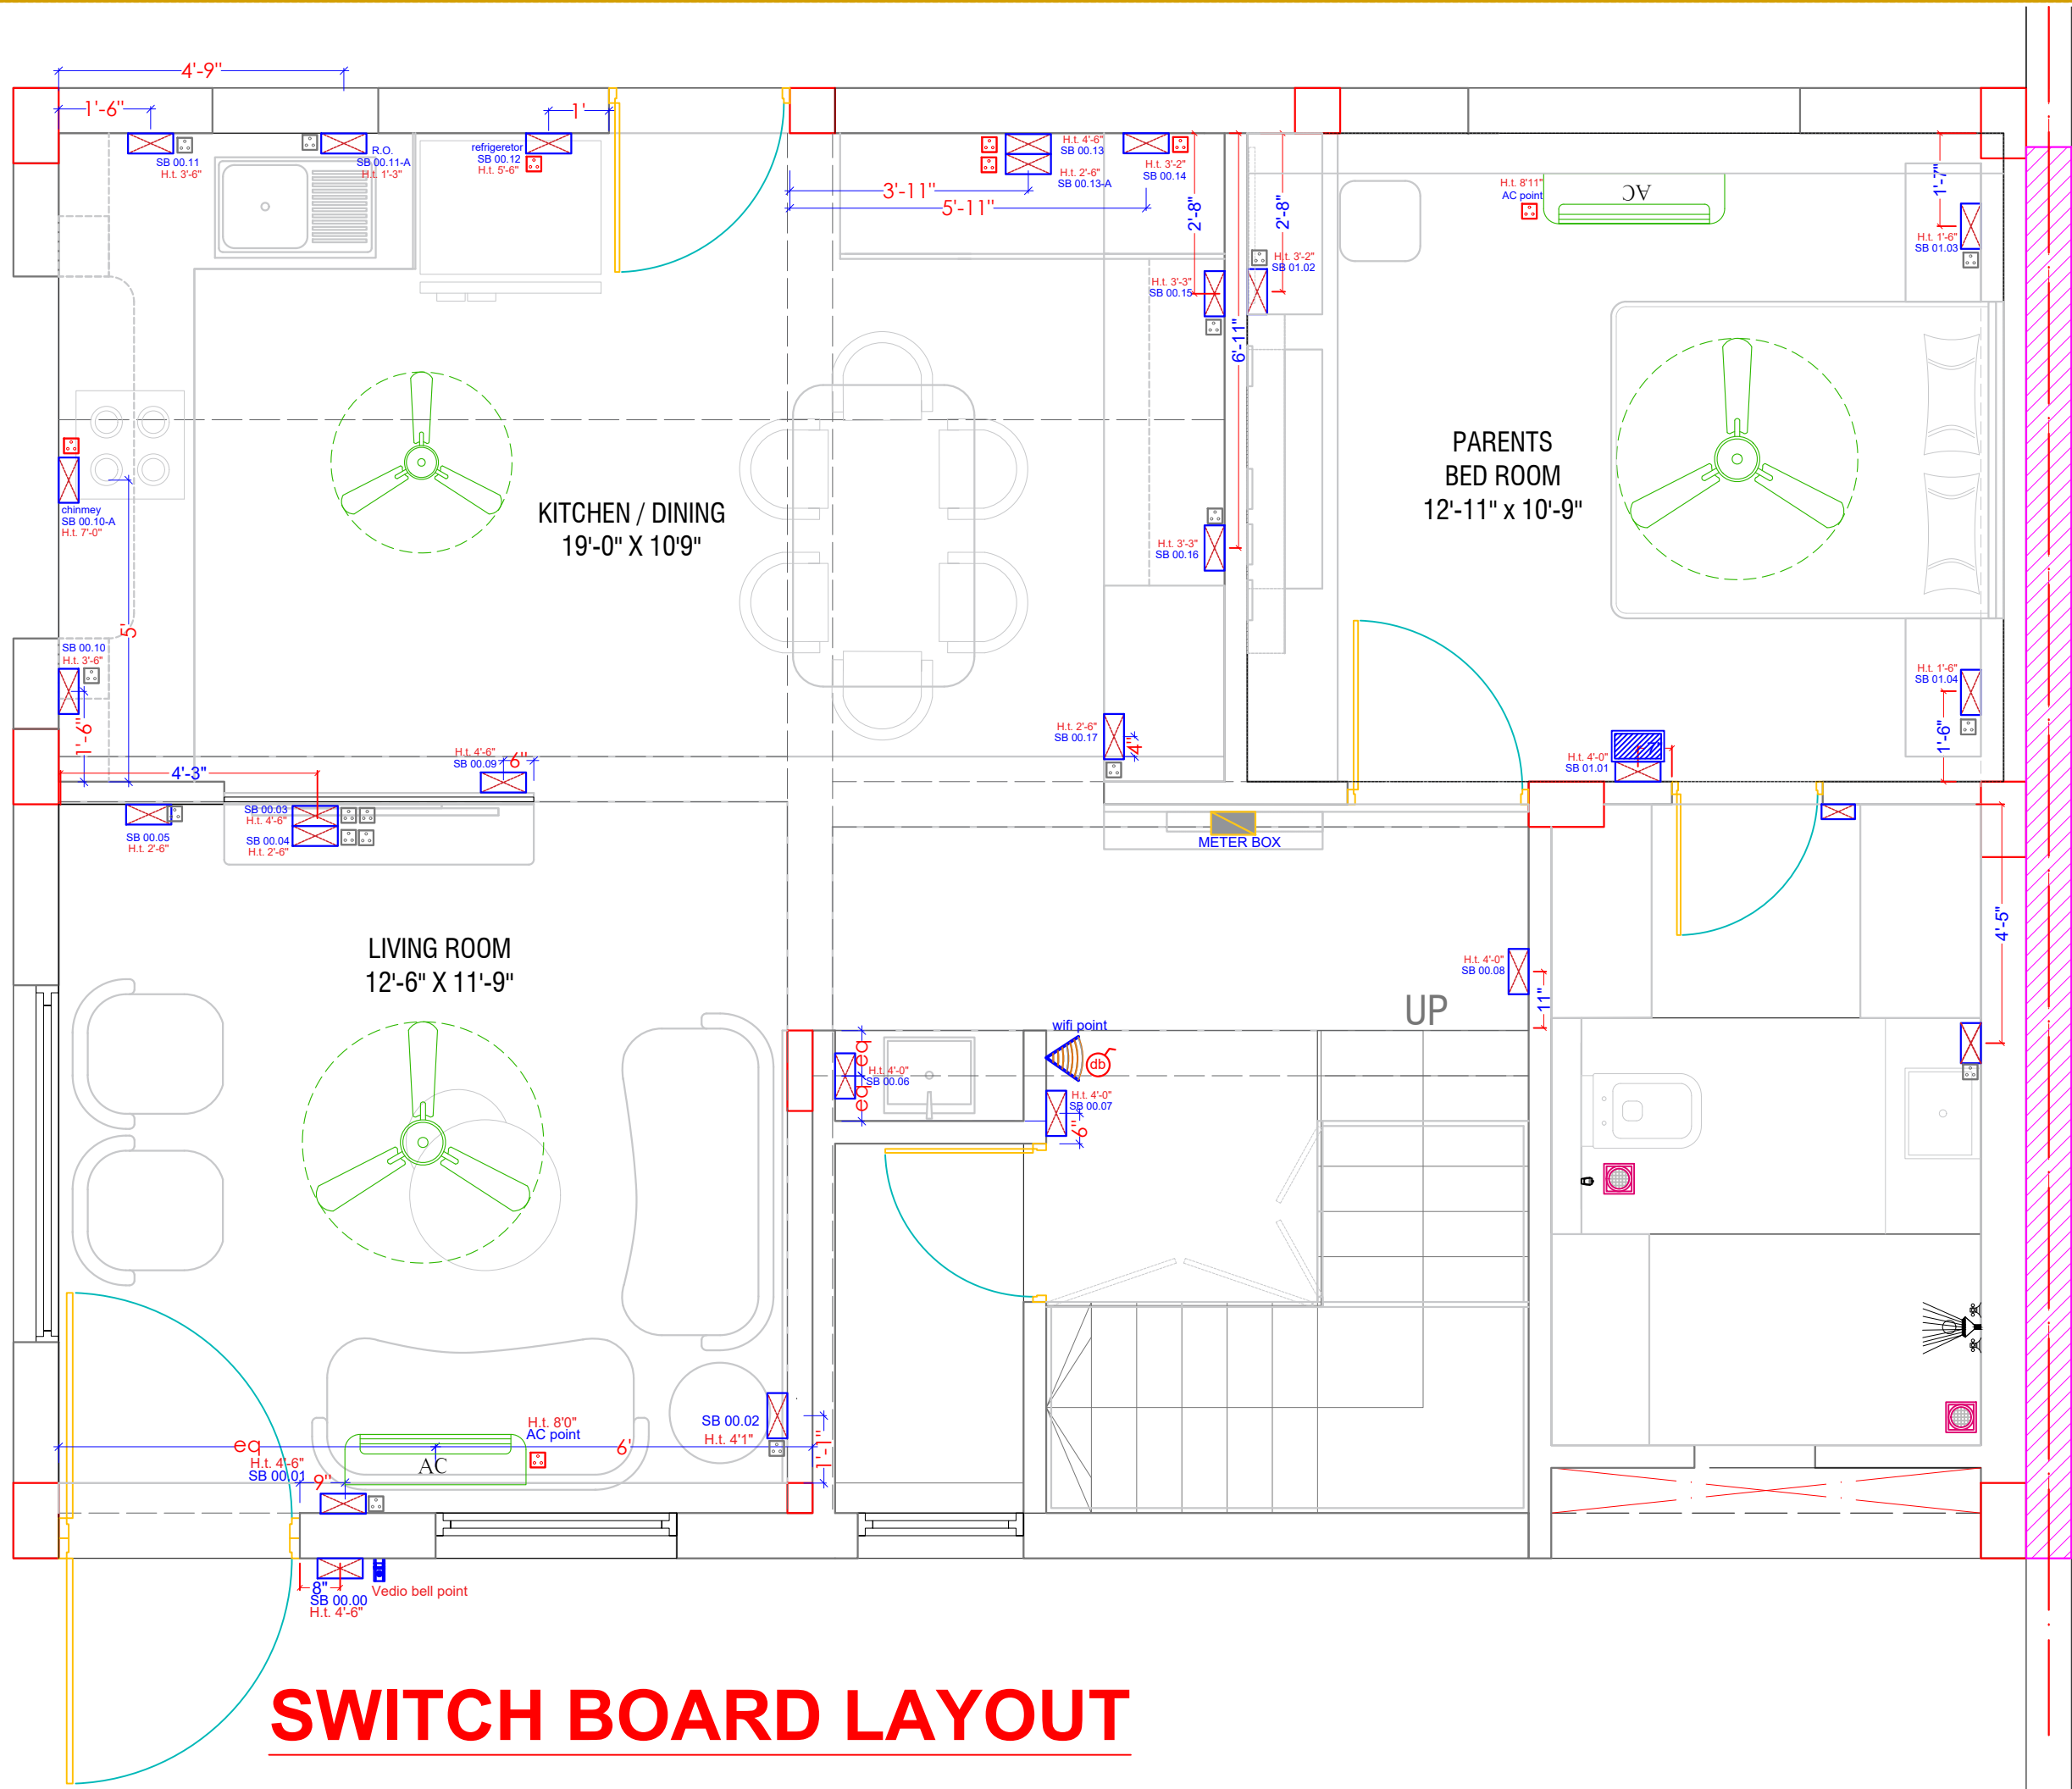

DRAWING TITLE :

LIVING ROOM
SWITCH BOARD LAYOUT

NOTES:

* DO NOT SCALE THE DRAWING.
* ALL DIMENSIONS ARE IN FEET \ INCHES.
* ANY DISCREPENCY IN THE DRAWING TO BE BROUGHT IN THE DESIGNER'S NOTICE BEFORE IMPLEMENTATION ON SITE.

SITE ADDRESS:

SAVAD
VADODARA

CLIENT NAME:


RONAK PANCHOLI

DATE:	02-06-2025
NORTH:	

DRAWING DETAIL			
REVISION NO.	R1	R2	R3
REVISED DATE:	12/02/26		
SCALE:	N.T.S		
DRAWN BY:	ARCHANA		
CHECKED BY:	MITTAL		

- www.mayaspace.studio
- mayaspace.studio@gmail.com
- +918980144077
- @mayaspace.studio



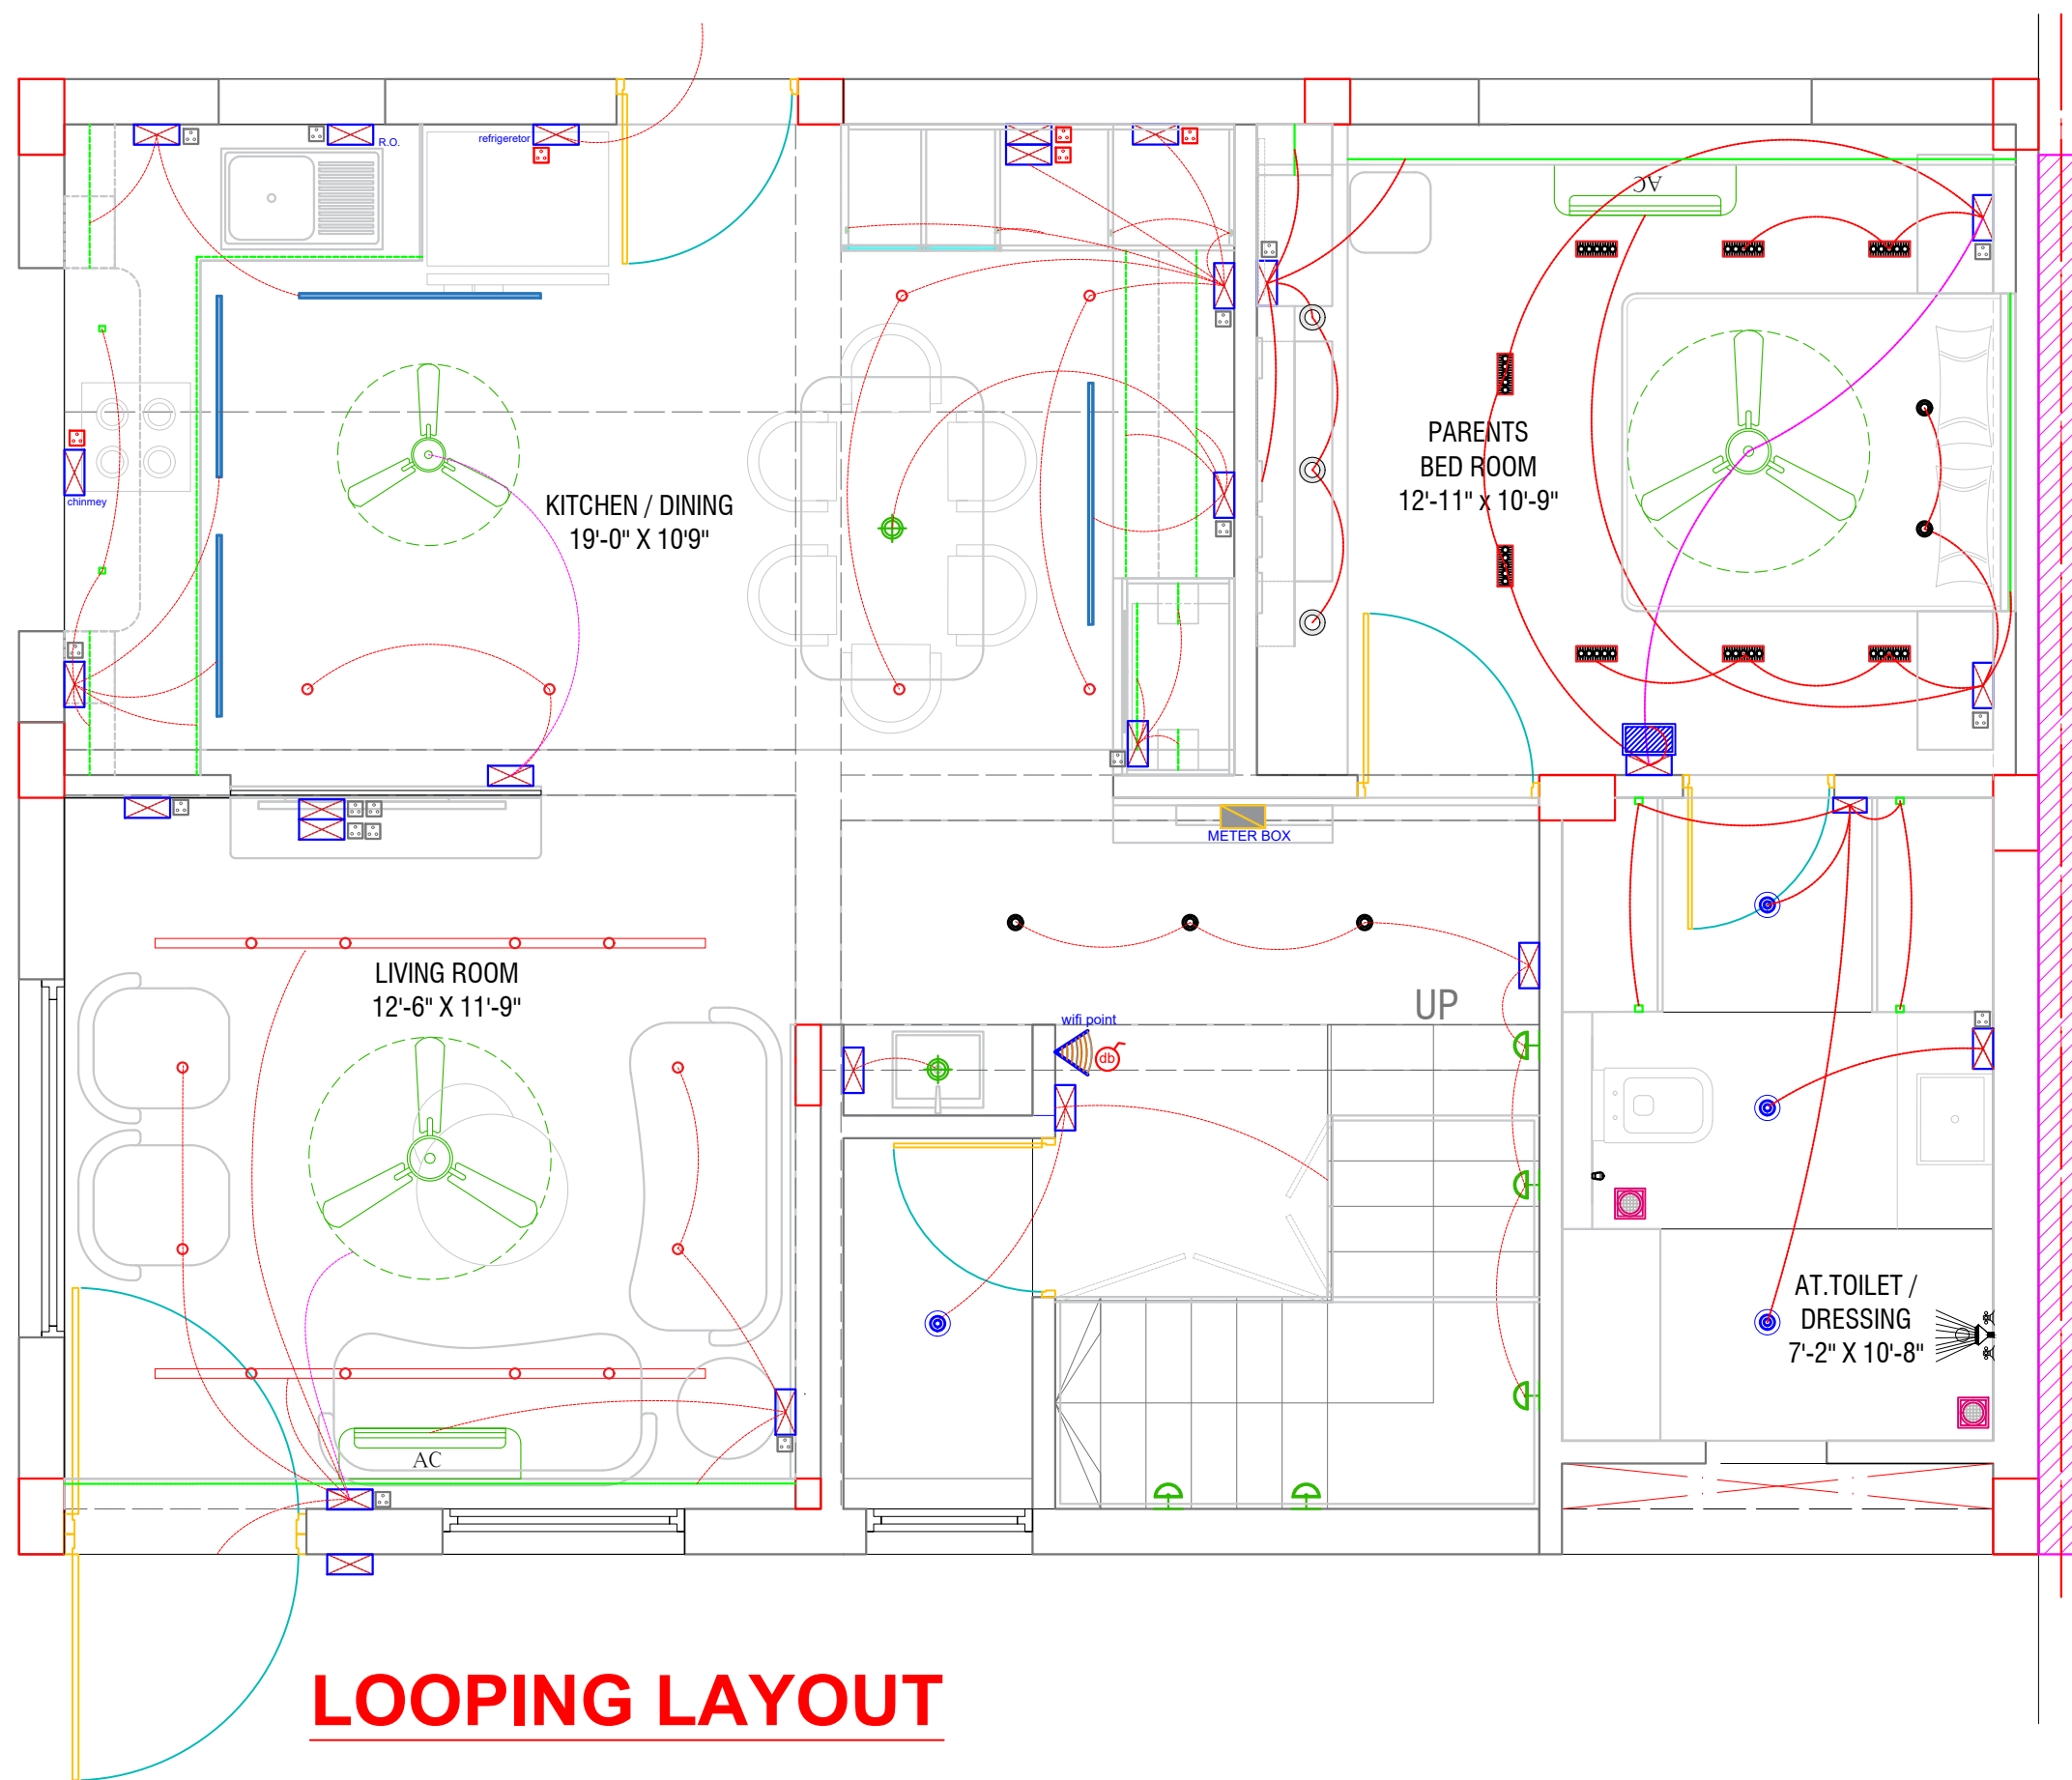

LOOPING LAYOUT

DRAWING TITLE :

LIVING ROOM LOOPING LAYOUT

NOTES:

- * DO NOT SCALE THE DRAWING.
- * ALL DIMENSIONS ARE IN FEET \ INCHES.
- * ANY DISCREPANCY IN THE DRAWING TO BE BROUGHT IN THE DESIGNER'S NOTICE BEFORE IMPLEMENTATION ON SITE.

SITE ADDRESS:

SAVAD
VADODARA

CLIENT NAME:

RONAK PANCHOLI

DATE: 02-06-2025

NORTH:


DRAWING DETAIL

REVISION NO.	R1	R2	R3
REVISED DATE:	12/02/26		
SCALE:	N.T.S		
DRAWN BY:	ARCHANA		
CHECKED BY:	MITTAL		

LEGENDS	
	pin lights 10 WATT
	pop-outs 5 WATT
	Indirect light
	Laser blade 10 WATT
	SPOT light
	Hanging light
	Profile light 17 mm
	cylinder
	Foot lamp
	Switch board
	Wall point
	A/C
	Wi-Fi point
	FAN
	COB

	www.mayaspace.studio
	mayaspace.studio@gmail.com
	+918980144077
	@mayaspace.studio



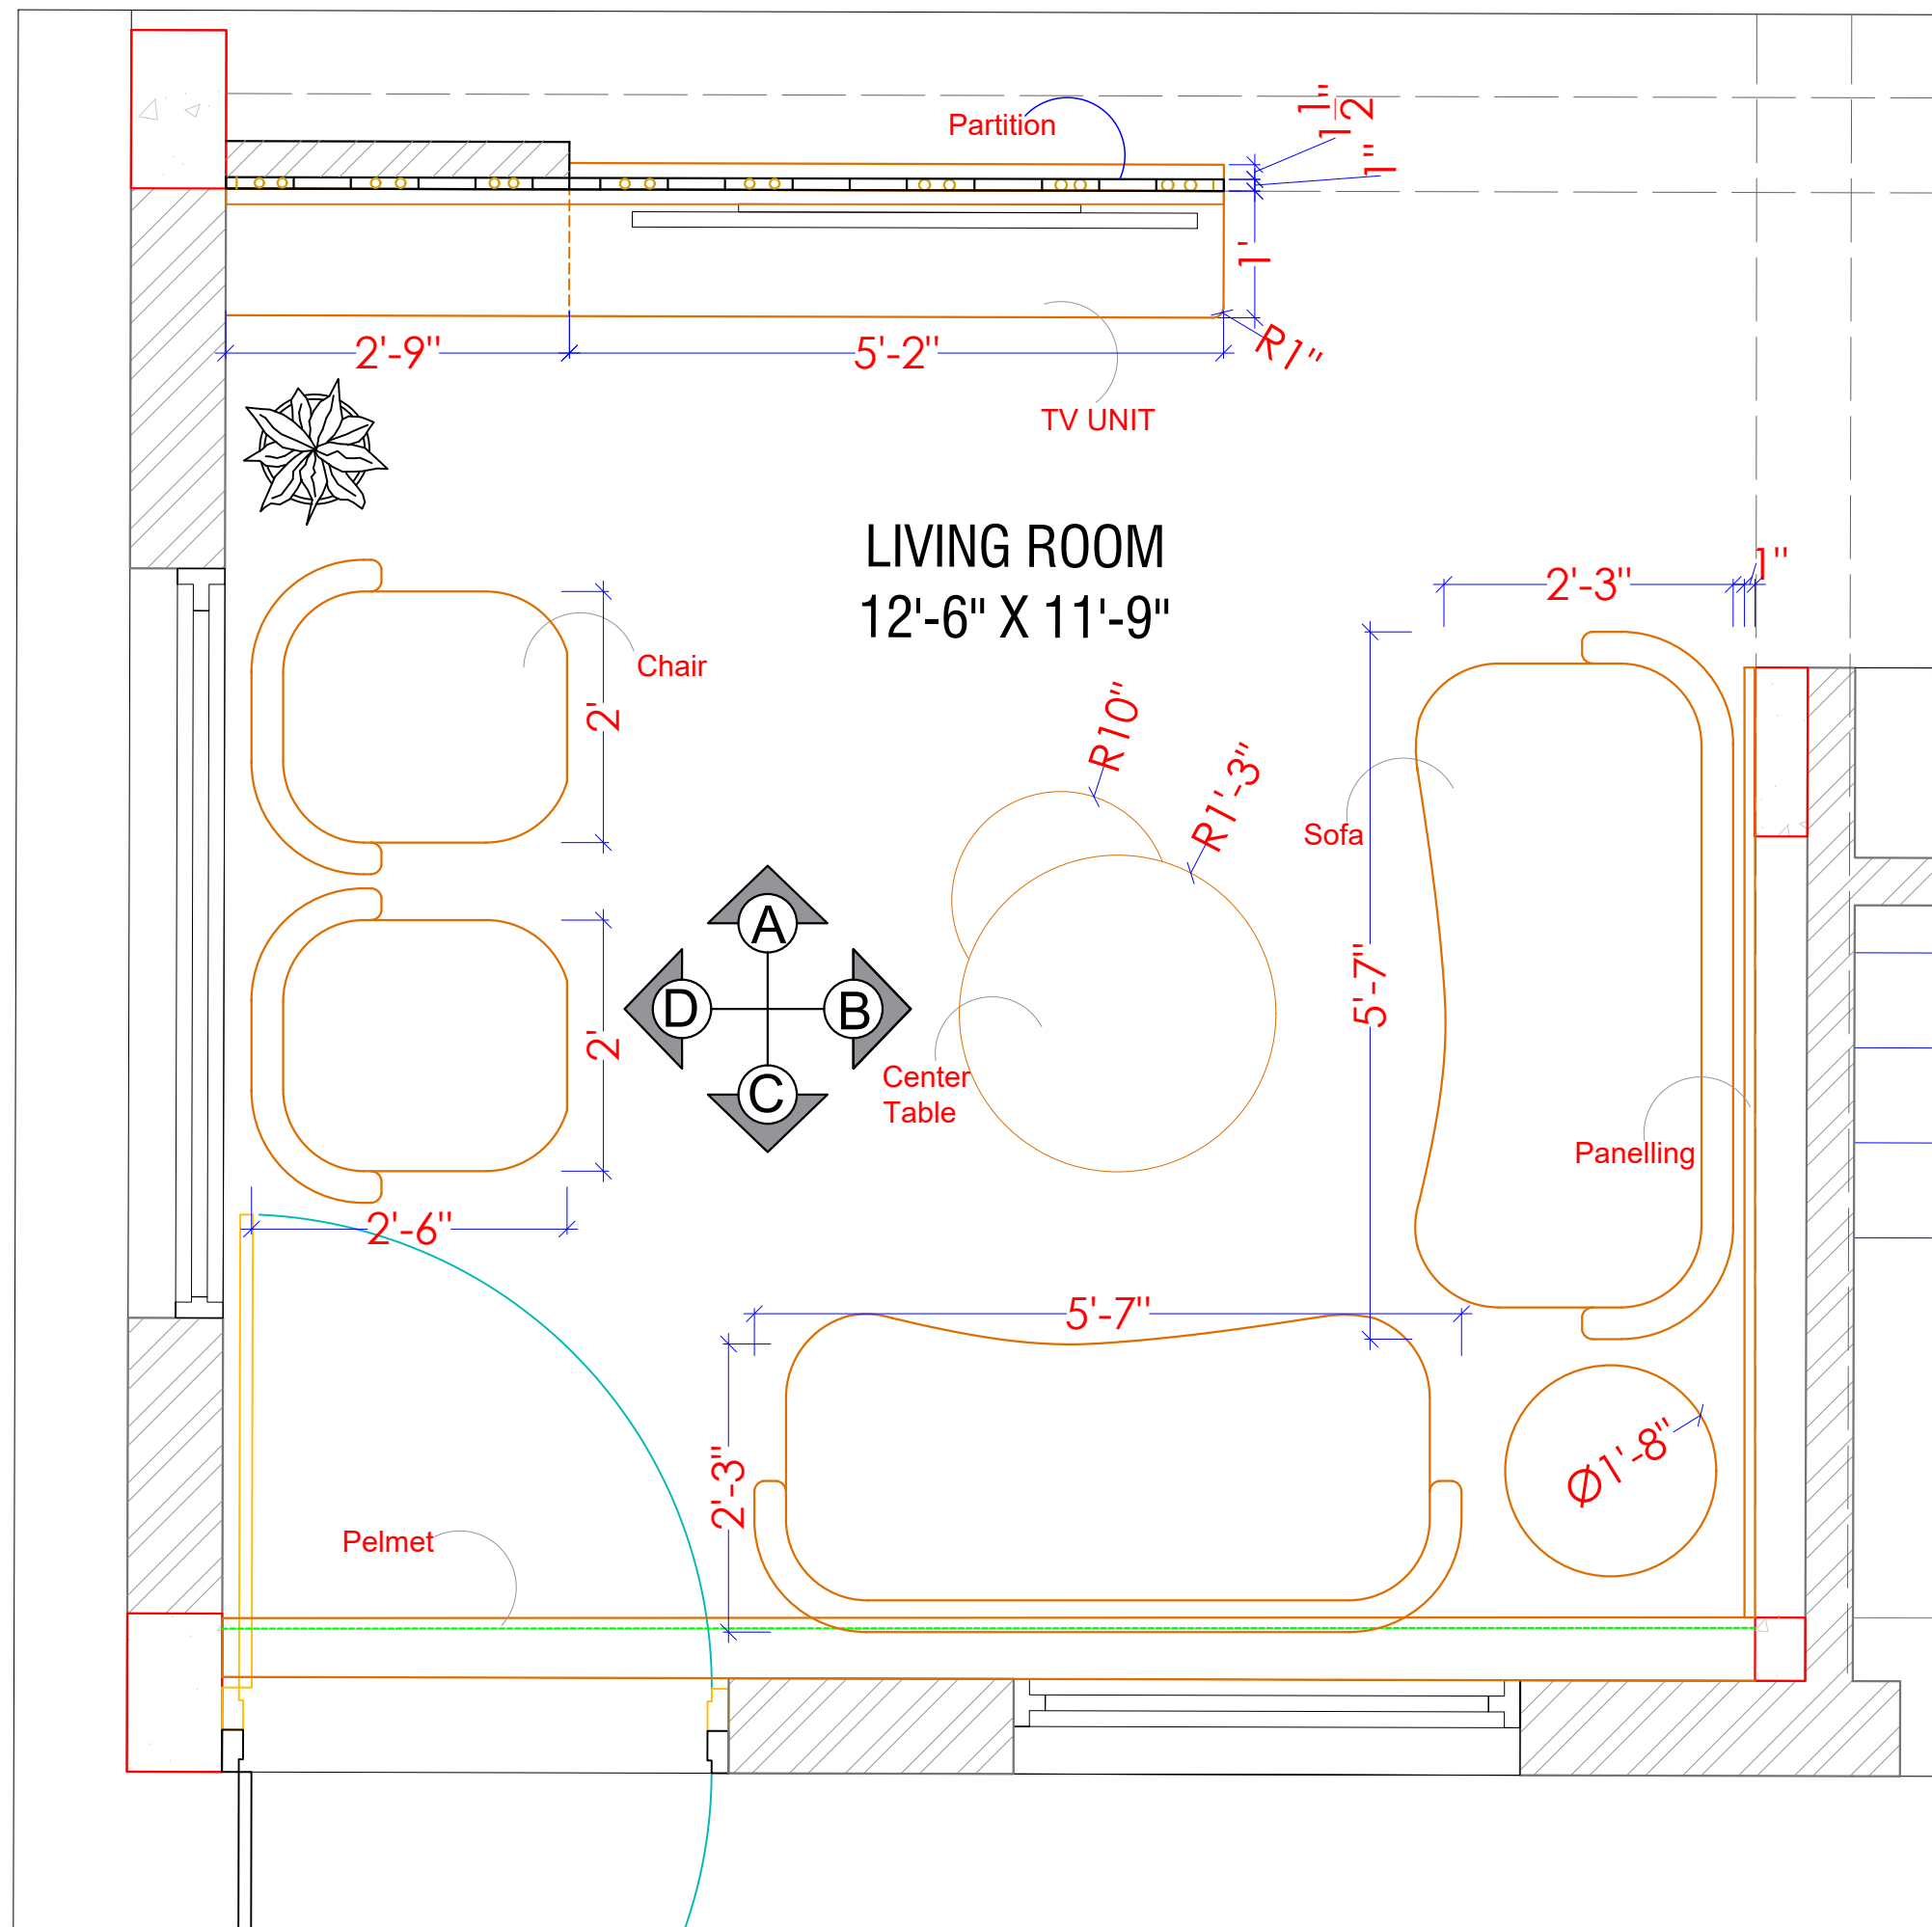

PLAN

DRAWING TITLE :

**LIVING ROOM
FURNITURE LAYOUT**

NOTES:

- * DO NOT SCALE THE DRAWING.
- * ALL DIMENSIONS ARE IN FEET \ INCHES.
- * ANY DISCREPANCY IN THE DRAWING TO BE BROUGHT IN THE DESIGNER'S NOTICE BEFORE IMPLEMENTATION ON SITE.

SITE ADDRESS:

**SAVAD
VADODARA**

CLIENT NAME:

RONAK PANCHOLI

DATE: 02-06-2025


NORTH:

DRAWING DETAIL


REVISION NO.	R1	R2	R3
REVISED DATE:	12/02/2026		
SCALE:	N.T.S		
DRAWN BY:	ARCHANA		
CHECKED BY:	MITTAL		

	www.mayaspace.studio
	mayaspace.studio@gmail.com
	+918980144077
	@mayaspace.studio



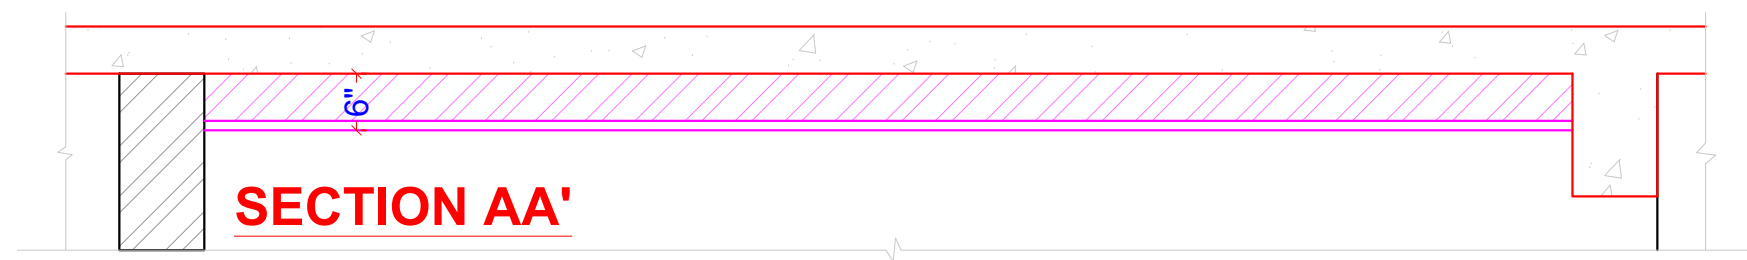

SECTION AA'

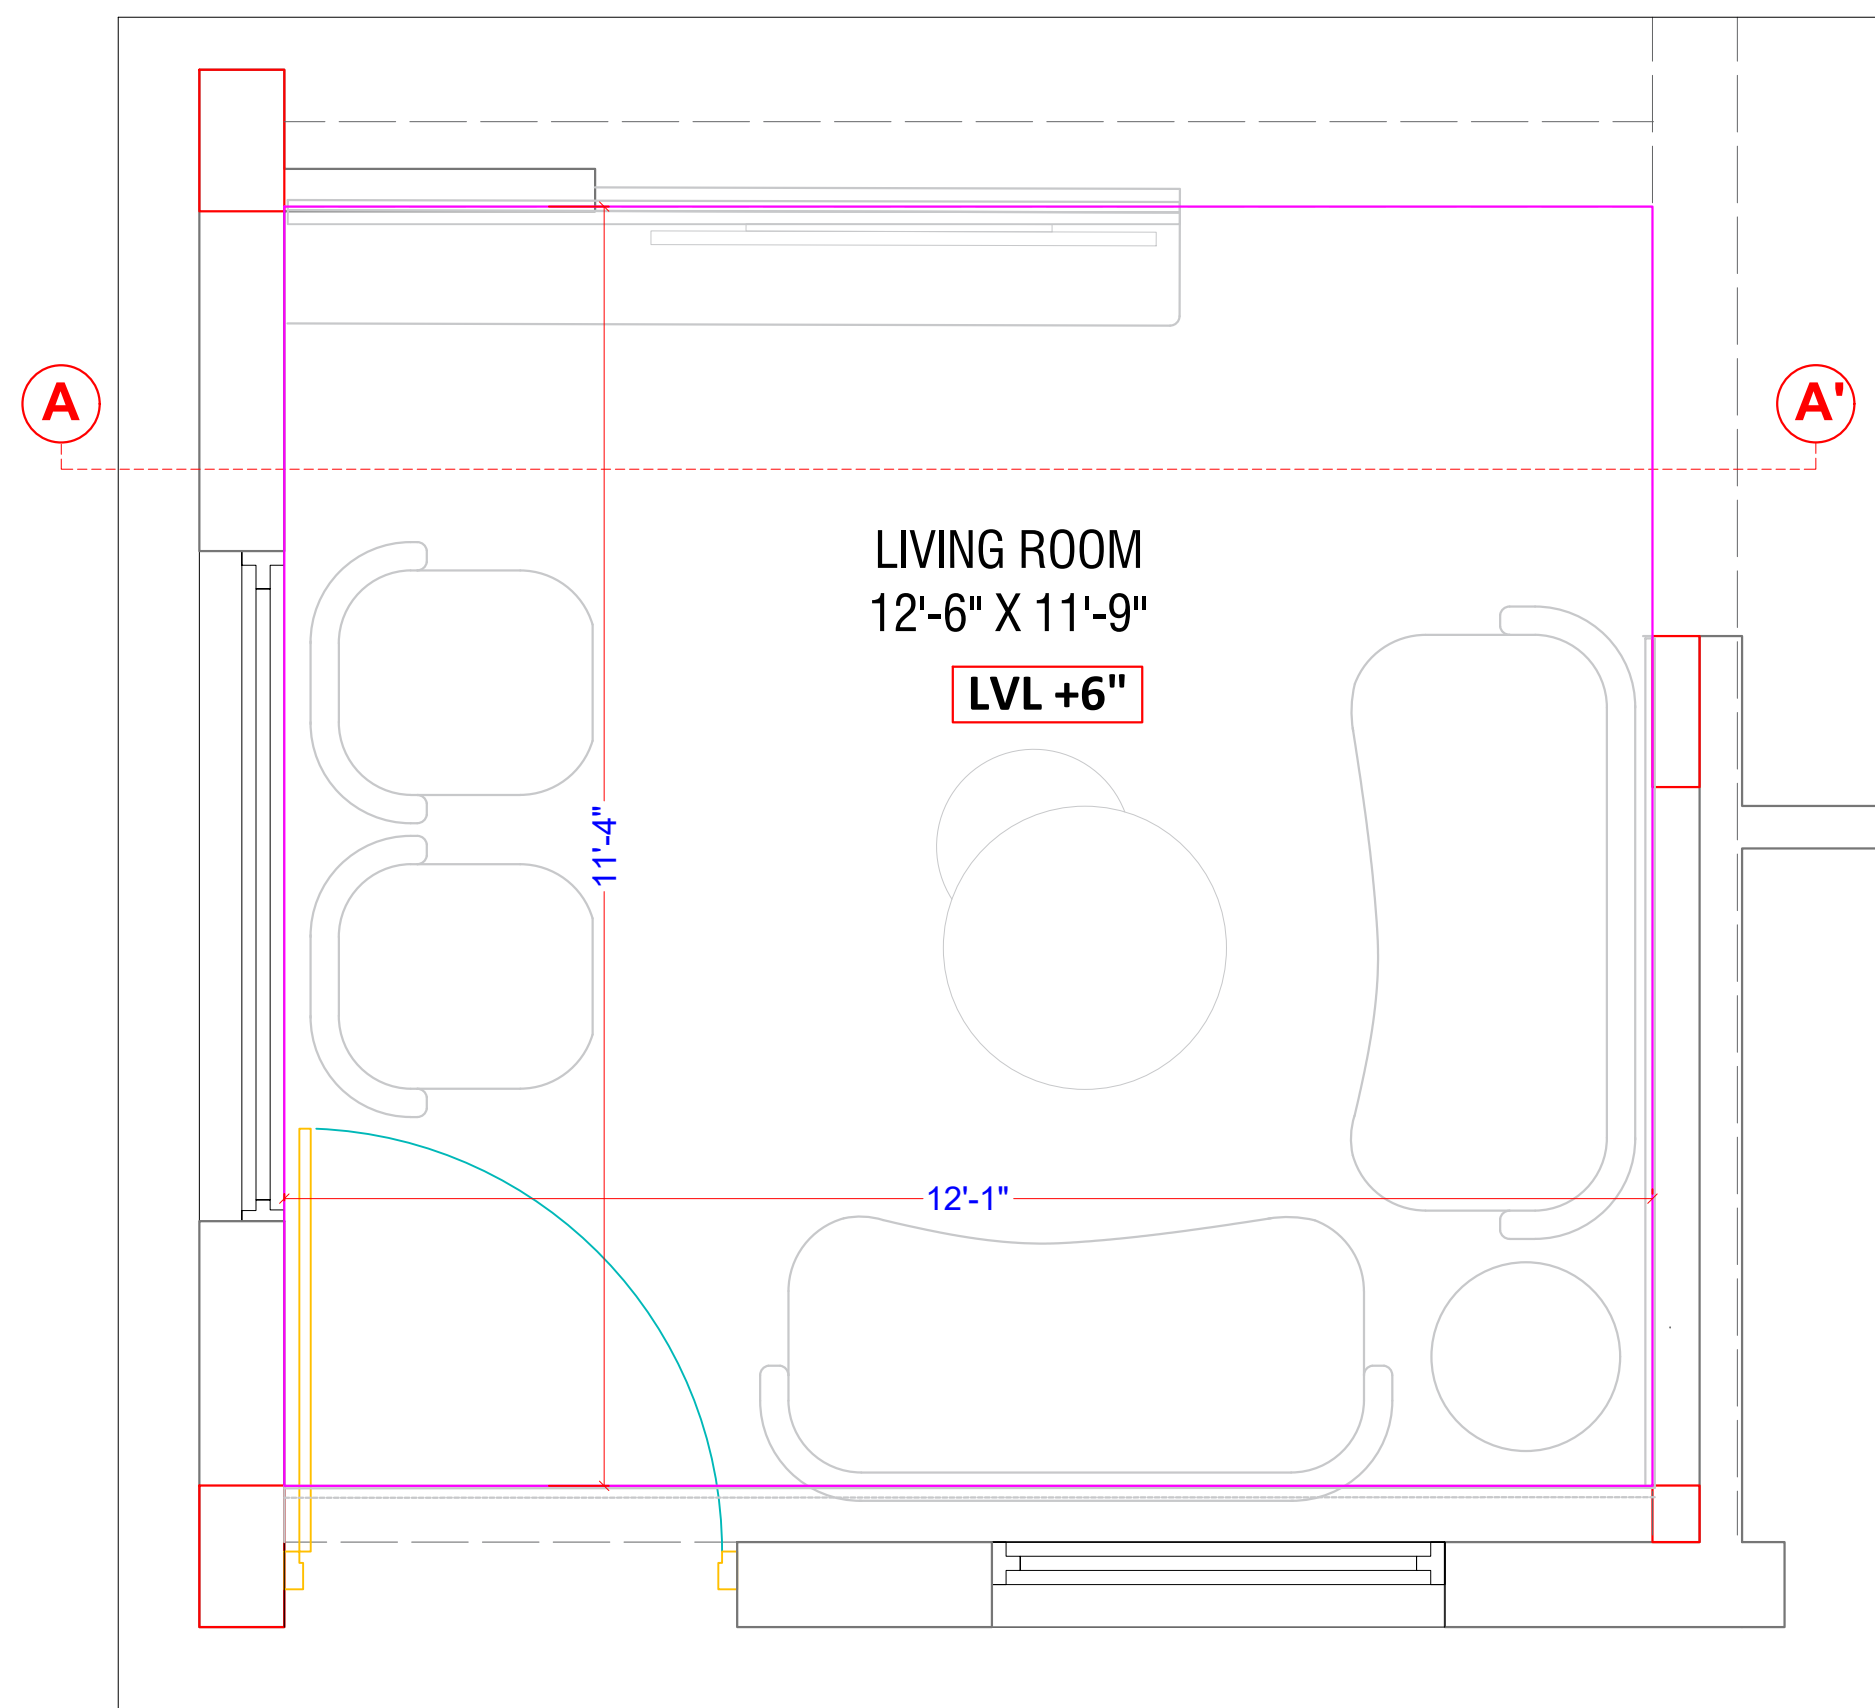

LIVING ROOM
12'-6" X 11'-9"

LVL +6"

FALSE CEILING LAYOUT

DRAWING TITLE :

LIVING ROOM
FALSE CEILING LAYOUT

NOTES:

- * DO NOT SCALE THE DRAWING.
- * ALL DIMENSIONS ARE IN FEET \ INCHES.
- * ANY DISCREPENCY IN THE DRAWING TO BE BROUGHT IN THE DESIGNER'S NOTICE BEFORE IMPLEMENTATION ON SITE.

SITE ADDRESS:

SAVAD
VADODARA

CLIENT NAME:

RONAK PANCHOLI

DATE:

02-06-2025


NORTH:

DRAWING DETAIL

REVISION NO.	R1	R2	R3
REVISED DATE:	12/02/26		
SCALE:	N.T.S		
DRAWN BY:	ARCHANA		
CHECKED BY:	MITTAL		

	www.mayaspace.studio
	mayaspace.studio@gmail.com
	+918980144077
	@mayaspace.studio



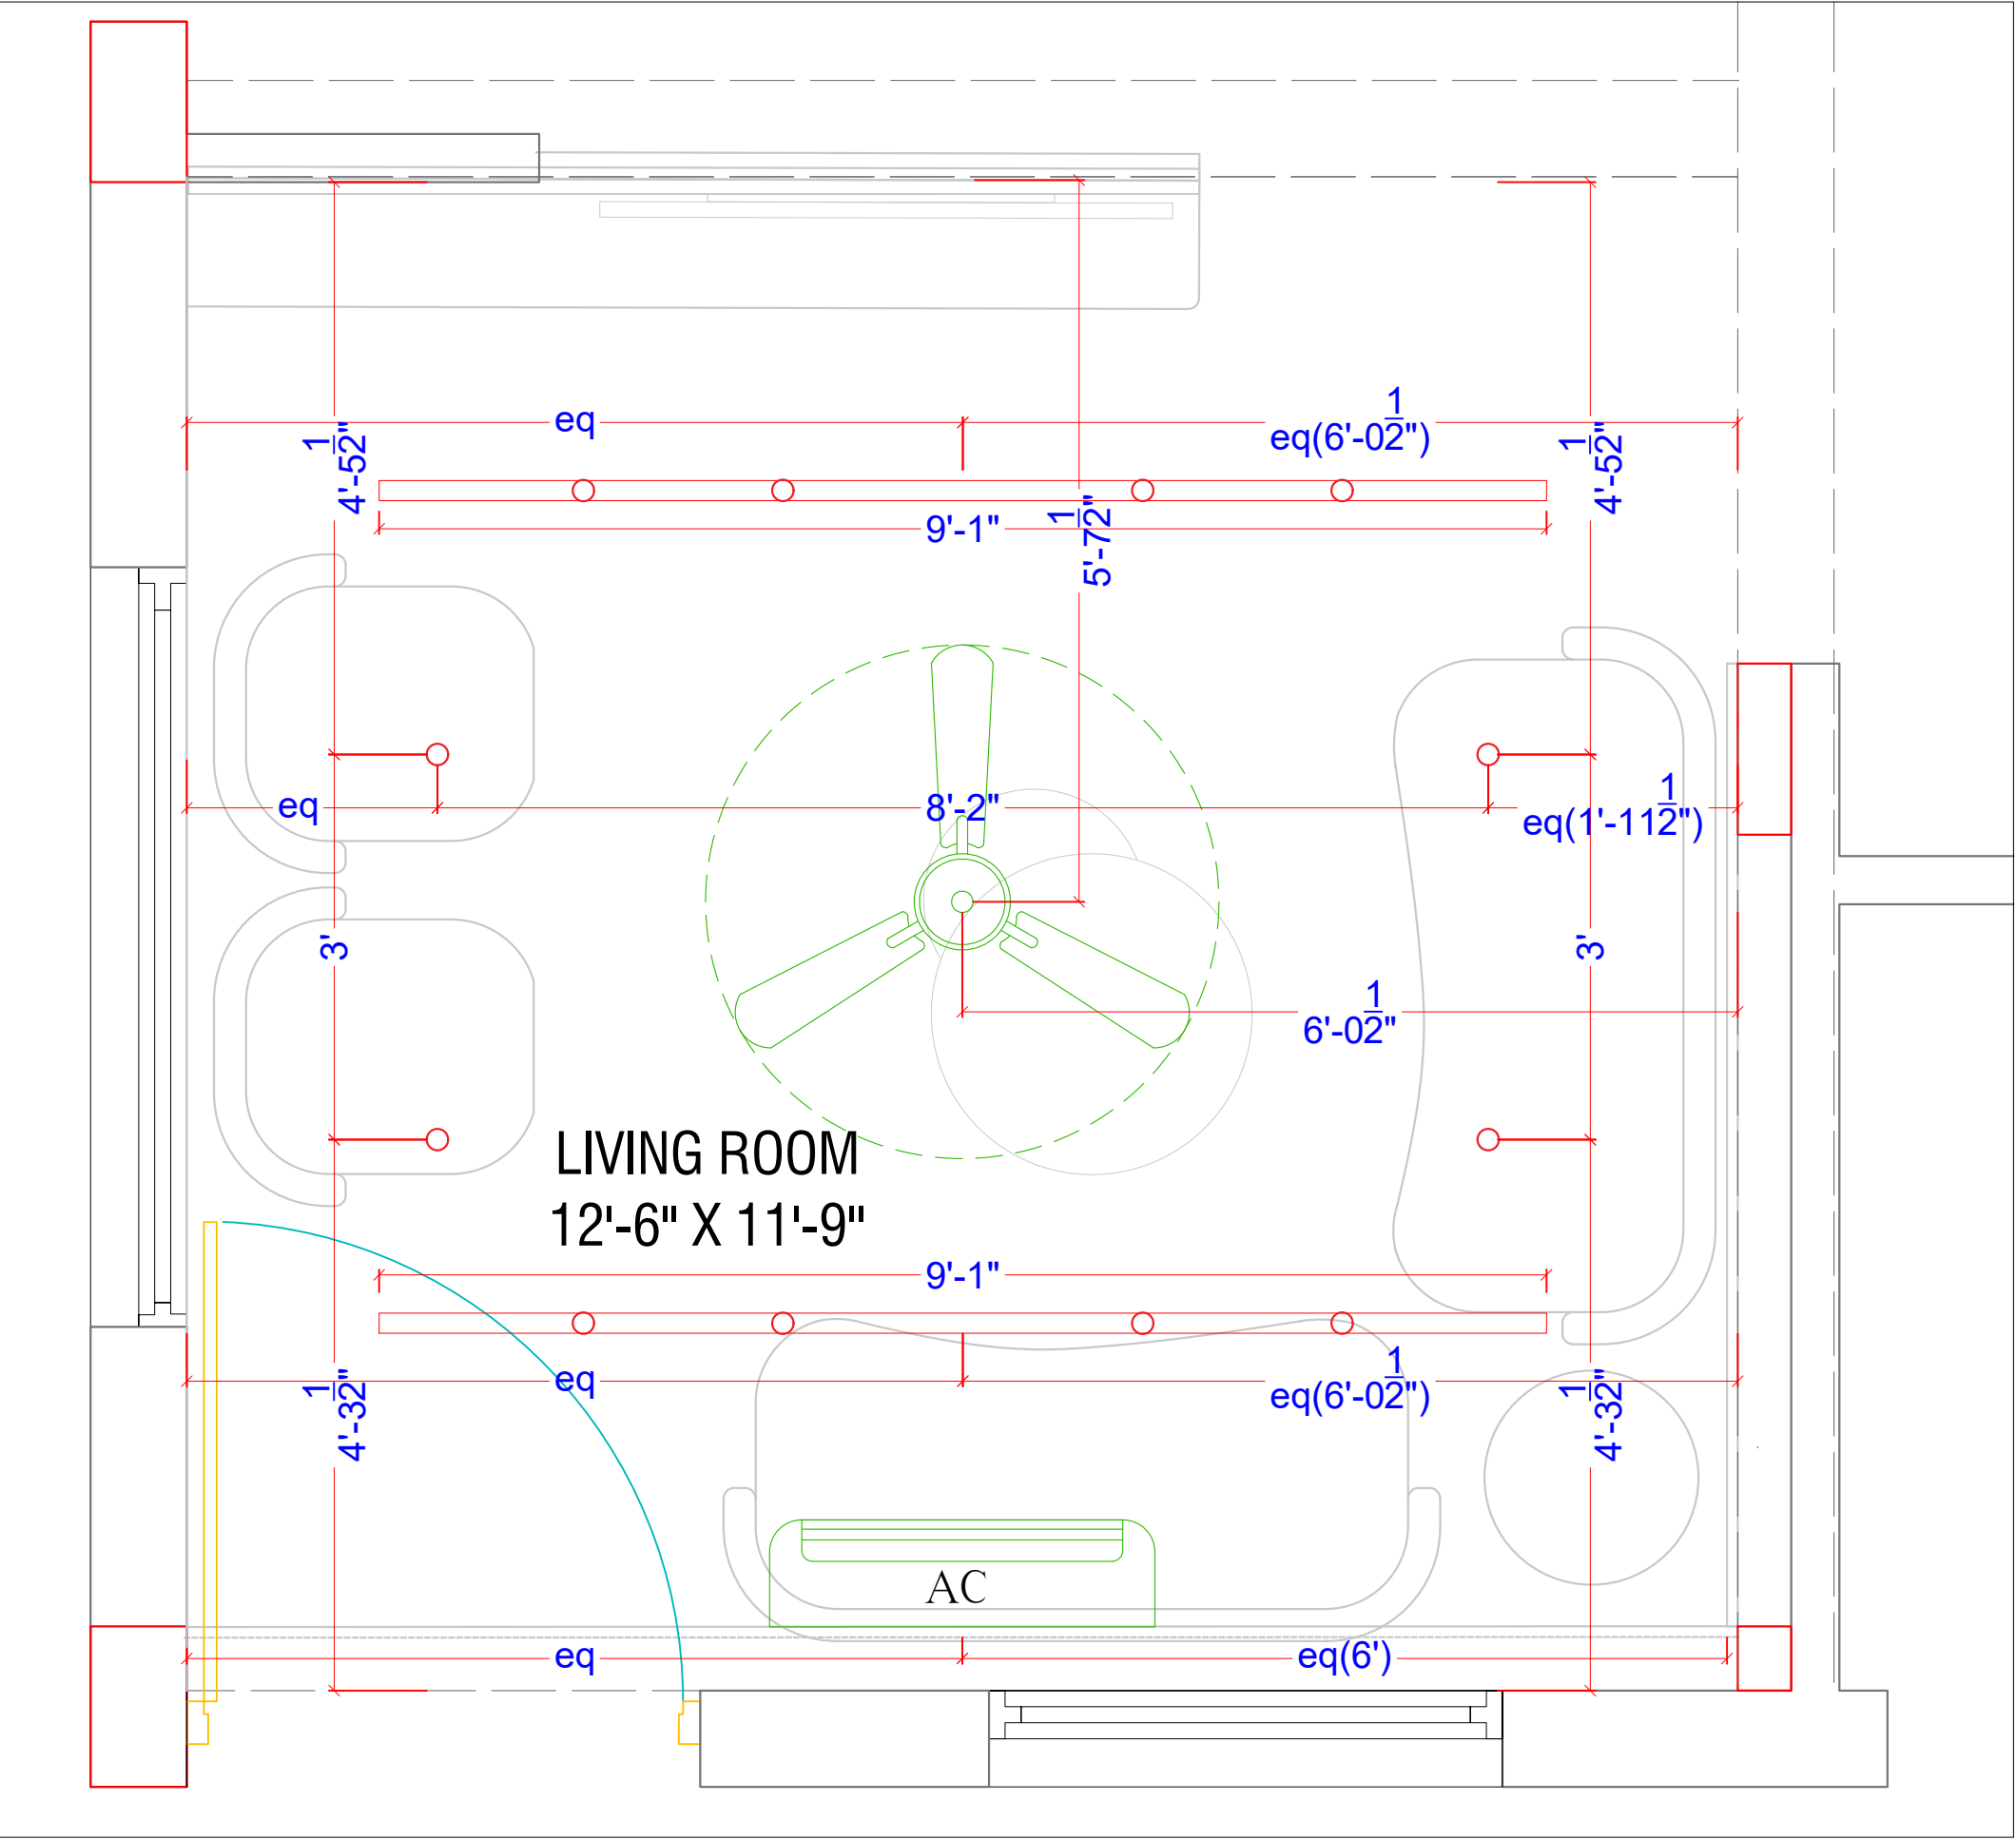

LIGHTING LAYOUT

DRAWING TITLE :

LIVING ROOM
LIGHTING LAYOUT

NOTES:

- * DO NOT SCALE THE DRAWING.
- * ALL DIMENSIONS ARE IN FEET \ INCHES.
- * ANY DISCREPENCY IN THE DRAWING TO BE BROUGHT IN THE DESIGNER'S NOTICE BEFORE IMPLEMENTATION ON SITE.

SITE ADDRESS:

SAVAD
VADODARA

CLIENT NAME:

RONAK PANCHOLI

DATE: 02-06-2025


NORTH:

DRAWING DETAIL

REVISION NO.	R1	R2	R3
REVISED DATE:	12/02/26		
SCALE:	N.T.S		
DRAWN BY:	ARCHANA		
CHECKED BY:	MITTAL		

- www.mayaspace.studio
- mayaspace.studio@gmail.com
- +918980144077
- @mayaspace.studio



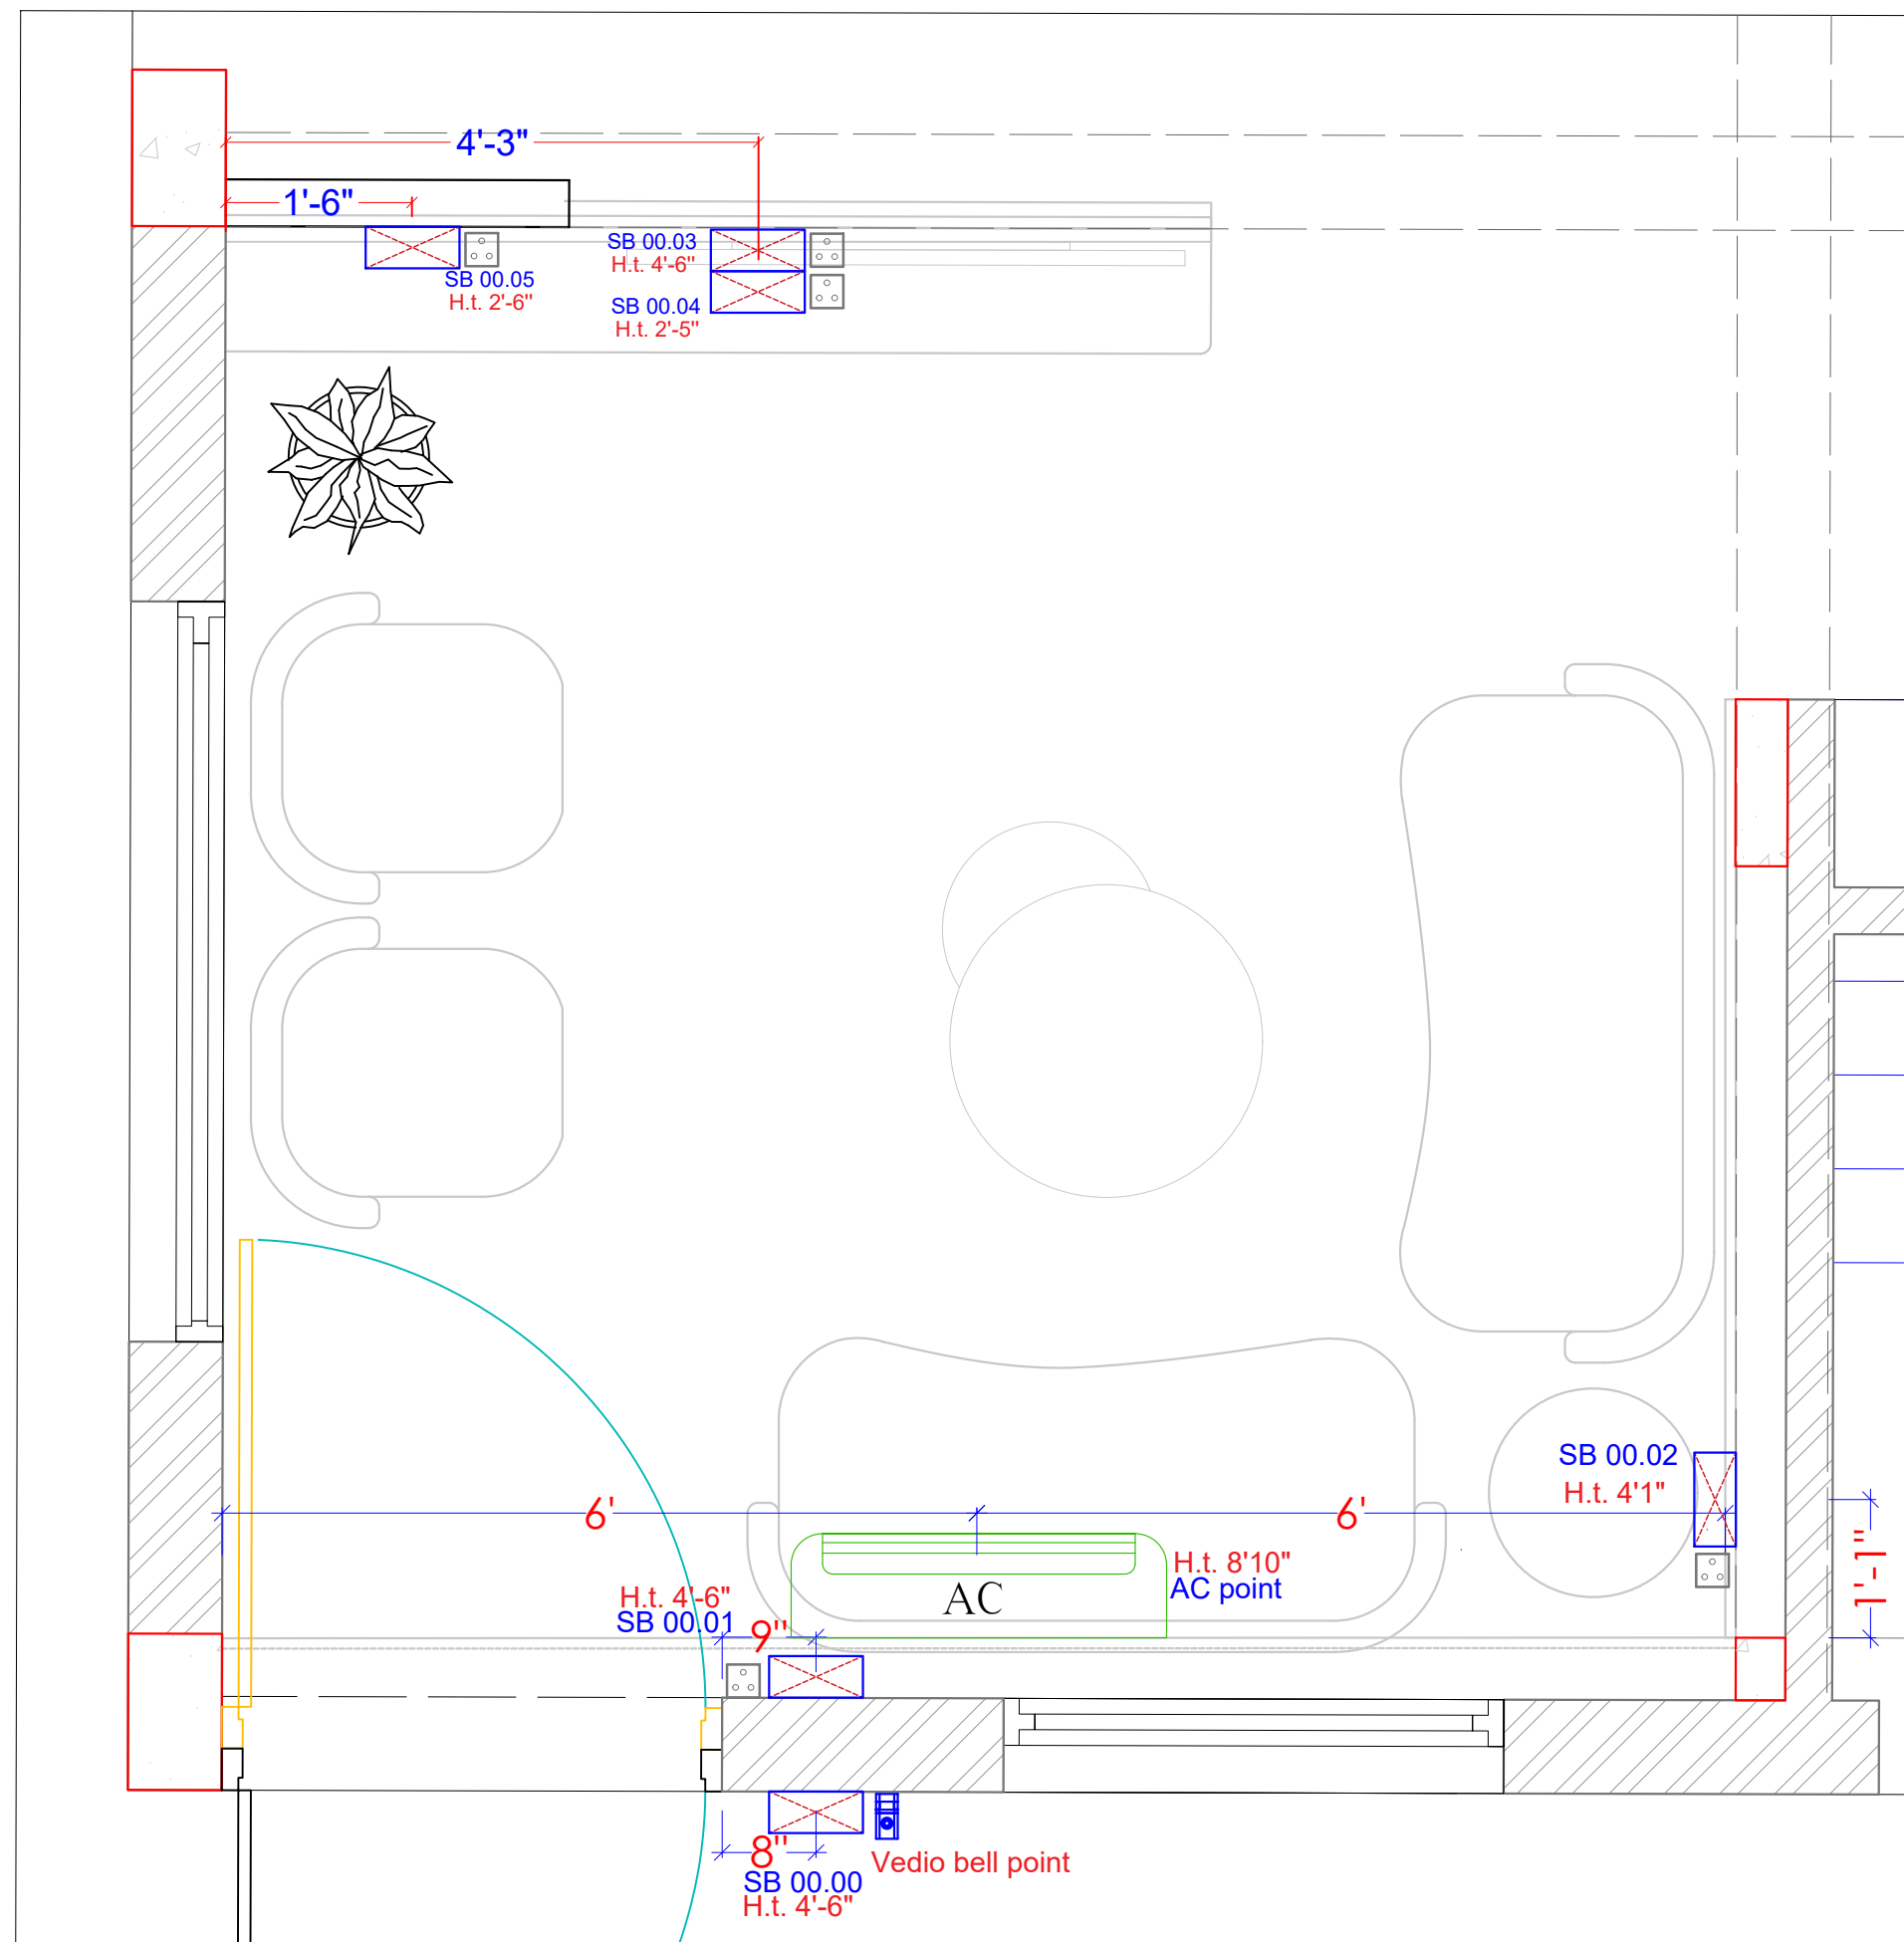

SWITCH BOARD LAYOUT

DRAWING TITLE :

LIVING ROOM SWITCH BOARD LAYOUT

NOTES:

- * DO NOT SCALE THE DRAWING.
- * ALL DIMENSIONS ARE IN FEET \ INCHES.
- * ANY DISCREPENCY IN THE DRAWING TO BE BROUGHT IN THE DESIGNER'S NOTICE BEFORE IMPLEMENTATION ON SITE.

SITE ADDRESS:

SAVAD
VADODARA

CLIENT NAME:

RONAK PANCHOLI

DATE: 02-06-2025


NORTH:

DRAWING DETAIL

REVISION NO.	R1	R2	R3
REVISED DATE:	12/02/26		
SCALE:	N.T.S		
DRAWN BY:	ARCHANA		
CHECKED BY:	MITTAL		

www.mayaspace.studio
mayaspace.studio@gmail.com
+918980144077
@mayaspace.studio



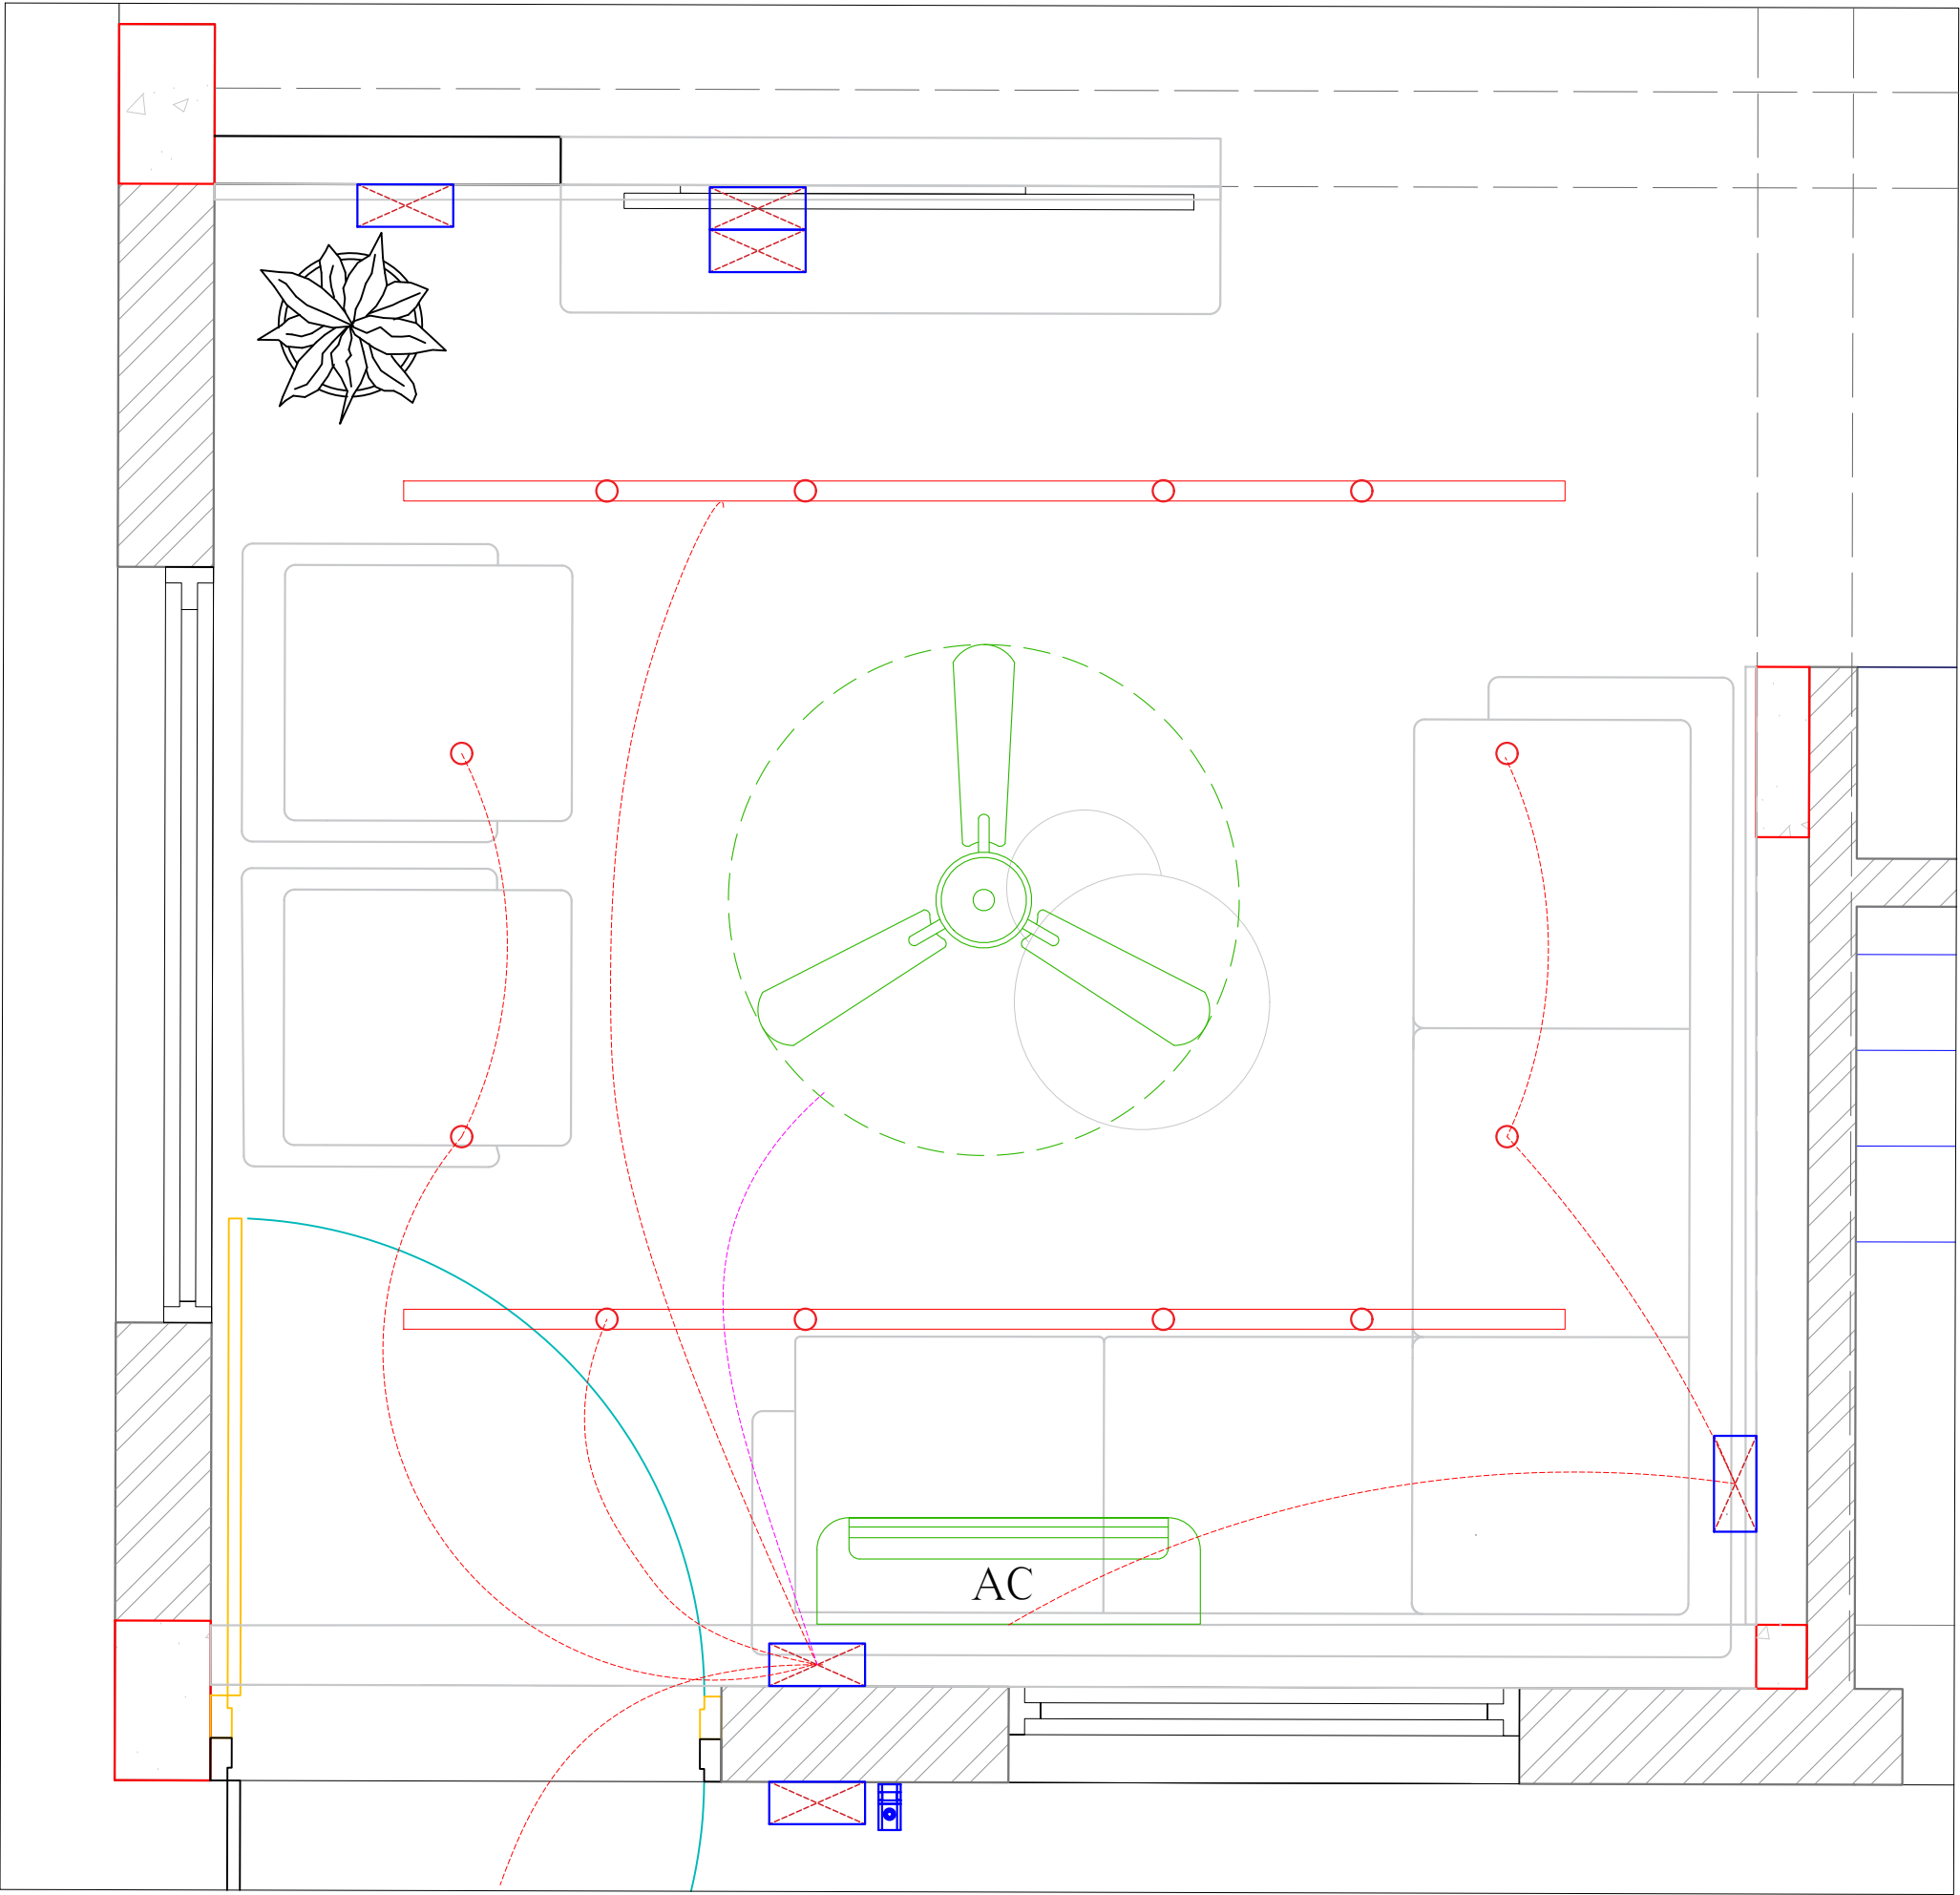

LOOPING LAYOUT

DRAWING TITLE :

LIVING ROOM
LOOPING LAYOUT

NOTES:

- * DO NOT SCALE THE DRAWING.
- * ALL DIMENSIONS ARE IN FEET \ INCHES.
- * ANY DISCREPENCY IN THE DRAWING TO BE BROUGHT IN THE DESIGNER'S NOTICE BEFORE IMPLEMENTATION ON SITE.

SITE ADDRESS:

SAVAD
VADODARA

CLIENT NAME:

RONAK PANCHOLI

DATE: 02-06-2025


NORTH:

DRAWING DETAIL

REVISION NO.	R1	R2	R3
REVISED DATE:	12/02/26		
SCALE:	N.T.S		
DRAWN BY:	ARCHANA		
CHECKED BY:	MITTAL		

- www.mayaspace.studio
- mayaspace.studio@gmail.com
- +918980144077
- @mayaspace.studio



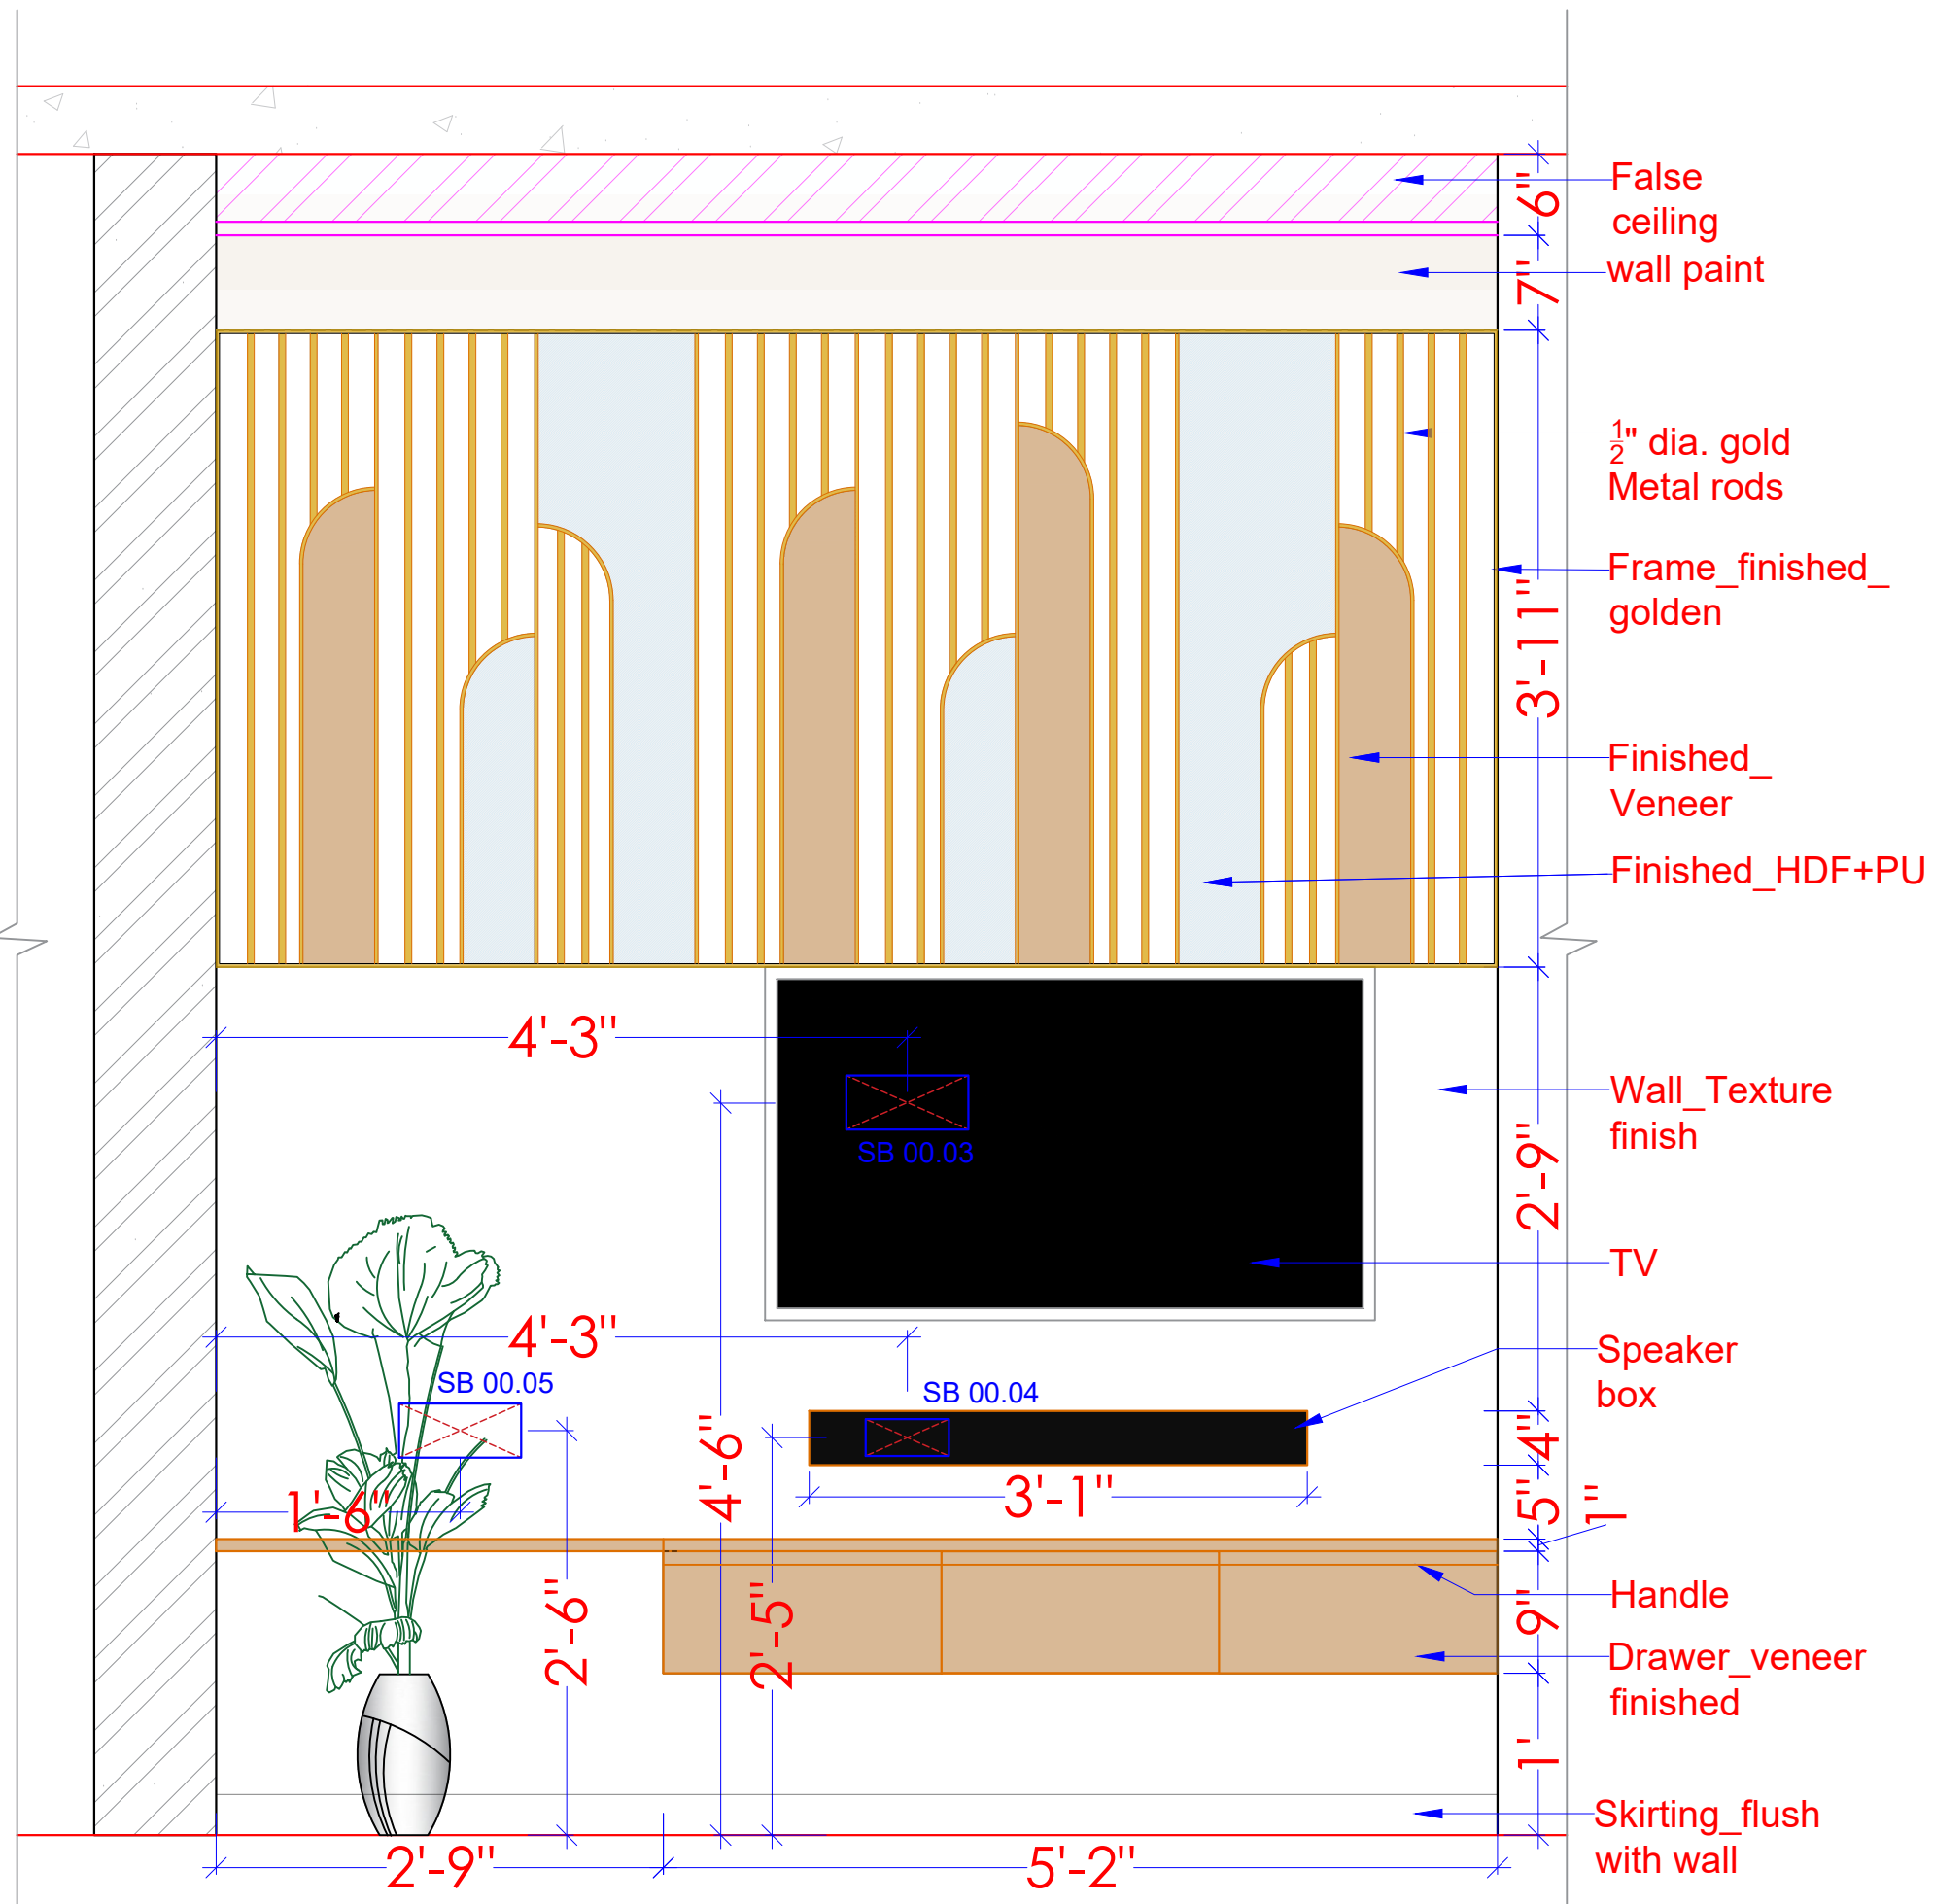

ELEVATION - A

DRAWING TITLE :

LIVING ROOM
ELEVATION- A

NOTES:

- * DO NOT SCALE THE DRAWING.
- * ALL DIMENSIONS ARE IN FEET \ INCHES.
- * ANY DISCREPENCY IN THE DRAWING TO BE BROUGHT IN THE DESIGNER'S NOTICE BEFORE IMPLEMENTATION ON SITE.

SITE ADDRESS:

SAVAD
VADODARA

CLIENT NAME:

RONAK PANCHOLI

DATE: 02-06-2025


NORTH:

DRAWING DETAIL

REVISION NO.	R1	R2	R3
REVISED DATE:	12/02/26		
SCALE:	N.T.S		
DRAWN BY:	ARCHANA		
CHECKED BY:	MITTAL		

	www.mayaspace.studio
	mayaspace.studio@gmail.com
	+918980144077
	@mayaspace.studio



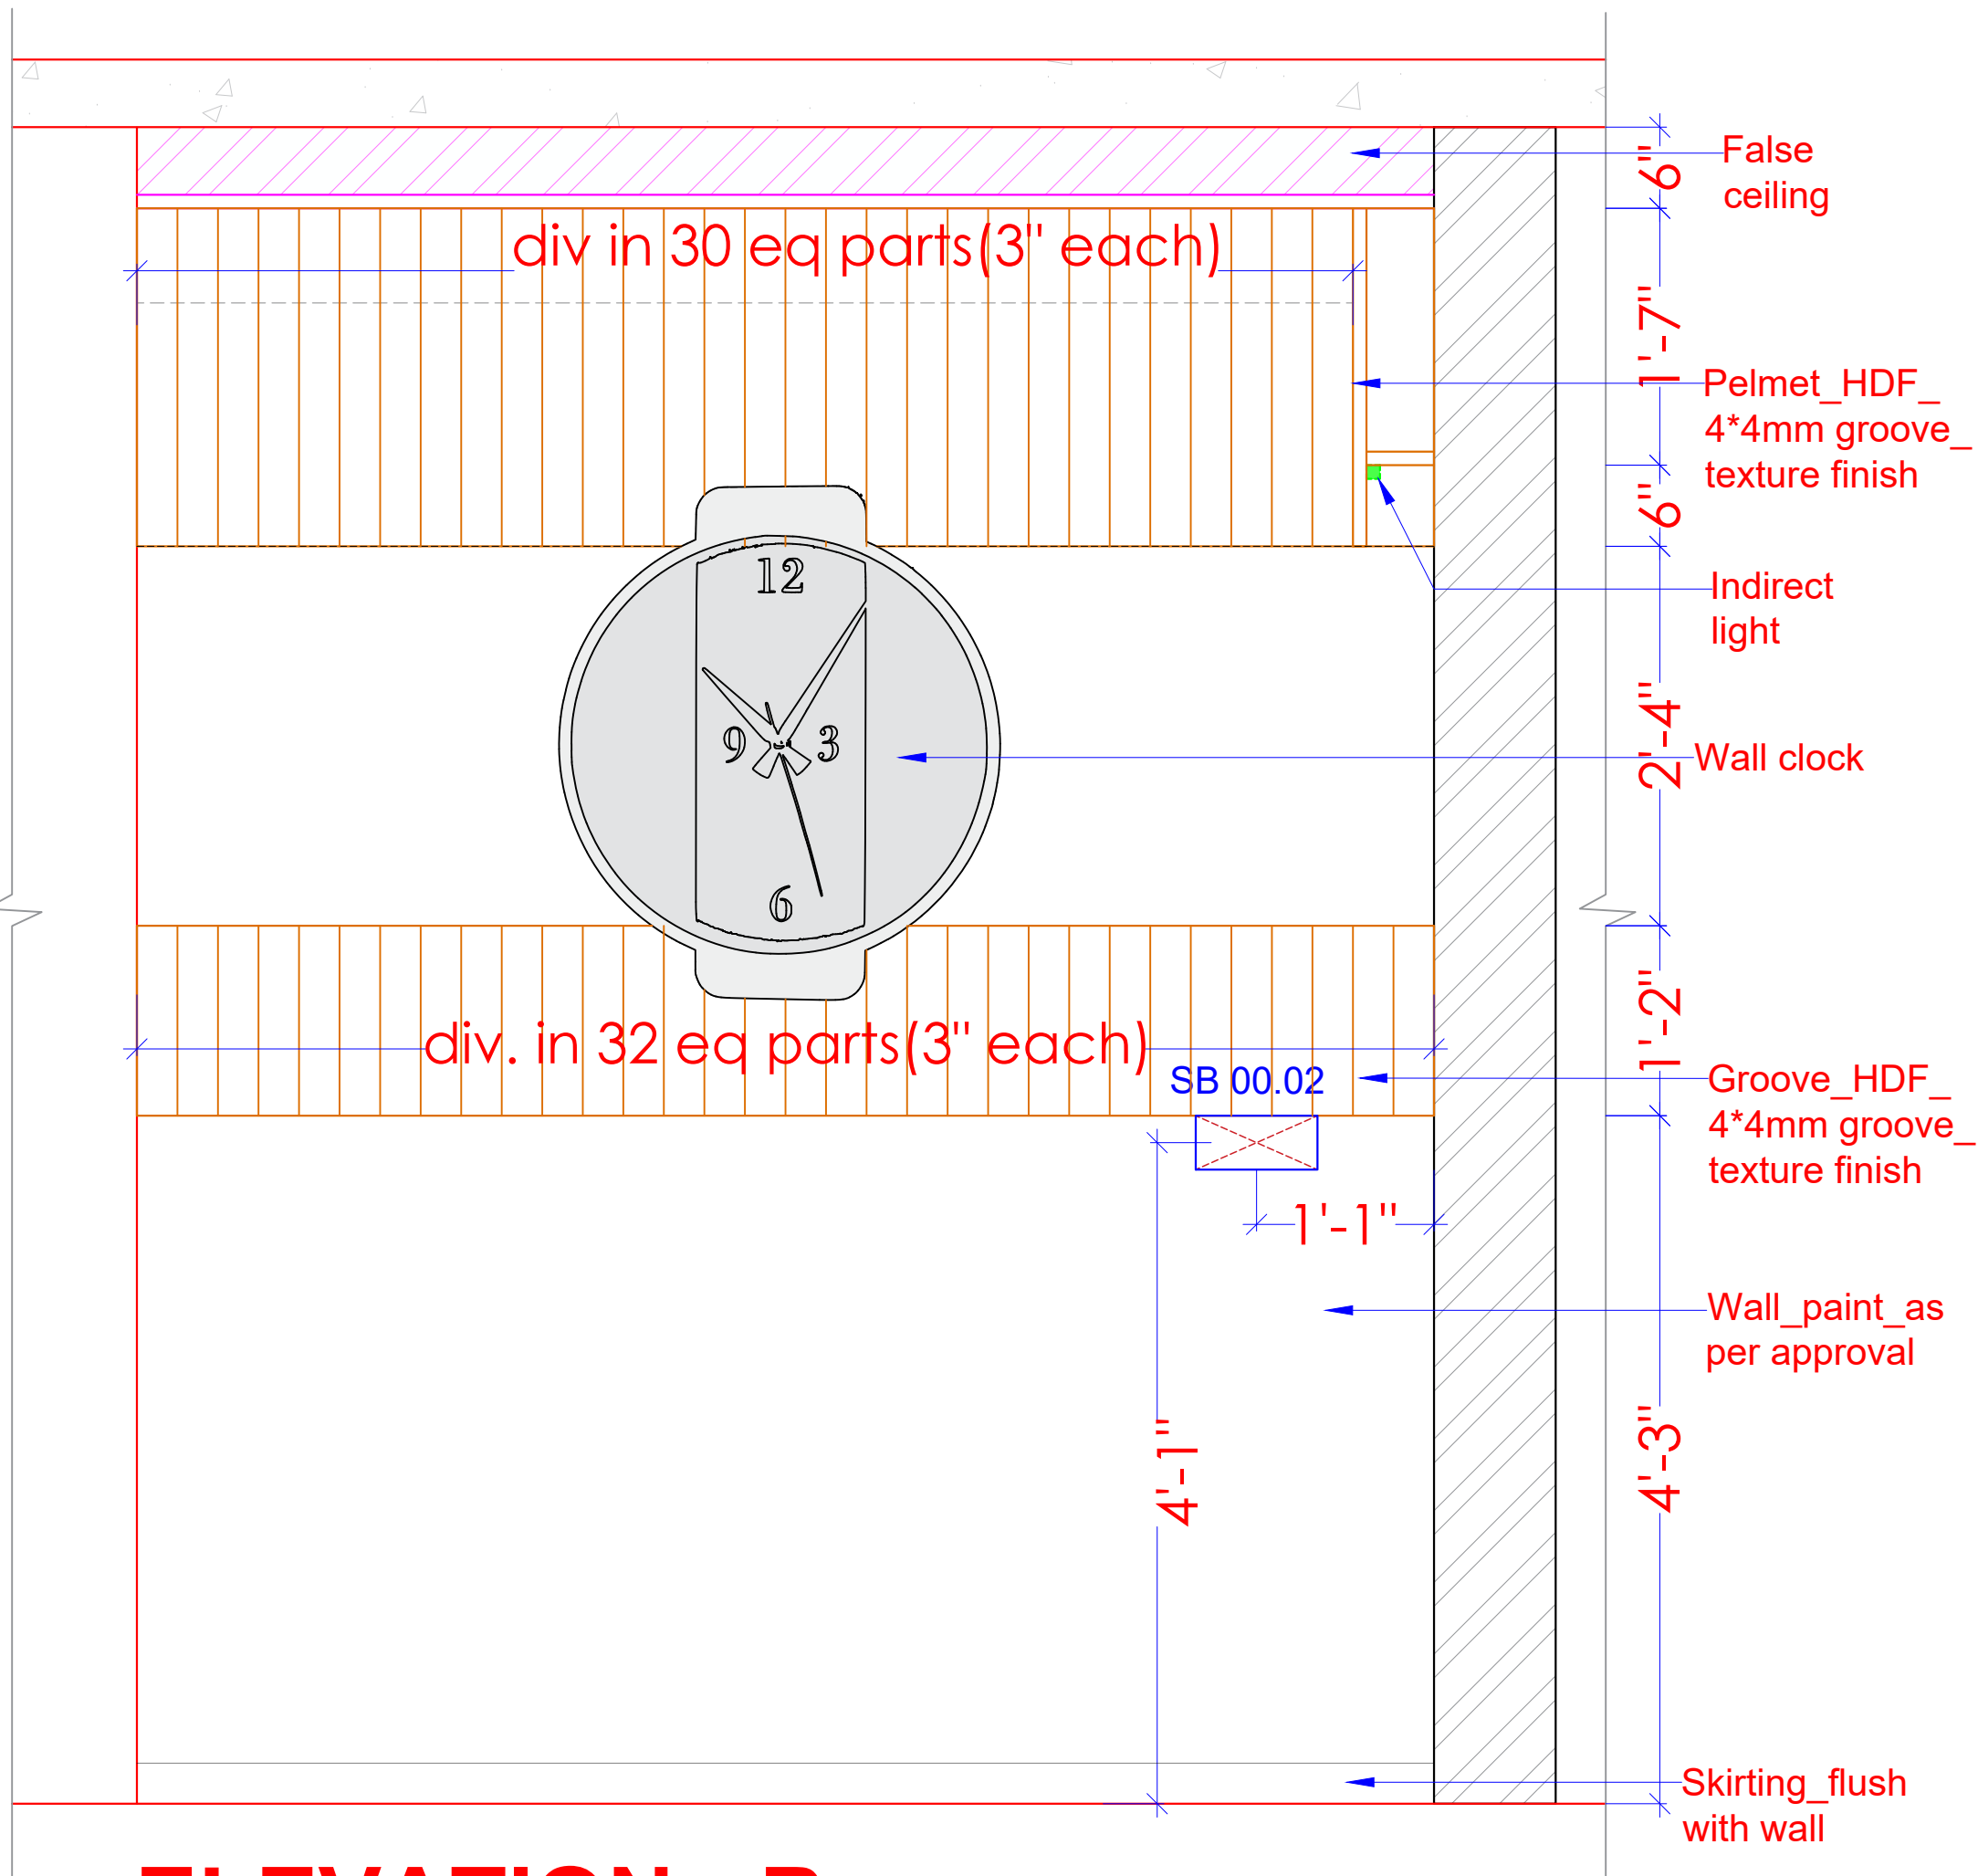

ELEVATION - B

DRAWING TITLE :

LIVING ROOM
ELEVATION- B

NOTES:

* DO NOT SCALE THE DRAWING.

* ALL DIMENSIONS ARE IN FEET \ INCHES.

* ANY DISCREPANCY IN THE DRAWING
TO BE BROUGHT IN THE DESIGNER'S
NOTICE BEFORE IMPLEMENTATION
ON SITE.

SITE ADDRESS:

SAVAD
VADODARA

CLIENT NAME:

RONAK PANCHOLI

DATE:

02-06-2025

NORTH:

DRAWING DETAIL

REVISION NO.

R1 R2 R3

REVISED DATE:

12/02/26

SCALE:

N.T.S

DRAWN BY:


ARCHANA

CHECKED BY:

MITTAL

www.mayaspace.studio
mayaspace.studio@gmail.com
+918980144077
@mayaspace.studio



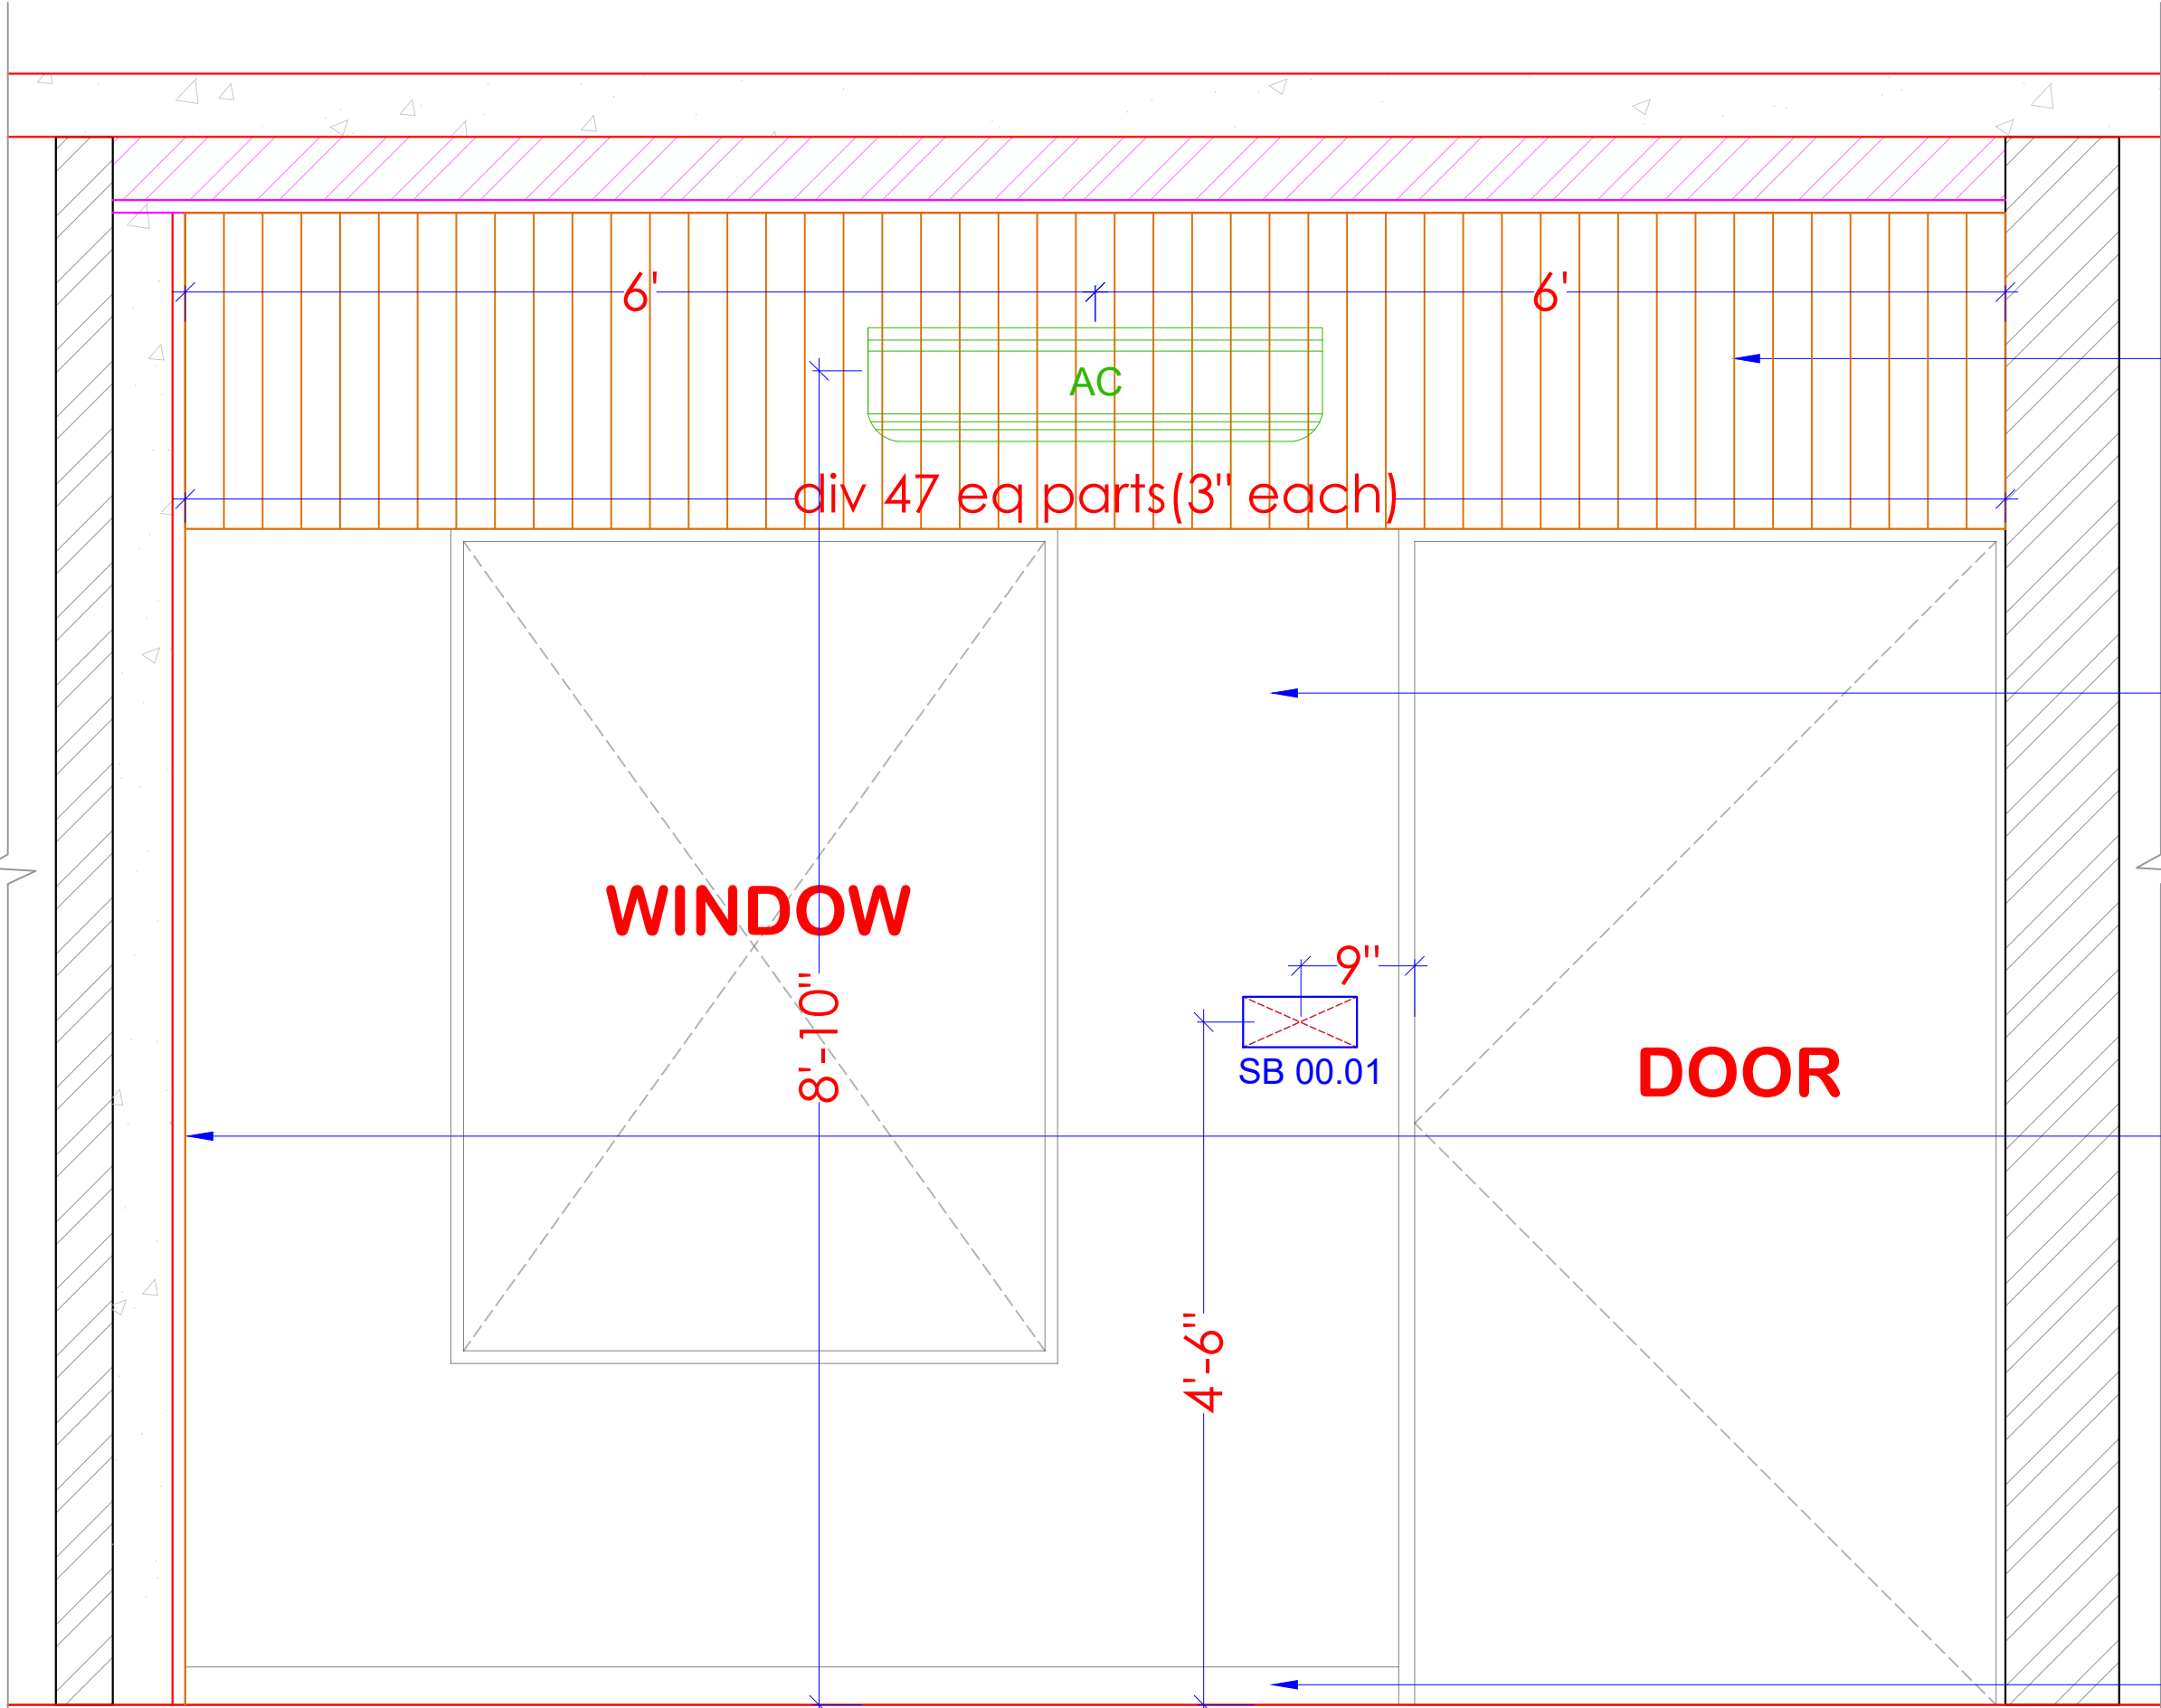

ELEVATION - C

DRAWING TITLE :

LIVING ROOM
ELEVATION- C

NOTES:

- * DO NOT SCALE THE DRAWING.
- * ALL DIMENSIONS ARE IN FEET \ INCHES.
- * ANY DISCREPANCY IN THE DRAWING TO BE BROUGHT IN THE DESIGNER'S NOTICE BEFORE IMPLEMENTATION ON SITE.

SITE ADDRESS:

SAVAD
VADODARA

CLIENT NAME:

RONAK PANCHOLI

DATE:

02-06-2025


NORTH:

DRAWING DETAIL

REVISION NO.	R1	R2	R3
REVISED DATE:	12/02/26		
SCALE:	N.T.S		
DRAWN BY:	ARCHANA		
CHECKED BY:	MITTAL		

www.mayaspace.studio
mayaspace.studio@gmail.com
+918980144077
@mayaspace.studio



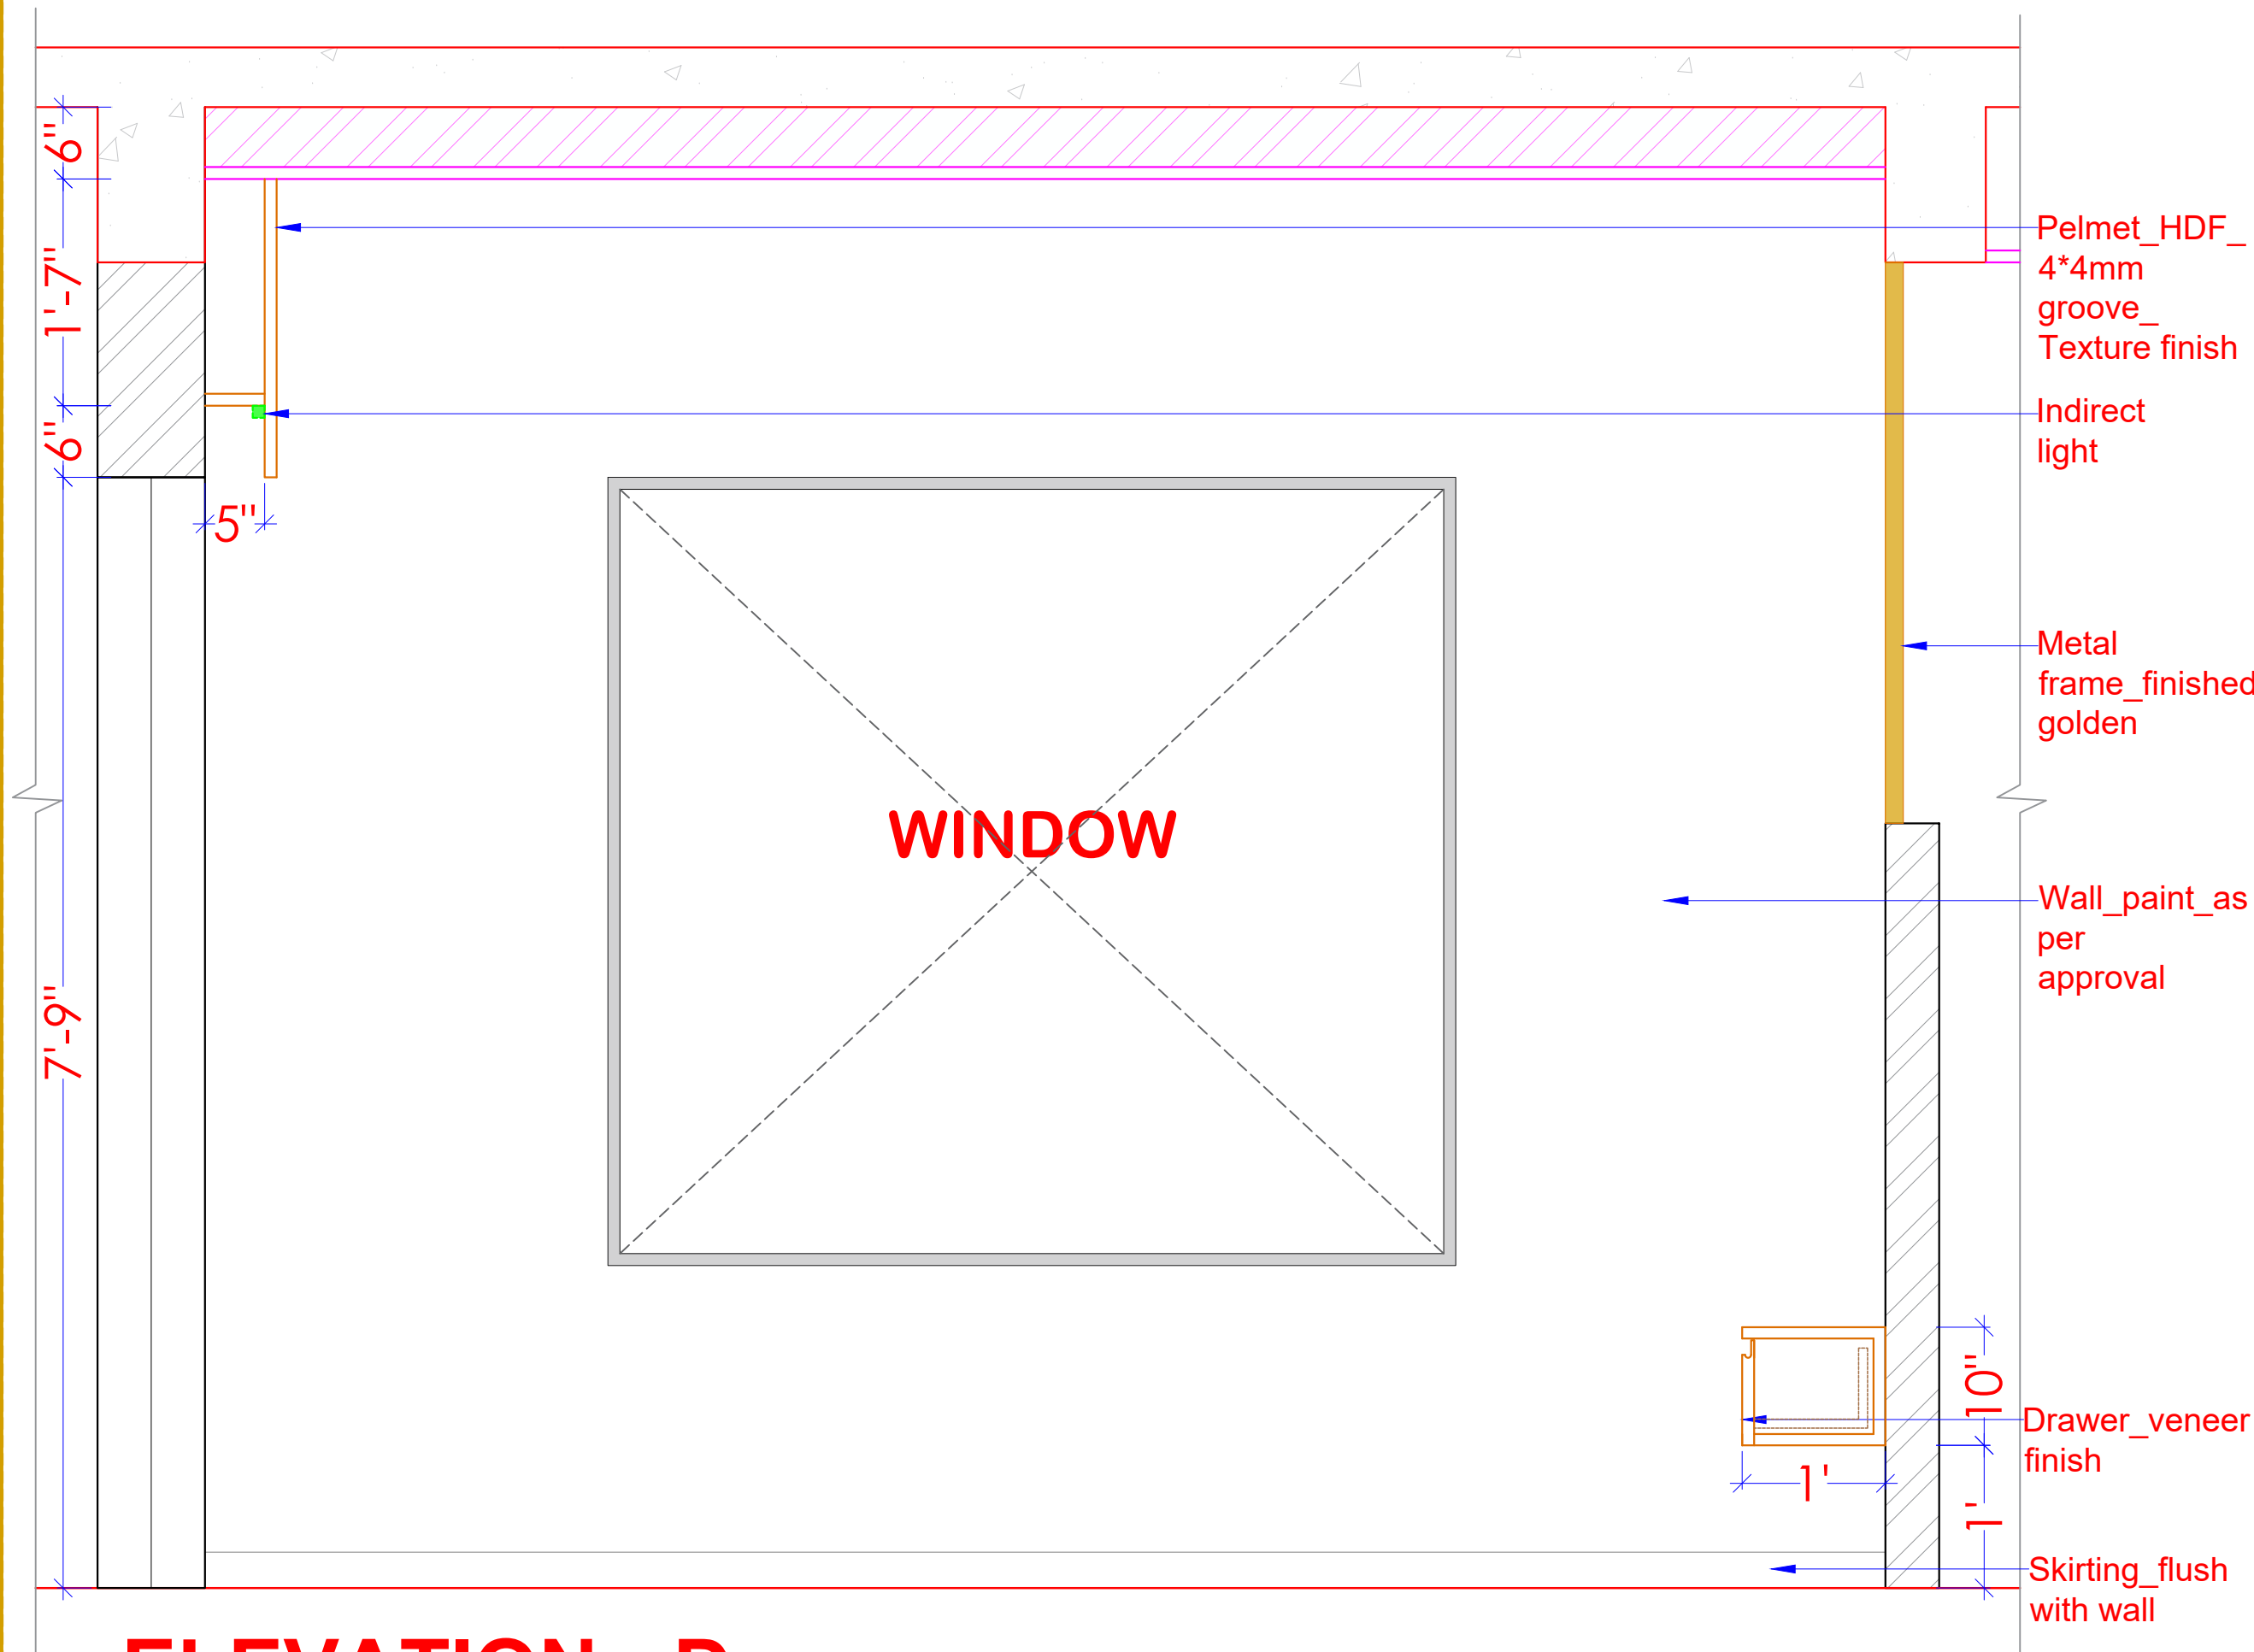

ELEVATION - D

DRAWING TITLE :

LIVING ROOM
ELEVATION- D

NOTES:

- * DO NOT SCALE THE DRAWING.
- * ALL DIMENSIONS ARE IN FEET \ INCHES.
- * ANY DISCREPENCY IN THE DRAWING TO BE BROUGHT IN THE DESIGNER'S NOTICE BEFORE IMPLEMENTATION ON SITE.

SITE ADDRESS:

SAVAD
VADODARA

CLIENT NAME:

RONAK PANCHOLI

DATE: 02-06-2025


NORTH:

DRAWING DETAIL


REVISION NO.	R1	R2	R3
REVISED DATE:	12/02/26		
SCALE:	N.T.S		
DRAWN BY:	ARCHANA		
CHECKED BY:	MITTAL		

- www.mayaspace.studio
- mayaspace.studio@gmail.com
- +918980144077
- @mayaspace.studio




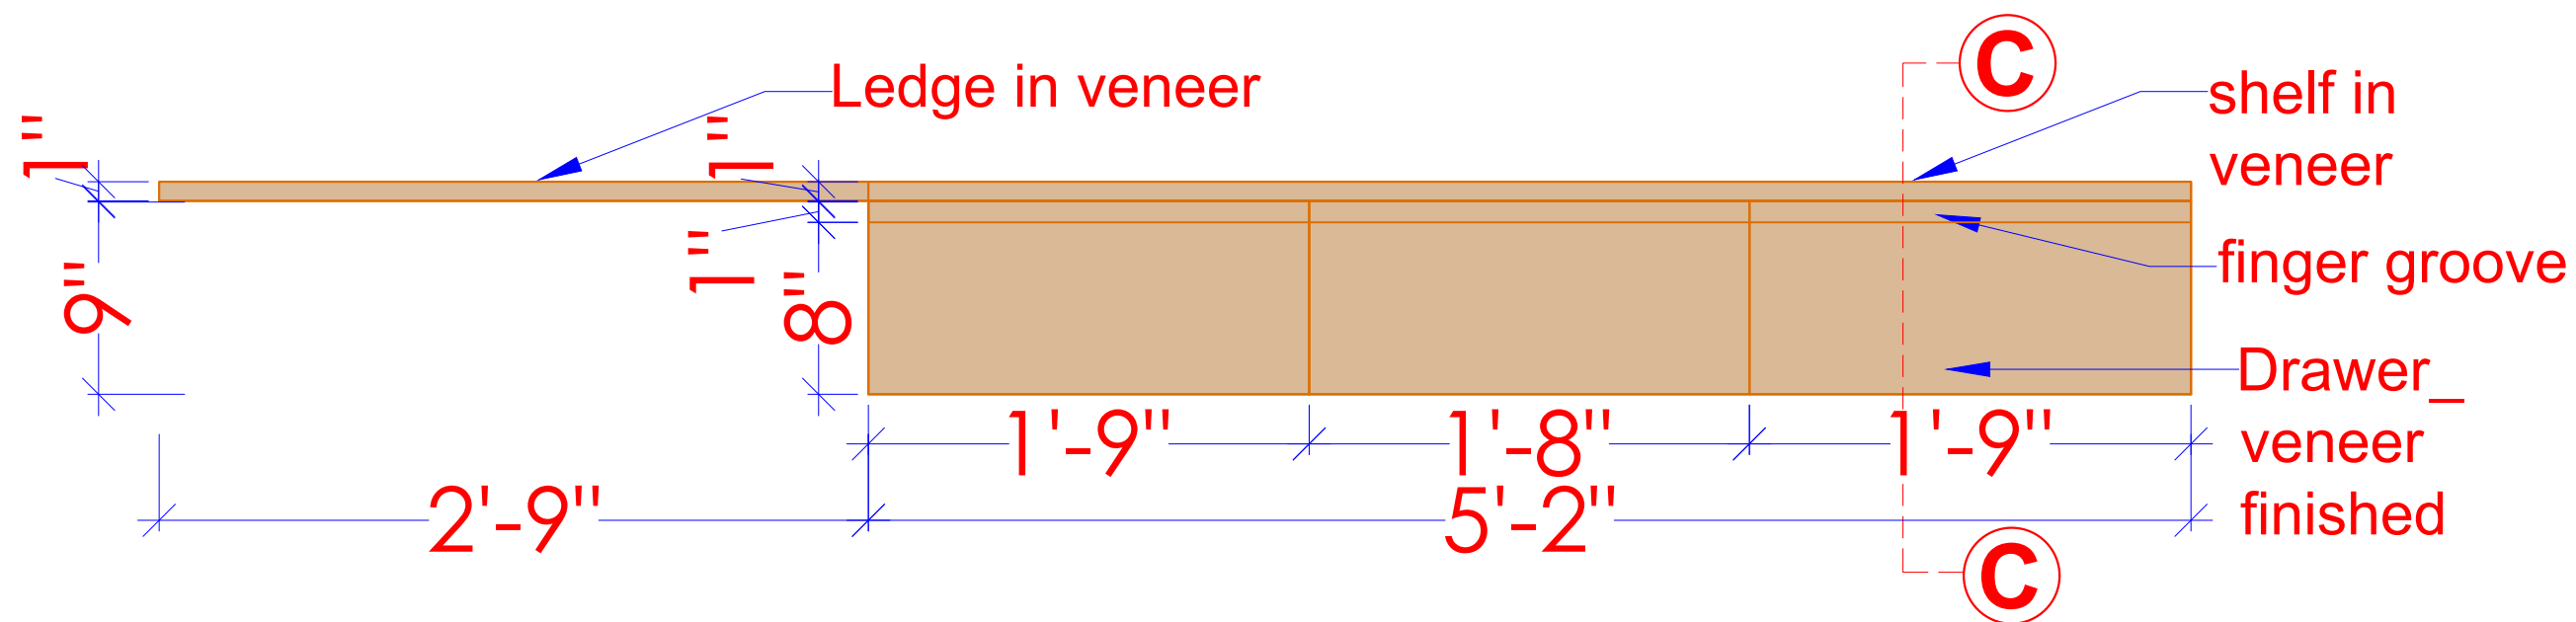


TV UNIT ELEVATION

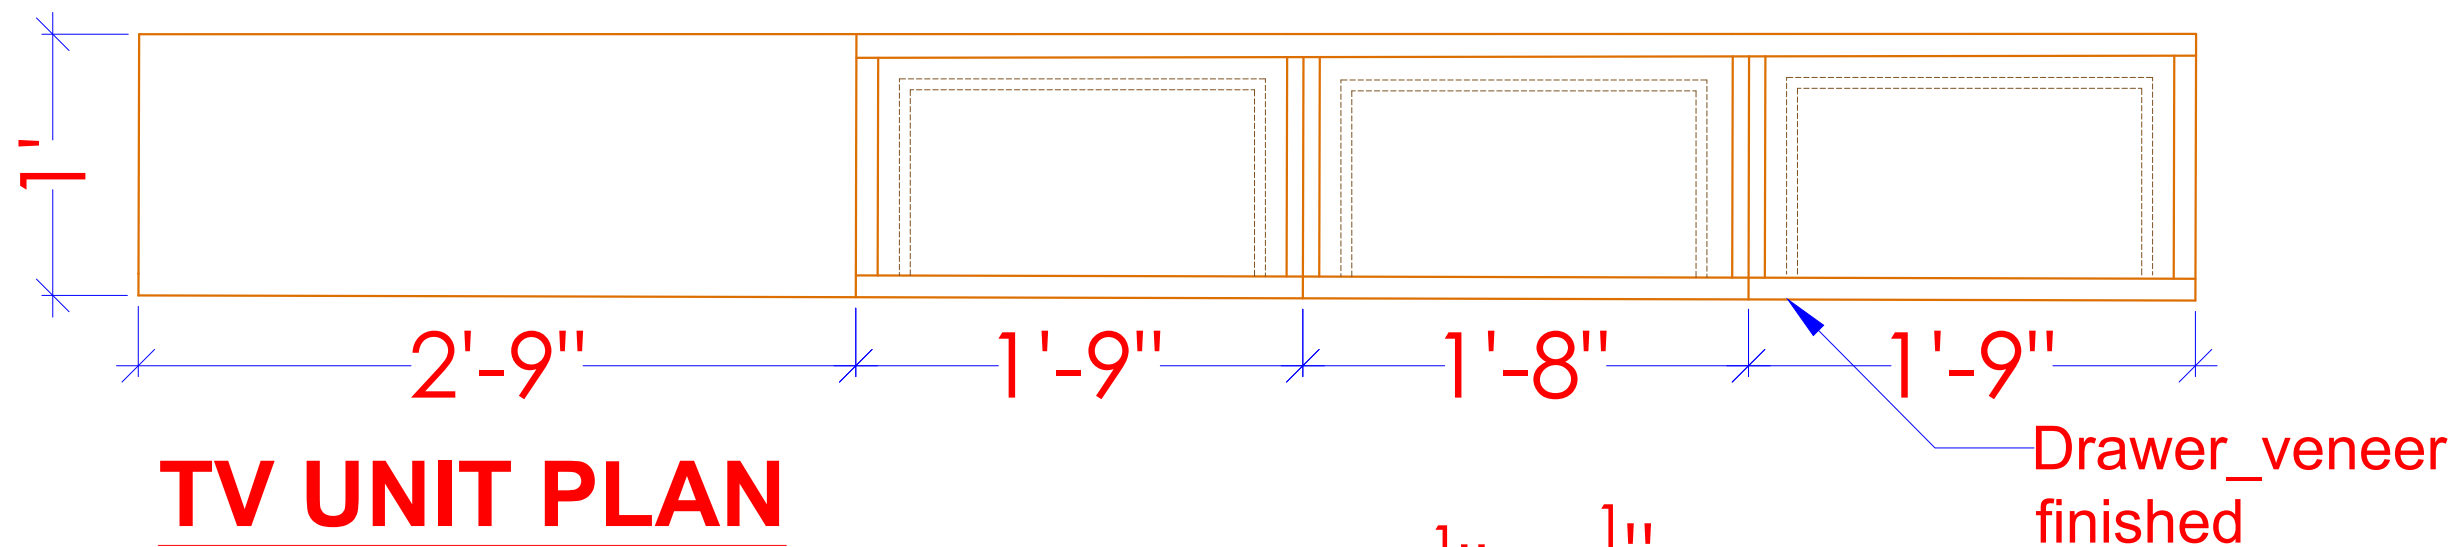

TV UNIT PLAN

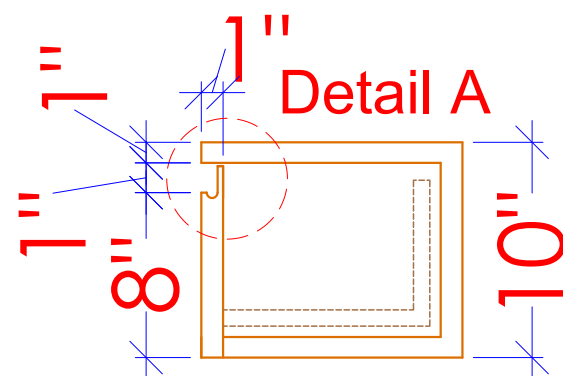

SECTION - CC'

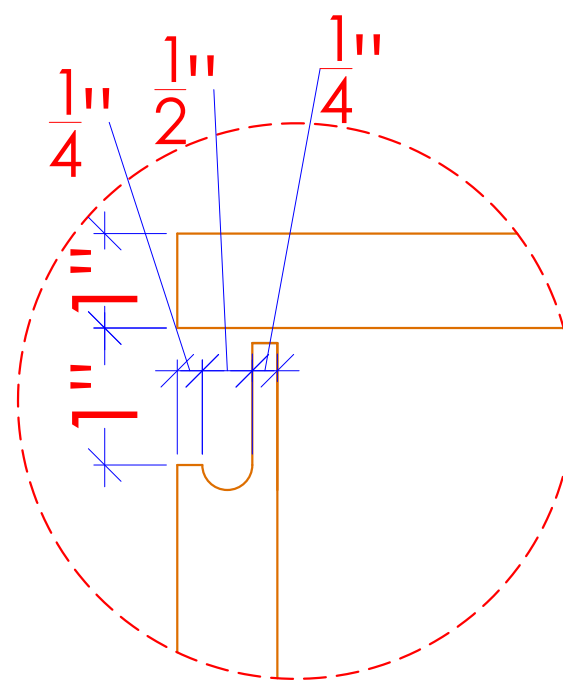

Detail A

DRAWING TITLE :

LIVING ROOM
TV UNIT DETAIL

NOTES:

- * DO NOT SCALE THE DRAWING.
- * ALL DIMENSIONS ARE IN FEET \ INCHES.
- * ANY DISCREPANCY IN THE DRAWING TO BE BROUGHT IN THE DESIGNER'S NOTICE BEFORE IMPLEMENTATION ON SITE.

SITE ADDRESS:

SAVAD
VADODARA

CLIENT NAME:

RONAK PANCHOLI

DATE:

02-06-2025

NORTH:

DRAWING DETAIL

REVISION NO.

R1 R2 R3

REVISED DATE:

12/02/26

SCALE:

N.T.S

DRAWN BY:

ARCHANA

CHECKED BY:

MITTAL


www.mayaspace.studio

mayaspace.studio@gmail.com

+918980144077

@mayaspace.studio



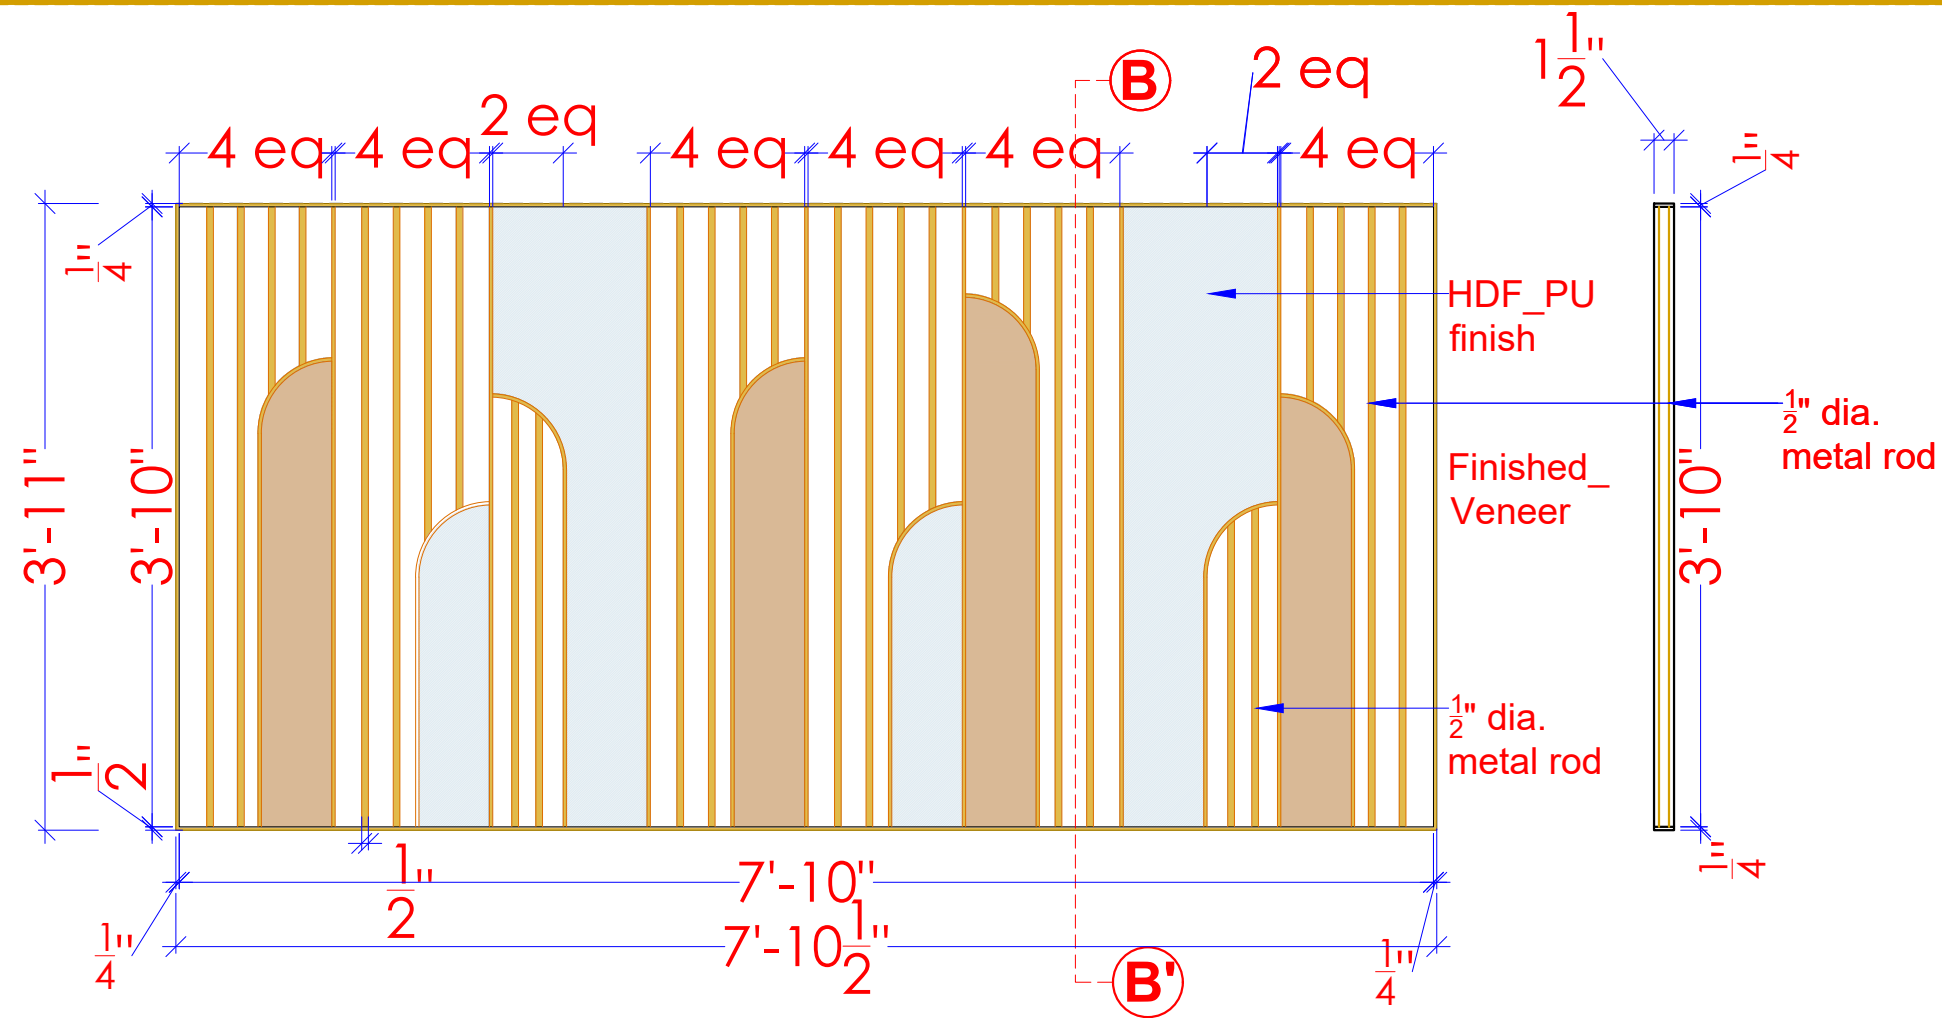


TV WALL ELEVATION

SECTION BB'



TV WALL PLAN

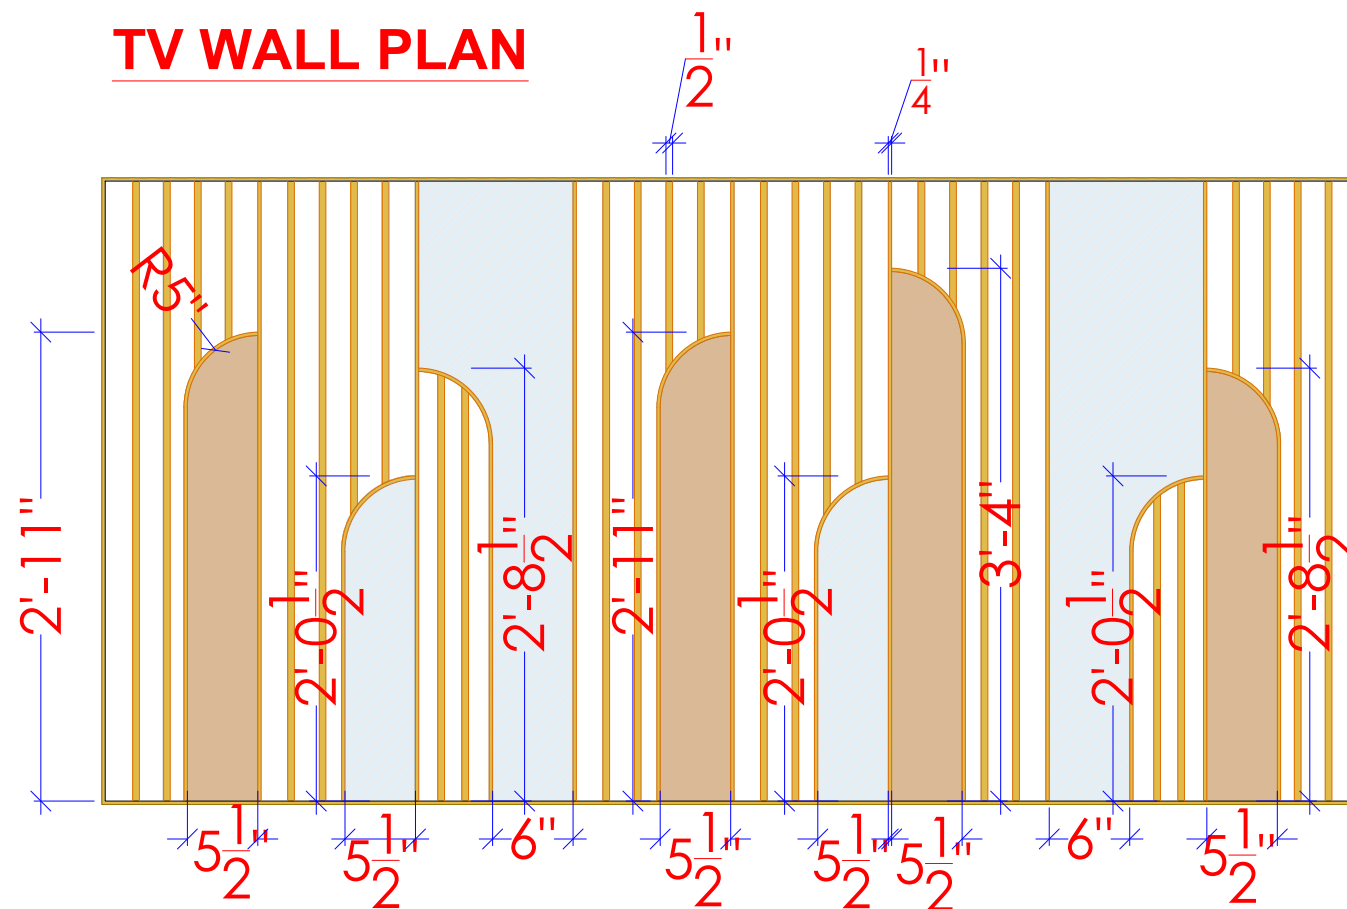

DRAWING TITLE :

LIVING ROOM
TV UNIT WALL DETAIL

NOTES:

- * DO NOT SCALE THE DRAWING.
- * ALL DIMENSIONS ARE IN FEET \ INCHES.
- * ANY DISCREPANCY IN THE DRAWING TO BE BROUGHT IN THE DESIGNER'S NOTICE BEFORE IMPLEMENTATION ON SITE.

SITE ADDRESS:

SAVAD
VADODARA

CLIENT NAME:

RONAK PANCHOLI

DATE:

02-06-2025

NORTH:

DRAWING DETAIL

REVISION NO.

R1 R2 R3

REVISED DATE:

12/02/26

SCALE:

N.T.S

DRAWN BY:


ARCHANA

CHECKED BY:

MITTAL

www.mayaspace.studio
mayaspace.studio@gmail.com
+918980144077
@mayaspace.studio



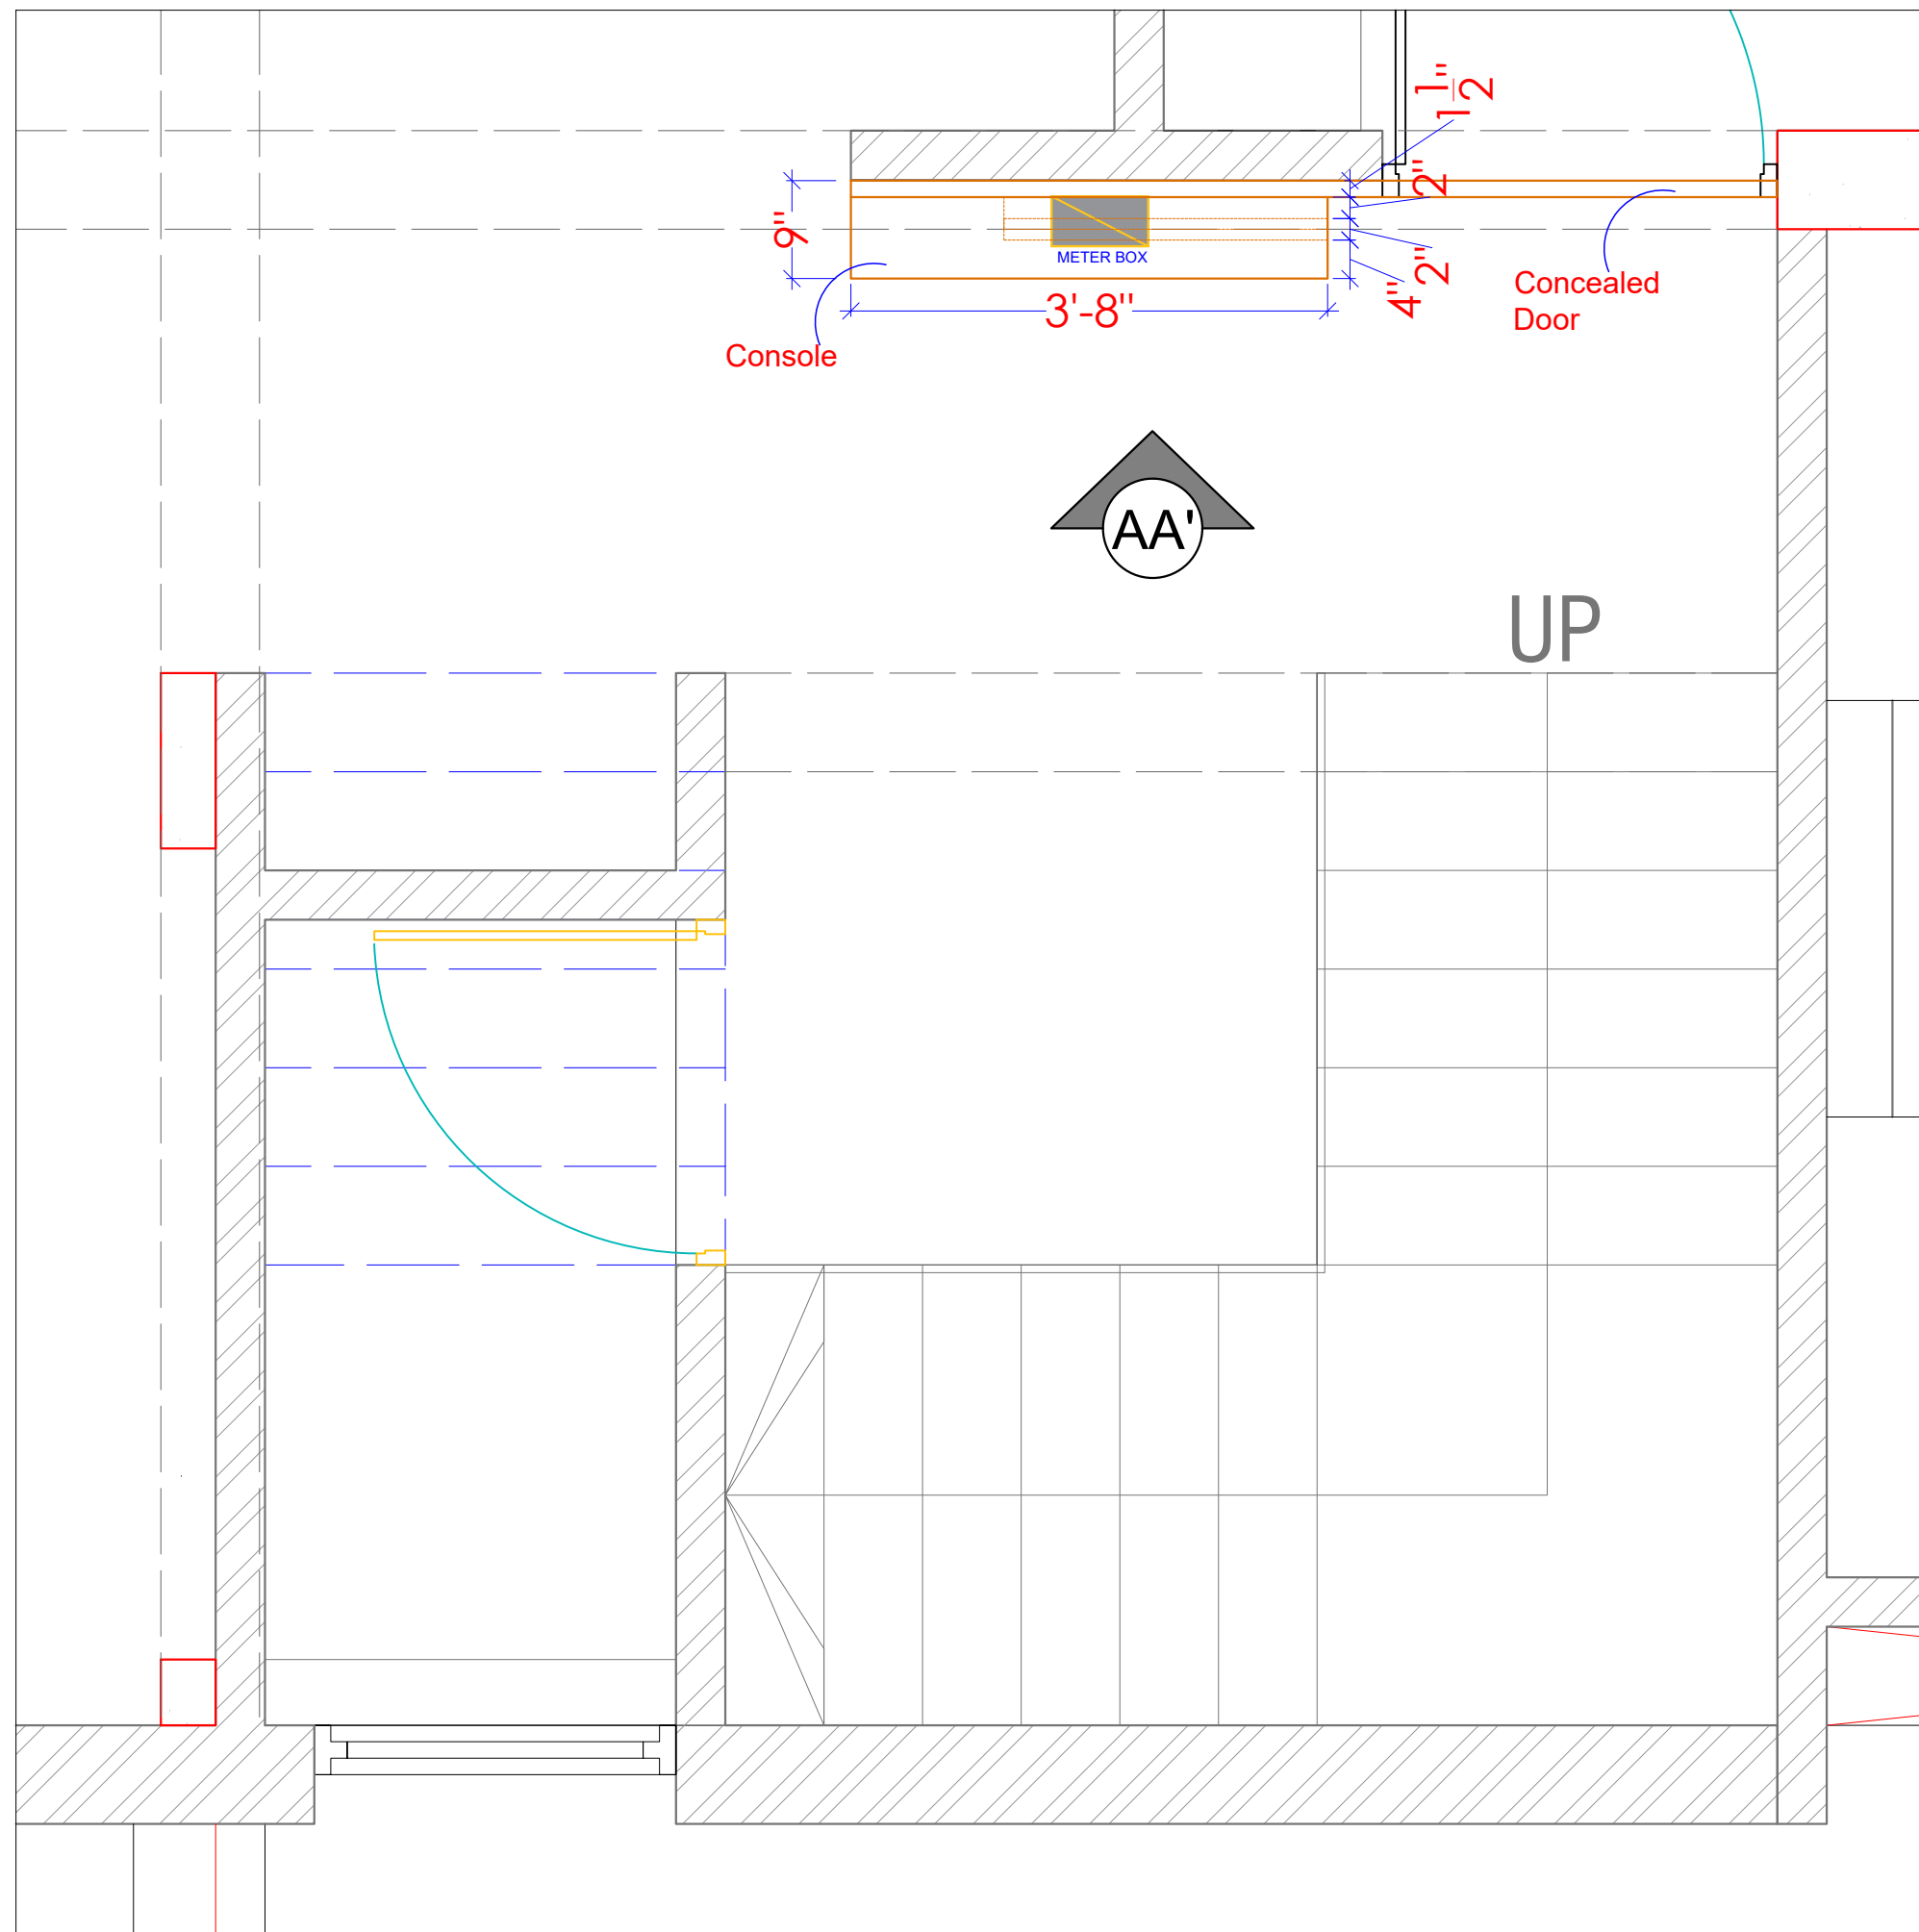

DRAWING TITLE :

LIVING ROOM PASSAGE DESIGN

NOTES:

- * DO NOT SCALE THE DRAWING.
- * ALL DIMENSIONS ARE IN FEET \ INCHES.
- * ANY DISCREPENCY IN THE DRAWING TO BE BROUGHT IN THE DESIGNER'S NOTICE BEFORE IMPLEMENTATION ON SITE.

SITE ADDRESS:

SAVAD
VADODARA

CLIENT NAME:

RONAK PANCHOLI

DATE: 02-06-2025


NORTH:

DRAWING DETAIL

REVISION NO.	R1	R2	R3
REVISED DATE:	12/02/26		
SCALE:	N.T.S		
DRAWN BY:	ARCHANA		
CHECKED BY:	MITTAL		

	www.mayaspace.studio
	mayaspace.studio@gmail.com
	+918980144077
	@mayaspace.studio



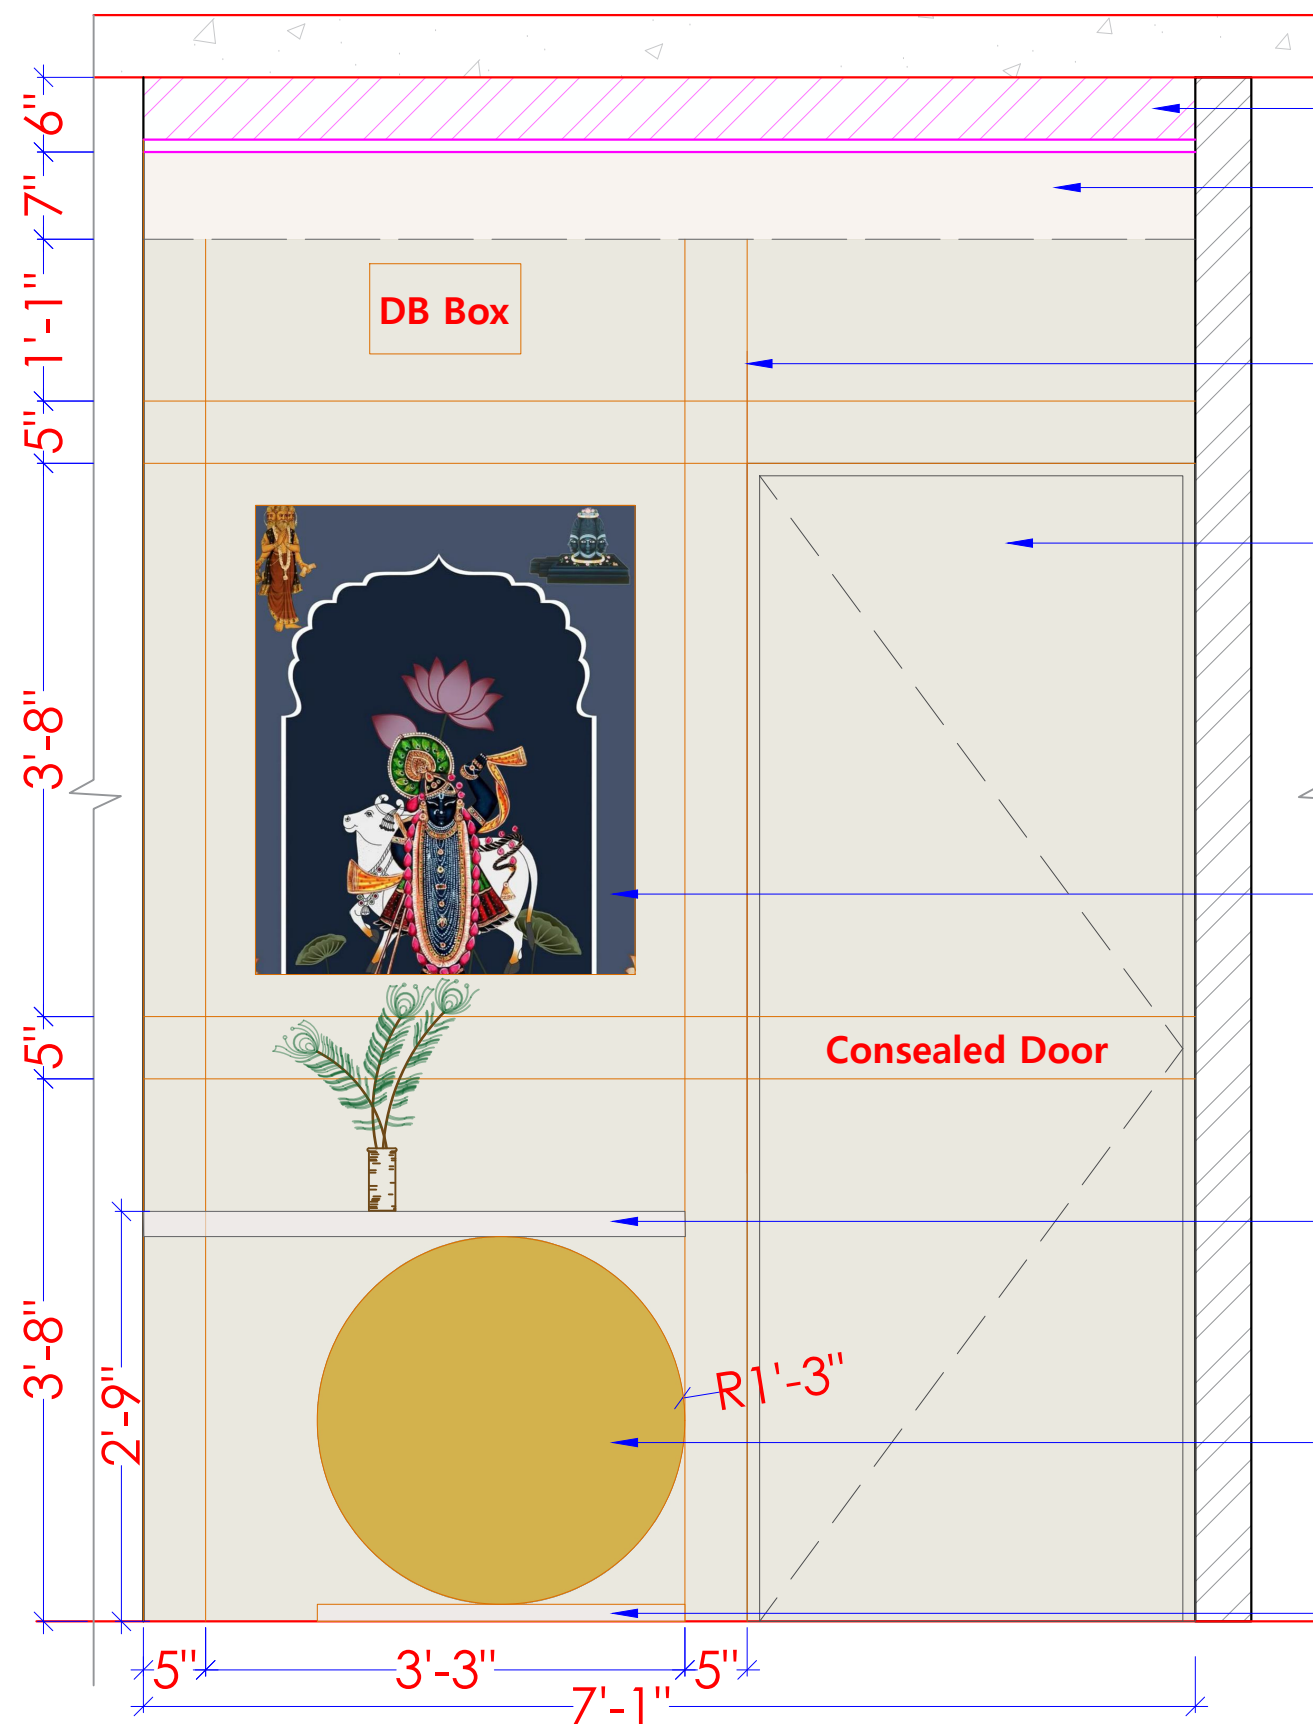

ELEVATION - AA'

False Ceiling

Wall Paint

DB Box

4X4MM
Groove

Panelling_Texture
finish


Painting

Consealed Door


Finished in
Veneer

Finished_Antique
Brass

Finished in
veneer

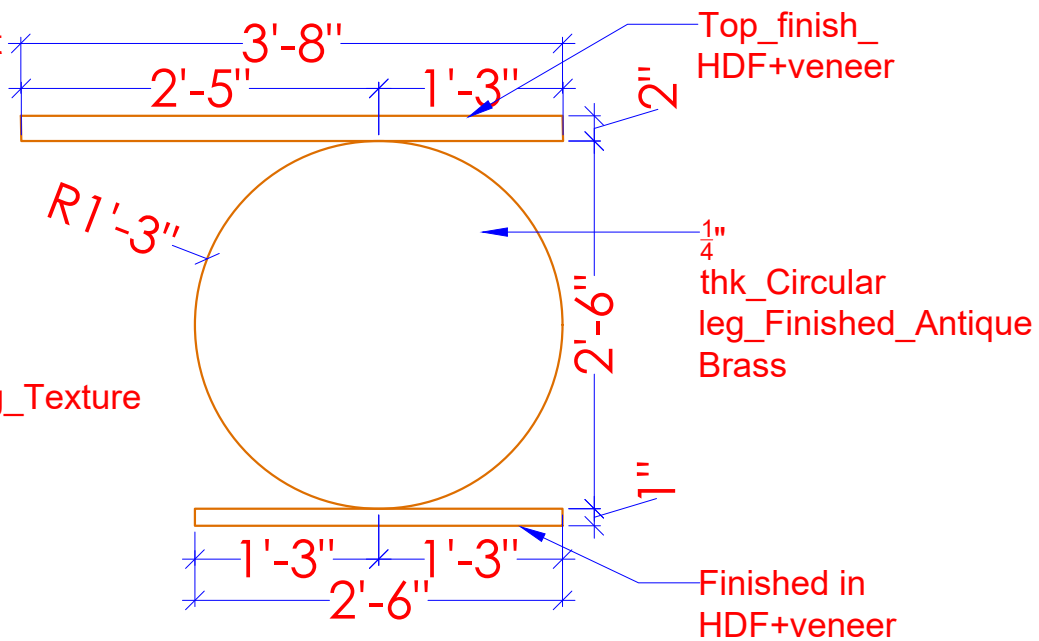

CONSOLE ELEVATION

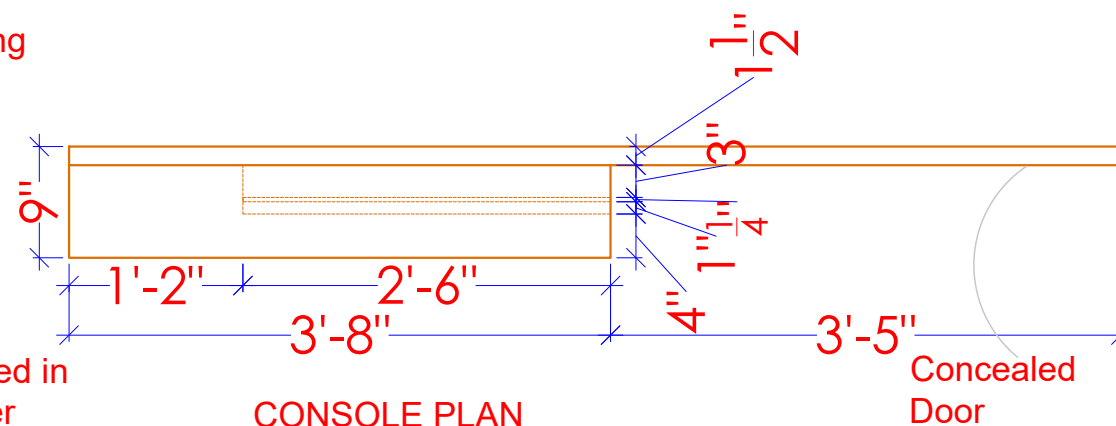

CONSOLE PLAN

DRAWING TITLE :

LIVING ROOM
PASSAGE DESIGN

NOTES:

- * DO NOT SCALE THE DRAWING.
- * ALL DIMENSIONS ARE IN FEET \ INCHES.
- * ANY DISCREPANCY IN THE DRAWING TO BE BROUGHT IN THE DESIGNER'S NOTICE BEFORE IMPLEMENTATION ON SITE.

SITE ADDRESS:

SAVAD
VADODARA

CLIENT NAME:

RONAK PANCHOLI

DATE: 02-06-2025






NORTH:

DRAWING DETAIL

REVISION NO.	R1	R2	R3
REVISED DATE:	12/02/26		
SCALE:	N.T.S		
DRAWN BY:	ARCHANA		
CHECKED BY:	MITTAL		

www.mayaspace.studio
mayaspace.studio@gmail.com
+918980144077
@mayaspace.studio



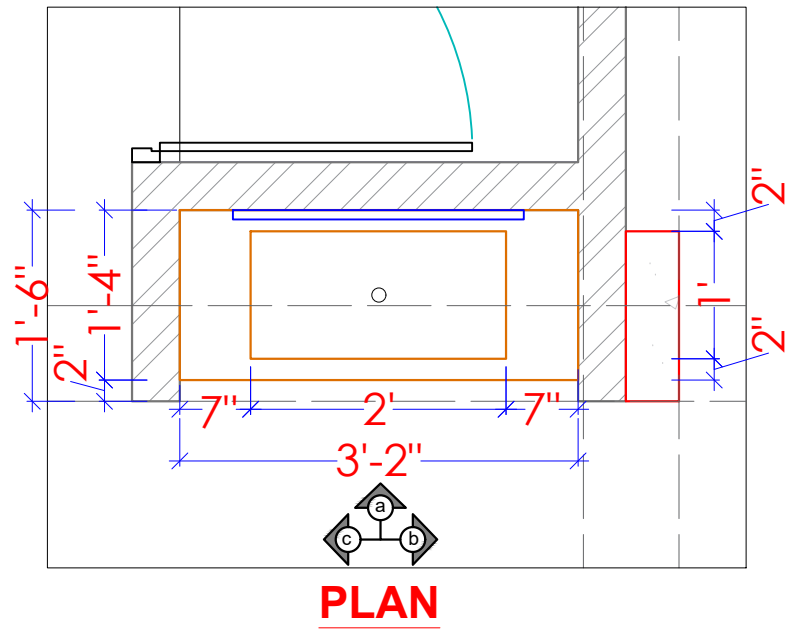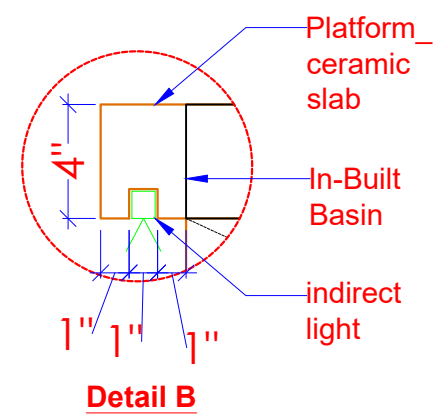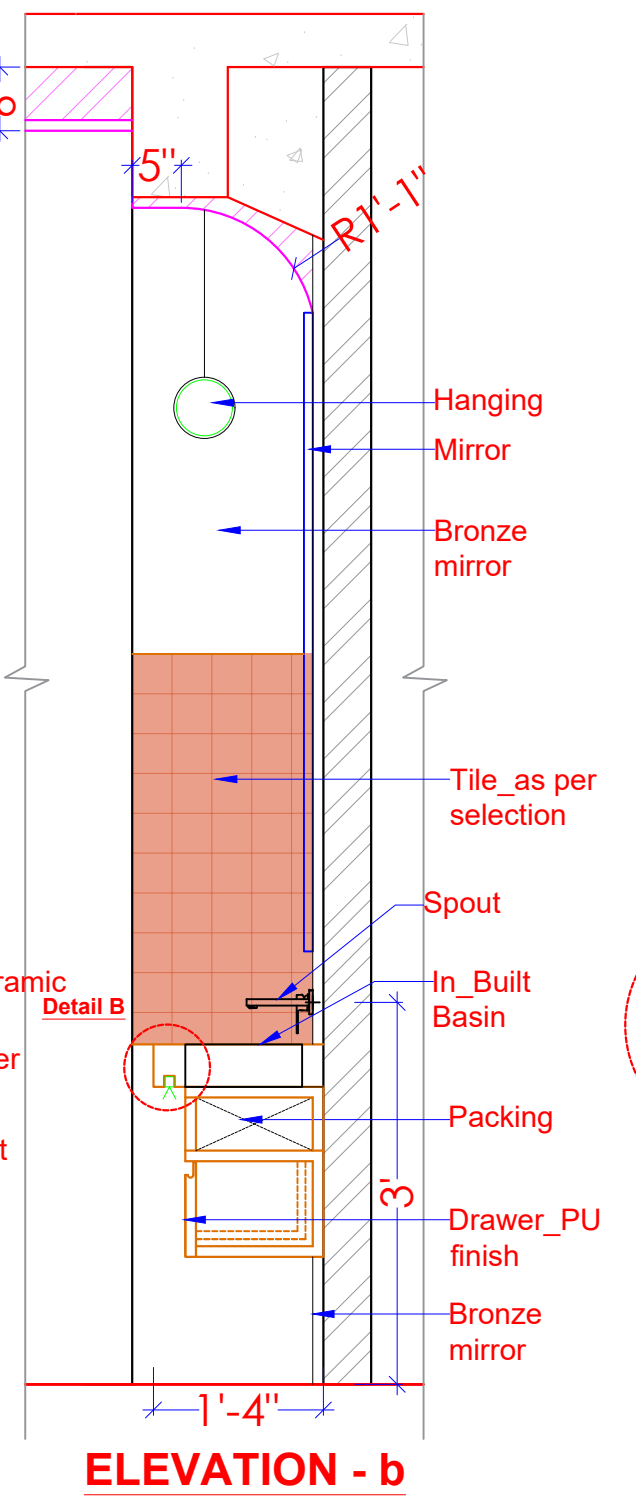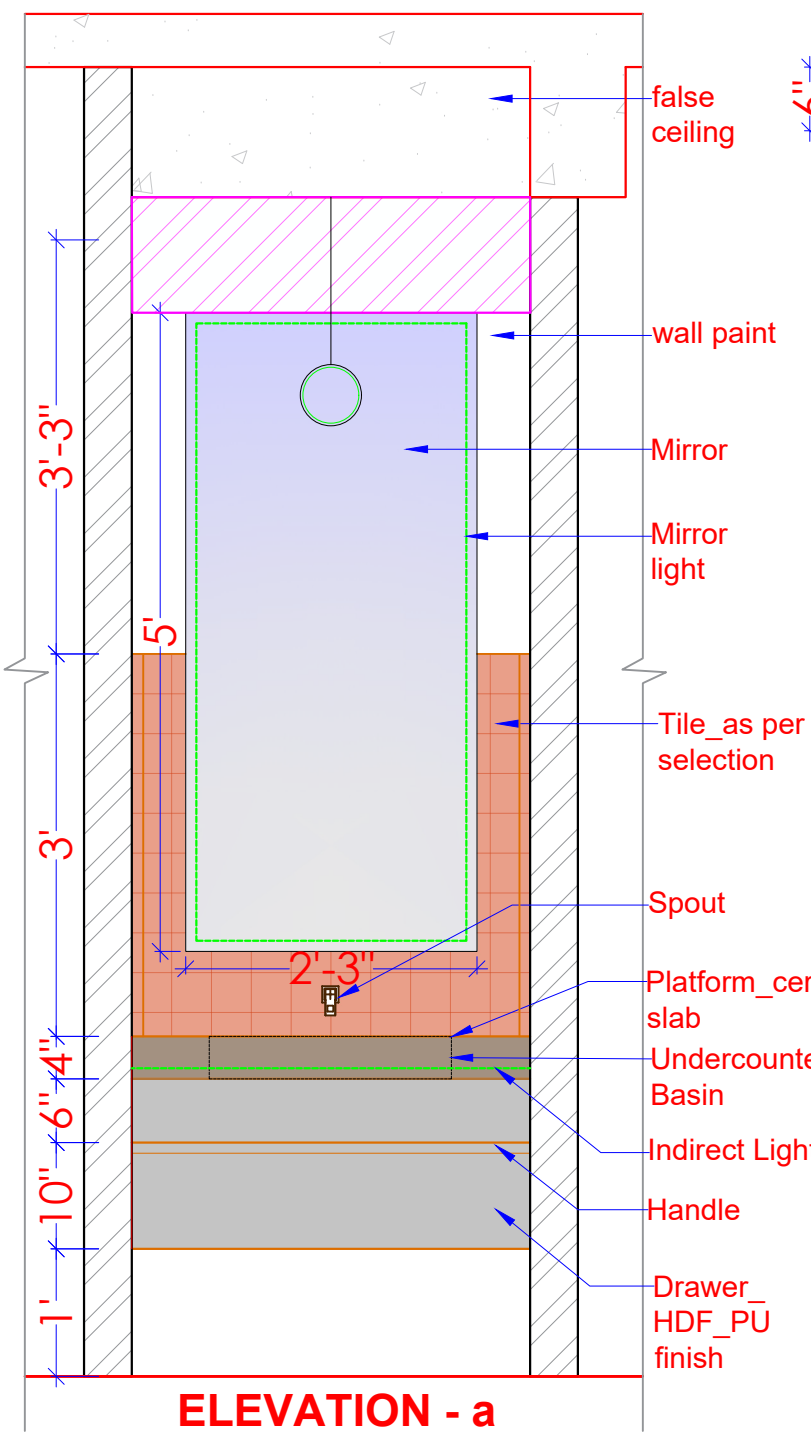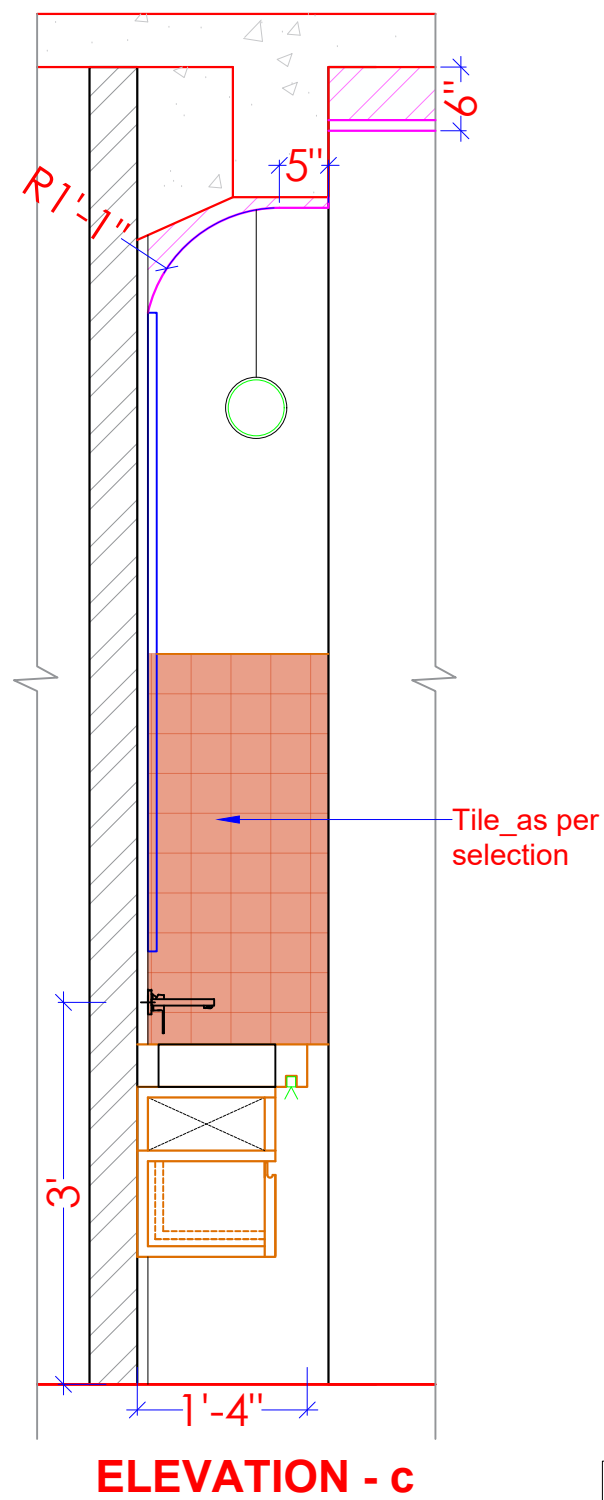

DRAWING TITLE :

**LIVING ROOM
BASIN AREA**

NOTES:

- * DO NOT SCALE THE DRAWING.
- * ALL DIMENSIONS ARE IN FEET \ INCHES.
- * ANY DISCREPANCY IN THE DRAWING TO BE BROUGHT IN THE DESIGNER'S NOTICE BEFORE IMPLEMENTATION ON SITE.

SITE ADDRESS:

**SAVAD
VADODARA**

CLIENT NAME:

RONAK PANCHOLI

DATE: 02-06-2025

NORTH:

DRAWING DETAIL

REVISION NO.	R1	R2	R3
REVISED DATE:	12/02/26		
SCALE:	N.T.S		
DRAWN BY:	ARCHANA		
CHECKED BY:	MITTAL		


www.mayaspace.studio

mayaspace.studio@gmail.com


+918980144077

@mayaspace.studio


**Maya
SPACE STUDIO**

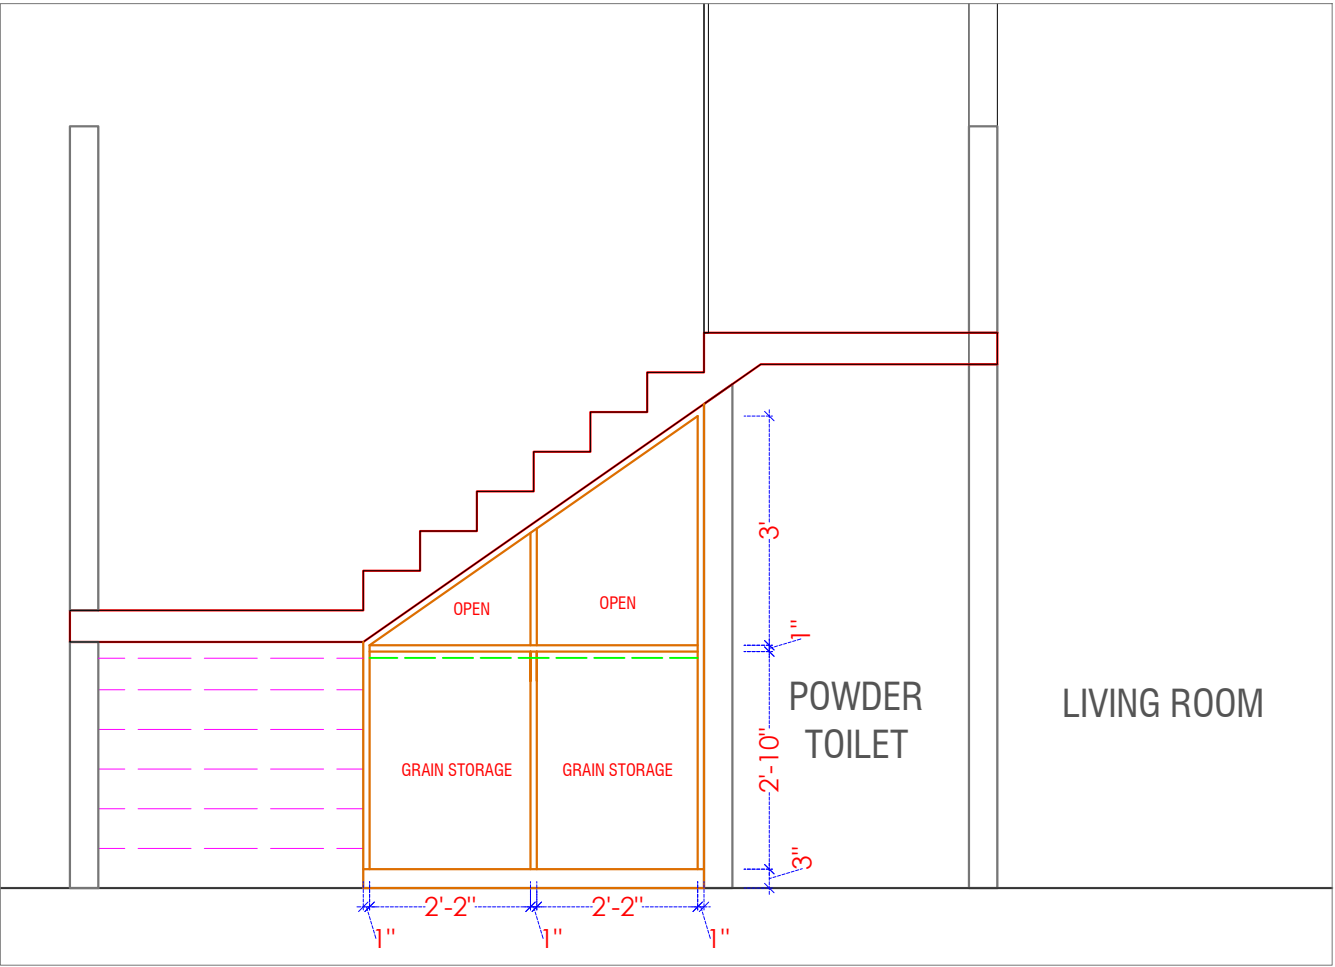


SECTION AA'

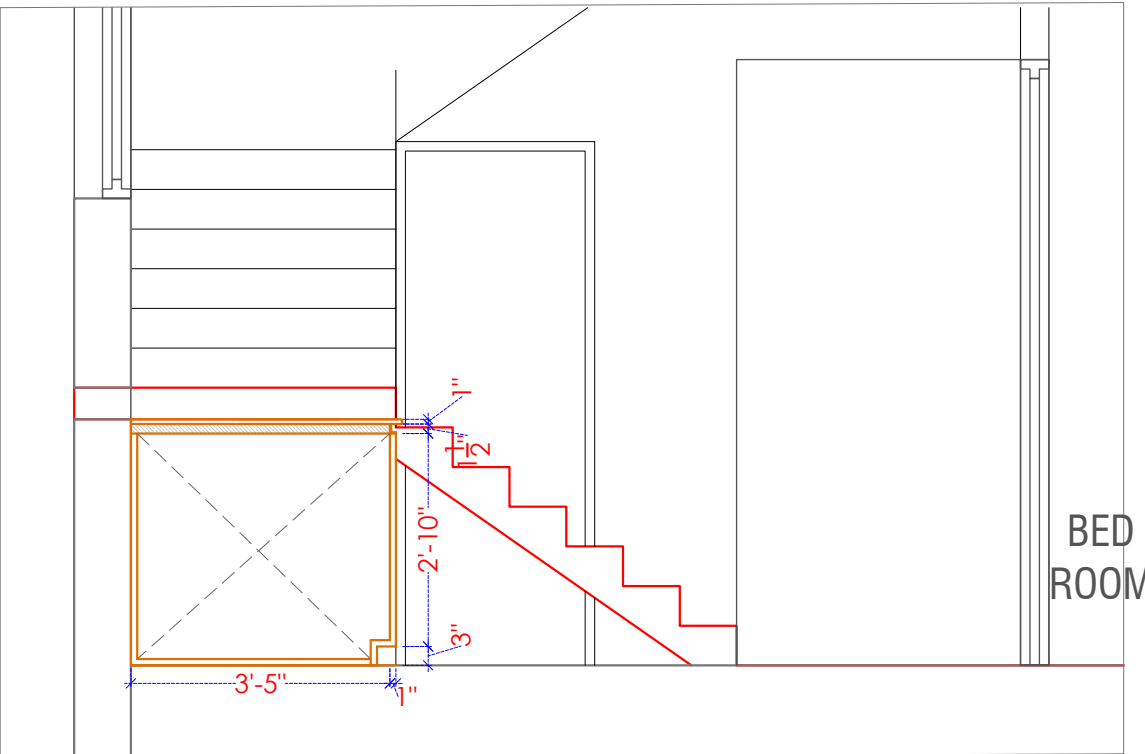

SECTION BB'

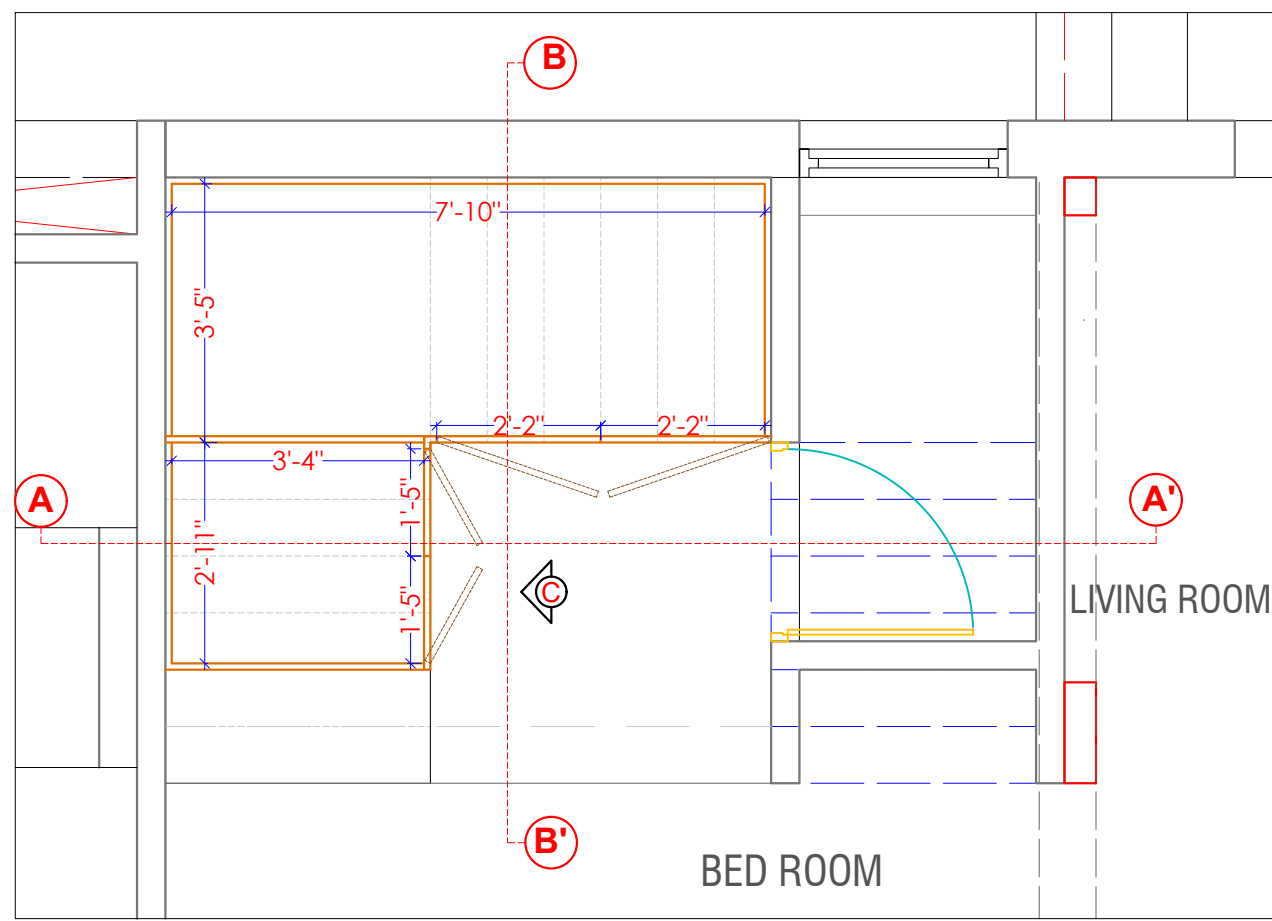

PLAN

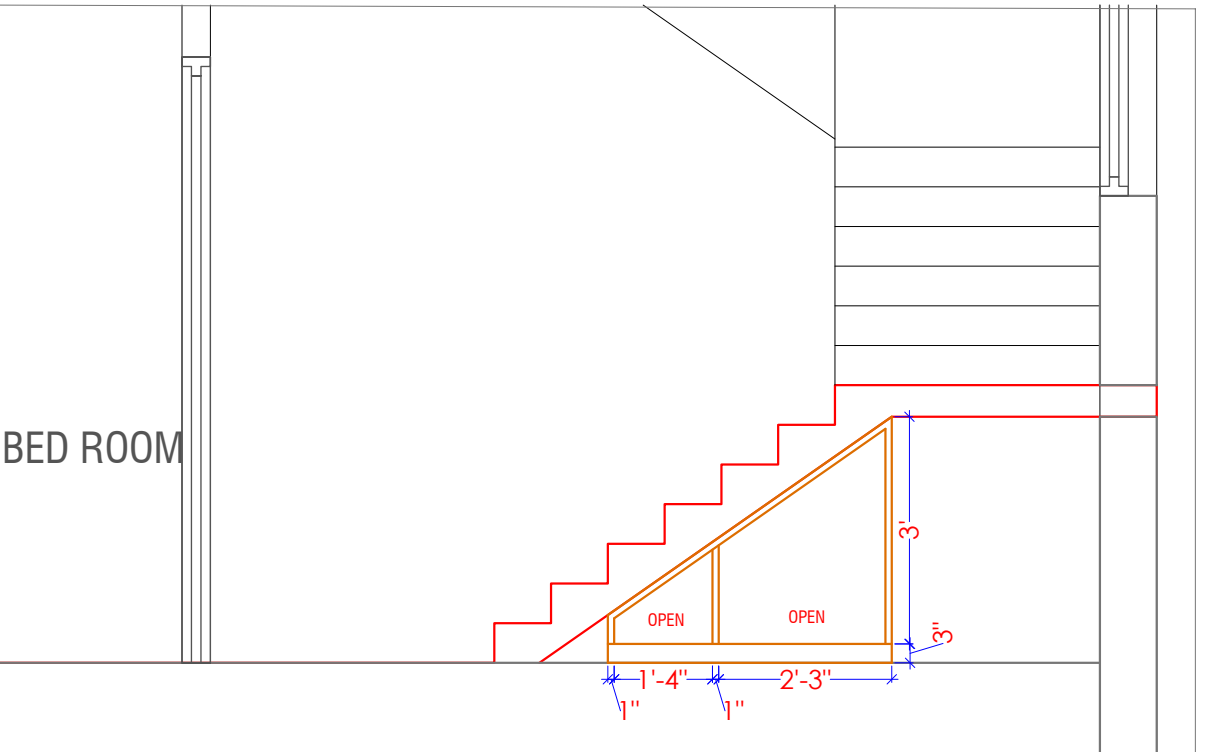

ELEVATION C

NOTES:

- * DO NOT SCALE THE DRAWING.
- * ALL DIMENSIONS ARE IN FEET \ INCHES.
- * ANY DISCREPENCY IN THE DRAWING TO BE BROUGHT IN THE DESIGNER'S NOTICE BEFORE IMPLEMENTATION ON SITE.

DRAWING TITLE :

GF
BELOW STAIRCASE
STORAGE

SITE ADDRESS:

SAVAD
VADODARA

CLIENT NAME:

RONAK PANCHOLI

DATE:	02-06-2025
NORTH:	

DRAWING DETAIL

REVISION NO.	R1	R2	R3
REVISED DATE:	12/02/26		
SCALE:	N.T.S		
DRAWN BY:	PRASANNA		
CHECKED BY:	MITTAL		


www.mayaspace.studio

mayaspace.studio@gmail.com


+918980144077

@mayaspace.studio



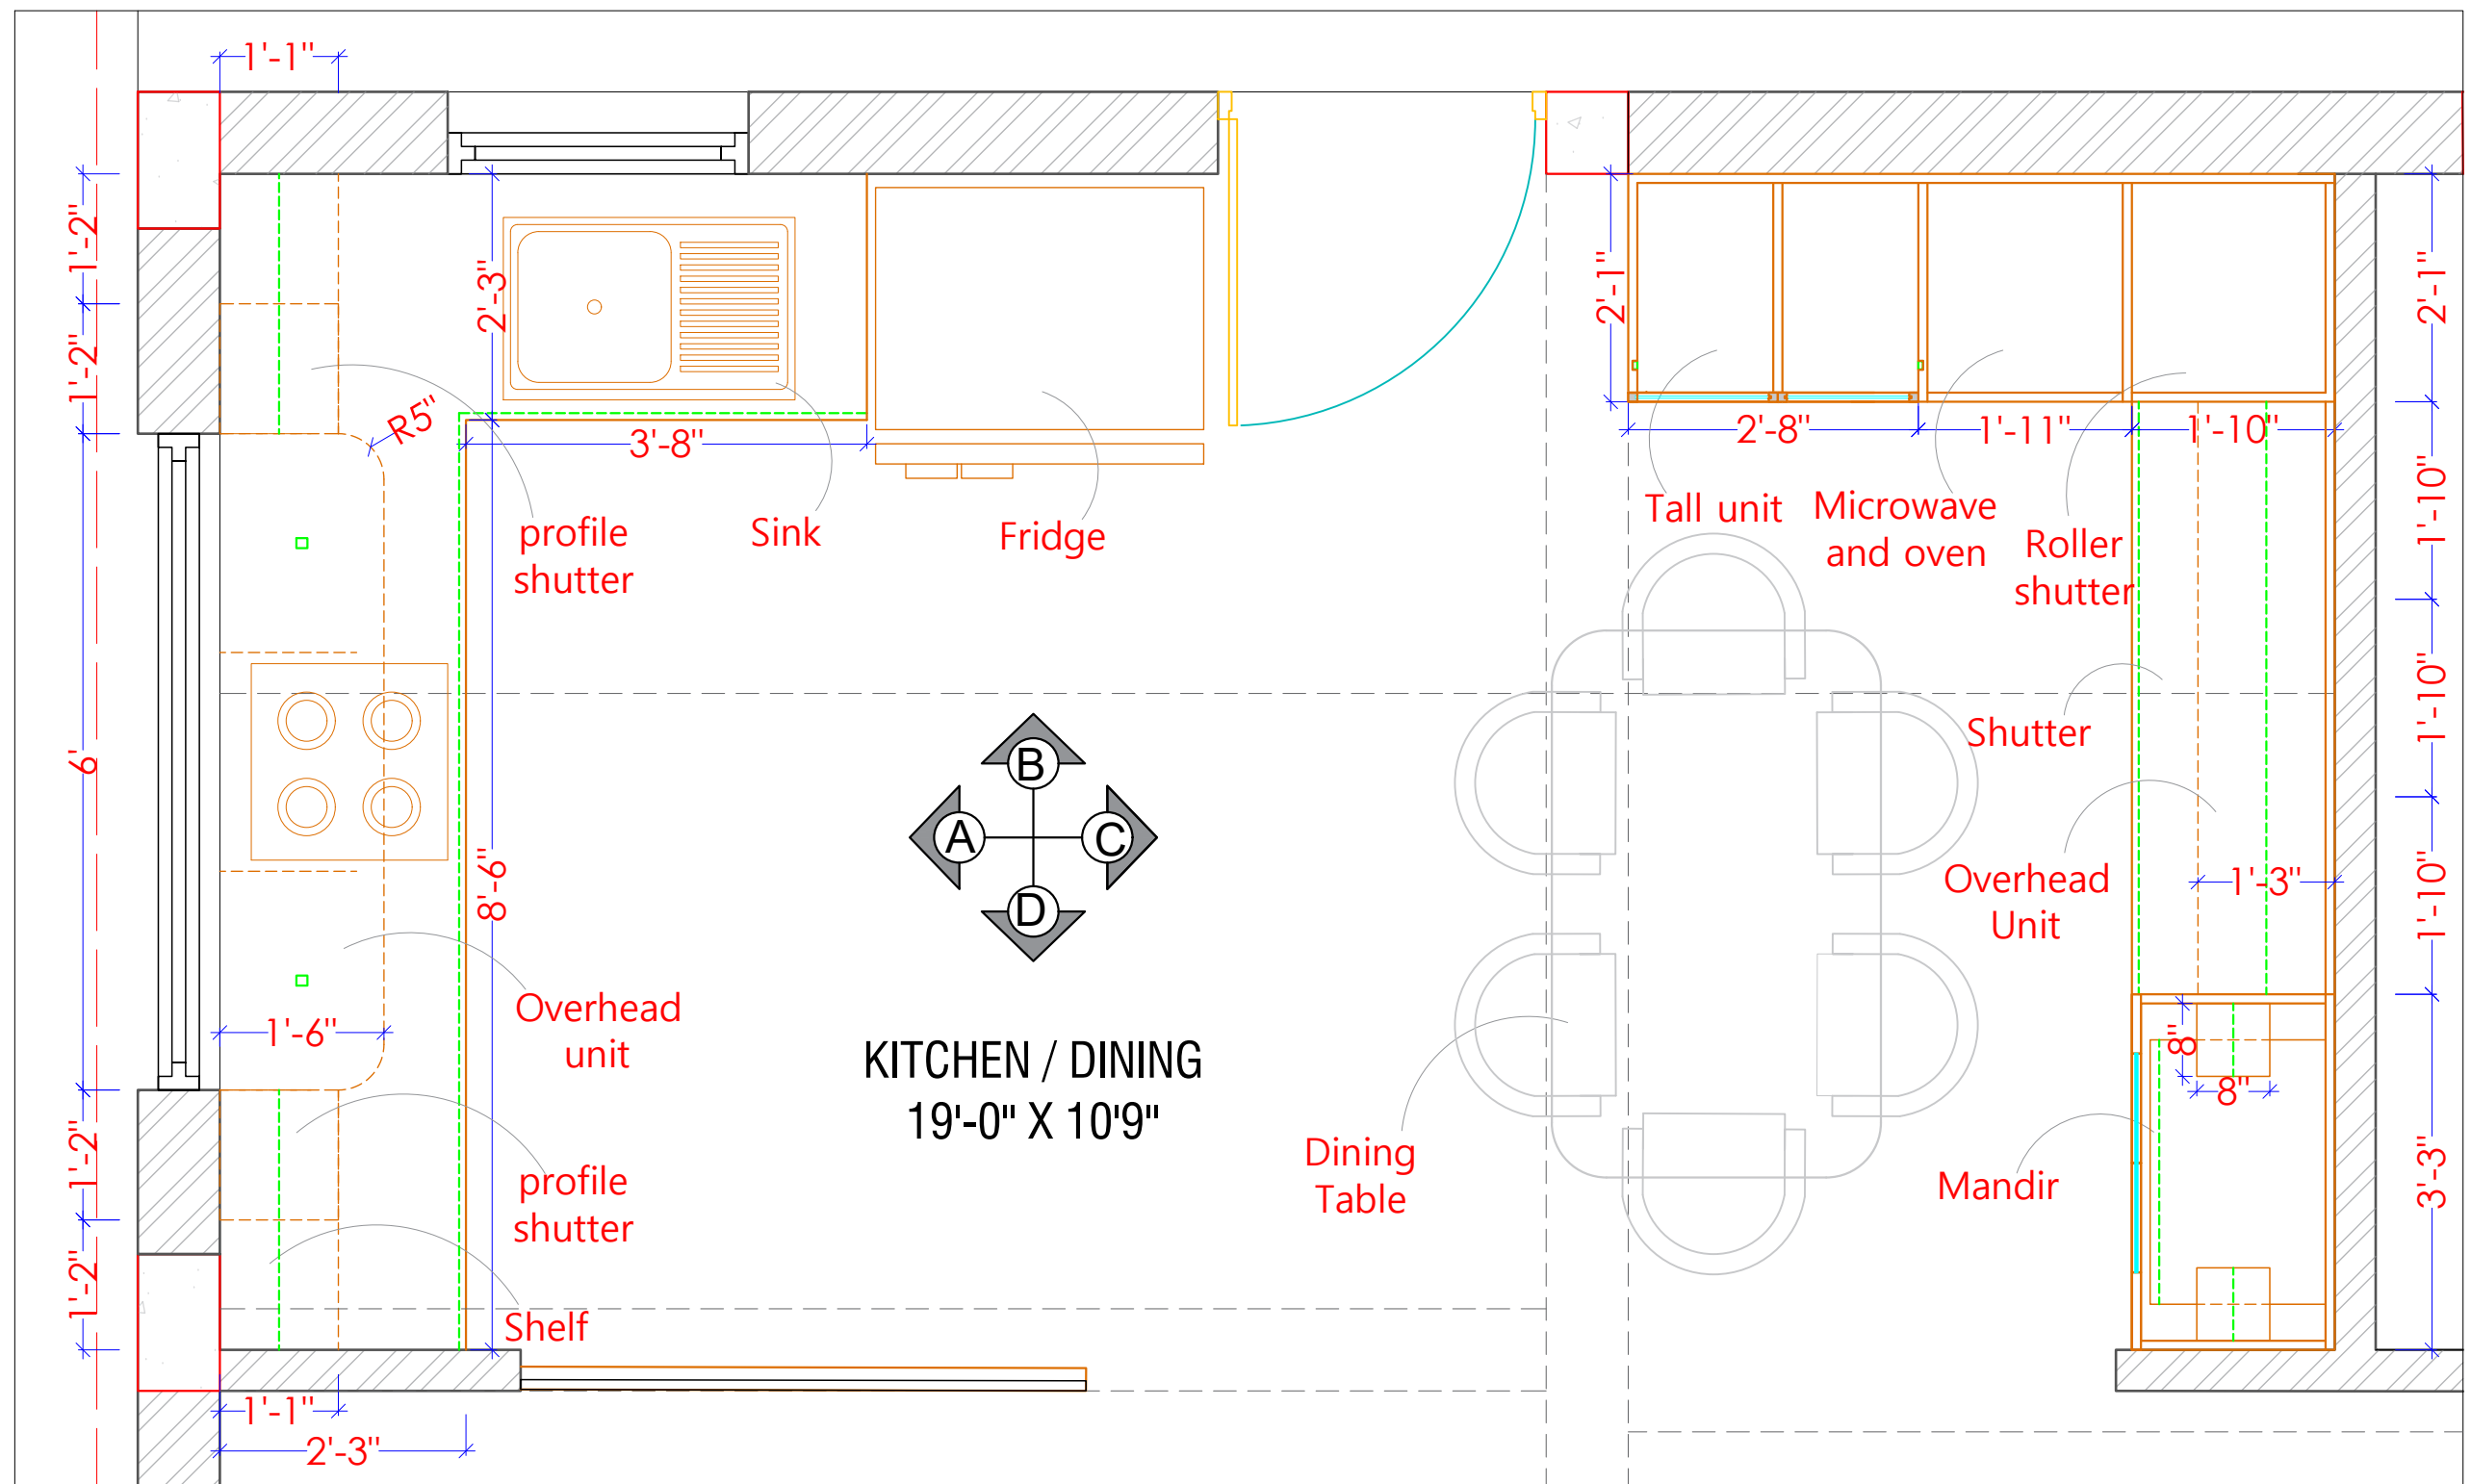

FURNITURE LAYOUT

 Provide light point in furniture	
Provide spot point in furniture	

DRAWING TITLE :

KITCHEN FURNITURE LAYOUT

NOTES:

- * DO NOT SCALE THE DRAWING.
- * ALL DIMENSIONS ARE IN FEET \ INCHES.
- * ANY DISCREPANCY IN THE DRAWING TO BE BROUGHT IN THE DESIGNER'S NOTICE BEFORE IMPLEMENTATION ON SITE.

SITE ADDRESS:

SAVAD
VADODARA

CLIENT NAME:

RONAK PANCHOLI

DATE:

02-06-2025

NORTH:




DRAWING DETAIL

REVISION NO.	R1	R2	R3
REVISED DATE:	12/02/26		
SCALE:	N.T.S		
DRAWN BY:	ARCHANA		
CHECKED BY:	MITTAL		

	www.mayaspace.studio
	mayaspace.studio@gmail.com
	+918980144077
	@mayaspace.studio



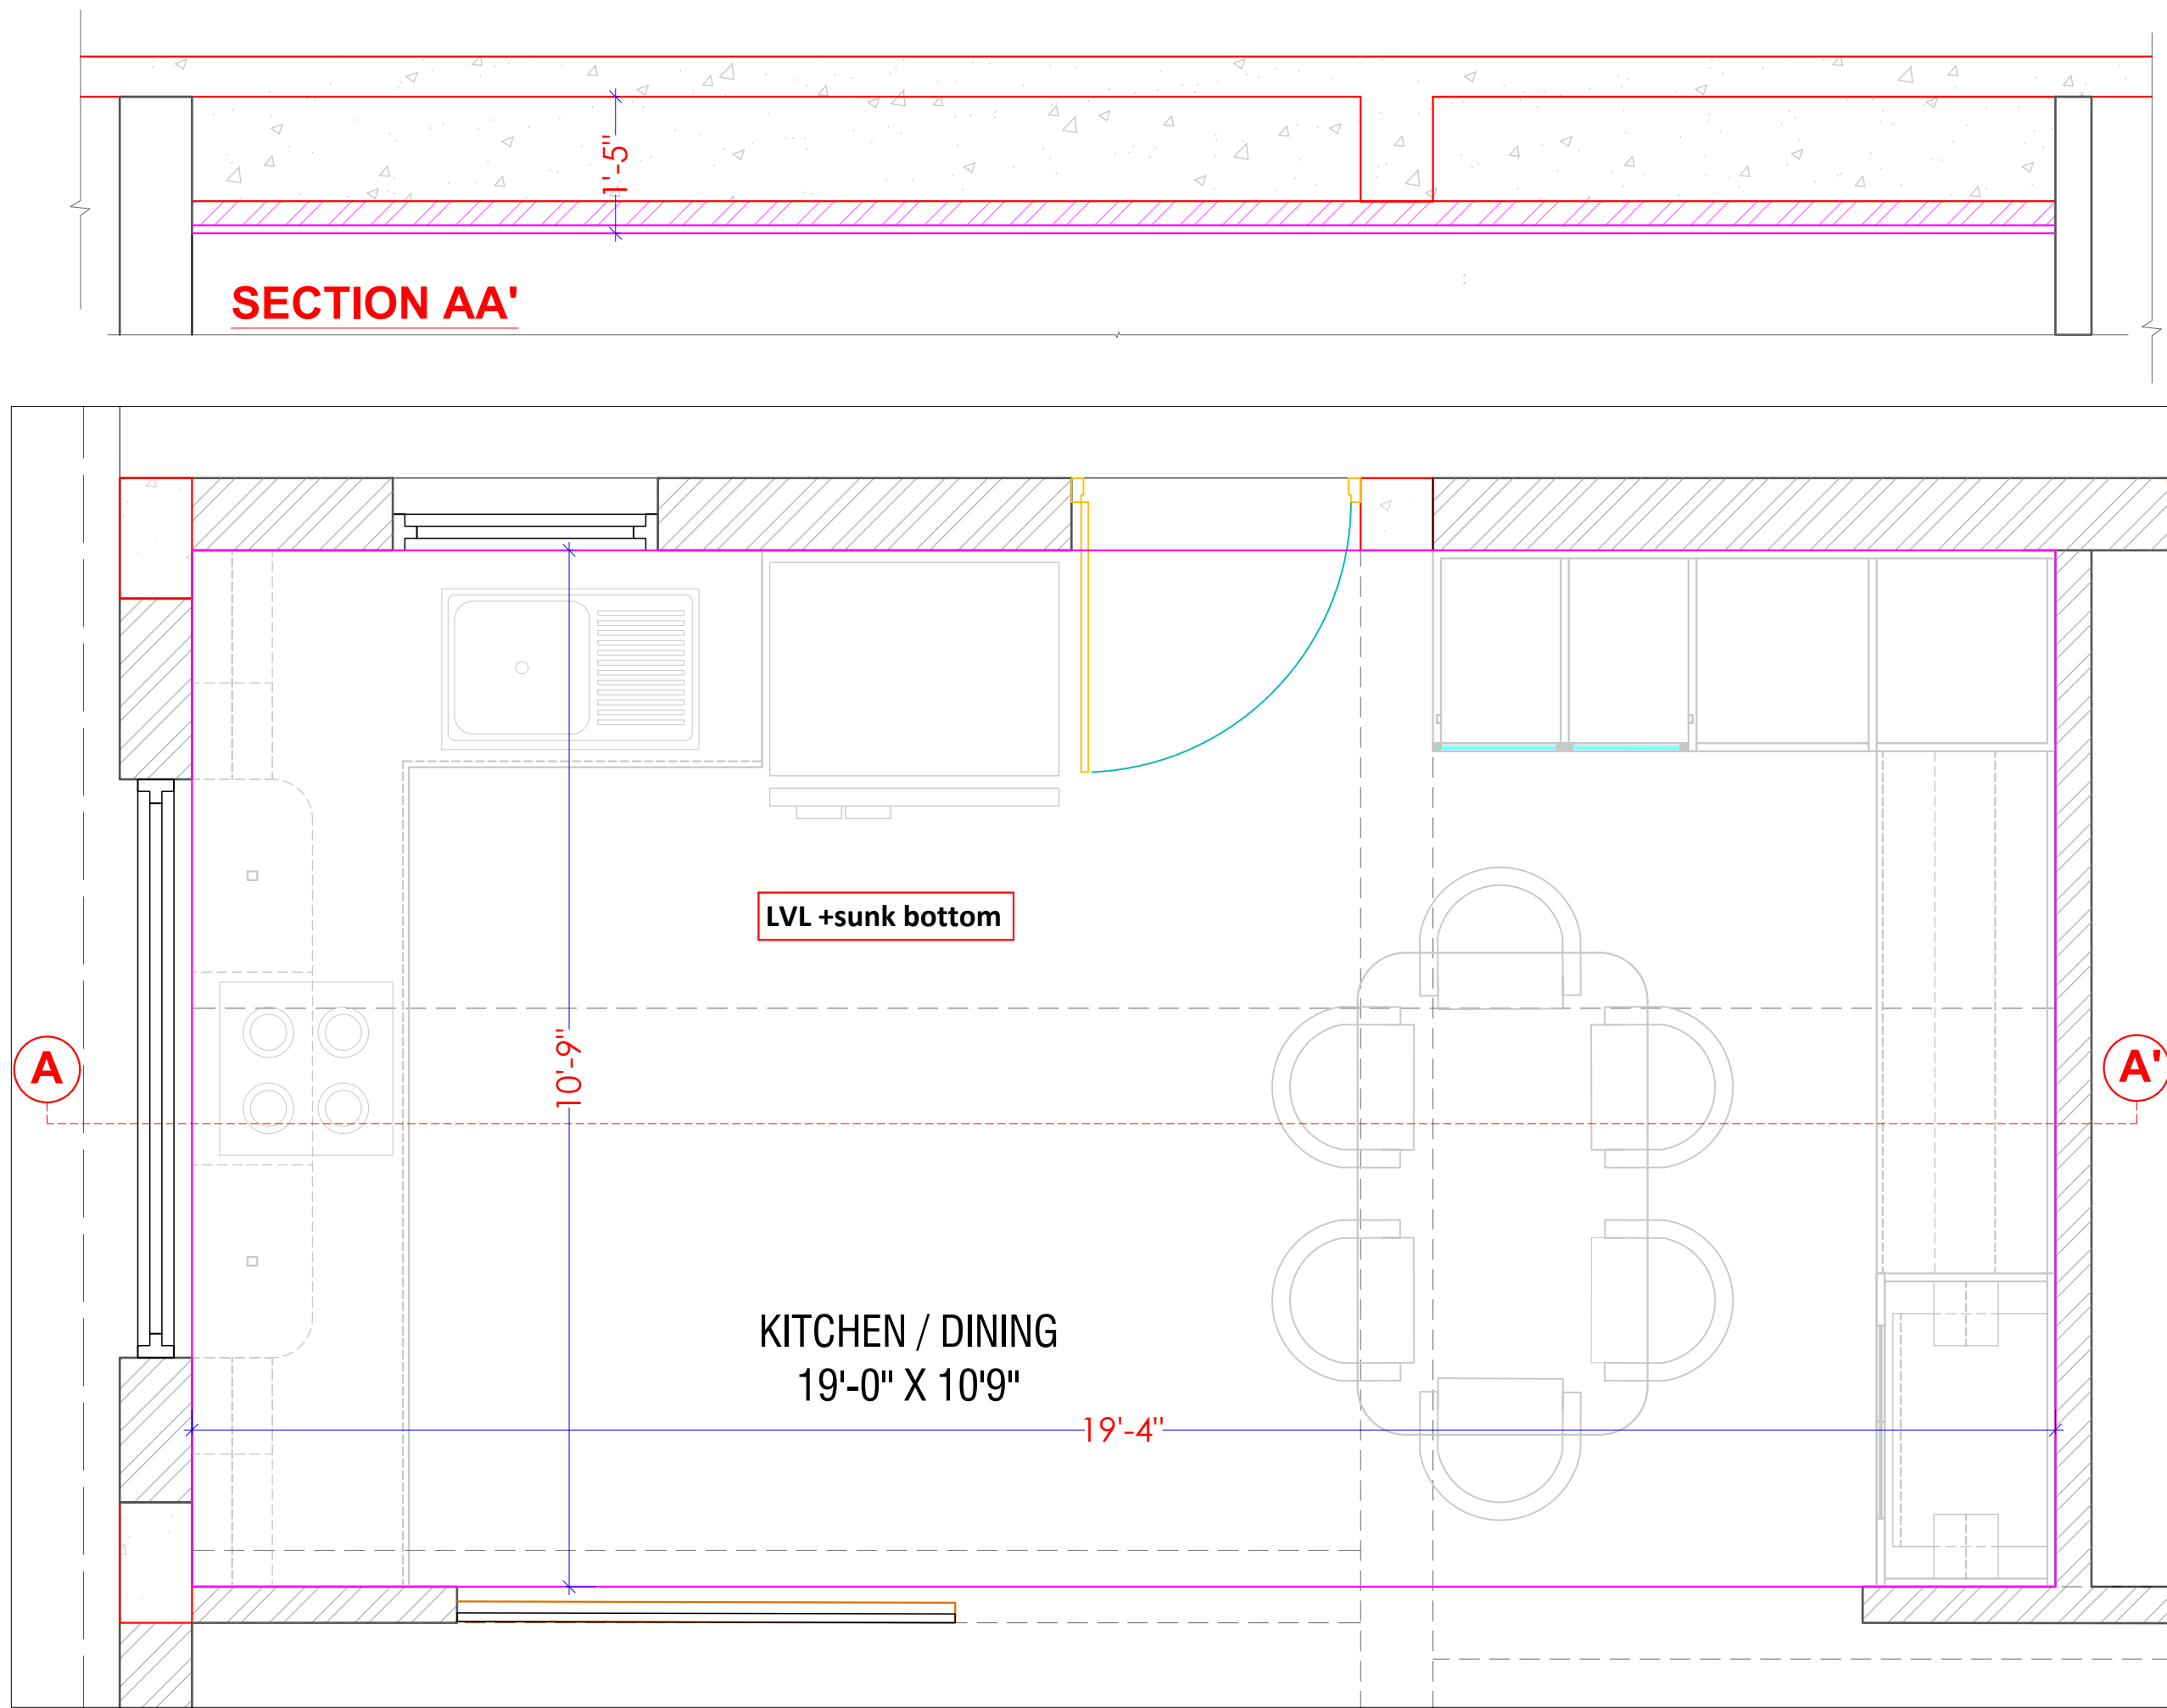

SECTION AA'

LVL +sunk bottom

KITCHEN / DINING
19'-0" X 10'-9"

19'-4"

A

A'

FALSE CEILING LAYOUT

DRAWING TITLE :

KITCHEN
FALSE CEILING LAYOUT

NOTES:

- * DO NOT SCALE THE DRAWING.
- * ALL DIMENSIONS ARE IN FEET \ INCHES.
- * ANY DISCREPENCY IN THE DRAWING TO BE BROUGHT IN THE DESIGNER'S NOTICE BEFORE IMPLEMENTATION ON SITE.

SITE ADDRESS:

SAVAD
VADODARA

CLIENT NAME:

RONAK PANCHOLI

DATE:

02-06-2025

NORTH:



DRAWING DETAIL

REVISION NO.

R1 R2 R3

REVISED DATE:

12/02/26

SCALE:

N.T.S

DRAWN BY:

ARCHANA

CHECKED BY:

MITTAL

- www.mayaspace.studio
- mayaspace.studio@gmail.com
- +918980144077
- @mayaspace.studio



KITCHEN LIGHTING LAYOUT

- * DO NOT SCALE THE DRAWING.
- * ALL DIMENSIONS ARE IN FEET \ INCHES.
- * ANY DISCREPANCY IN THE DRAWING TO BE BROUGHT IN THE DESIGNER'S NOTICE BEFORE IMPLEMENTATION ON SITE.


SAVAD
VADODARA

RONAK PANCHOLI


NORTH: 

REVISION NO.	R1	R2	R3
REVISED DATE:	12/02/26		
SCALE:	N.T.S		
DRAWN BY:	ARCHANA		
CHECKED BY:	MITTAL		

	www.mayaspace.studio
	mayaspace.studio@gmail.com
	+918980144077
	@mayaspace.studio

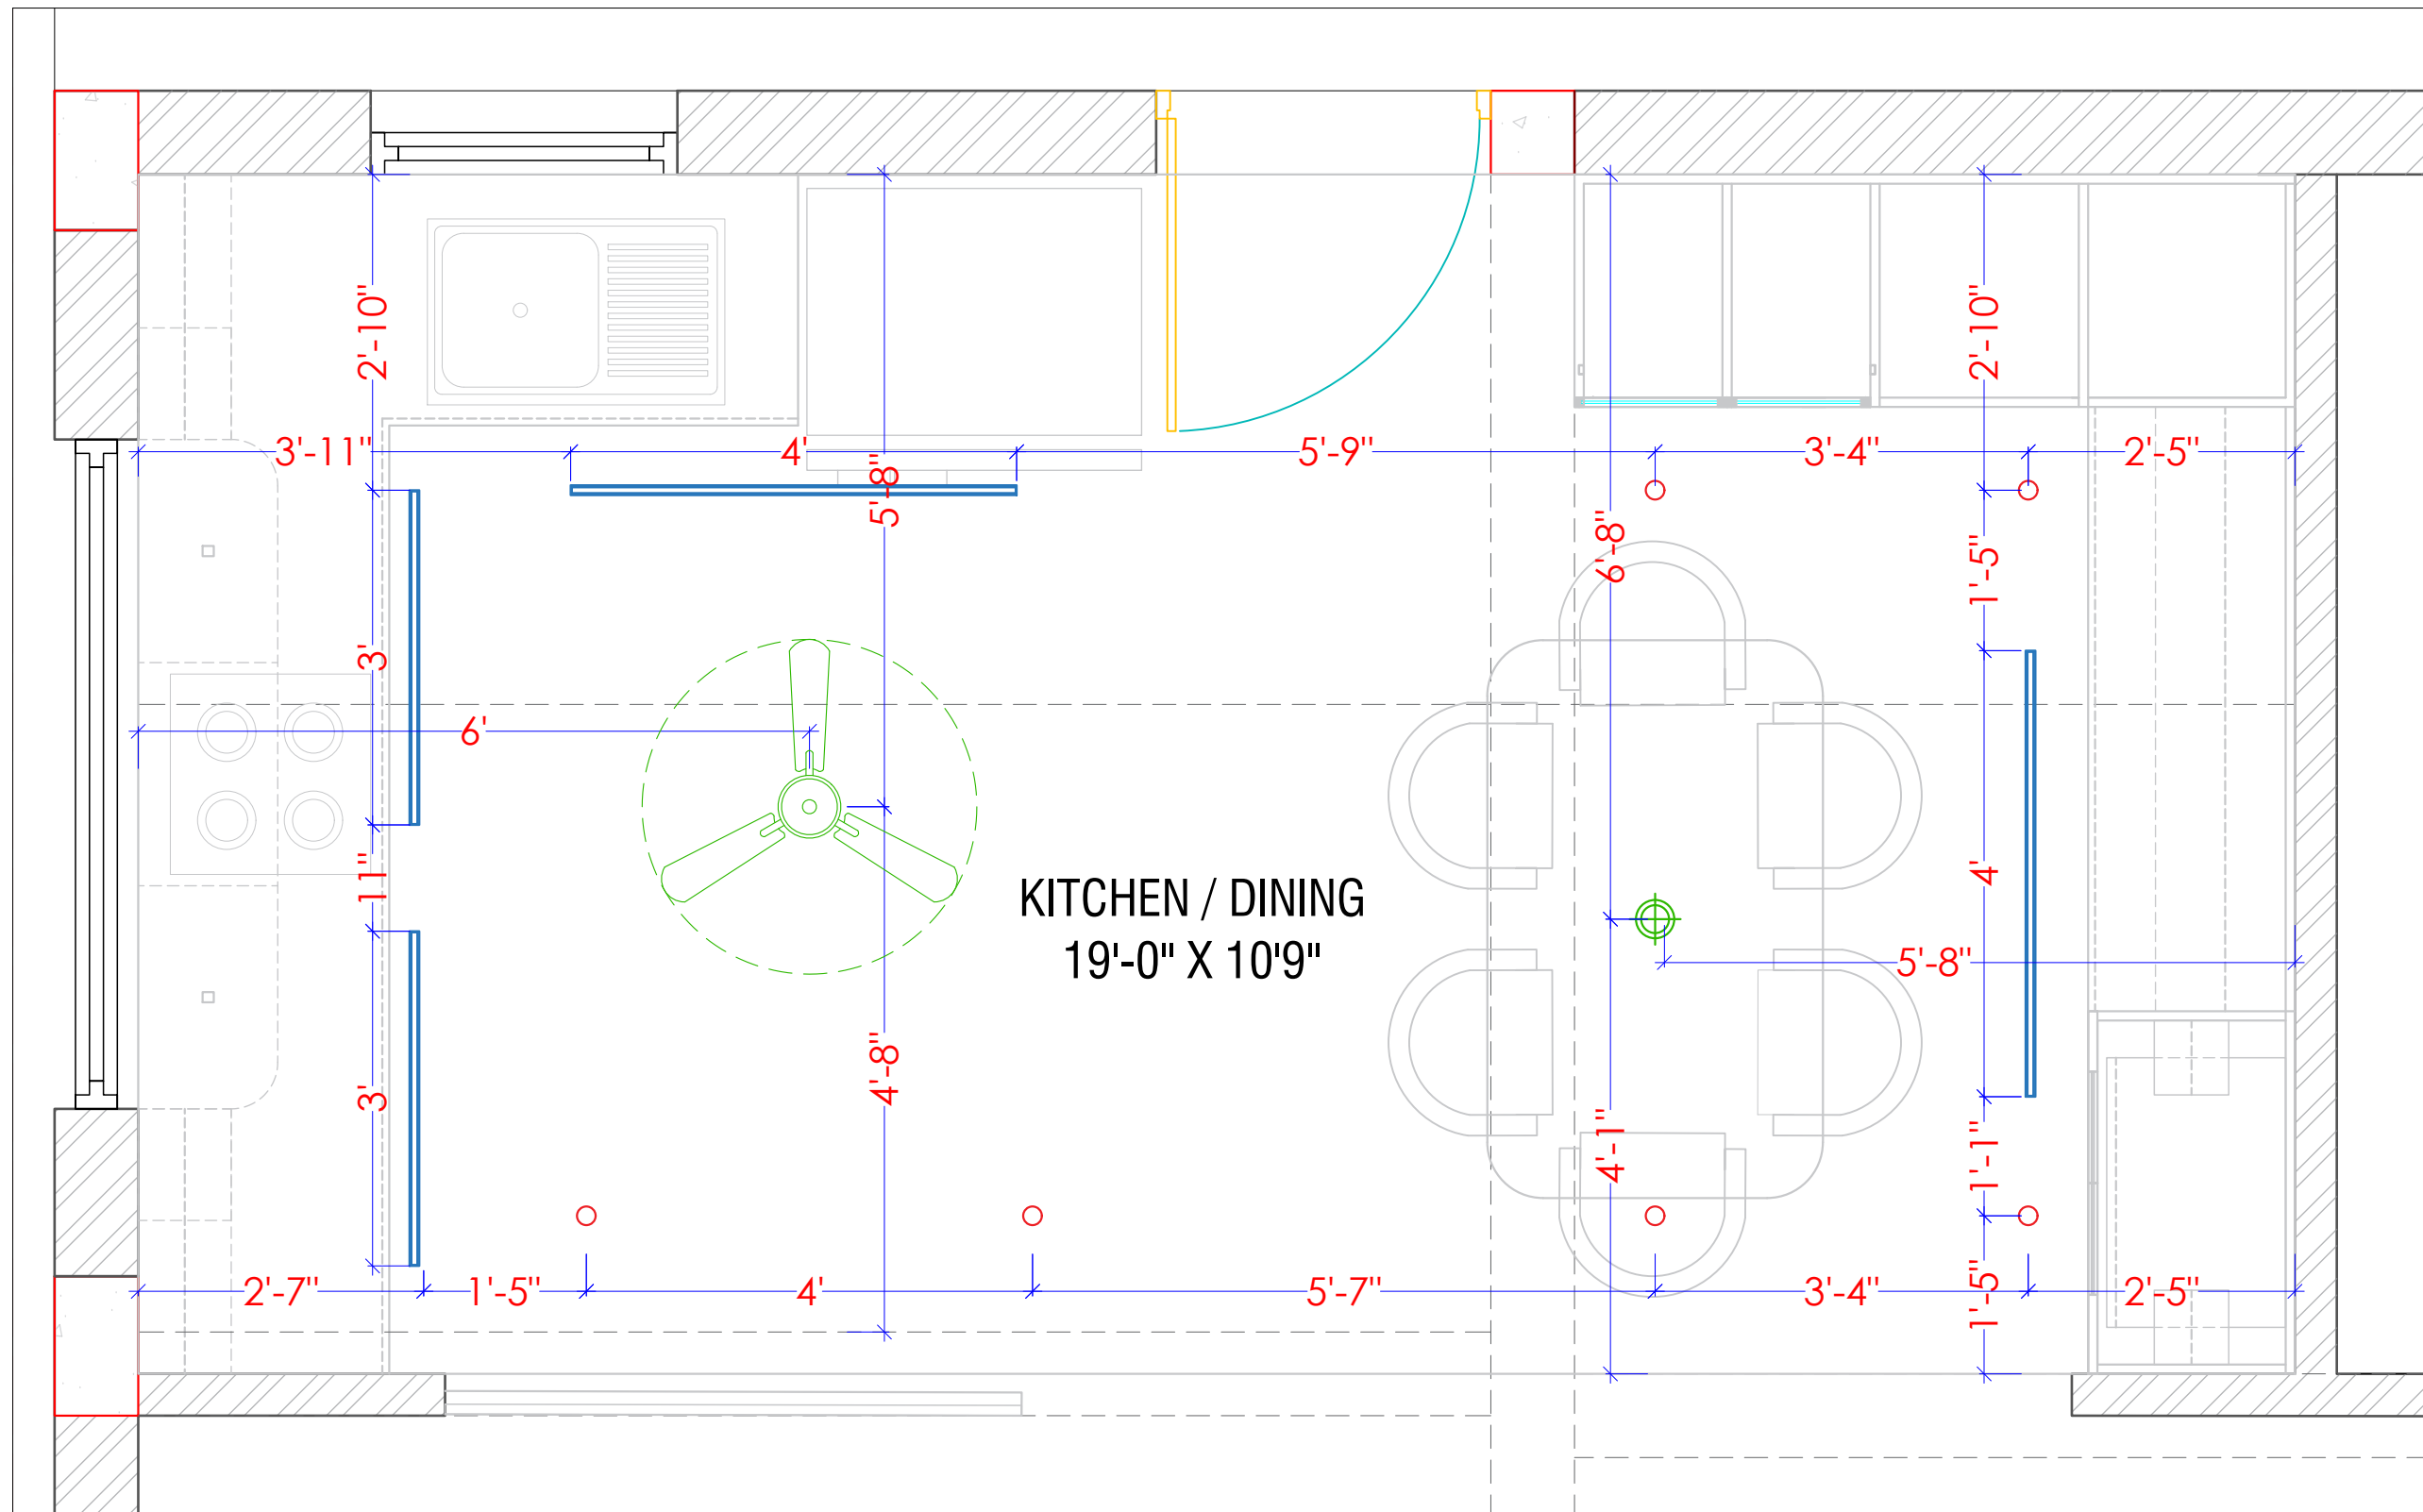

LIGHTING LAYOUT

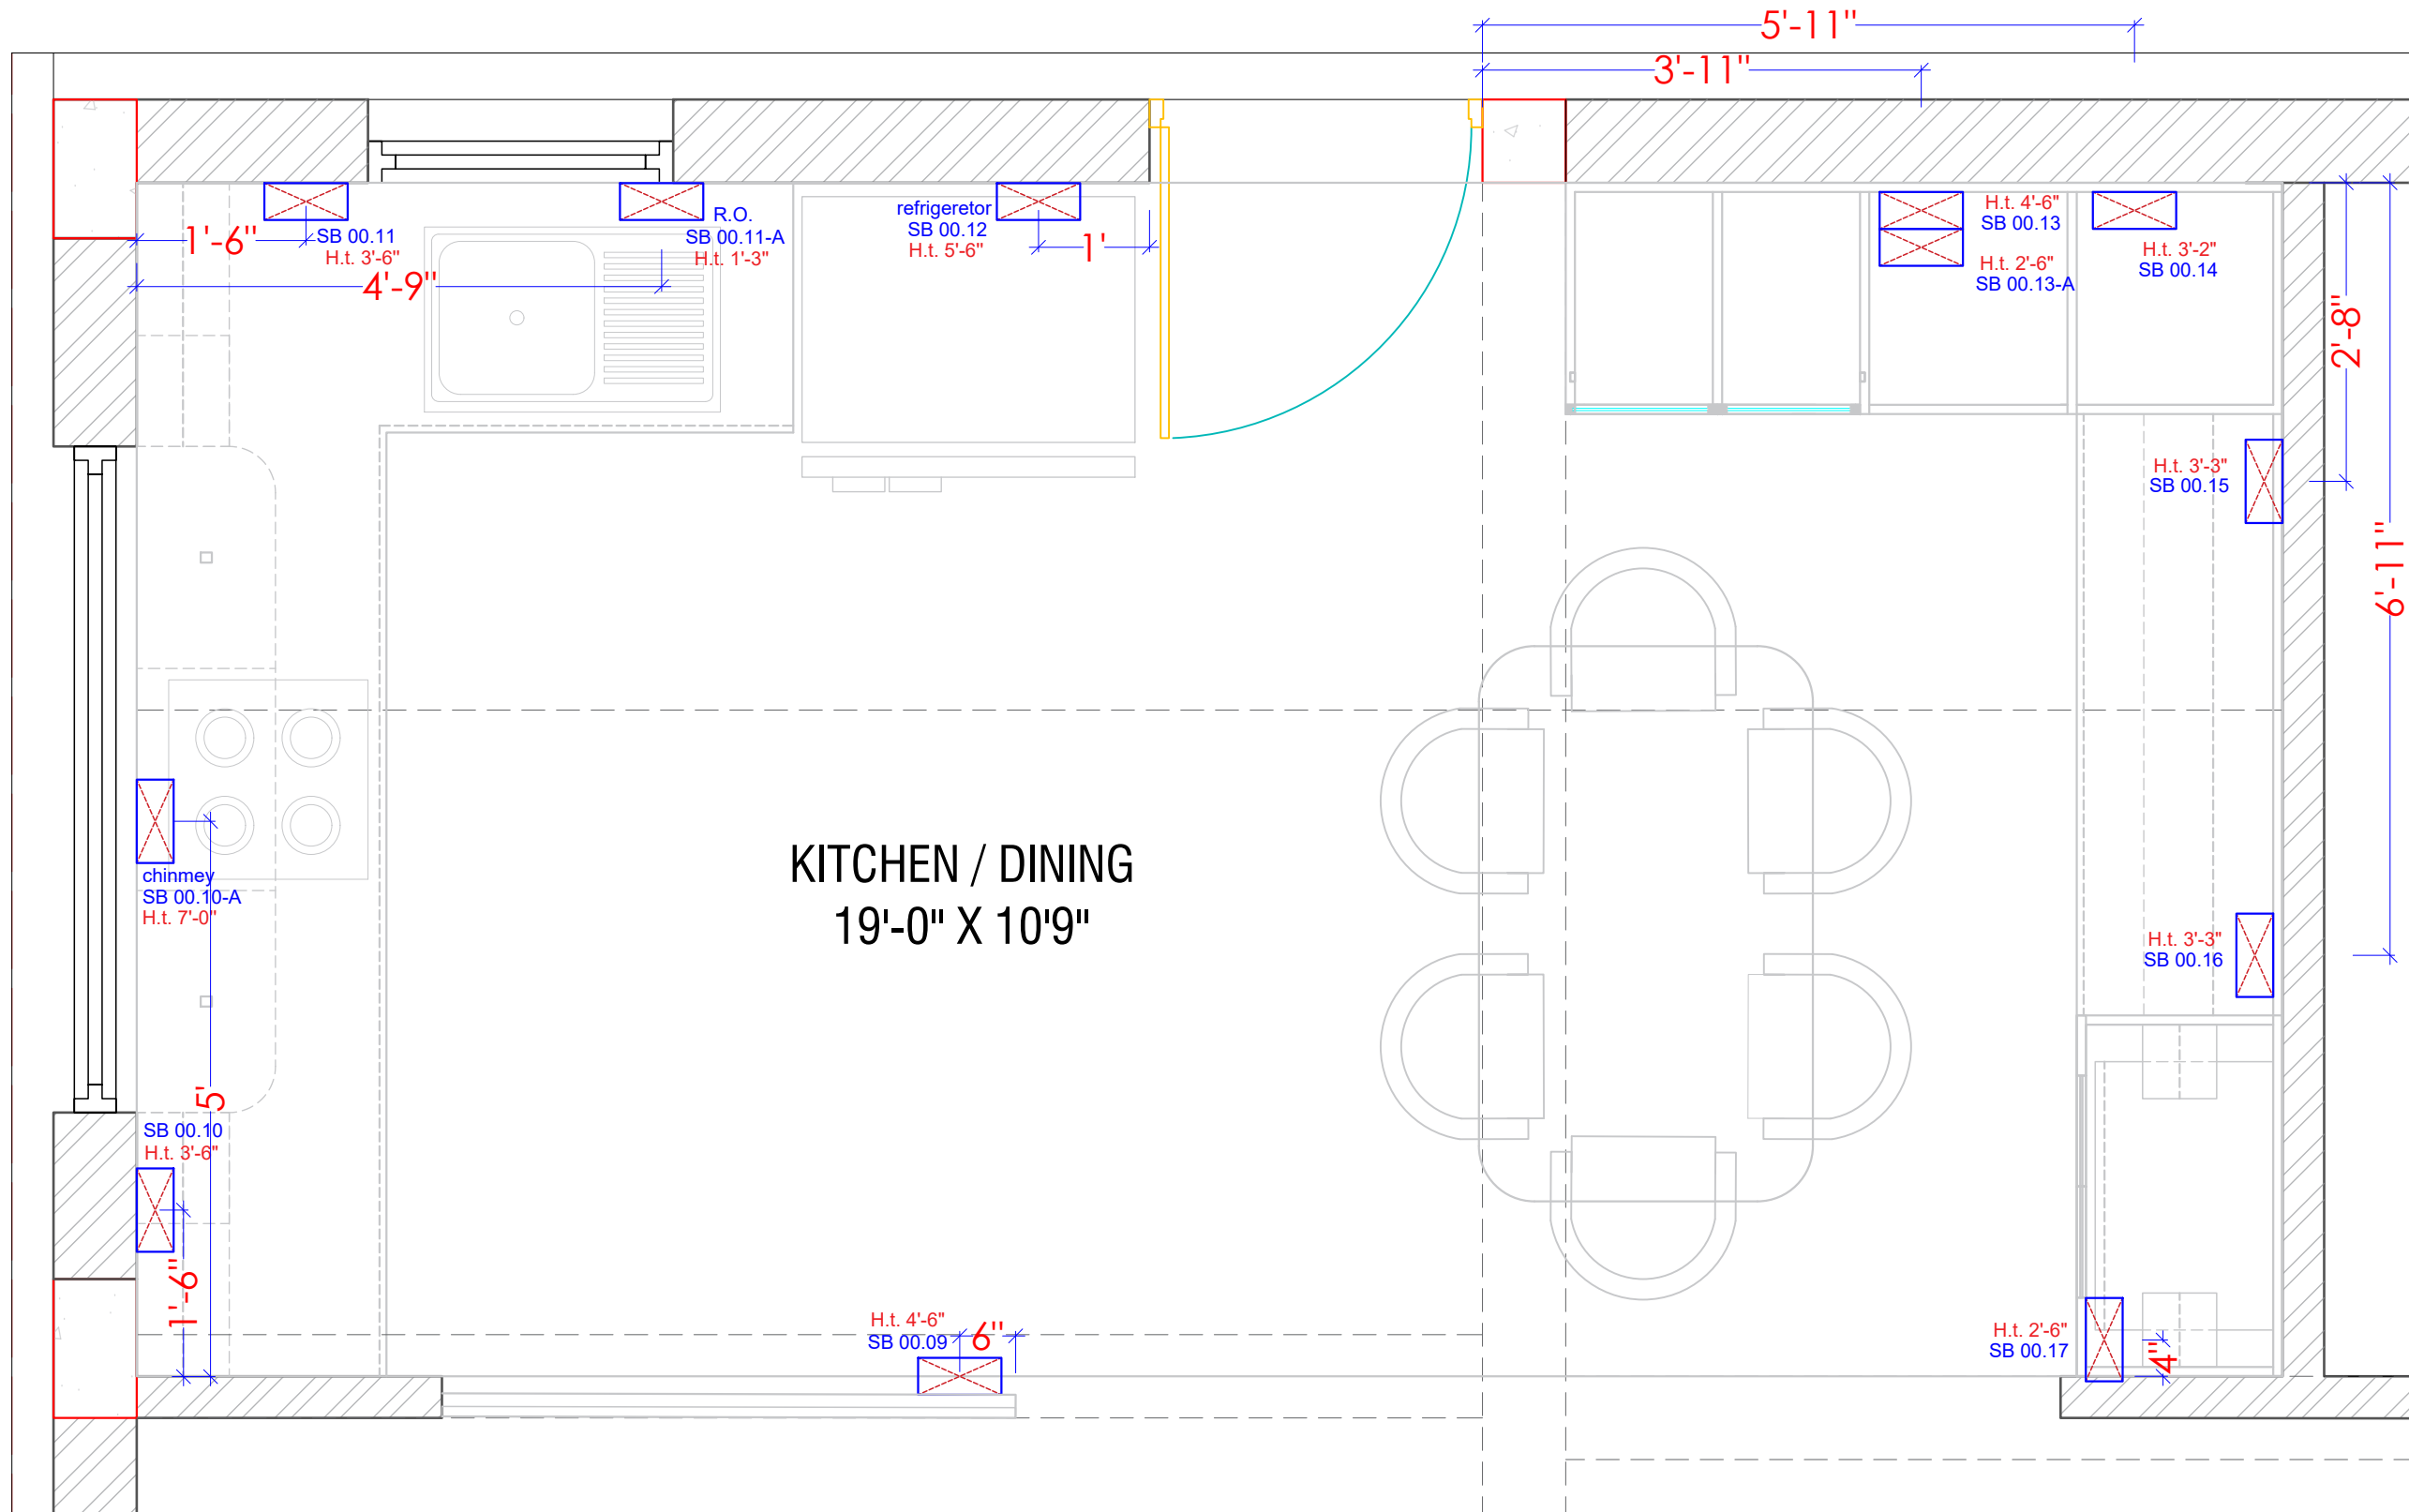

SWITCH BOARD LAYOUT

DRAWING TITLE :

KITCHEN SB LAYOUT

NOTES:

* DO NOT SCALE THE DRAWING.

* ALL DIMENSIONS ARE IN FEET \ INCHES.

* ANY DISCREPANCY IN THE DRAWING
TO BE BROUGHT IN THE DESIGNER'S
NOTICE BEFORE IMPLEMENTATION
ON SITE.

SITE ADDRESS:

SAVAD
VADODARA

CLIENT NAME:

RONAK PANCHOLI

DATE:

02-06-2025

NORTH:



DRAWING DETAIL

REVISION NO.

R1 R2 R3

REVISED DATE:

12/02/26

SCALE:

N.T.S

DRAWN BY:

ARCHANA

CHECKED BY:

MITTAL


www.mayaspace.studio

mayaspace.studio@gmail.com

+918980144077

@mayaspace.studio



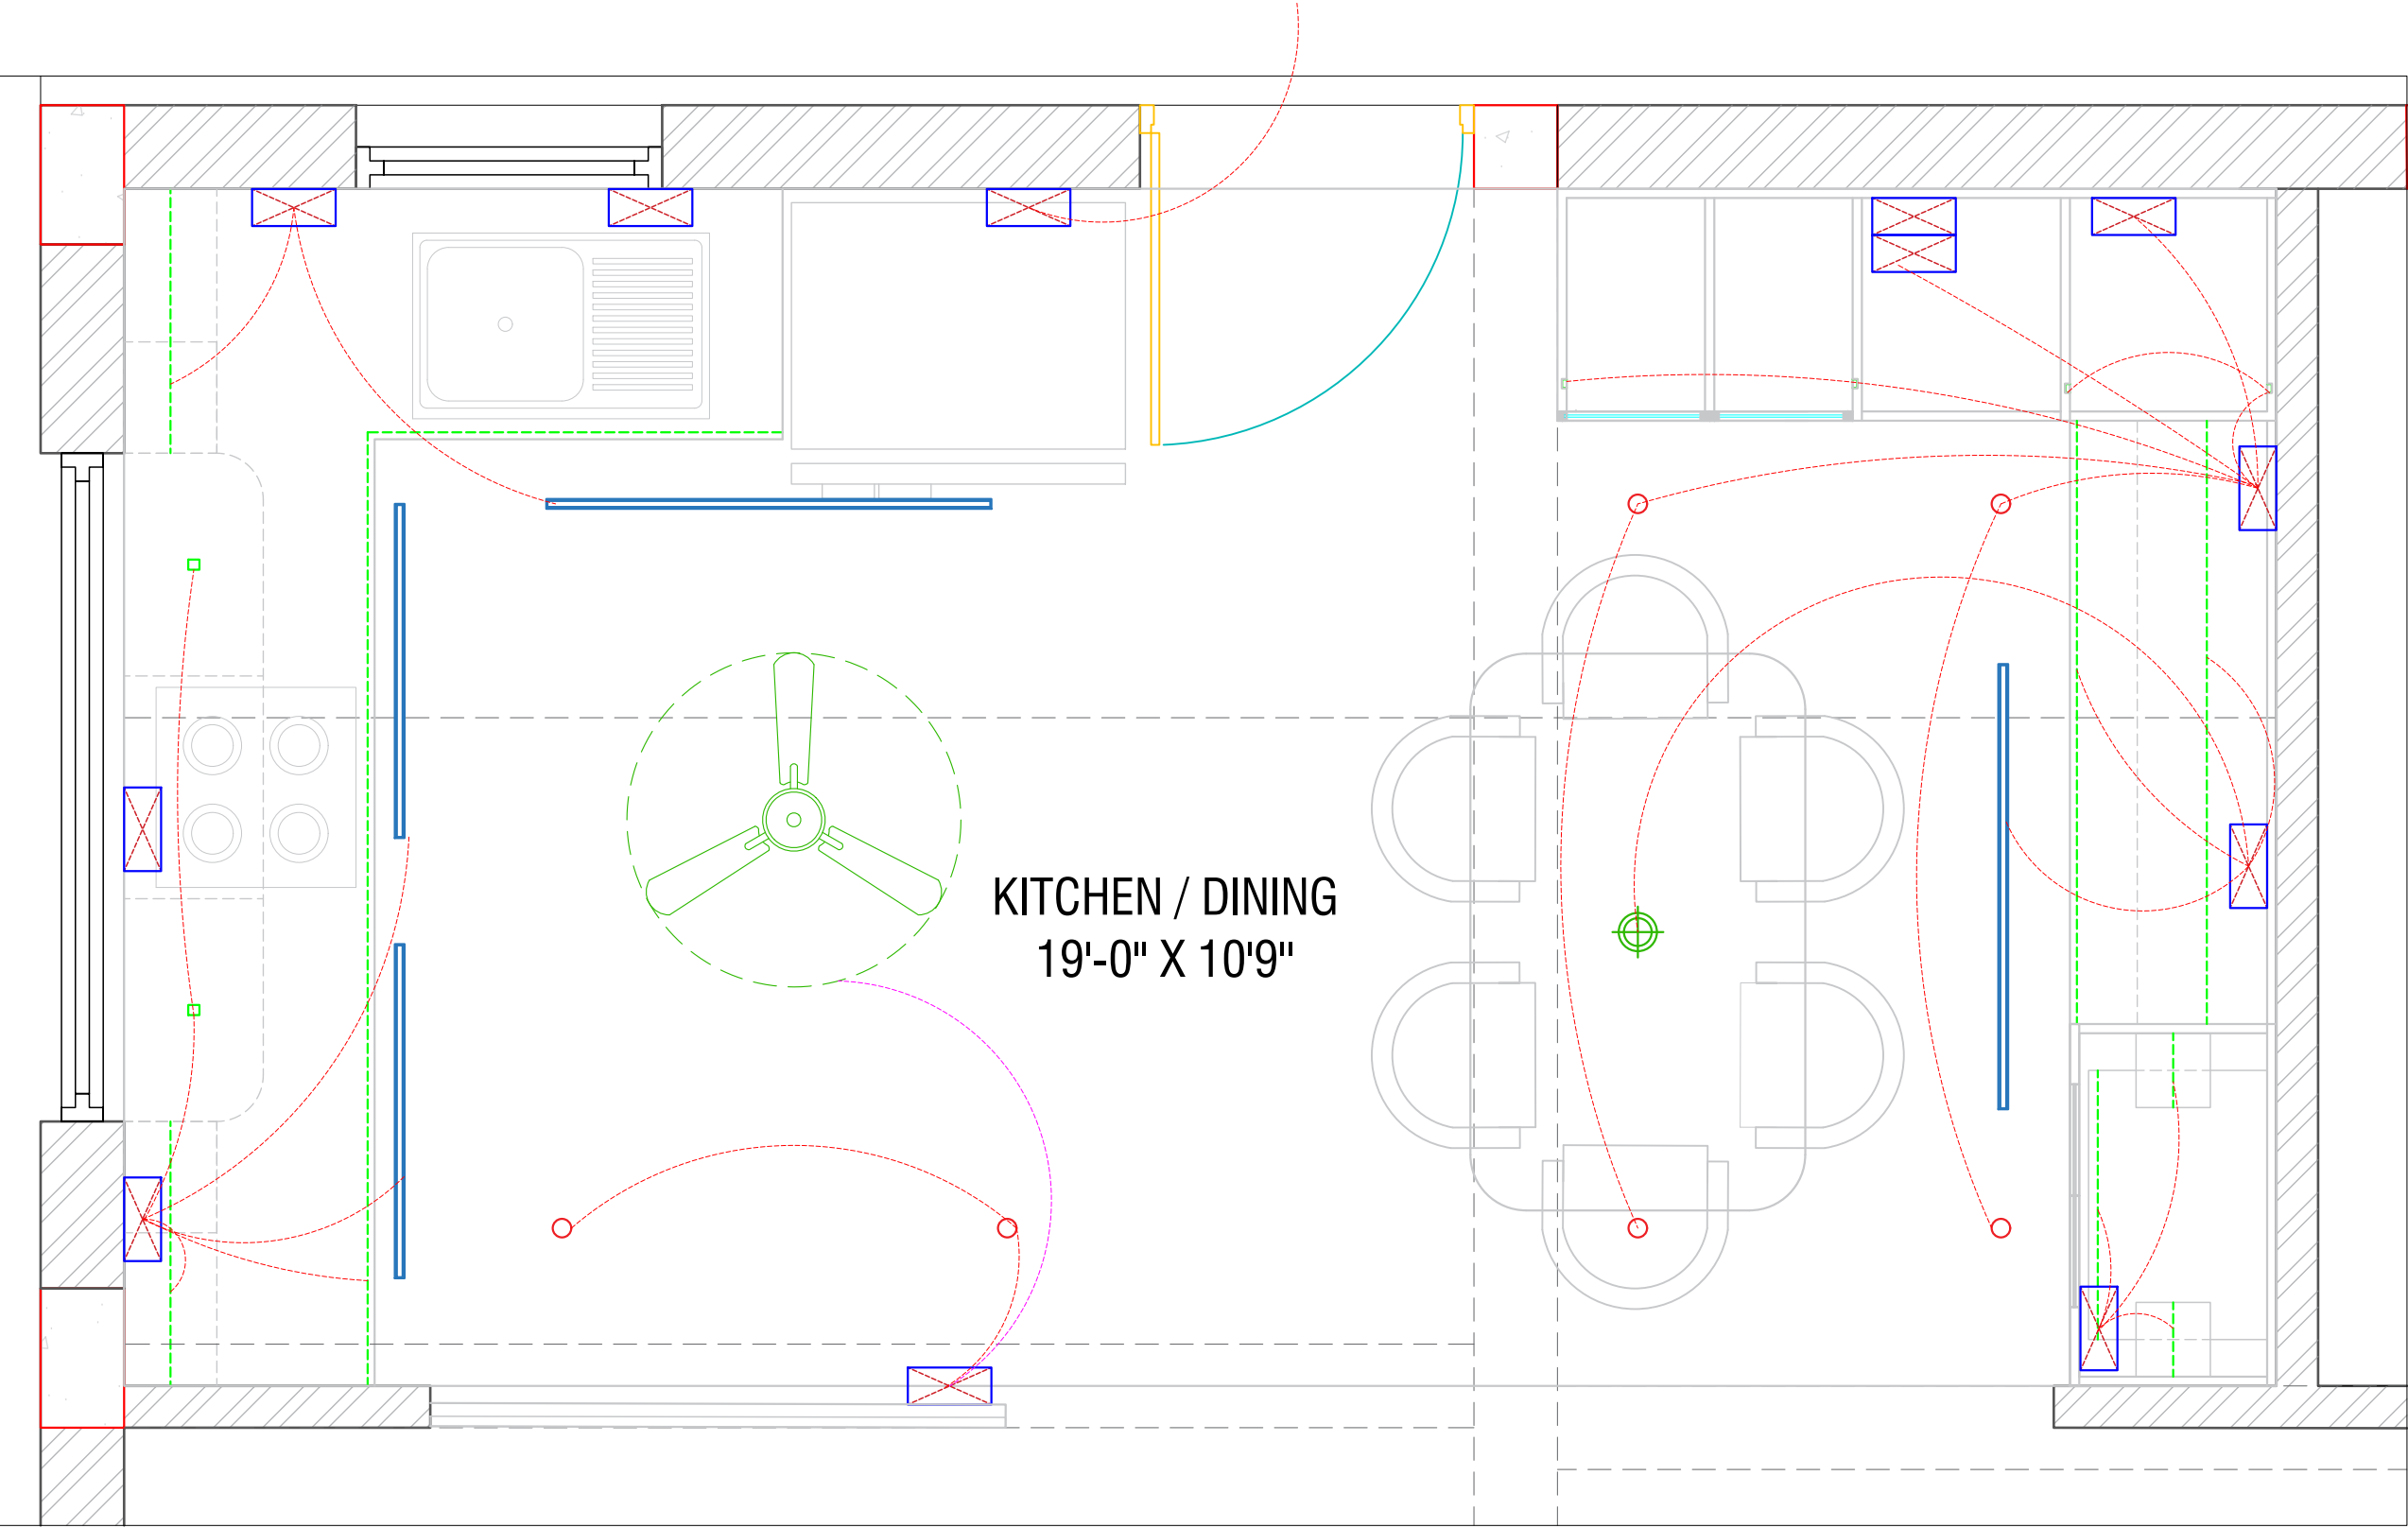

LOOPING LAYOUT

DRAWING TITLE :

KITCHEN
LOOPING LAYOUT

NOTES:

* DO NOT SCALE THE DRAWING.

* ALL DIMENSIONS ARE IN FEET \ INCHES.

* ANY DISCREPANCY IN THE DRAWING TO BE BROUGHT IN THE DESIGNER'S NOTICE BEFORE IMPLEMENTATION ON SITE.

SITE ADDRESS:

SAVAD
VADODARA

CLIENT NAME:

RONAK PANCHOLI

DATE:	02-06-2025
NORTH:	

DRAWING DETAIL

REVISION NO.	R1 R2 R3
REVISED DATE:	12/02/26
SCALE:	N.T.S
DRAWN BY:	ARCHANA
CHECKED BY:	MITTAL

	www.mayaspace.studio
	mayaspace.studio@gmail.com
	+918980144077
	@mayaspace.studio

Maya
SPACE STUDIO

DRAWING TITLE :

KITCHEN ELEVATION- A

NOTES:

- * DO NOT SCALE THE DRAWING.
- * ALL DIMENSIONS ARE IN FEET \ INCHES.
- * ANY DISCREPANCY IN THE DRAWING TO BE BROUGHT IN THE DESIGNER'S NOTICE BEFORE IMPLEMENTATION ON SITE.

SITE ADDRESS:

SAVAD
VADODARA

CLIENT NAME:

RONAK PANCHOLI

DATE:


02-06-2025

NORTH:

DRAWING DETAIL

REVISION NO.	☐ R1	☐ R2	☐ R3
REVISED DATE:	12/02/26		
SCALE:	N.T.S		
DRAWN BY:	ARCHANA		
CHECKED BY:	MITTAL		

	www.mayaspace.studio
	mayaspace.studio@gmail.com
	+918980144077
	@mayaspace.studio

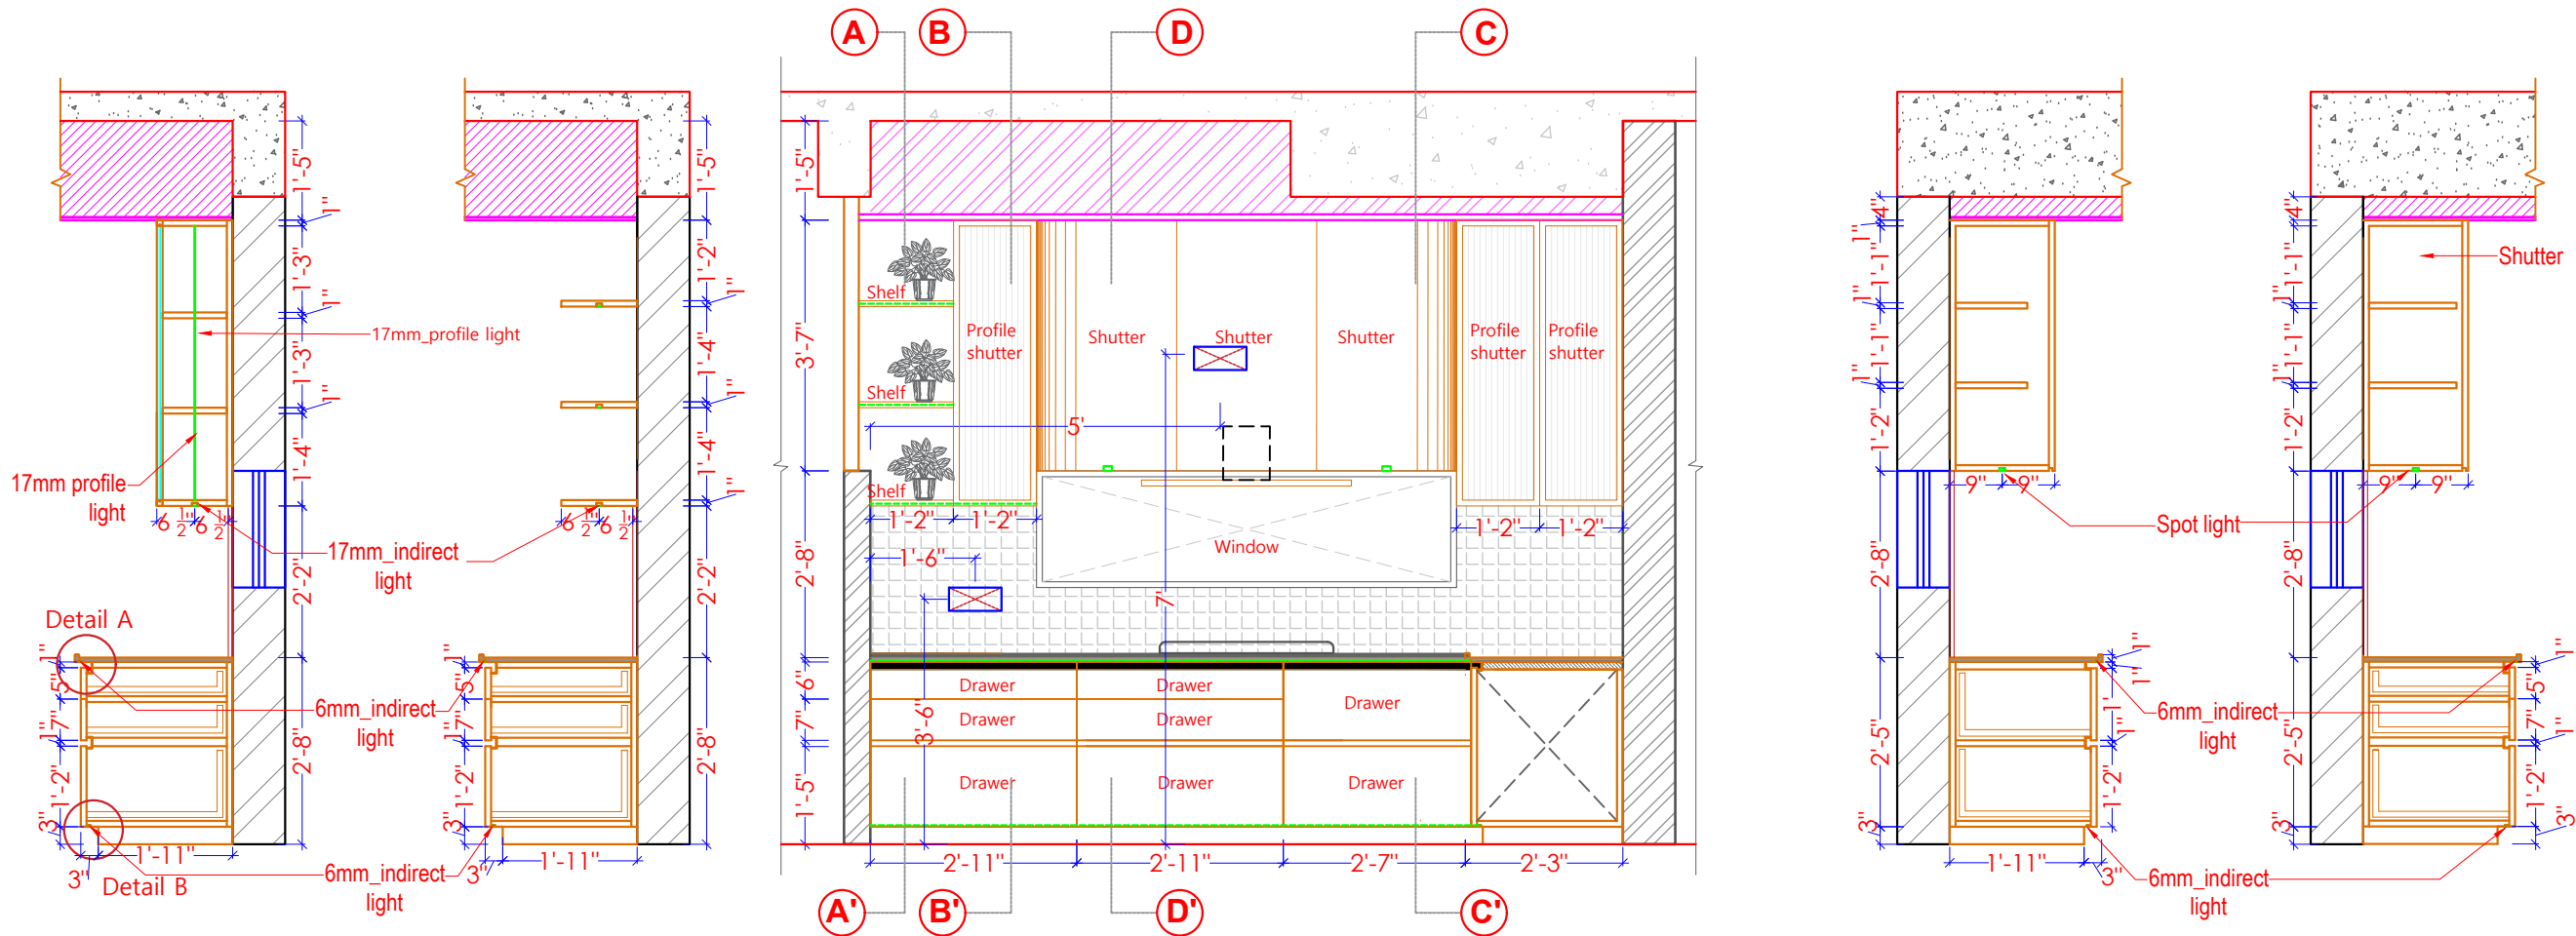


SECTION BB'


SECTION AA'

SECTION CC'

SECTION DD'

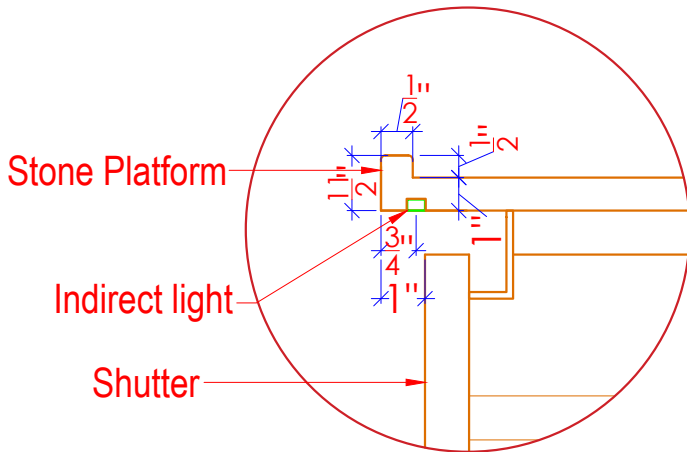

Detail A

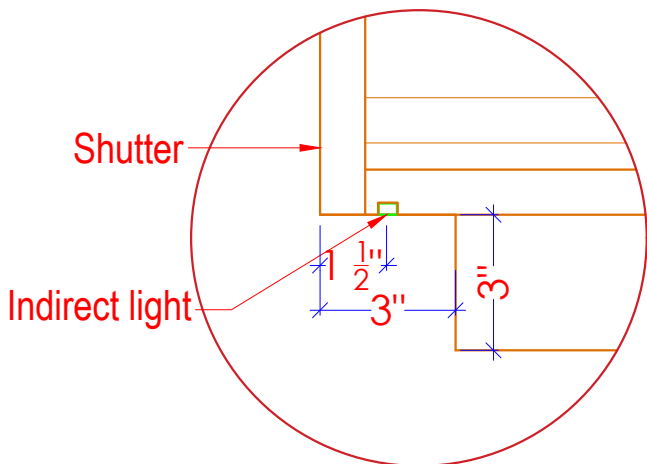

Detail B

ELEVATION - A

DRAWING TITLE :

KITCHEN
ELEVATION- B

NOTES:

- * DO NOT SCALE THE DRAWING.
- * ALL DIMENSIONS ARE IN FEET \ INCHES.
- * ANY DISCREPENCY IN THE DRAWING TO BE BROUGHT IN THE DESIGNER'S NOTICE BEFORE IMPLEMENTATION ON SITE.

SITE ADDRESS:

SAVAD
VADODARA

CLIENT NAME:

RONAK PANCHOLI


DATE: 02-06-2025

NORTH:

DRAWING DETAIL

REVISION NO.	R1	R2	R3
REVISED DATE:	12/02/26		
SCALE:	N.T.S		
DRAWN BY:	ARCHANA		
CHECKED BY:	MITTAL		

	www.mayaspace.studio
	mayaspace.studio@gmail.com
	+918980144077
	@mayaspace.studio

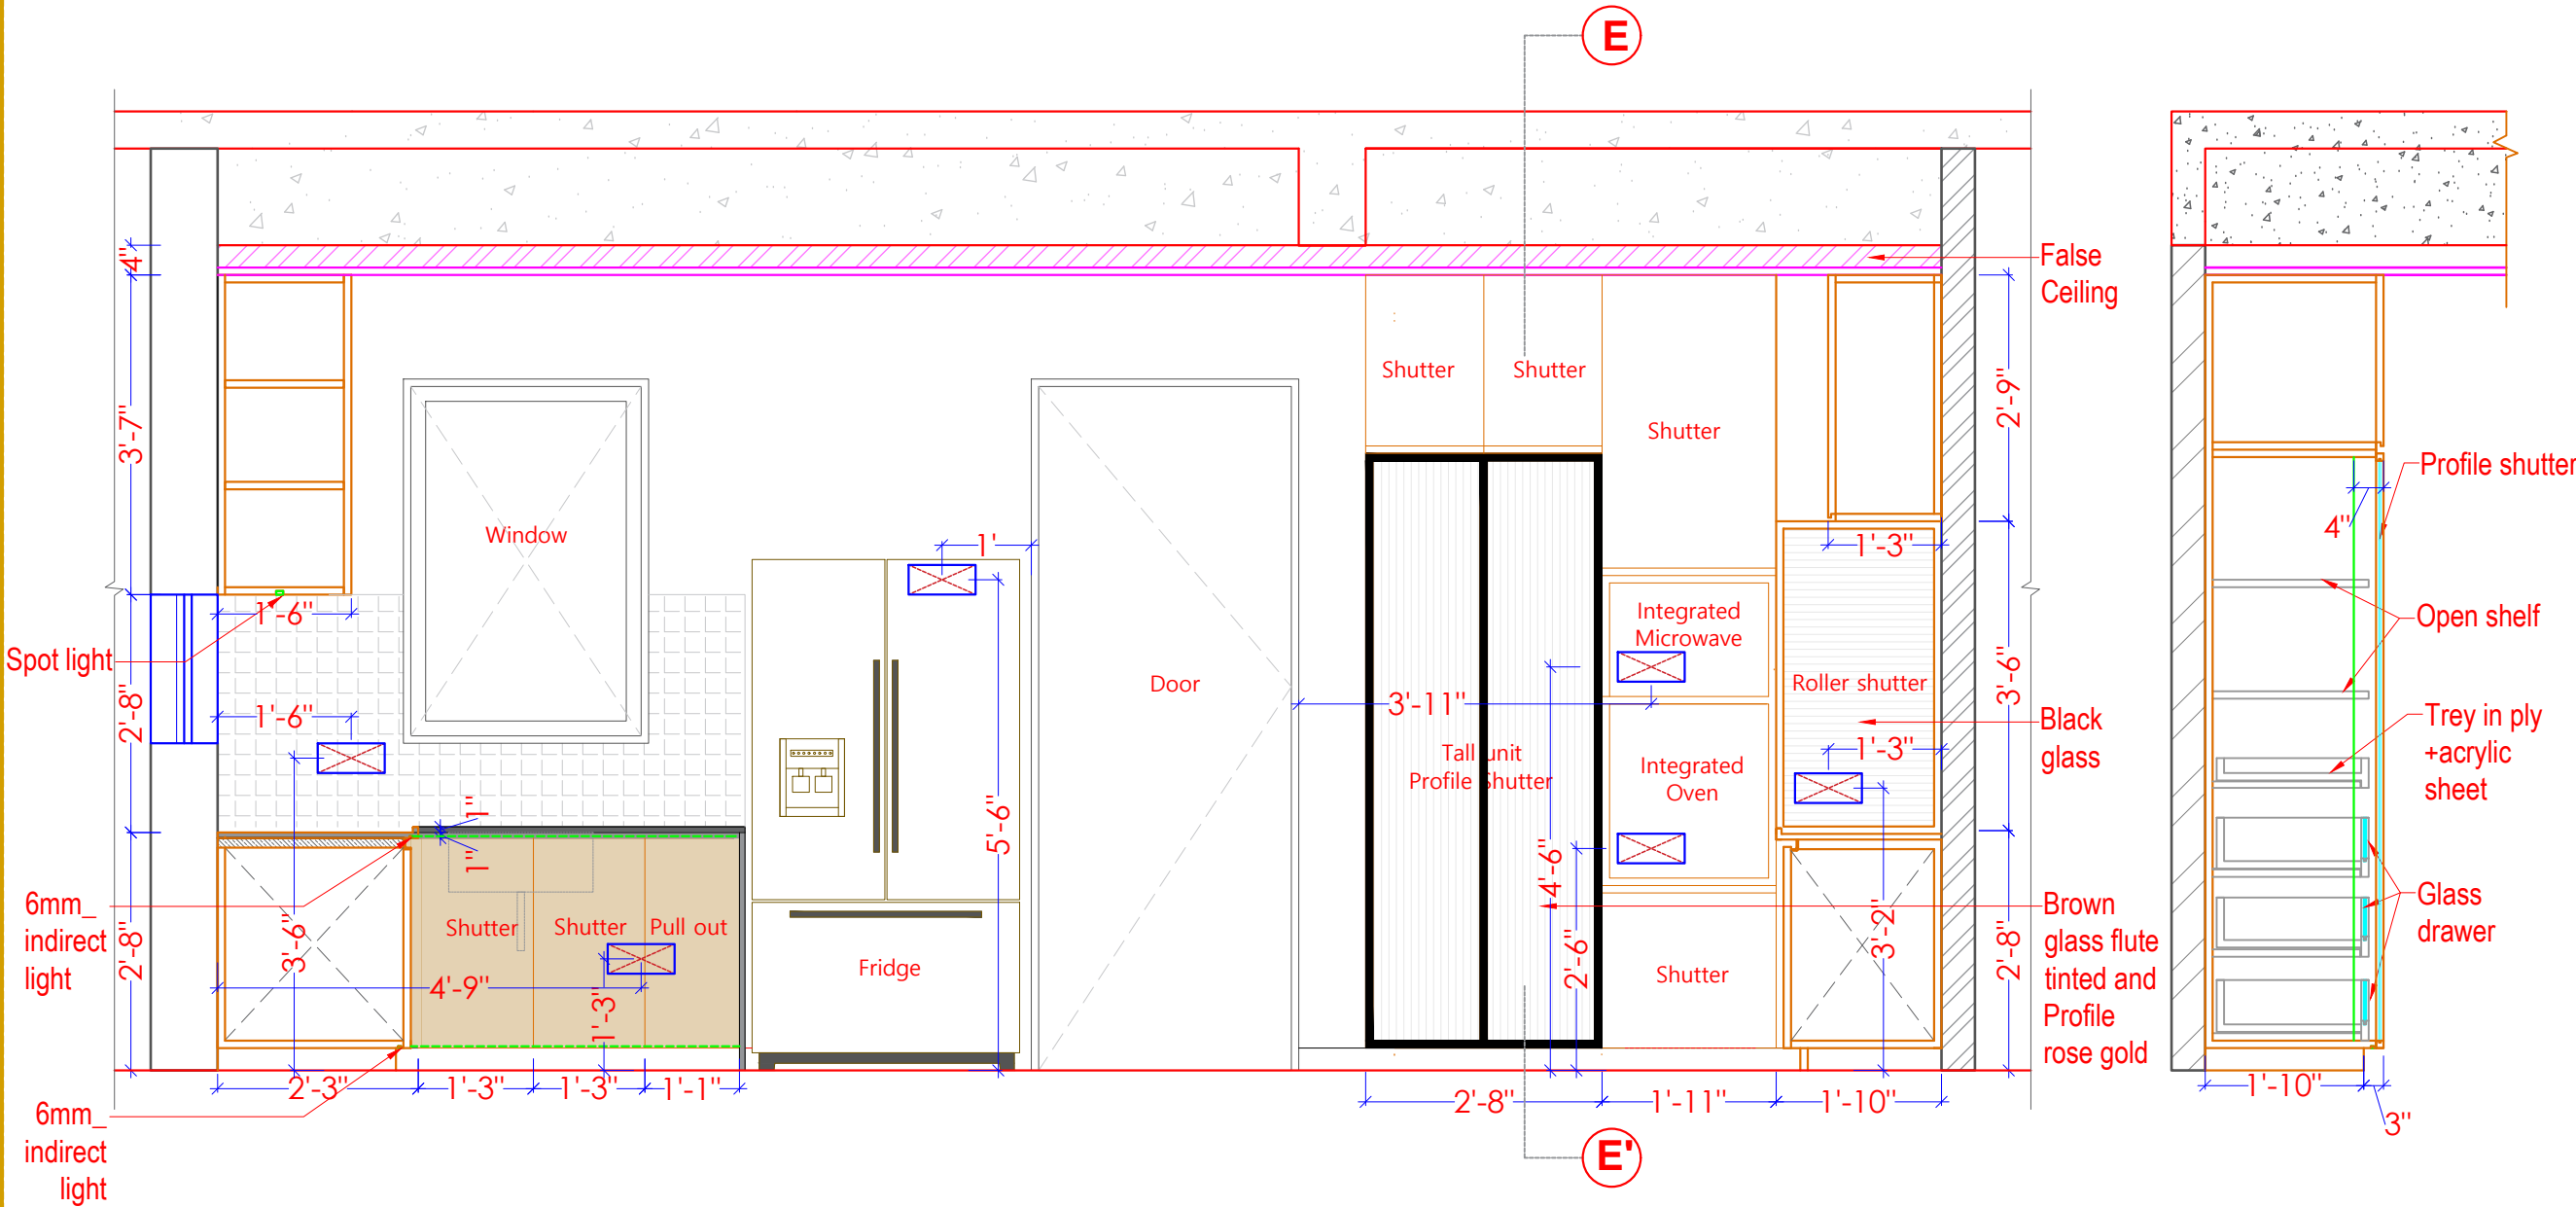

ELEVATION - B

SECTION EE'

DRAWING TITLE :

KITCHEN
ELEVATION- C

NOTES:

- * DO NOT SCALE THE DRAWING.
- * ALL DIMENSIONS ARE IN FEET \ INCHES.
- * ANY DISCREPENCY IN THE DRAWING TO BE BROUGHT IN THE DESIGNER'S NOTICE BEFORE IMPLEMENTATION ON SITE.

SITE ADDRESS:

SAVAD
VADODARA

CLIENT NAME:

RONAK PANCHOLI




DATE: 02-06-2025

NORTH:


DRAWING DETAIL

REVISION NO.	R1	R2	R3
REVISED DATE:	12/02/26		
SCALE:	N.T.S		
DRAWN BY:	ARCHANA		
CHECKED BY:	MITTAL		

	www.mayaspace.studio
	mayaspace.studio@gmail.com
	+918980144077
	@mayaspace.studio

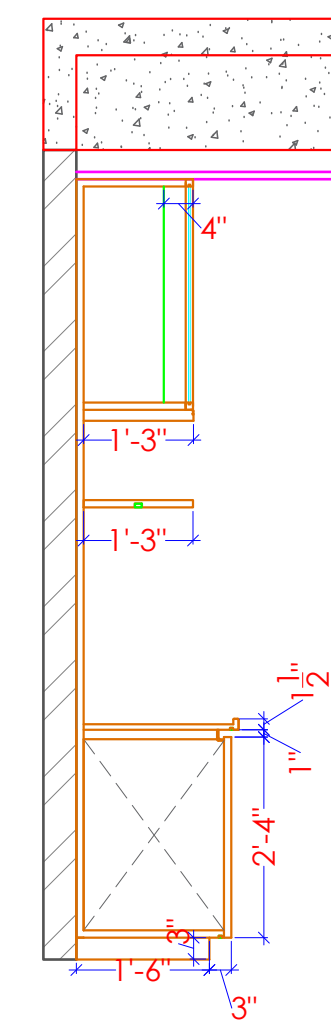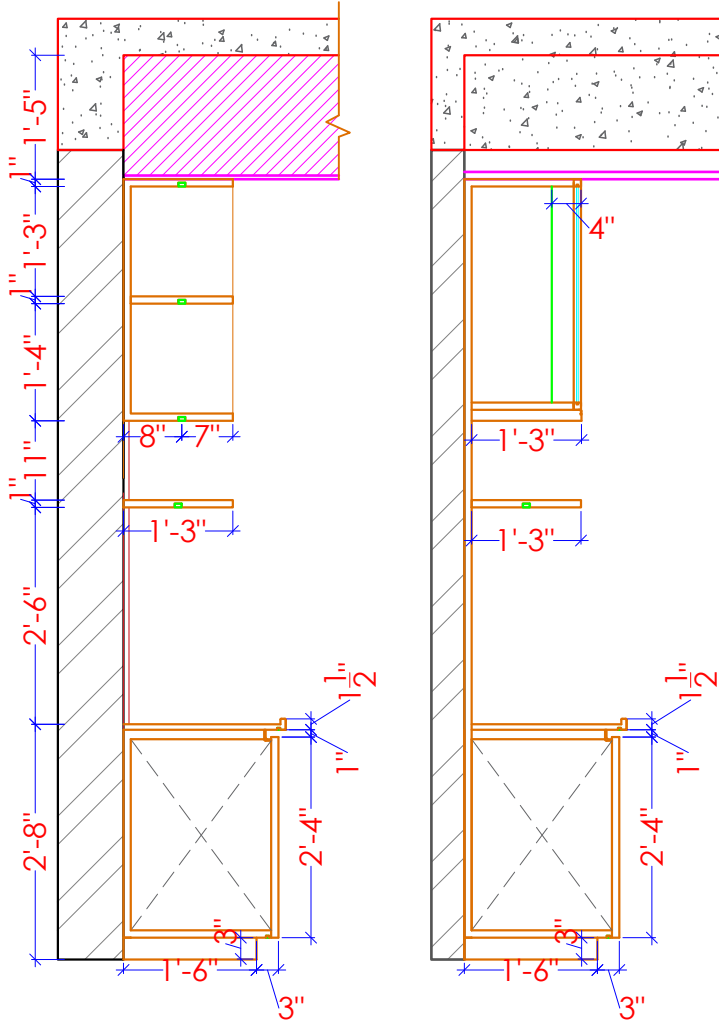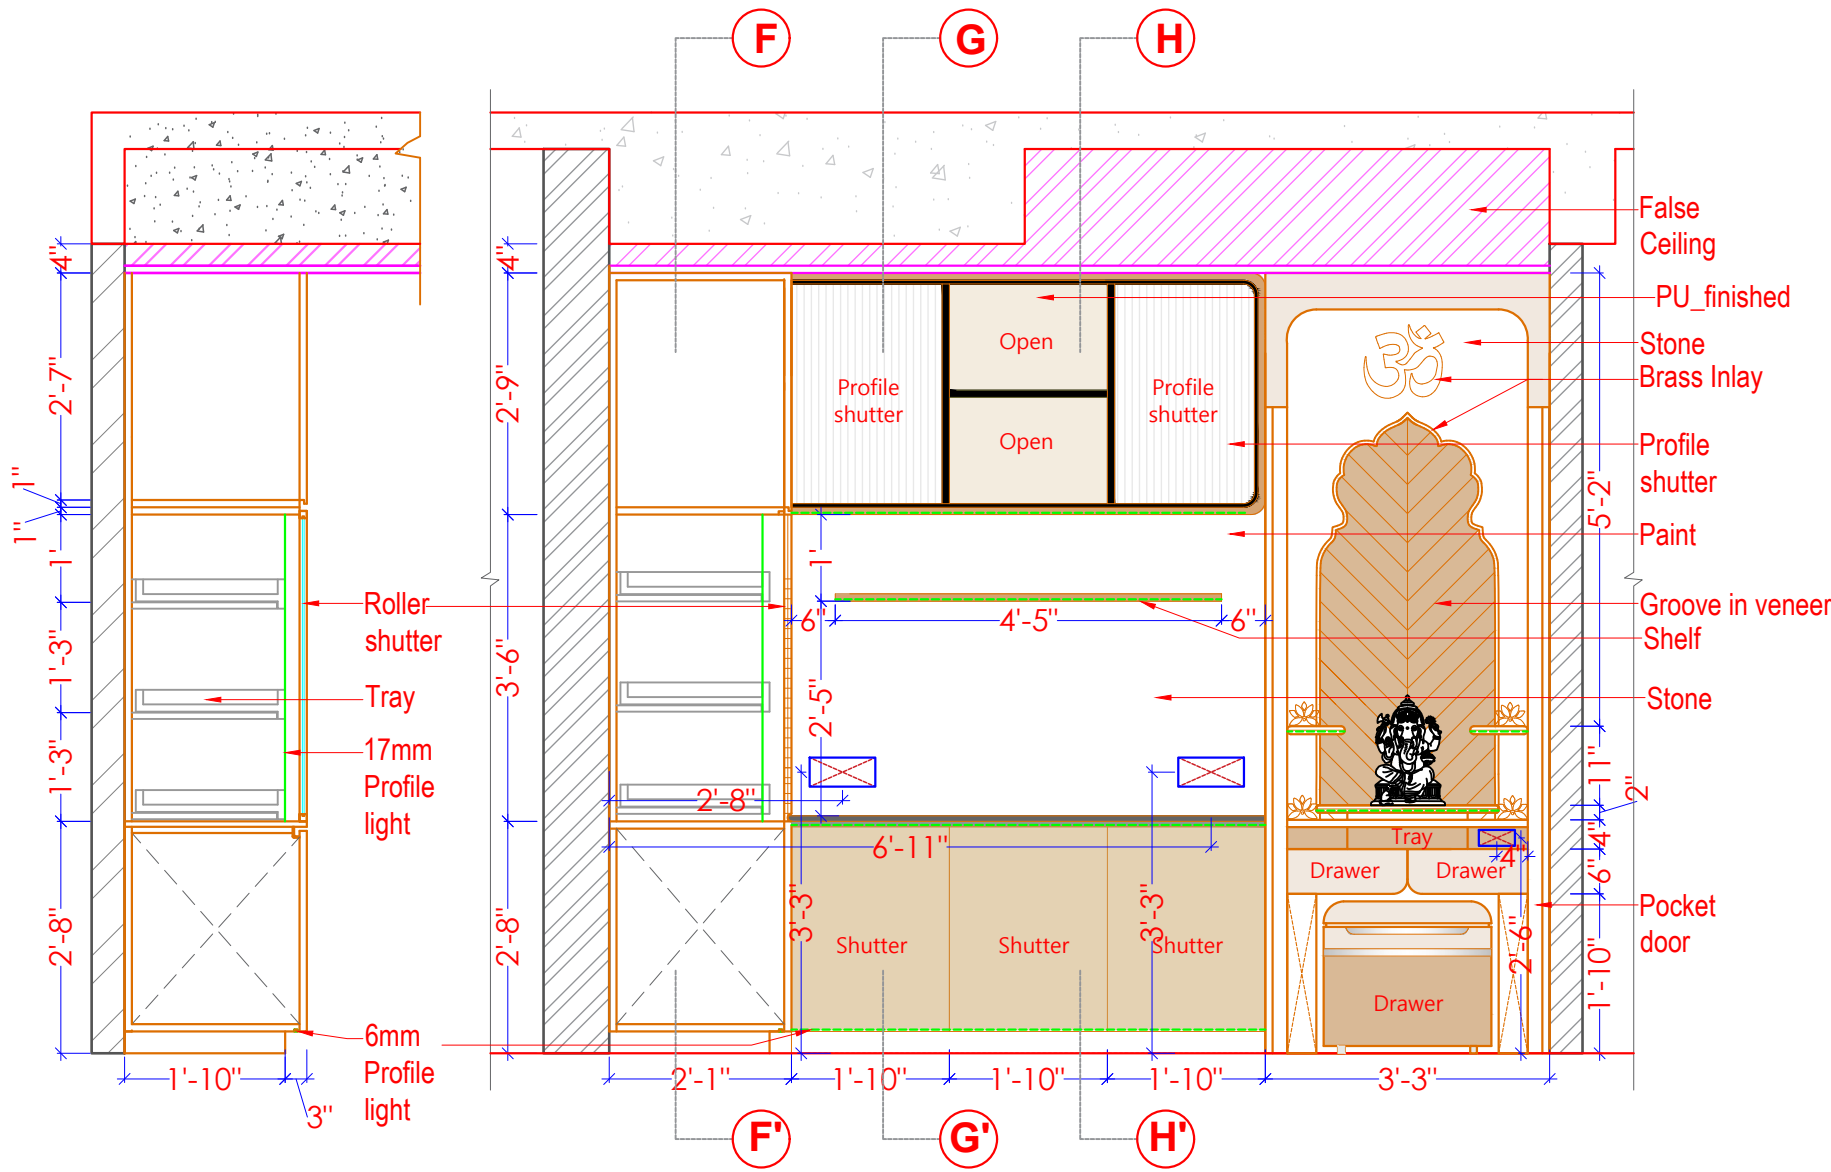

ELEVATION - C

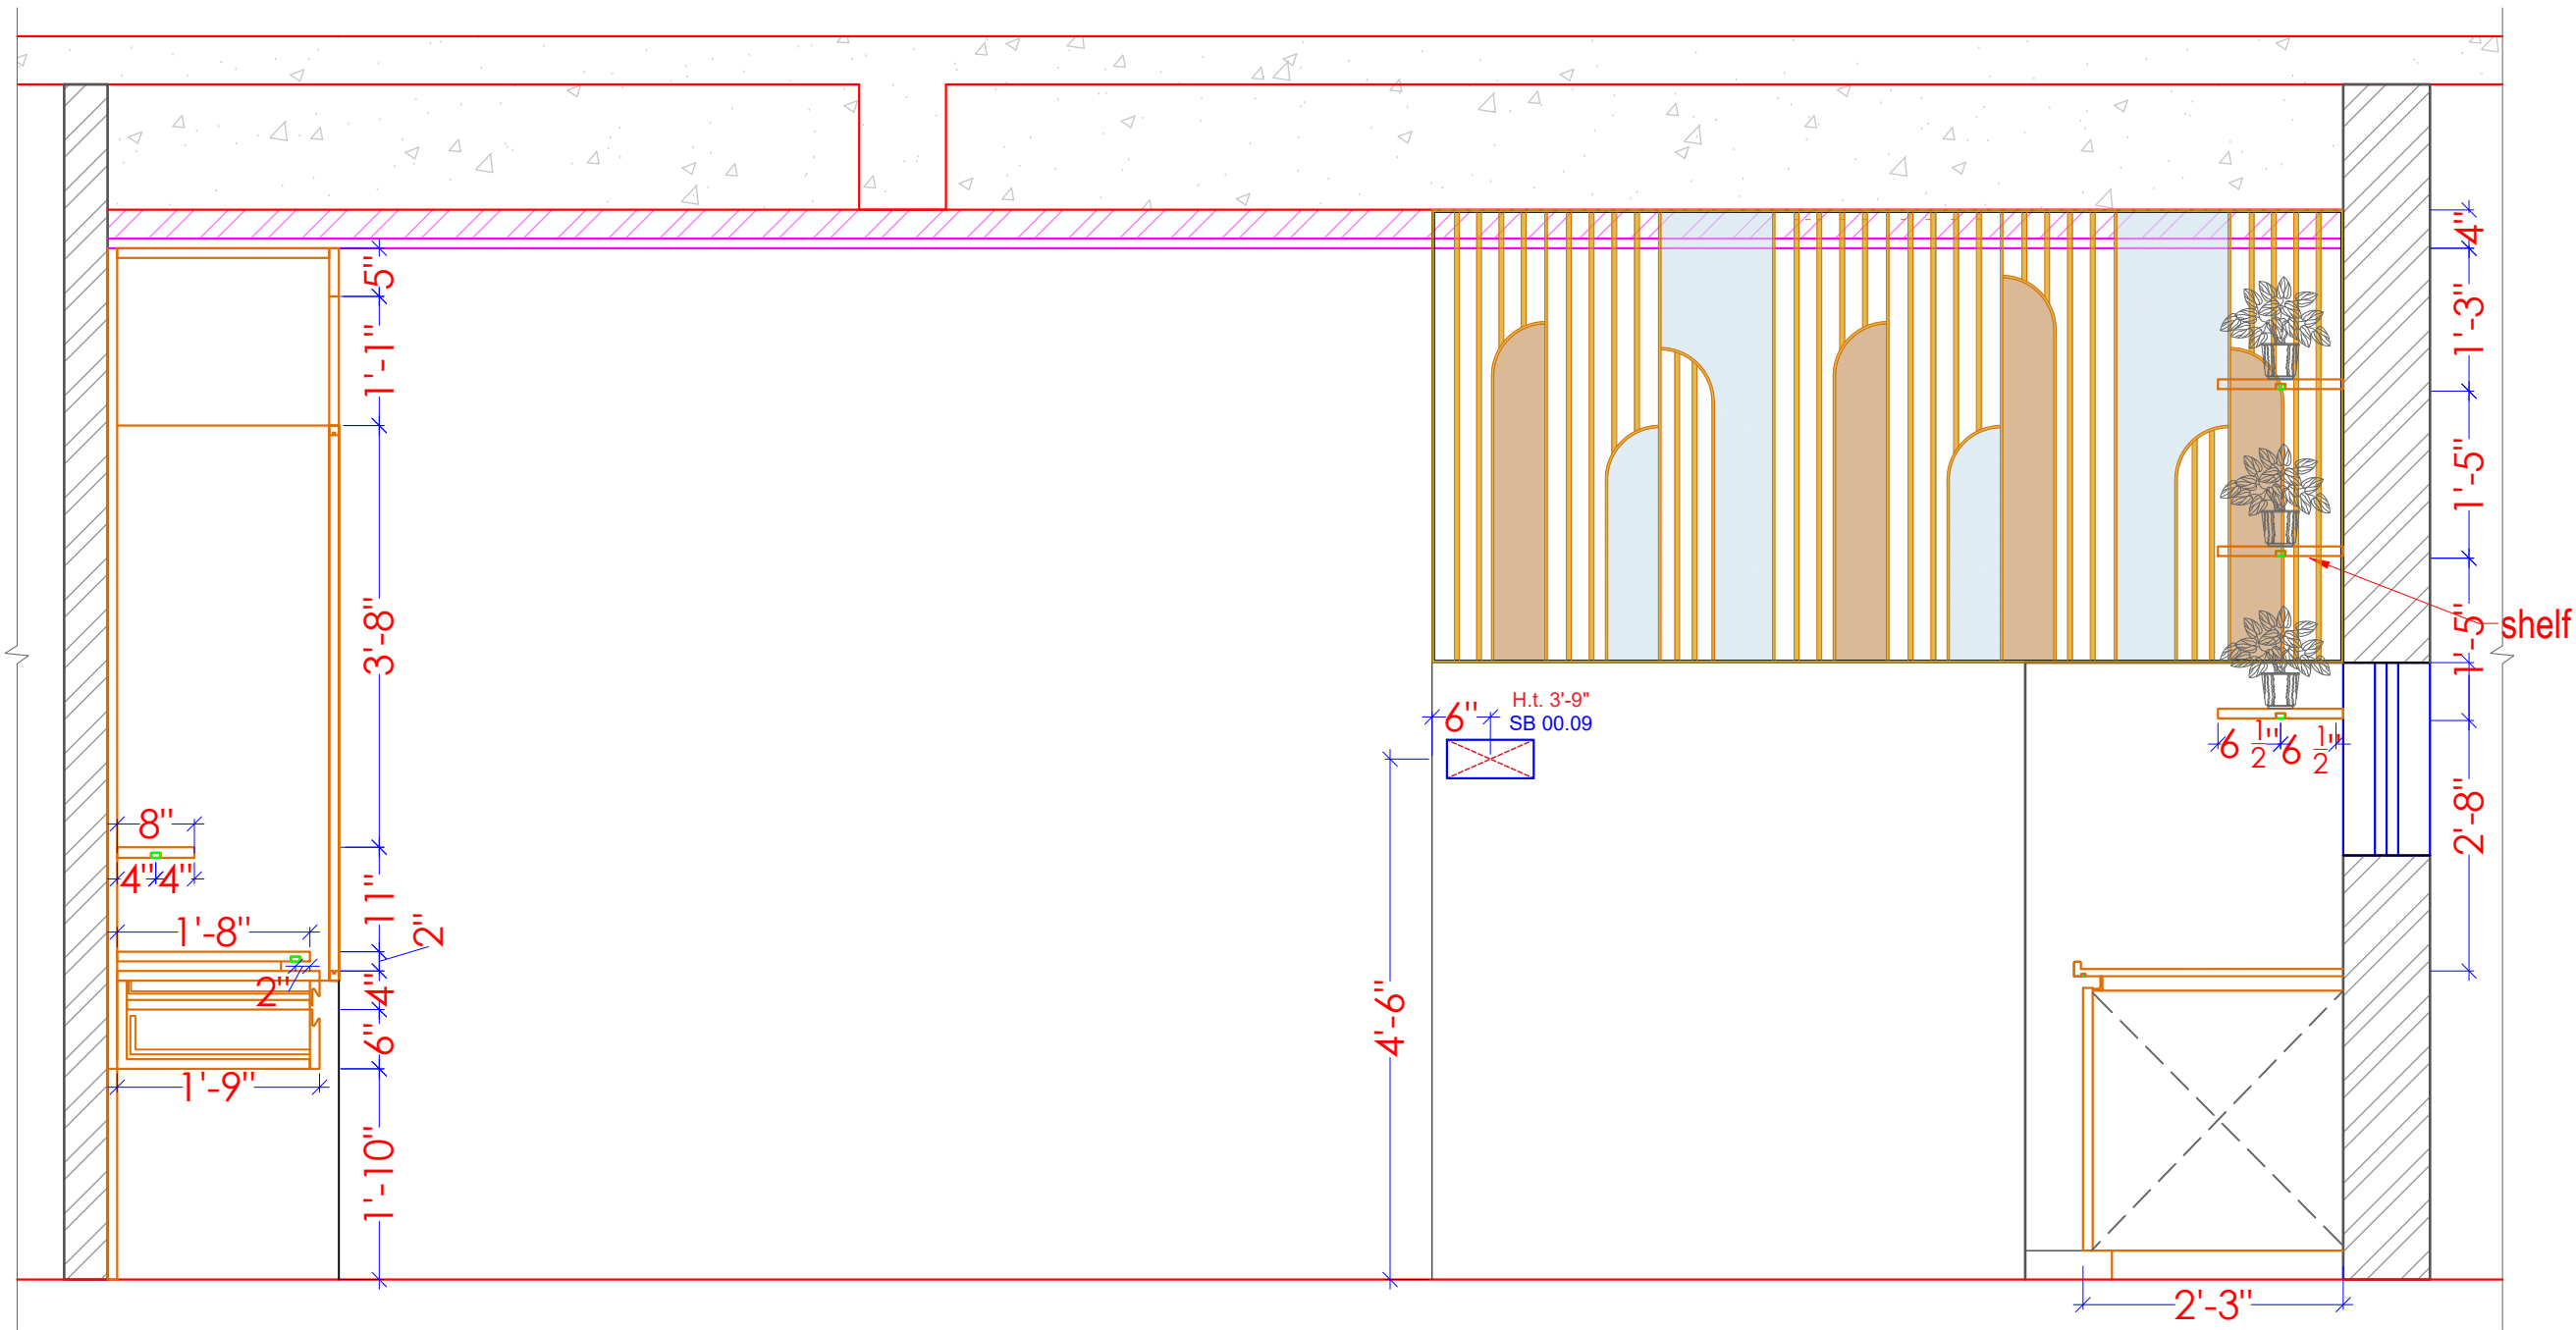

ELEVATION - D

DRAWING TITLE :

KITCHEN
ELEVATION- D

NOTES:

- * DO NOT SCALE THE DRAWING.
- * ALL DIMENSIONS ARE IN FEET \ INCHES.
- * ANY DISCREPANCY IN THE DRAWING TO BE BROUGHT IN THE DESIGNER'S NOTICE BEFORE IMPLEMENTATION ON SITE.

SITE ADDRESS:

SAVAD
VADODARA

CLIENT NAME:

RONAK PANCHOLI

DATE: 02-06-2025


NORTH:

DRAWING DETAIL


REVISION NO.	R1	R2	R3
REVISED DATE:	12/02/26		
SCALE:	N.T.S		
DRAWN BY:	ARCHANA		
CHECKED BY:	MITTAL		

	www.mayaspace.studio
	mayaspace.studio@gmail.com
	+918980144077
	@mayaspace.studio



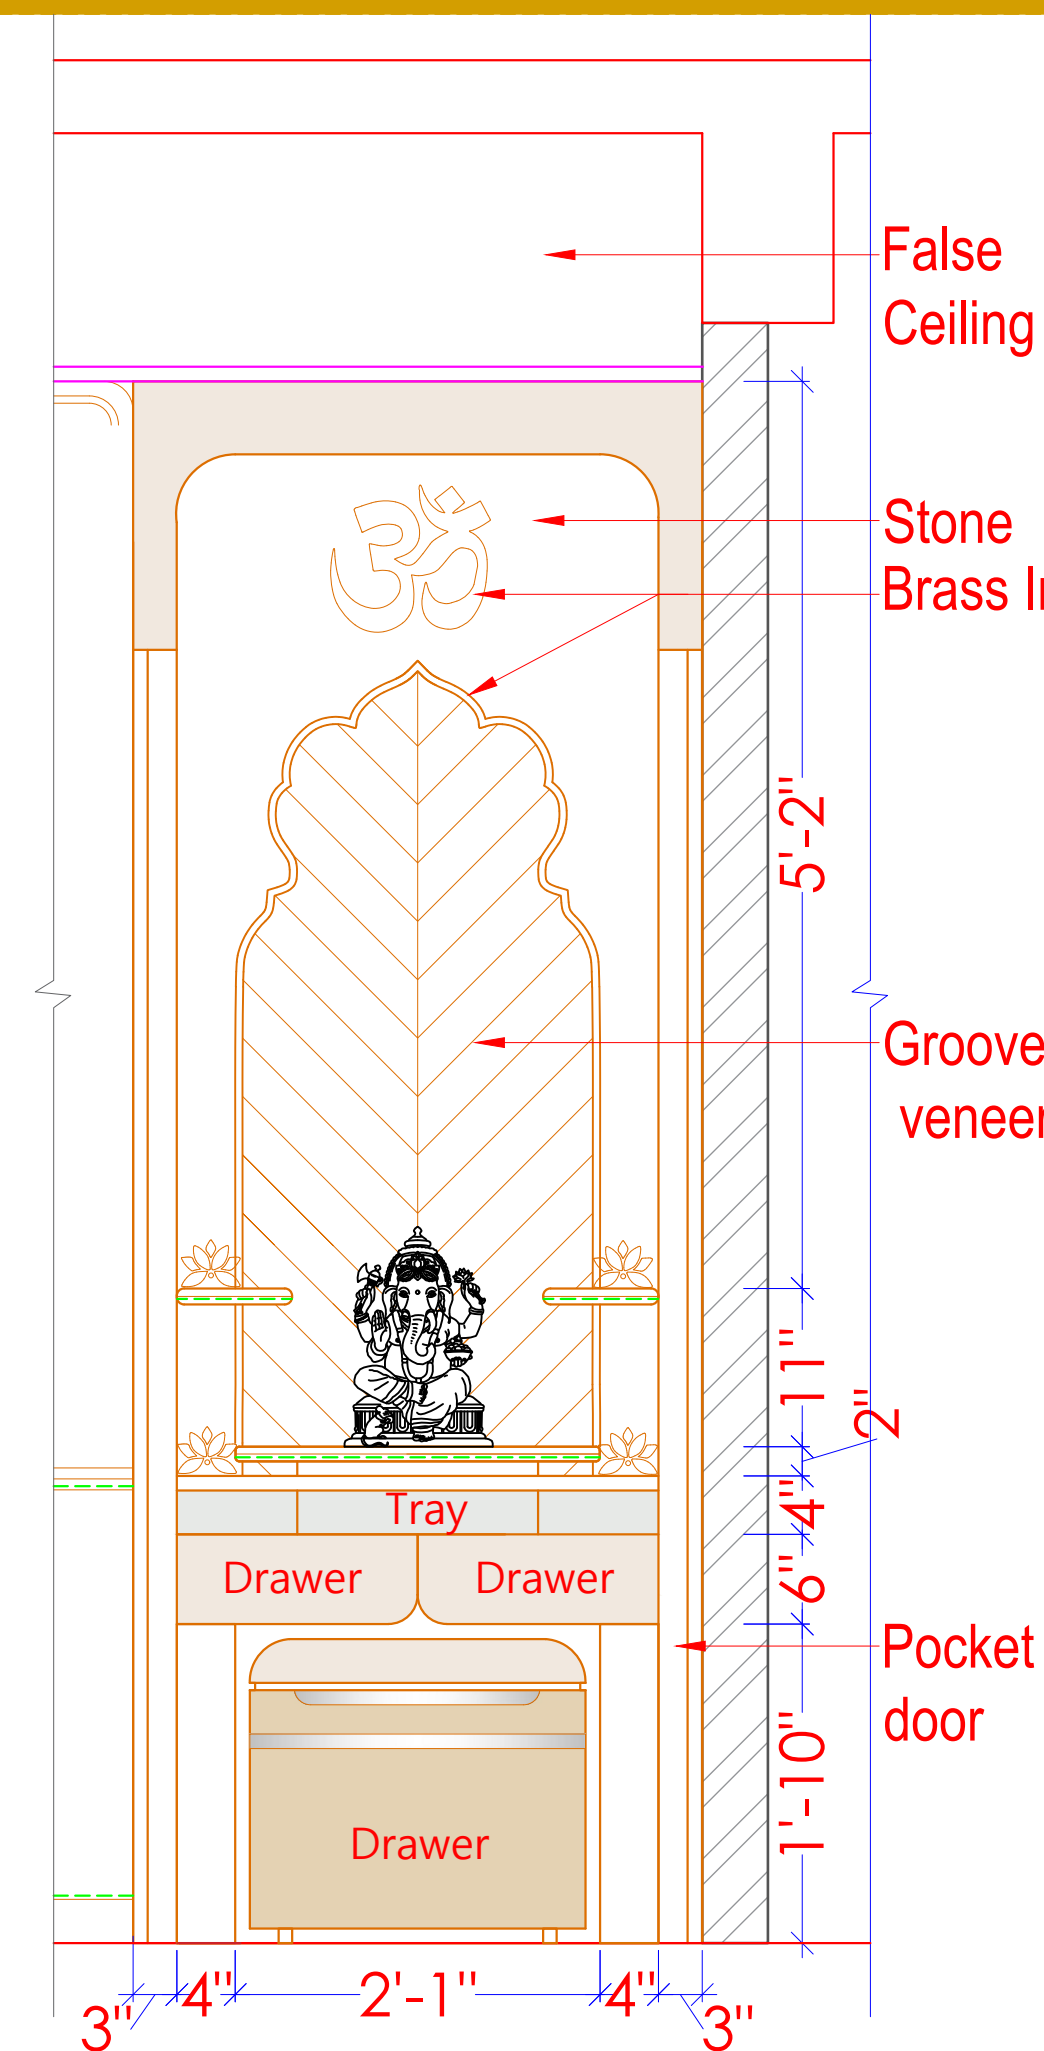

INTERNAL ELEVATION

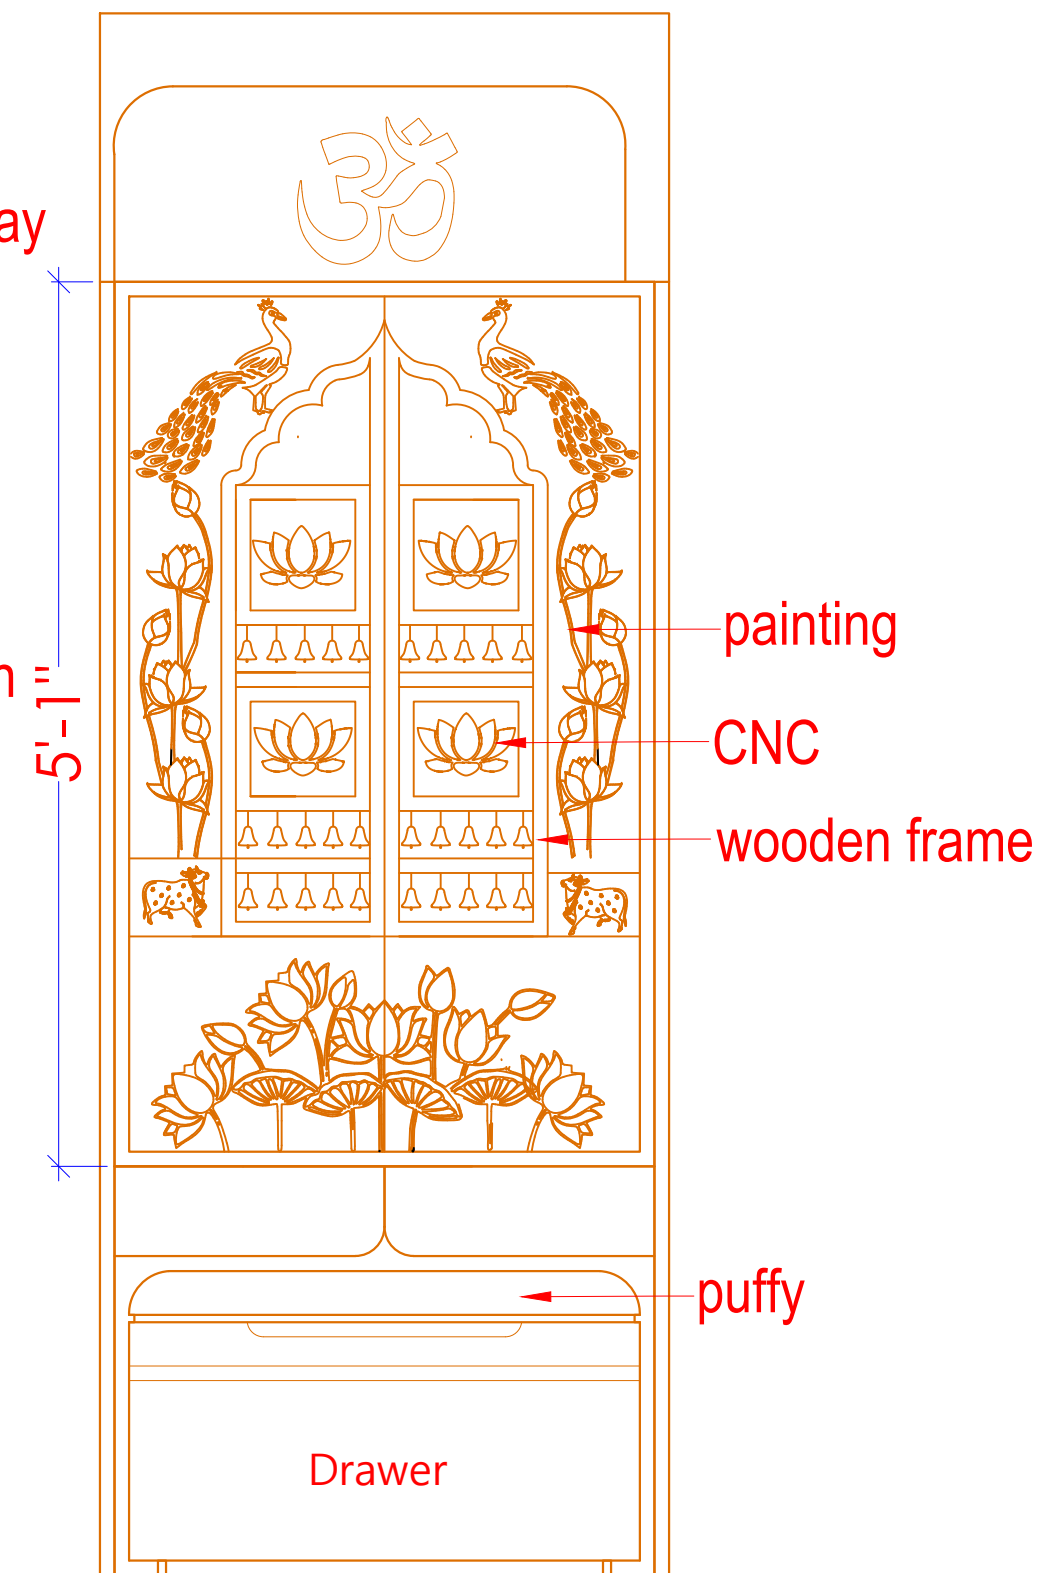

EXTERNAL ELEVATION

DRAWING TITLE :

KITCHEN
MANDIR DETAIL

NOTES:

* DO NOT SCALE THE DRAWING.
* ALL DIMENSIONS ARE IN FEET \ INCHES.
* ANY DISCREPENCY IN THE DRAWING
TO BE BROUGHT IN THE DESIGNER'S
NOTICE BEFORE IMPLEMENTATION
ON SITE.

SITE ADDRESS:

SAVAD
VADODARA

CLIENT NAME:

RONAK PANCHOLI

DATE:

02-06-2025

NORTH:

DRAWING DETAIL

REVISION NO.

R1 R2 R3

REVISED DATE:

12/02/26

SCALE:

N.T.S

DRAWN BY:


ARCHANA

CHECKED BY:

MITTAL

www.mayaspace.studio
mayaspace.studio@gmail.com
+918980144077
@mayaspace.studio



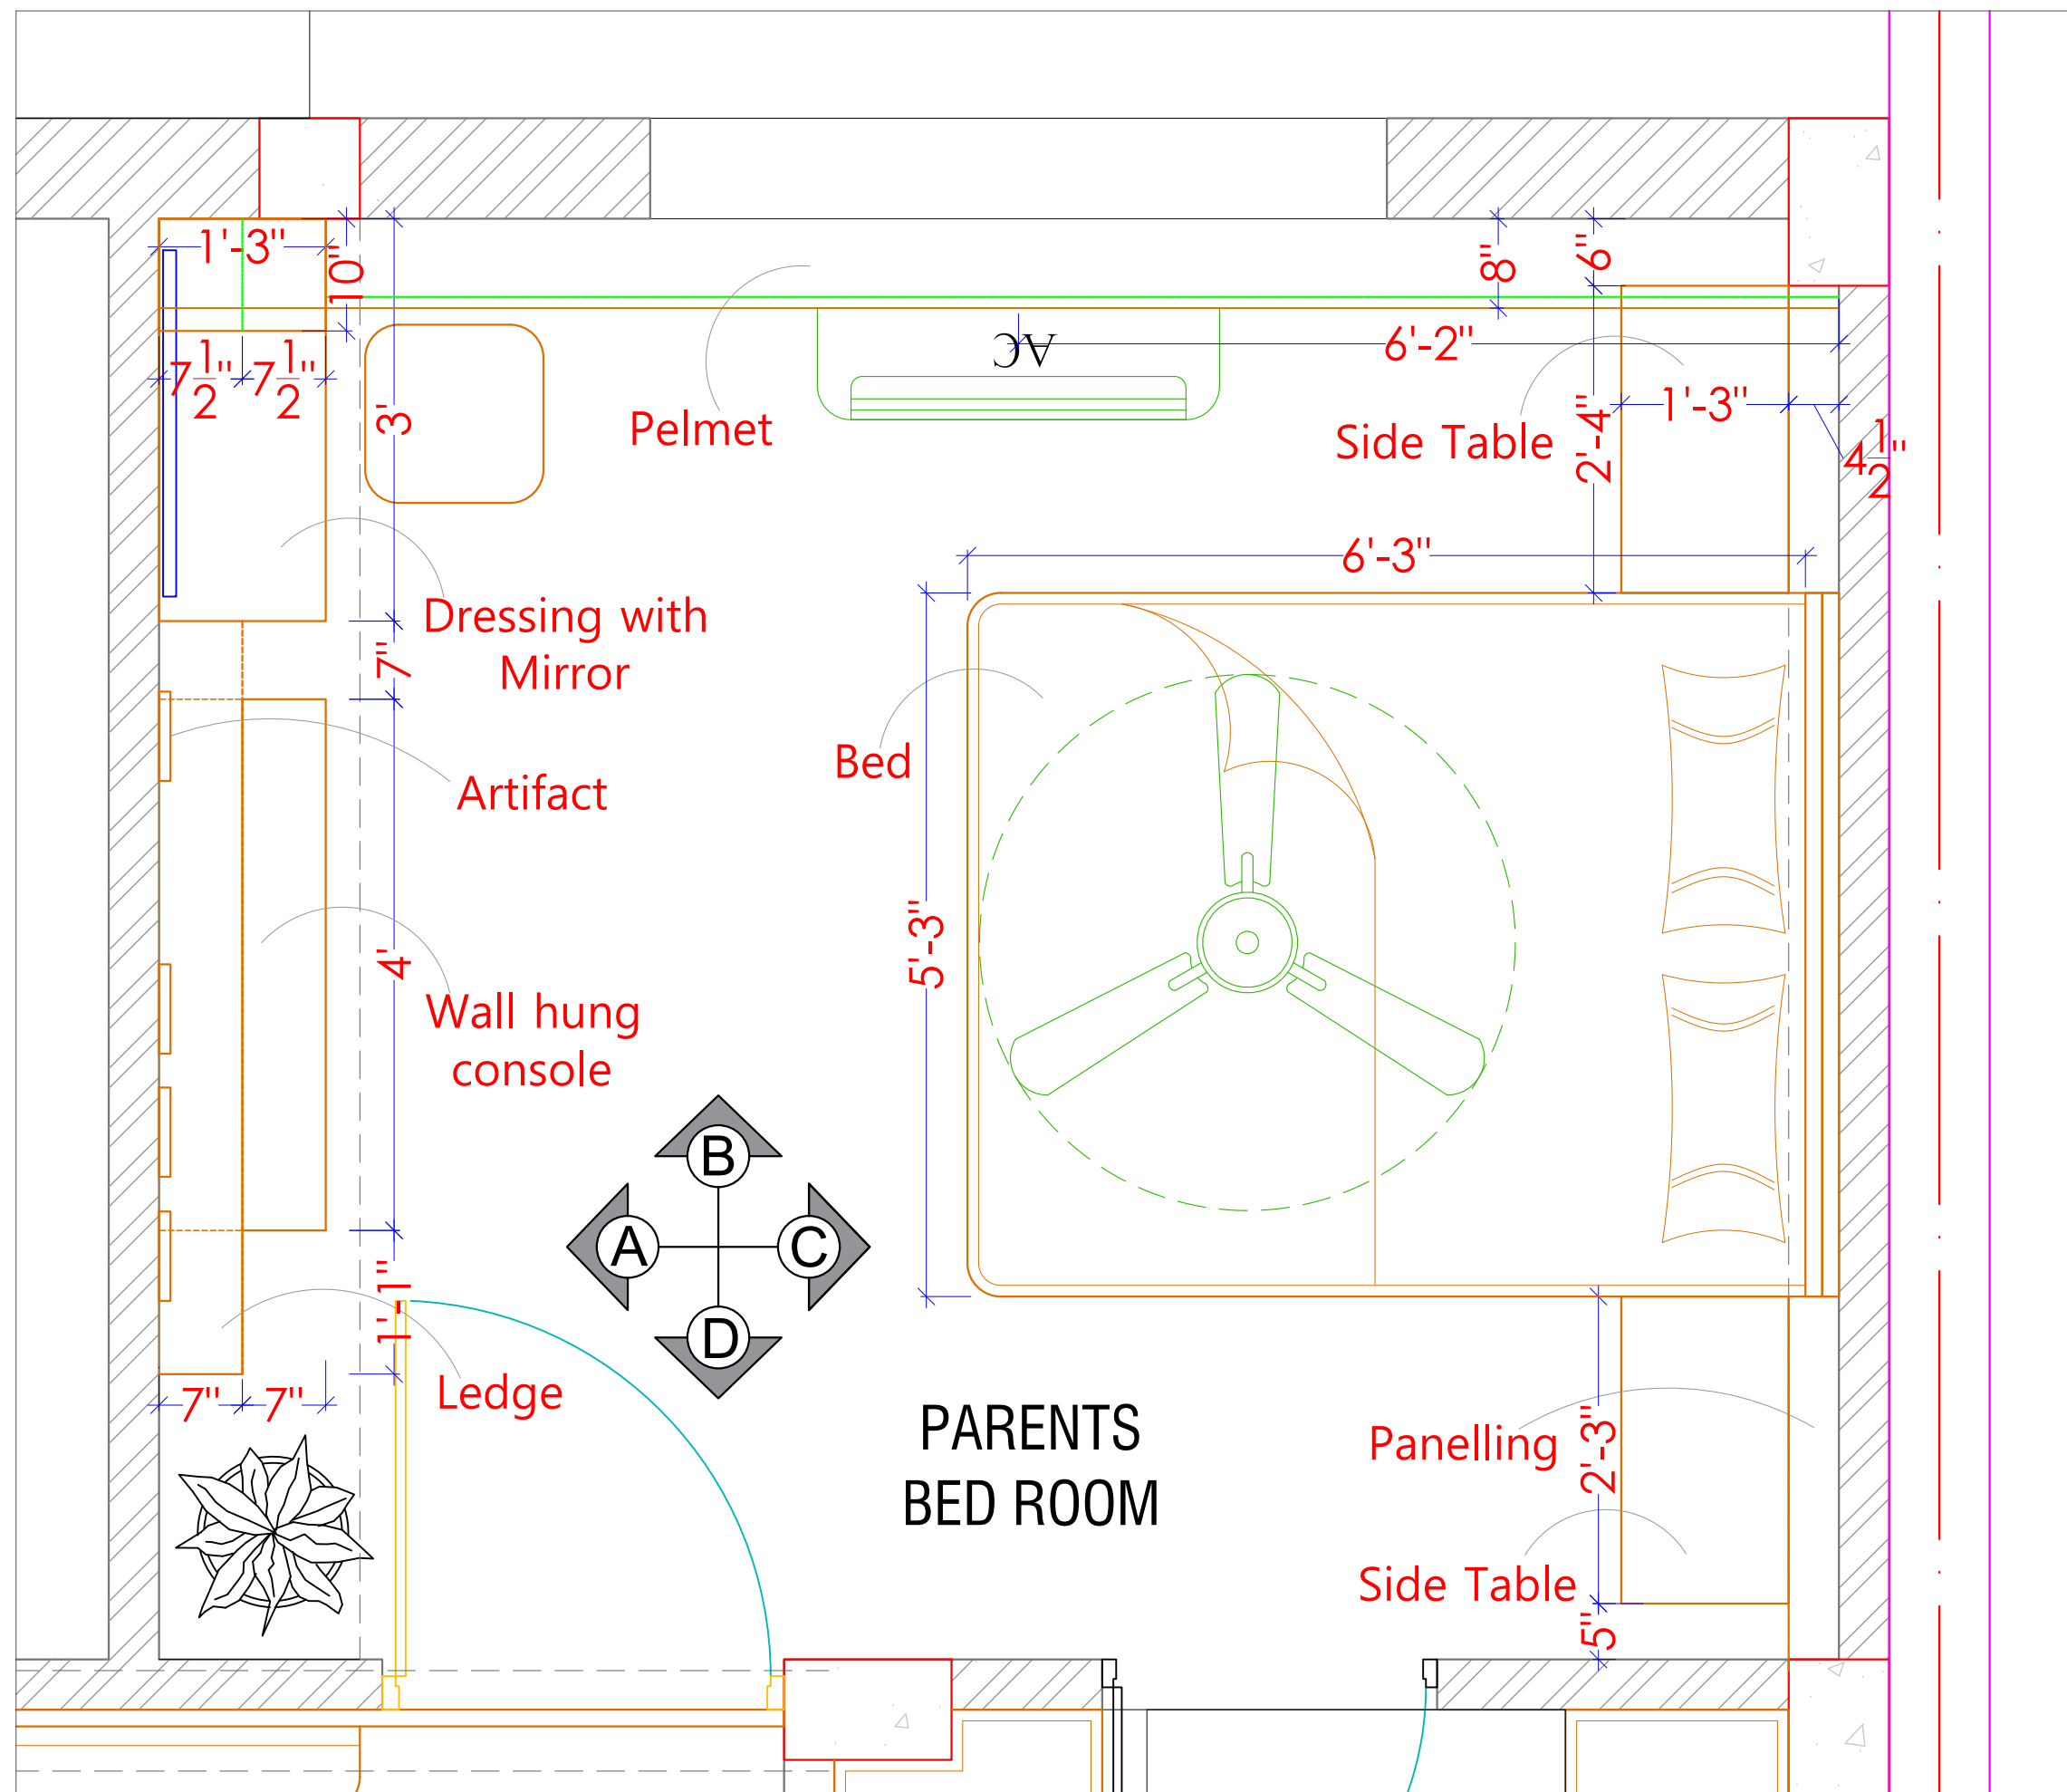

PLAN

DRAWING TITLE :

PARENTS BEDROOM
FURNITURE LAYOUT

NOTES:
* DO NOT SCALE THE DRAWING.
* ALL DIMENSIONS ARE IN FEET \ INCHES.
* ANY DISCREPENCY IN THE DRAWING
TO BE BROUGHT IN THE DESIGNER'S
NOTICE BEFORE IMPLEMENTATION
ON SITE.

SITE ADDRESS:
SAVAD
VADODARA

CLIENT NAME:
RONAK PANCHOLI

DATE: 02-06-2025


NORTH:

DRAWING DETAIL

REVISION NO.	R1	R2	R3
REVISED DATE:	12/02/26		
SCALE:	N.T.S		
DRAWN BY:	ARCHANA		
CHECKED BY:	MITTAL		

www.mayaspace.studio
 mayaspace.studio@gmail.com
 +918980144077
 @mayaspace.studio



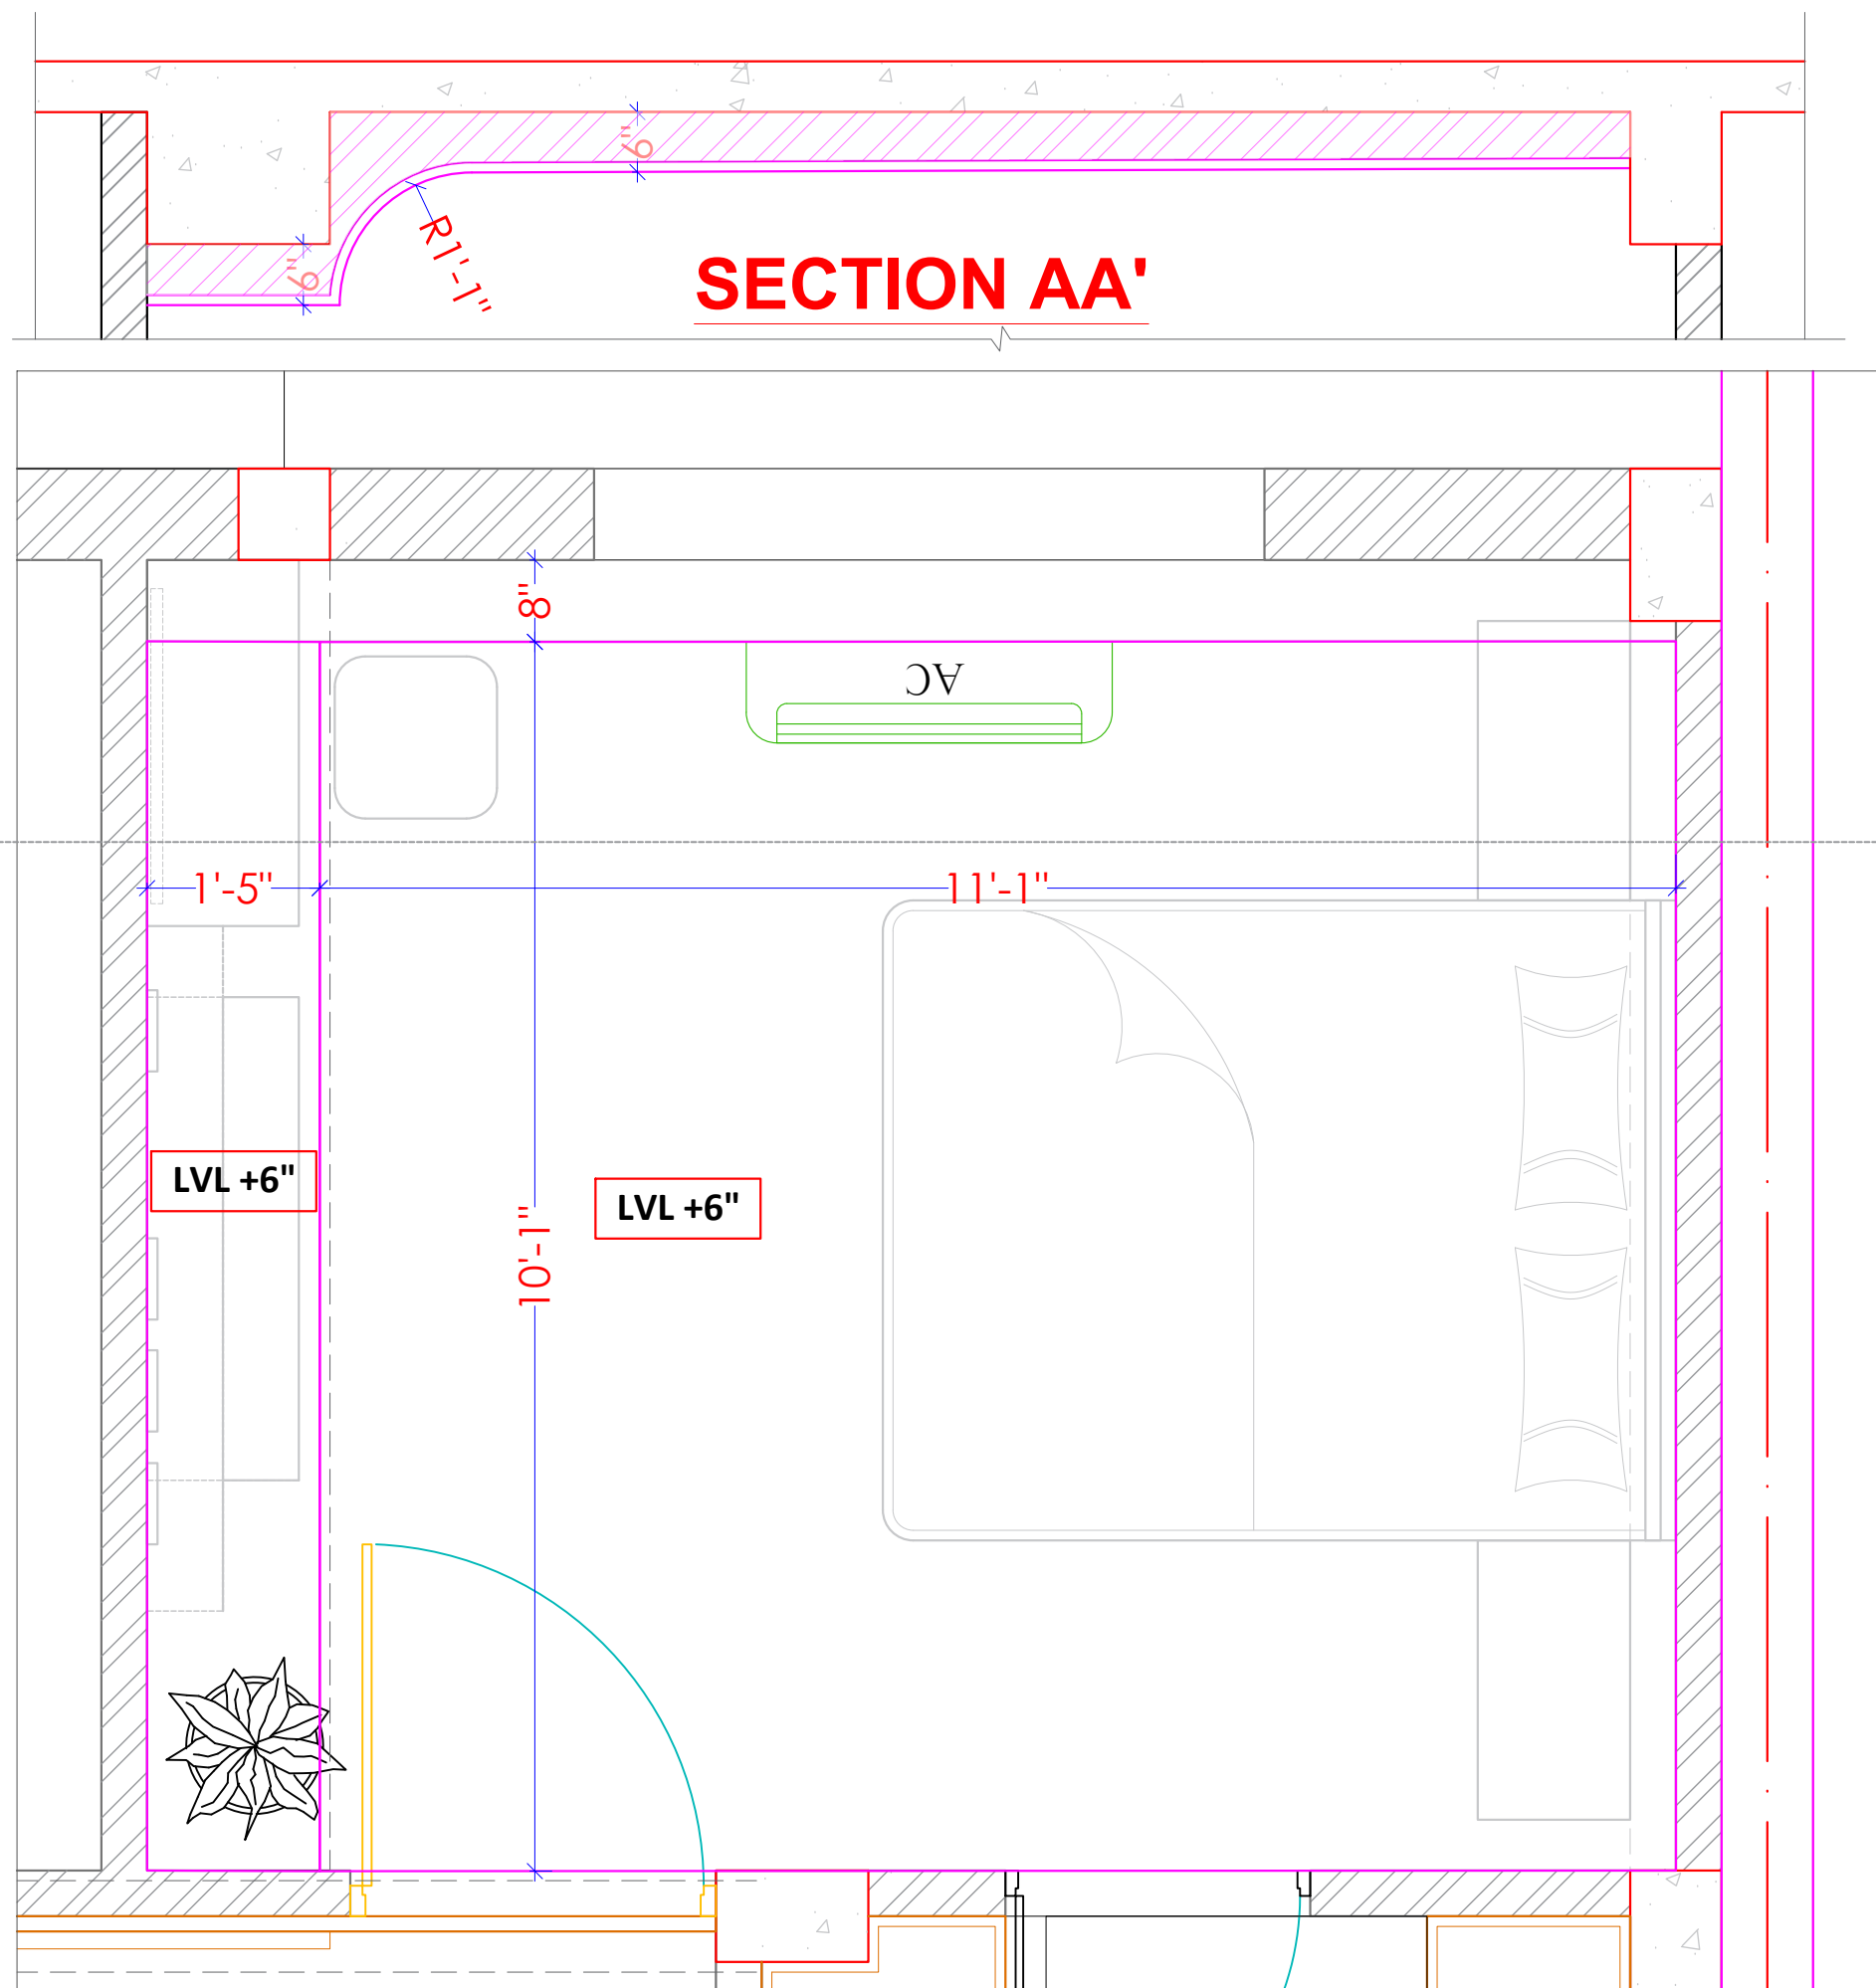

FALSE CEILING LAYOUT

**PARENTS BEDROOM
LIGHTING LAYOUT**

NOTES:

- * DO NOT SCALE THE DRAWING.
- * ALL DIMENSIONS ARE IN FEET \ INCHES.
- * ANY DISCREPANCY IN THE DRAWING TO BE BROUGHT IN THE DESIGNER'S NOTICE BEFORE IMPLEMENTATION ON SITE.

SITE ADDRESS:

SAVAD
VADODARA

CLIENT NAME:

RONAK PANCHOLI

DATE:

02-06-2025

NORTH:




DRAWING DETAIL

REVISION NO.	R1	R2	R3
REVISED DATE:	12/02/26		
SCALE:	N.T.S		
DRAWN BY:	ARCHANA		
CHECKED BY:	MITTAL		

	www.mayaspace.studio
	mayaspace.studio@gmail.com
	+918980144077
	@mayaspace.studio



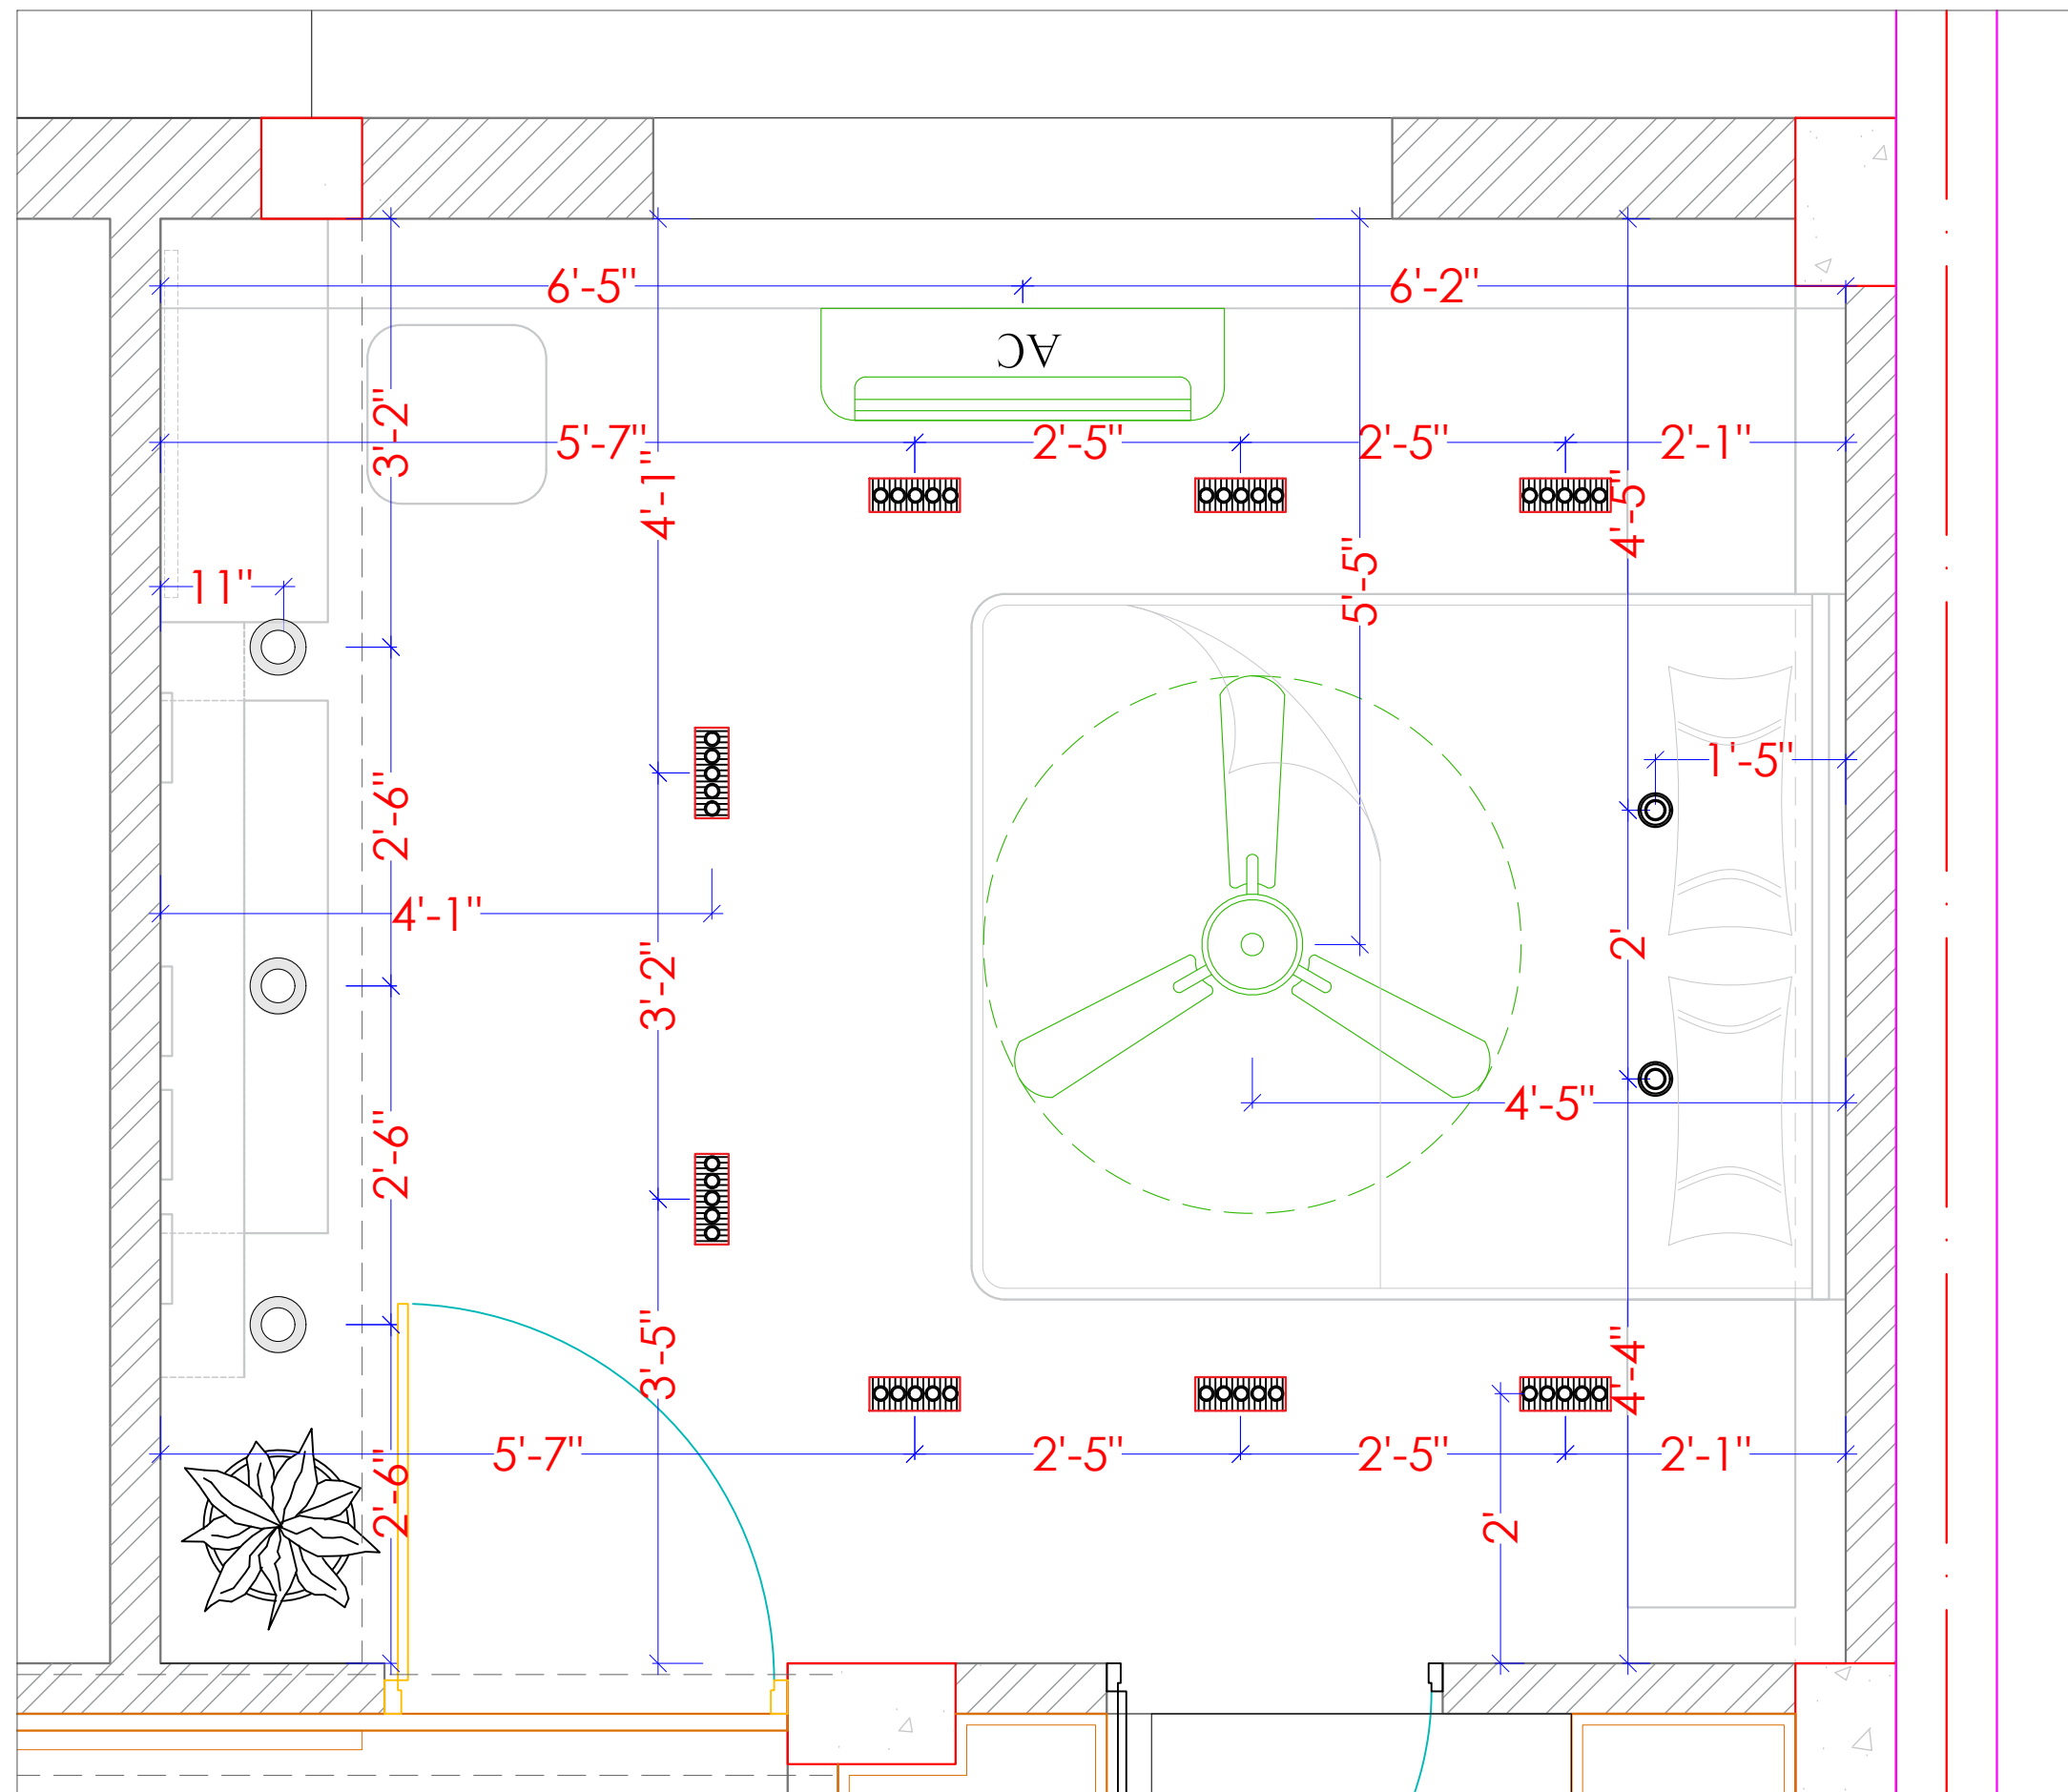

LIGHTING LAYOUT

PARENTS BEDROOM LIGHTING LAYOUT

NOTES:

- * DO NOT SCALE THE DRAWING.
- * ALL DIMENSIONS ARE IN FEET \ INCHES.
- * ANY DISCREPANCY IN THE DRAWING TO BE BROUGHT IN THE DESIGNER'S NOTICE BEFORE IMPLEMENTATION ON SITE.

SITE ADDRESS:

SAVAD
VADODARA

CLIENT NAME:

RONAK PANCHOLI

DATE:

02-06-2025

NORTH:




DRAWING DETAIL

REVISION NO.	R1	R2	R3
REVISED DATE:	04/02/26		
SCALE:	N.T.S		
DRAWN BY:	ARCHANA		
CHECKED BY:	MITTAL		

	www.mayaspace.studio
	mayaspace.studio@gmail.com
	+918980144077
	@mayaspace.studio



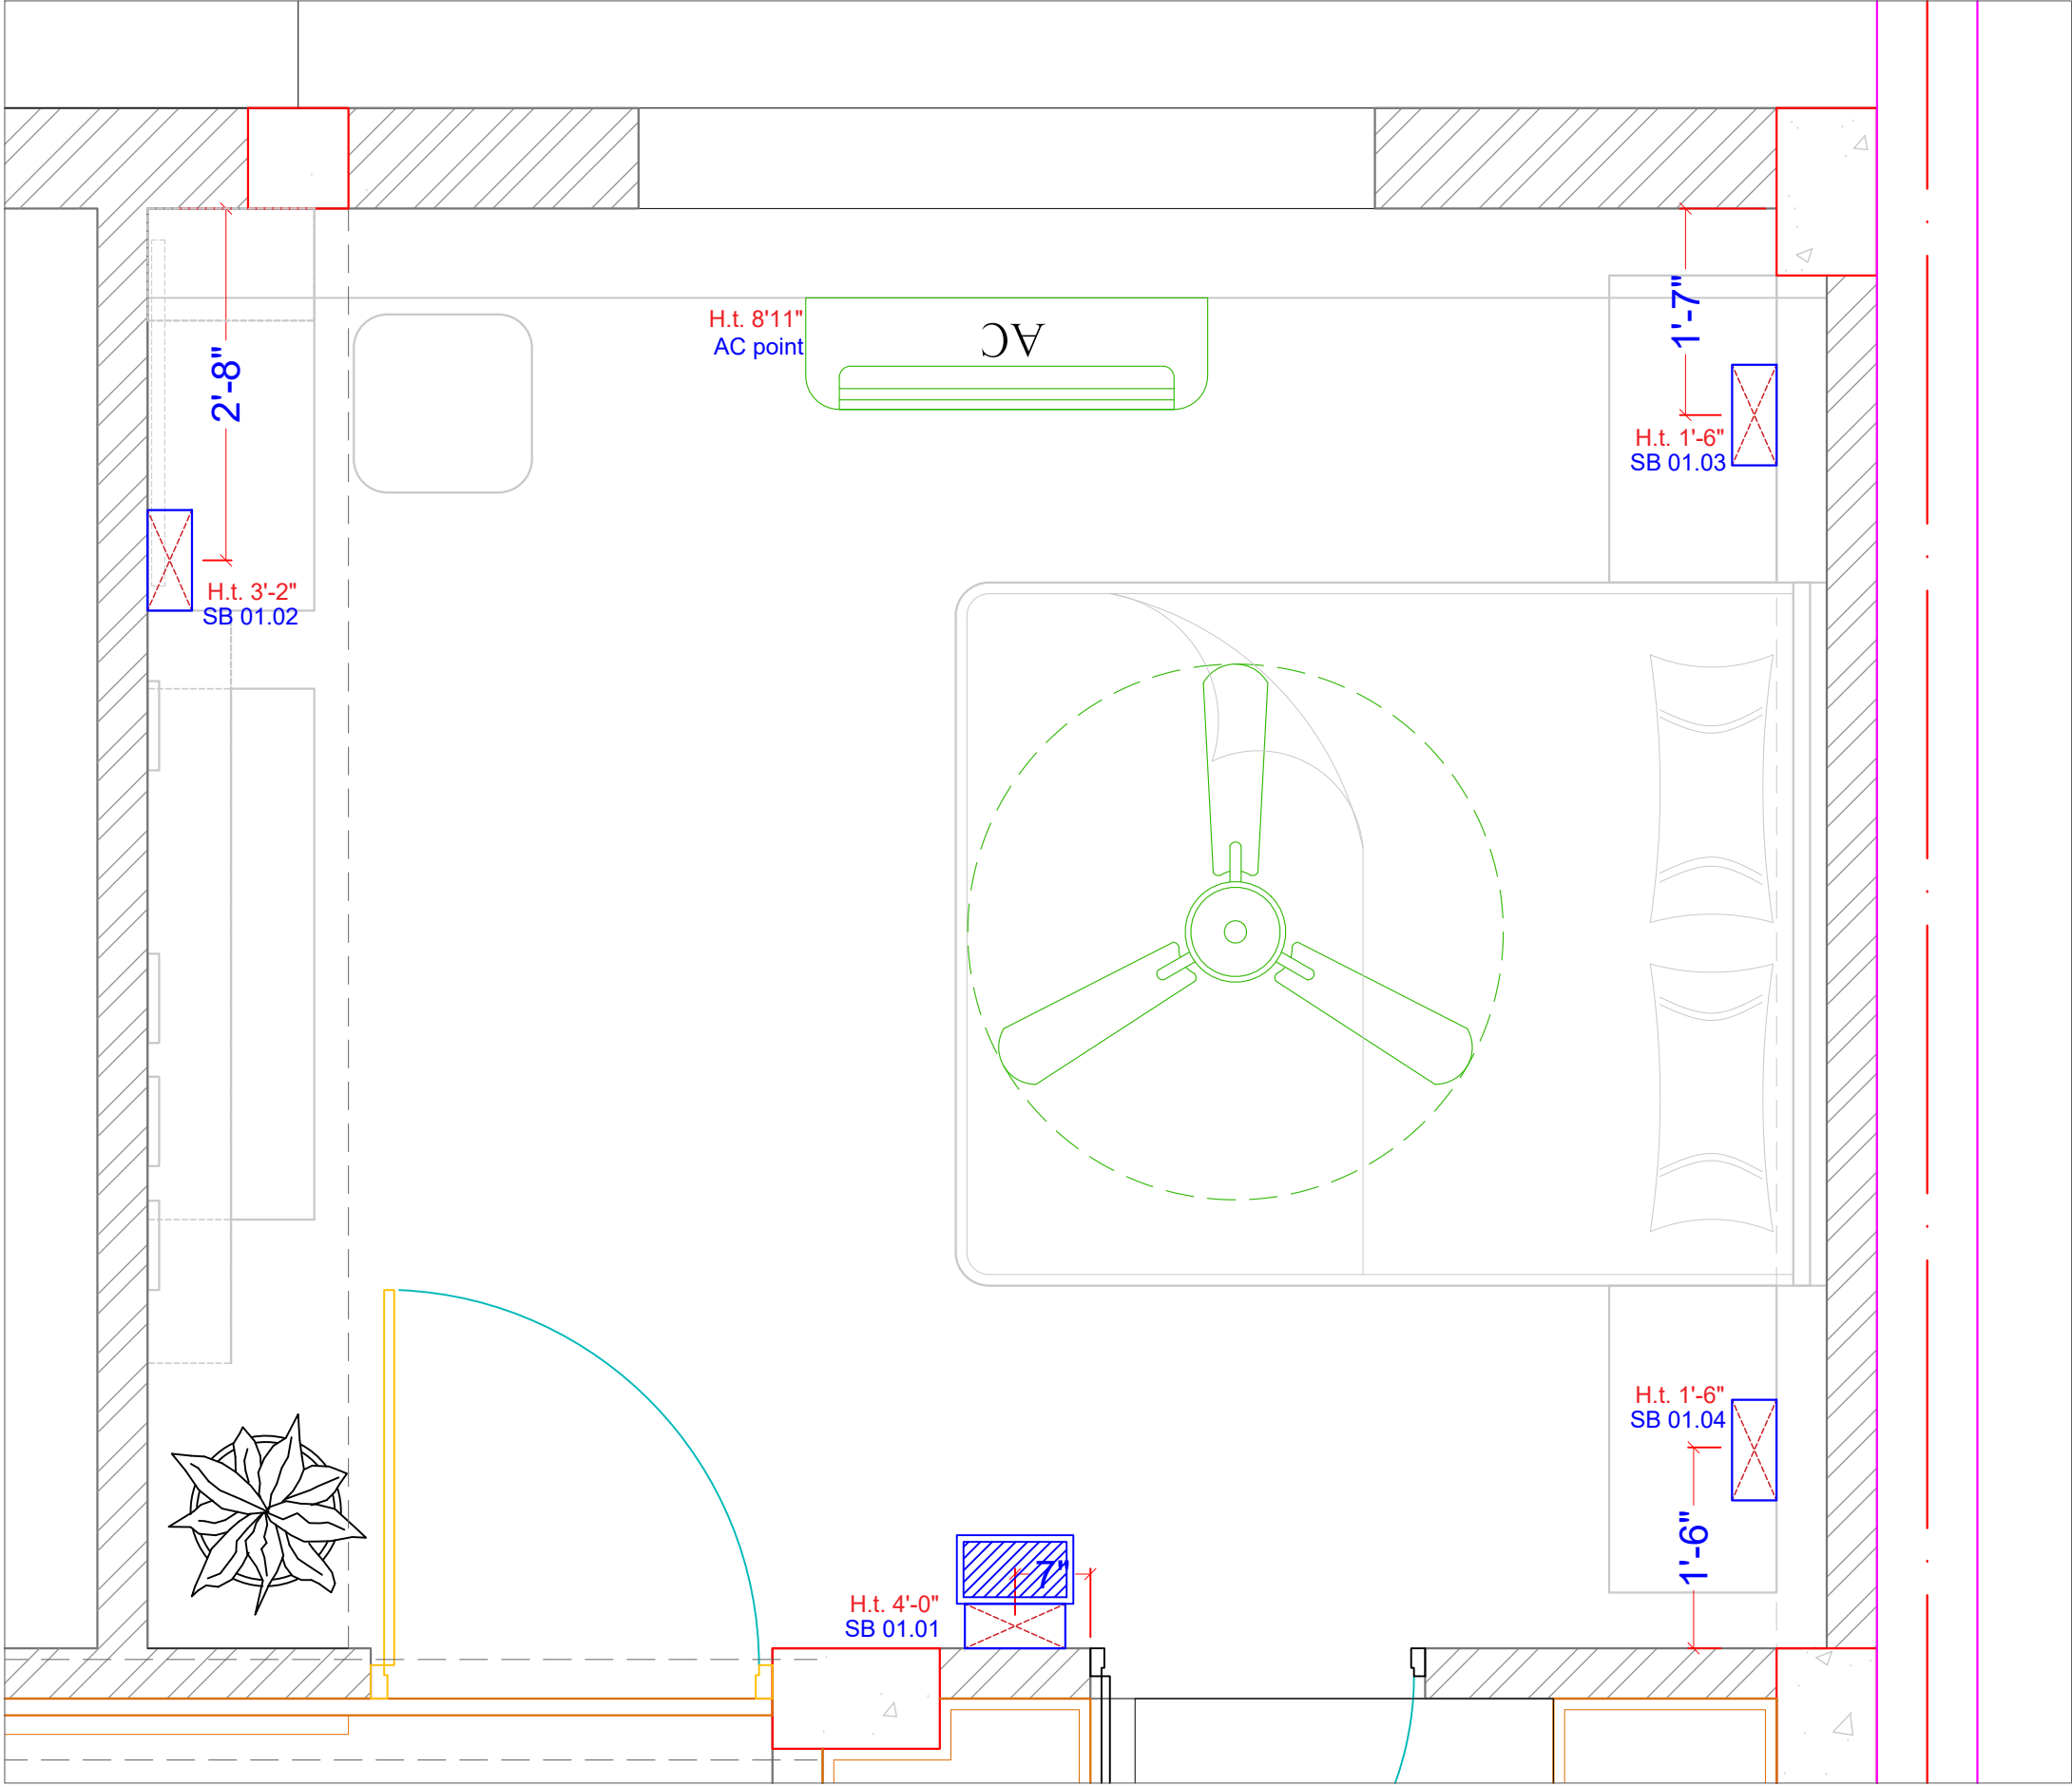

SWITCH BOARD LAYOUT

PARENTS BEDROOM SWITCH BOARD LAYOUT

NOTES:

- * DO NOT SCALE THE DRAWING.
- * ALL DIMENSIONS ARE IN FEET \ INCHES.
- * ANY DISCREPENCY IN THE DRAWING TO BE BROUGHT IN THE DESIGNER'S NOTICE BEFORE IMPLEMENTATION ON SITE.

SITE ADDRESS:

SAVAD
VADODARA

CLIENT NAME:

RONAK PANCHOLI

DATE:

02-06-2025

NORTH:




DRAWING DETAIL

REVISION NO.	R1	R2	R3
REVISED DATE:	04/02/26		
SCALE:	N.T.S		
DRAWN BY:	ARCHANA		
CHECKED BY:	MITTAL		

	www.mayaspace.studio
	mayaspace.studio@gmail.com
	+918980144077
	@mayaspace.studio



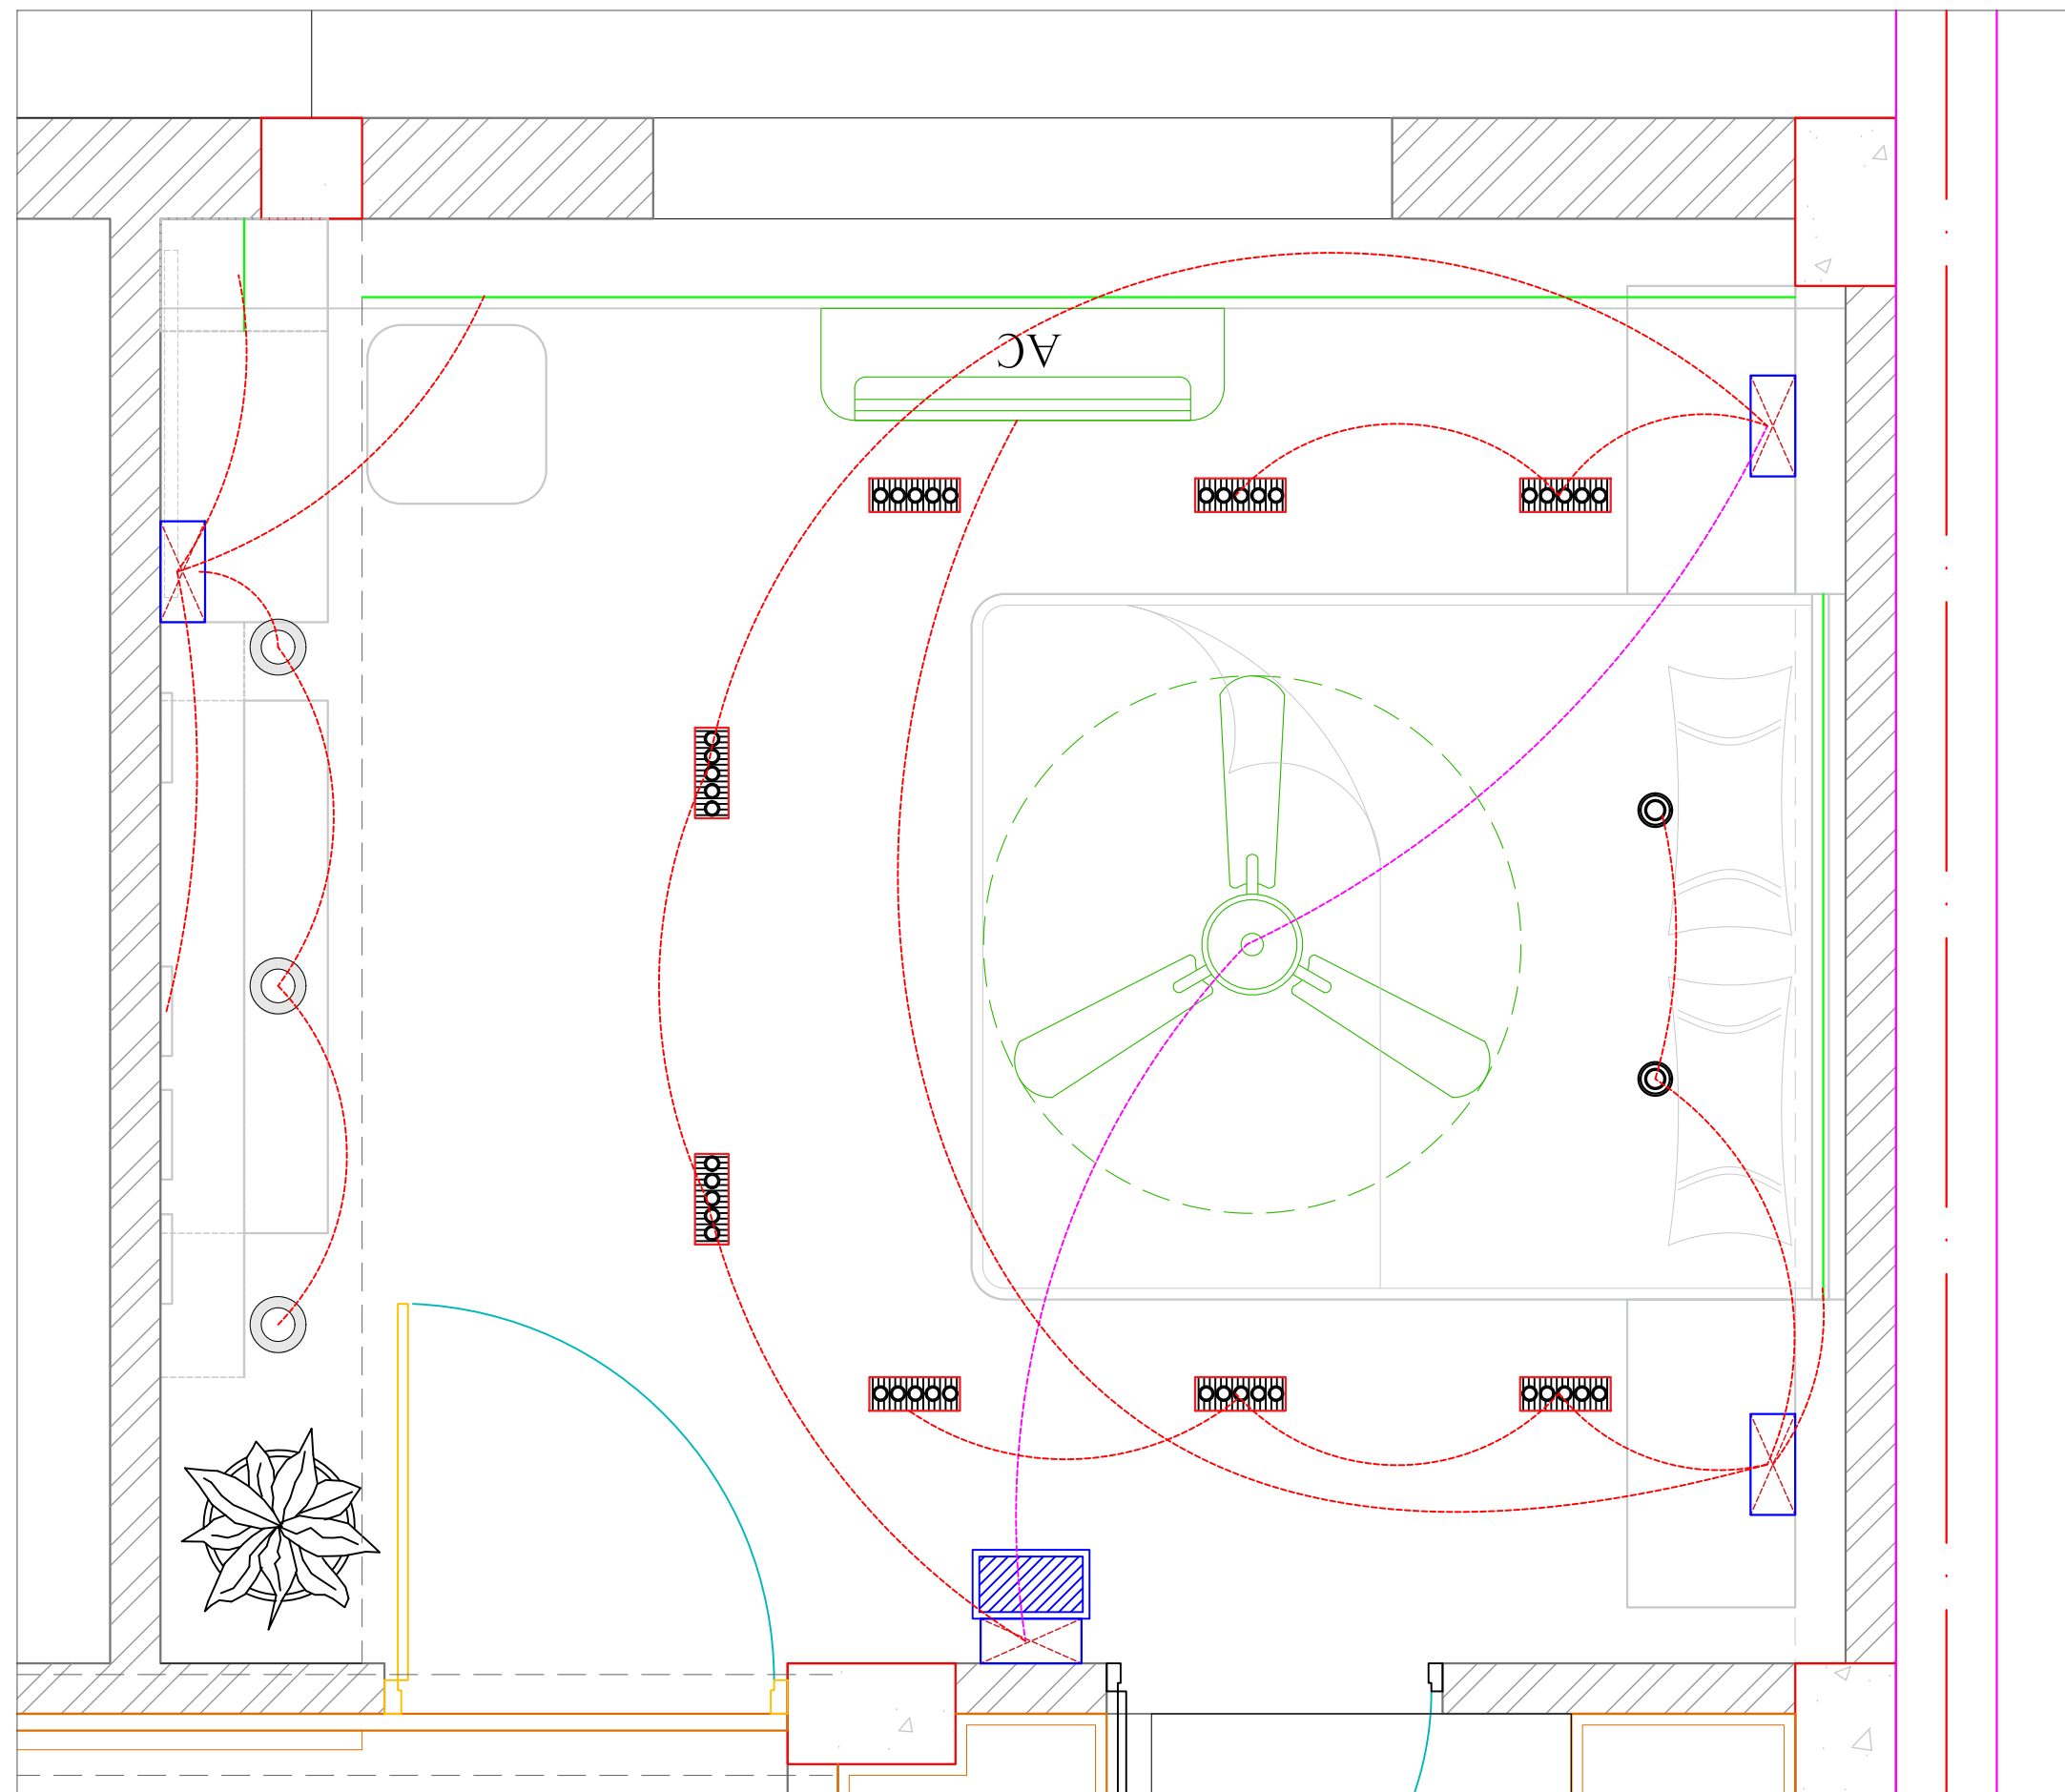

PARENTS BEDROOM LOOPING LAYOUT

NOTES:

- * DO NOT SCALE THE DRAWING.
- * ALL DIMENSIONS ARE IN FEET \ INCHES.
- * ANY DISCREPANCY IN THE DRAWING TO BE BROUGHT IN THE DESIGNER'S NOTICE BEFORE IMPLEMENTATION ON SITE.

SITE ADDRESS:

SAVAD
VADODARA

CLIENT NAME:

RONAK PANCHOLI

DATE: 02-06-2025

NORTH:




DRAWING DETAIL

REVISION NO.	R1	R2	R3
REVISED DATE:	04/02/26		
SCALE:	N.T.S		
DRAWN BY:	ARCHANA		
CHECKED BY:	MITTAL		

	www.mayaspace.studio
	mayaspace.studio@gmail.com
	+918980144077
	@mayaspace.studio



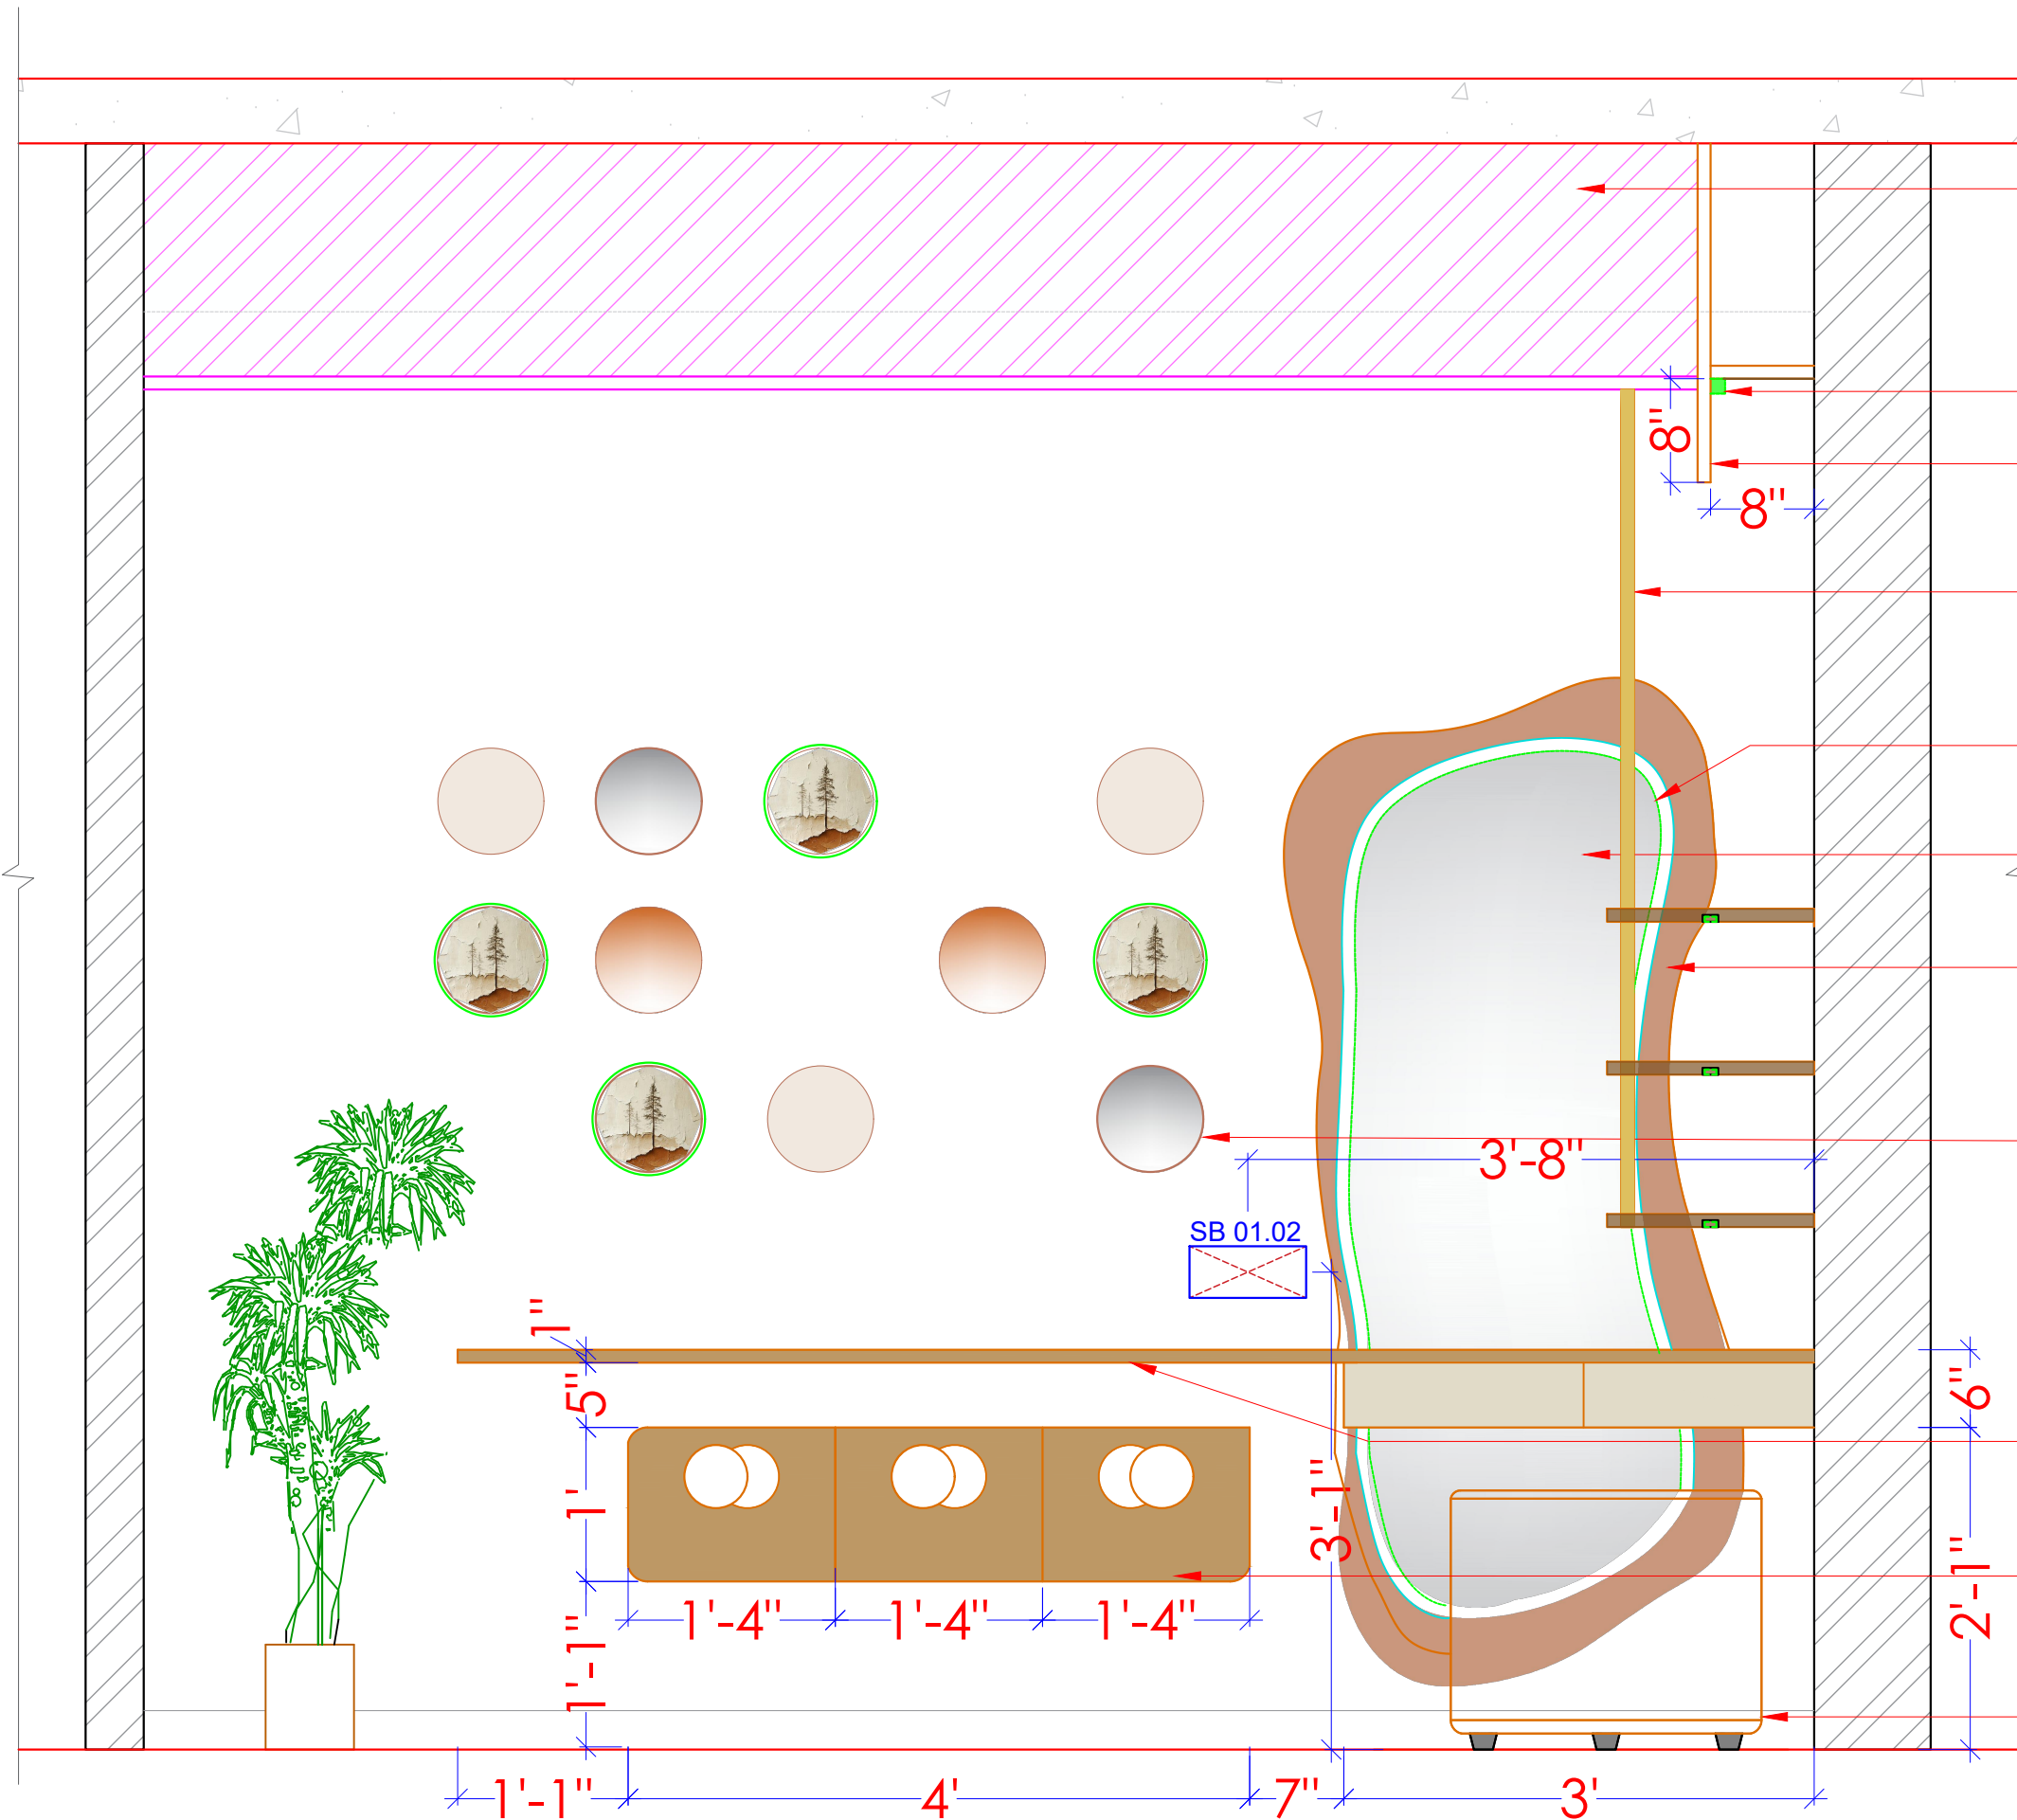

ELEVATION - A

- False Ceiling
- Indirect light
- Pelmet_wall color
- $\frac{3}{4}$ " dia. Brass rod indirect light
- Mirror
- Mirror border_Veneer finish
- Artifact/Lights /photos
- shelf_veneer finish
- Console_veneer
- Puffy

DRAWING TITLE :

**PARENTS BEDROOM
ELEVATION A**

NOTES:

- * DO NOT SCALE THE DRAWING.
- * ALL DIMENSIONS ARE IN FEET \ INCHES.
- * ANY DISCREPENCY IN THE DRAWING TO BE BROUGHT IN THE DESIGNER'S NOTICE BEFORE IMPLEMENTATION ON SITE.

SITE ADDRESS:

**SAVAD
VADODARA**

CLIENT NAME:

RONAK PANCHOLI

DATE: 02-06-2025

NORTH:

DRAWING DETAIL

REVISION NO.	R1	R2	R3
REVISED DATE:	12/02/26		
SCALE:	N.T.S		
DRAWN BY:	ARCHANA		
CHECKED BY:	MITTAL		


www.mayaspace.studio

mayaspace.studio@gmail.com

+918980144077

@mayaspace.studio

**Maya
SPACE STUDIO**

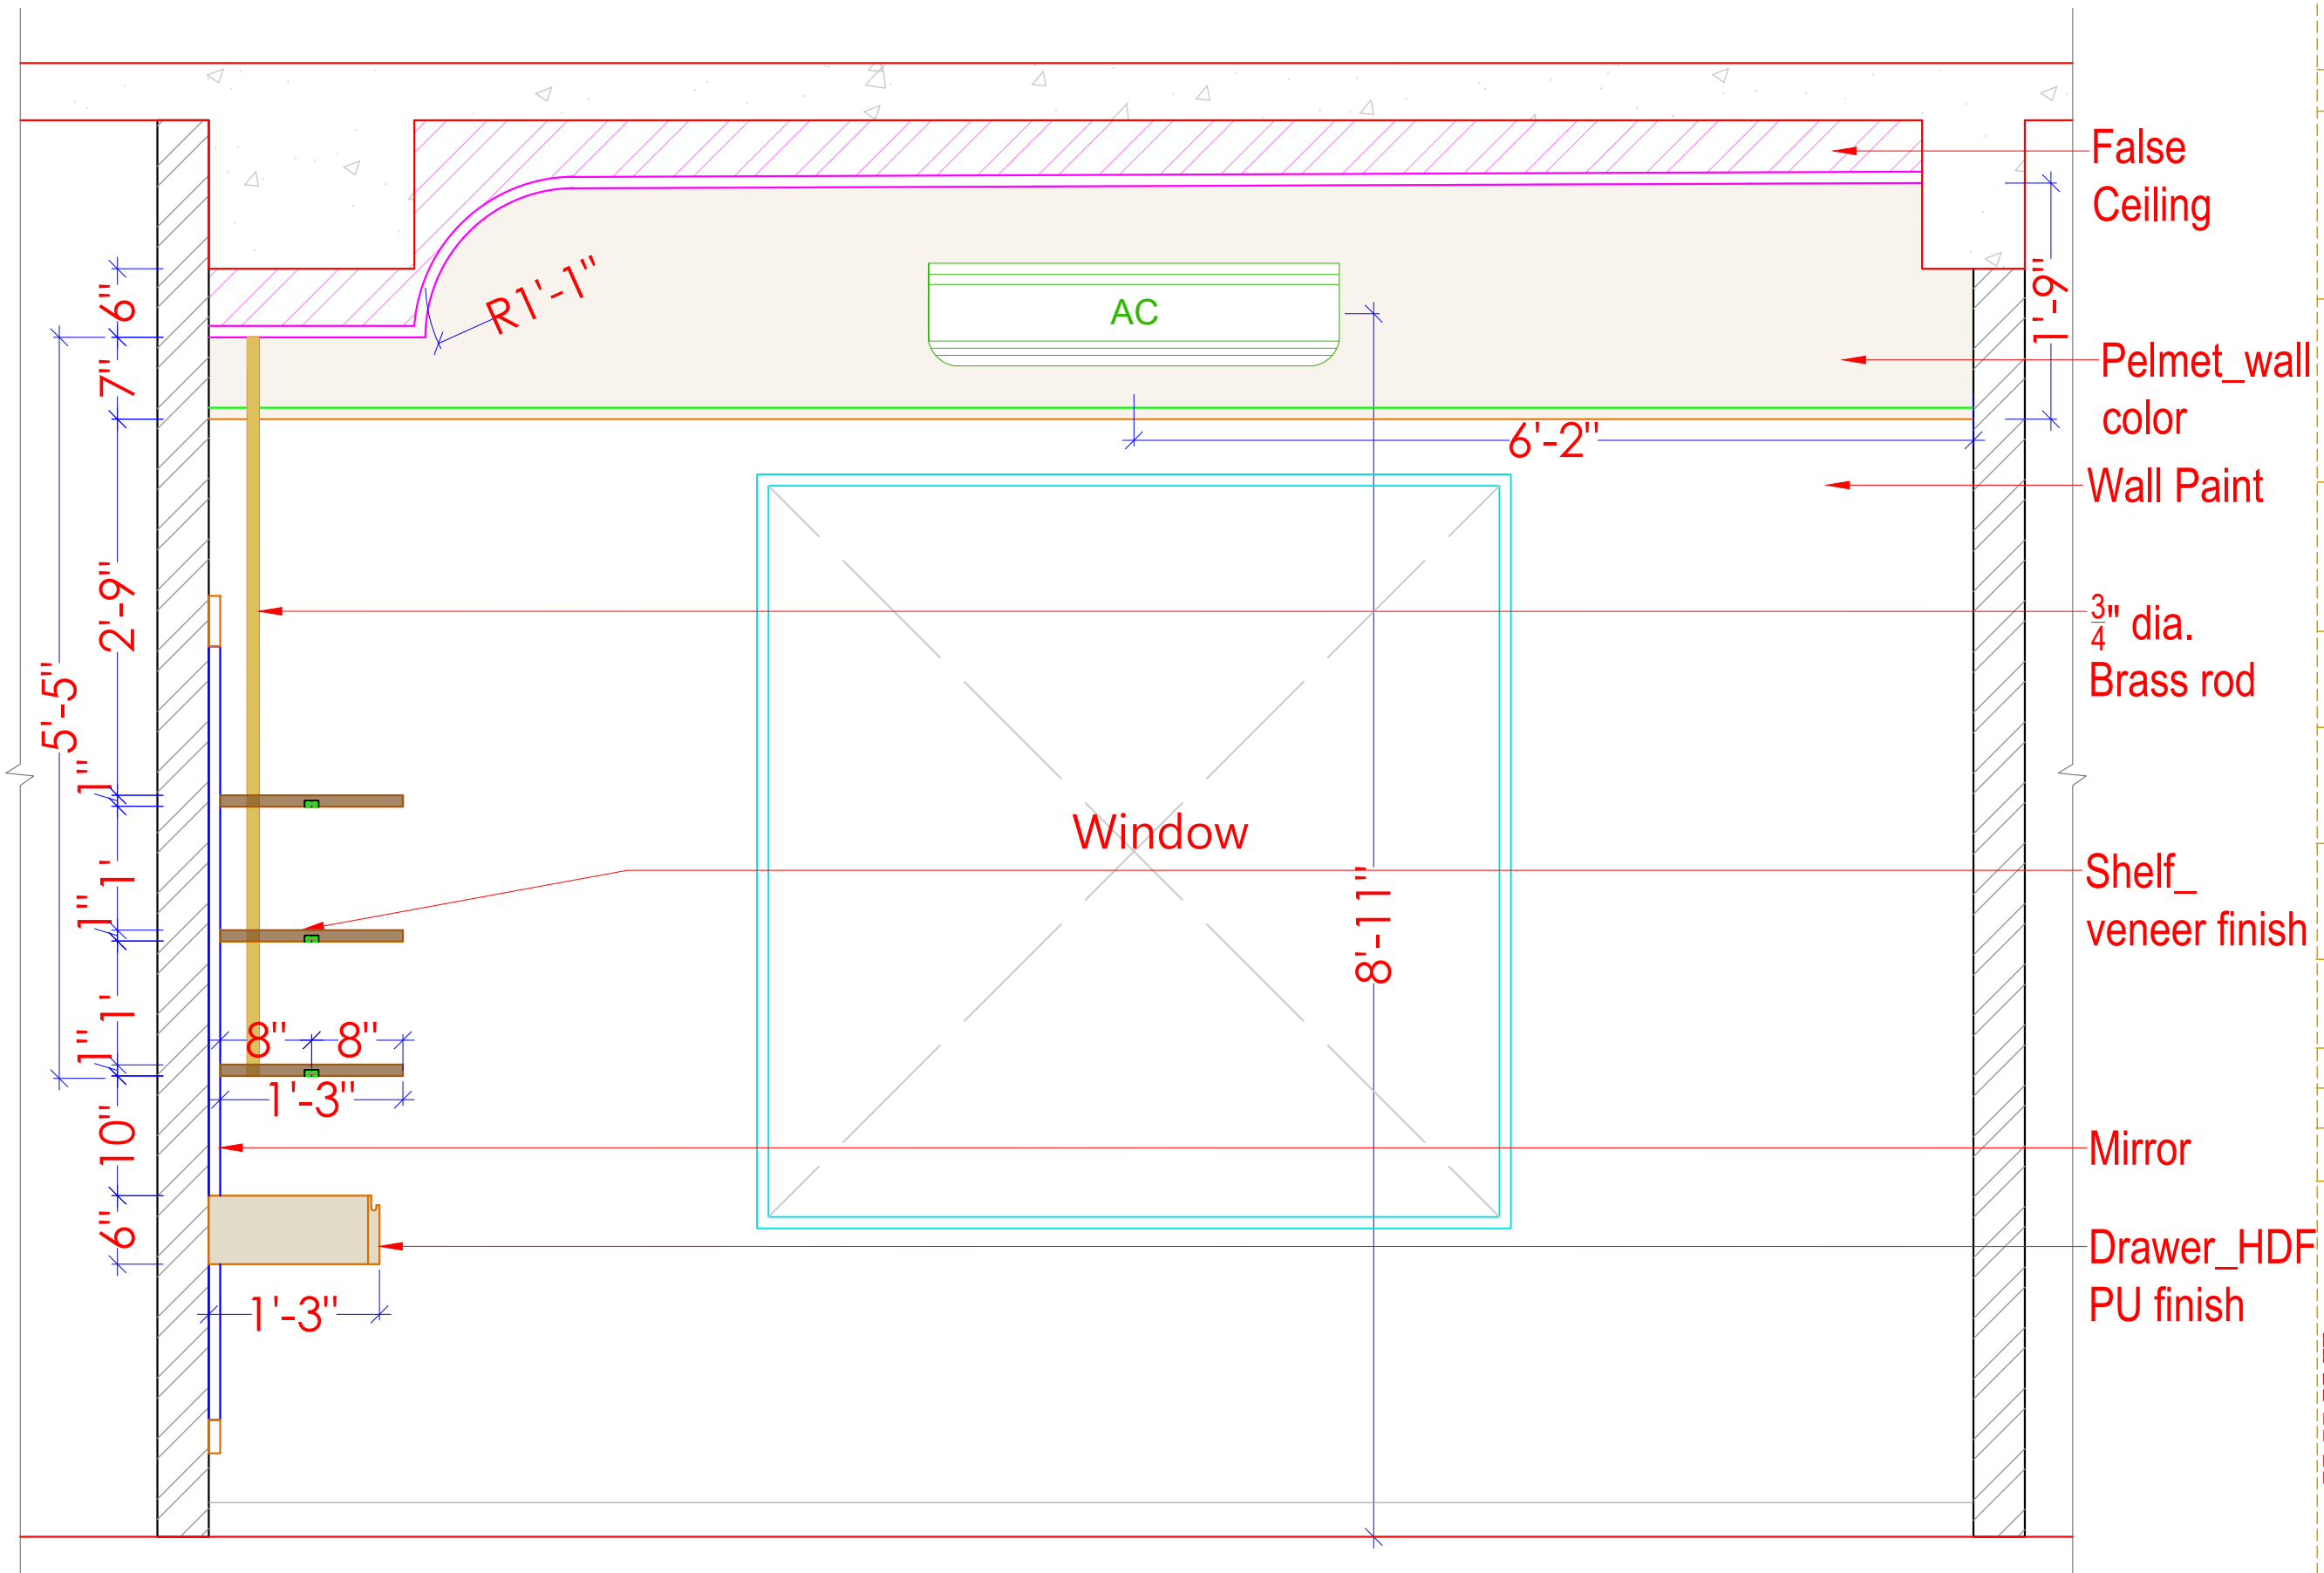

ELEVATION - B

DRAWING TITLE :

PARENTS BEDROOM
ELEVATION B

NOTES:

- * DO NOT SCALE THE DRAWING.
- * ALL DIMENSIONS ARE IN FEET \ INCHES.
- * ANY DISCREPANCY IN THE DRAWING TO BE BROUGHT IN THE DESIGNER'S NOTICE BEFORE IMPLEMENTATION ON SITE.

SITE ADDRESS:

SAVAD
VADODARA

CLIENT NAME:

RONAK PANCHOLI

DATE:

02-06-2025

NORTH:

DRAWING DETAIL

REVISION NO.

R1 R2 R3

REVISED DATE:

12/02/26

SCALE:

N.T.S

DRAWN BY:

ARCHANA

CHECKED BY:

MITTAL

www.mayaspace.studio
mayaspace.studio@gmail.com
+918980144077
@mayaspace.studio



PARENTS BEDROOM ELEVATION C

- * DO NOT SCALE THE DRAWING.
- * ALL DIMENSIONS ARE IN FEET \ INCHES.
- * ANY DISCREPANCY IN THE DRAWING TO BE BROUGHT IN THE DESIGNER'S NOTICE BEFORE IMPLEMENTATION ON SITE.


SAVAD
VADODARA

RONAK PANCHOLI


NORTH:

REVISION NO.	R1	R2	R3
REVISED DATE:	07/02/2025		
SCALE:	N.T.S		
DRAWN BY:	ARCHANA		
CHECKED BY:	MITTAL		

	www.mayaspace.studio
	mayaspace.studio@gmail.com
	+918980144077
	@mayaspace.studio

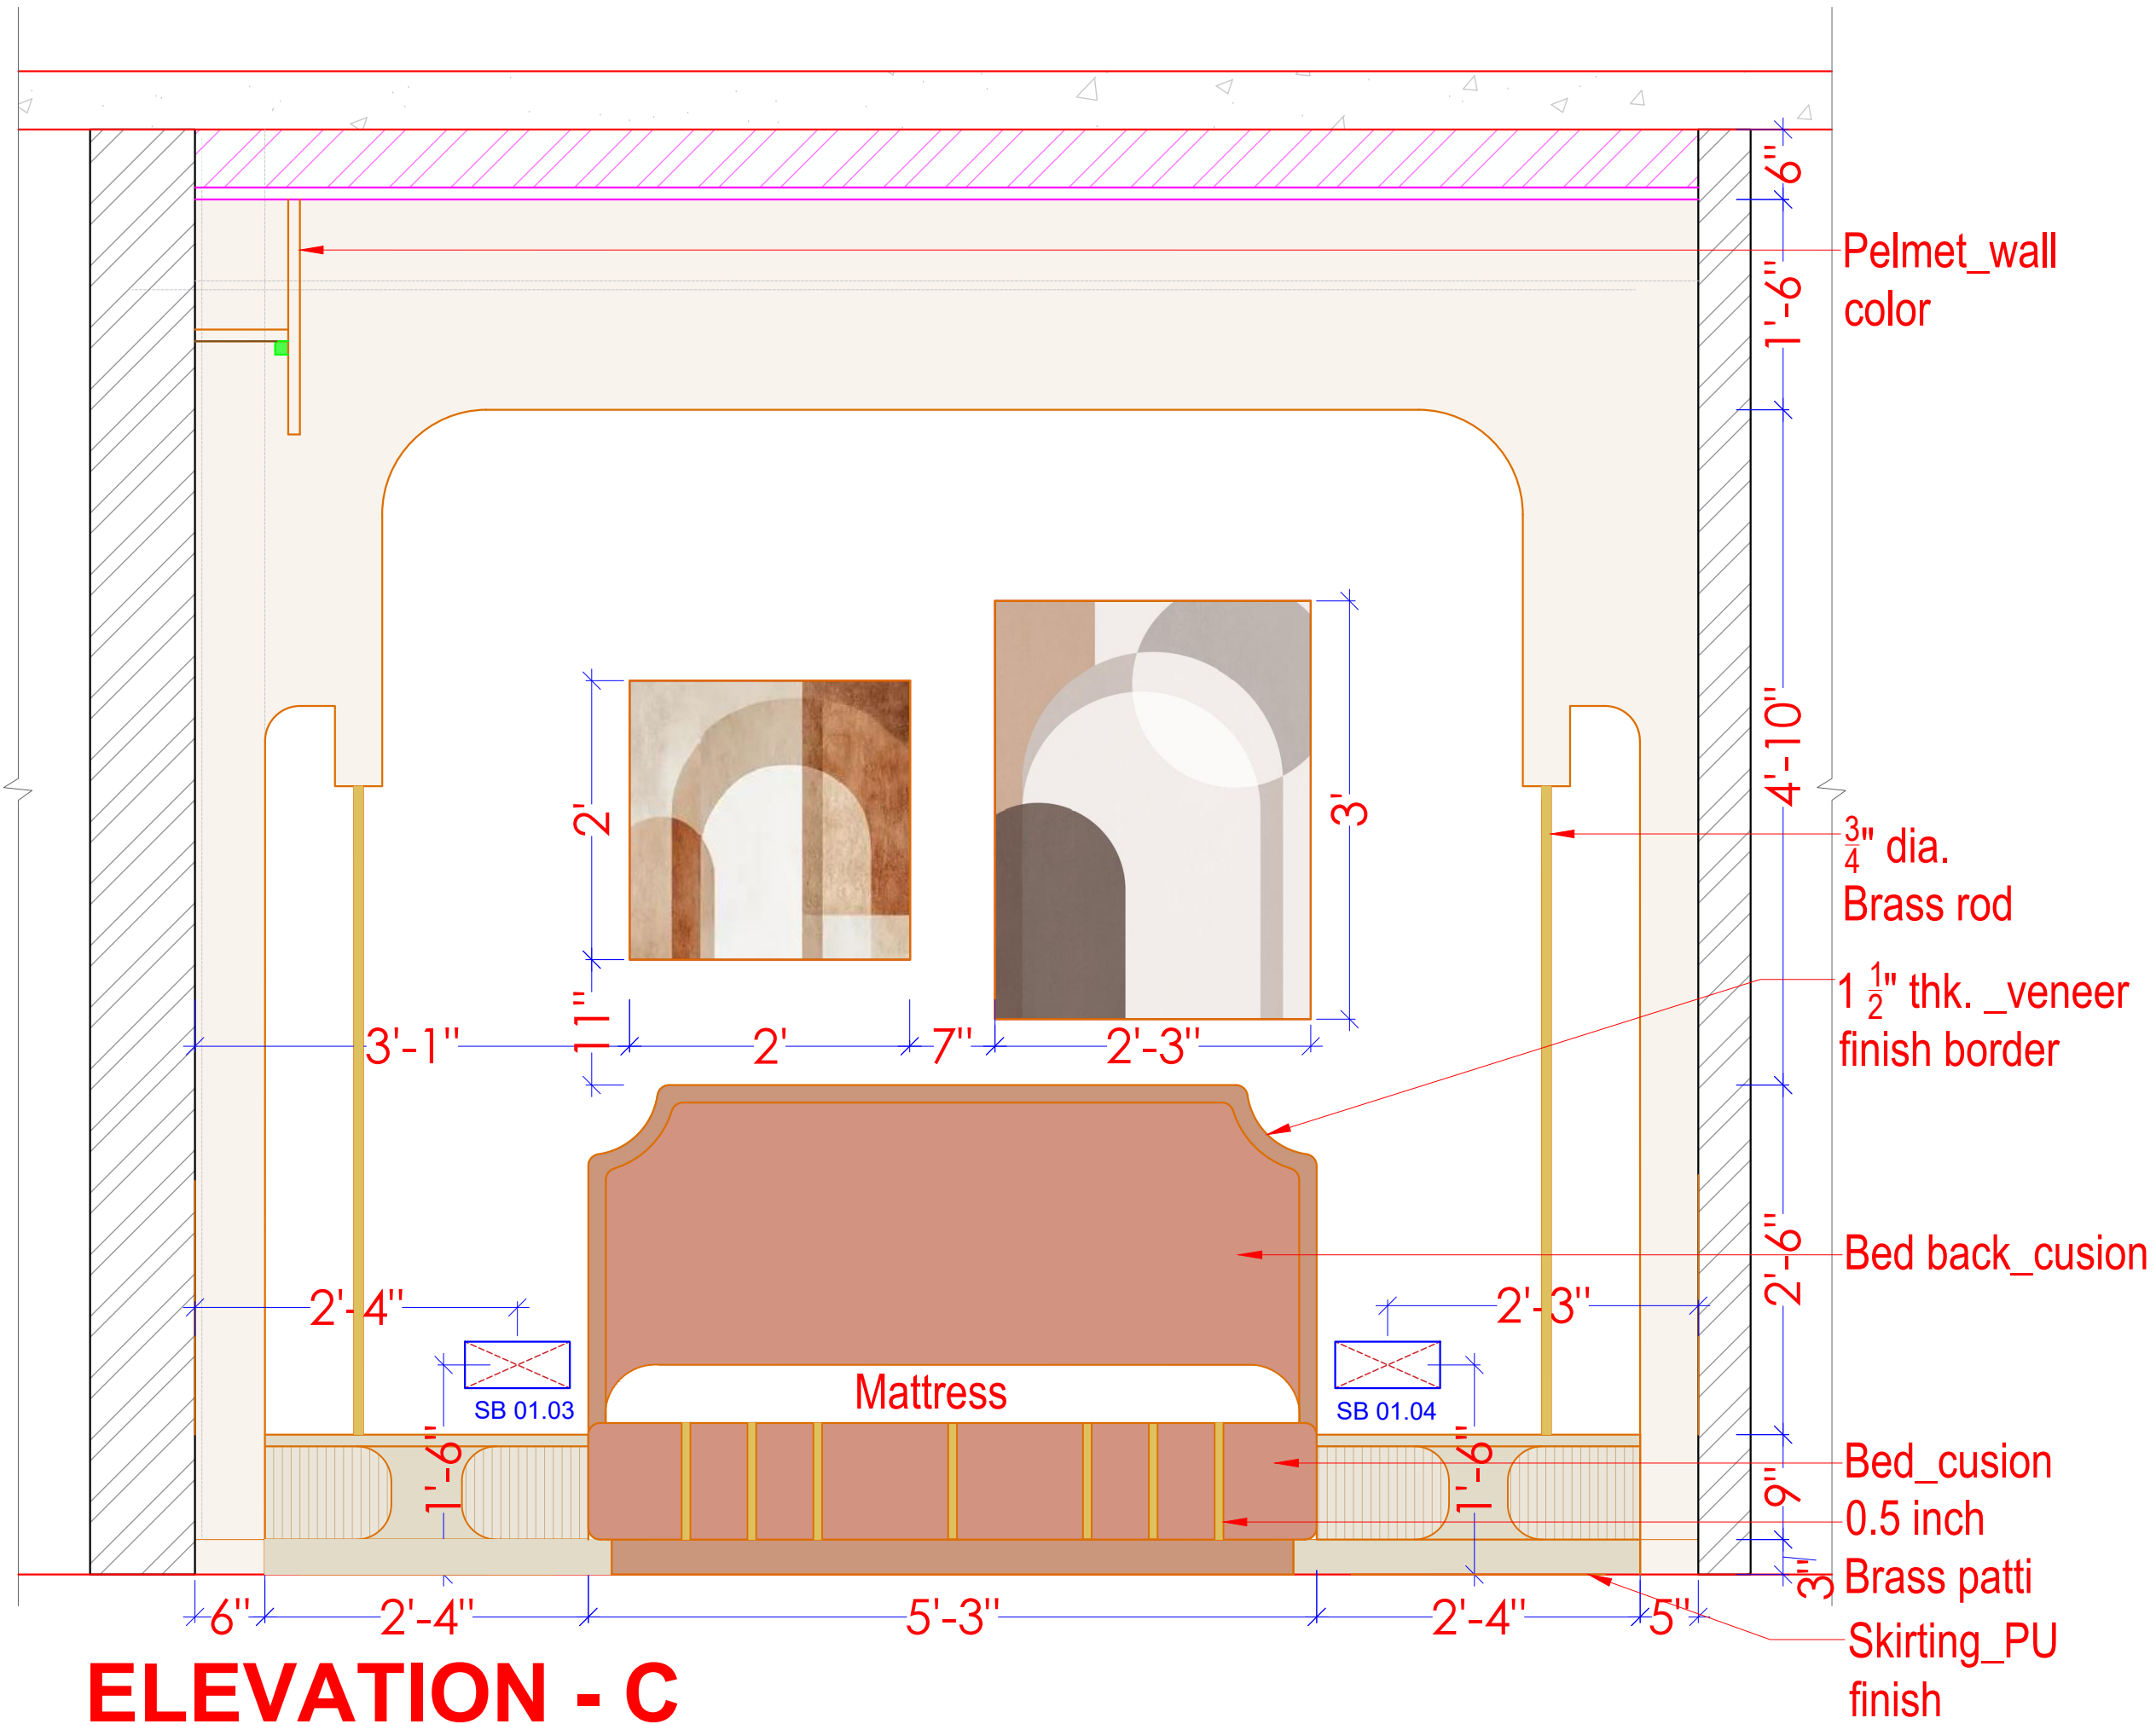

ELEVATION - C

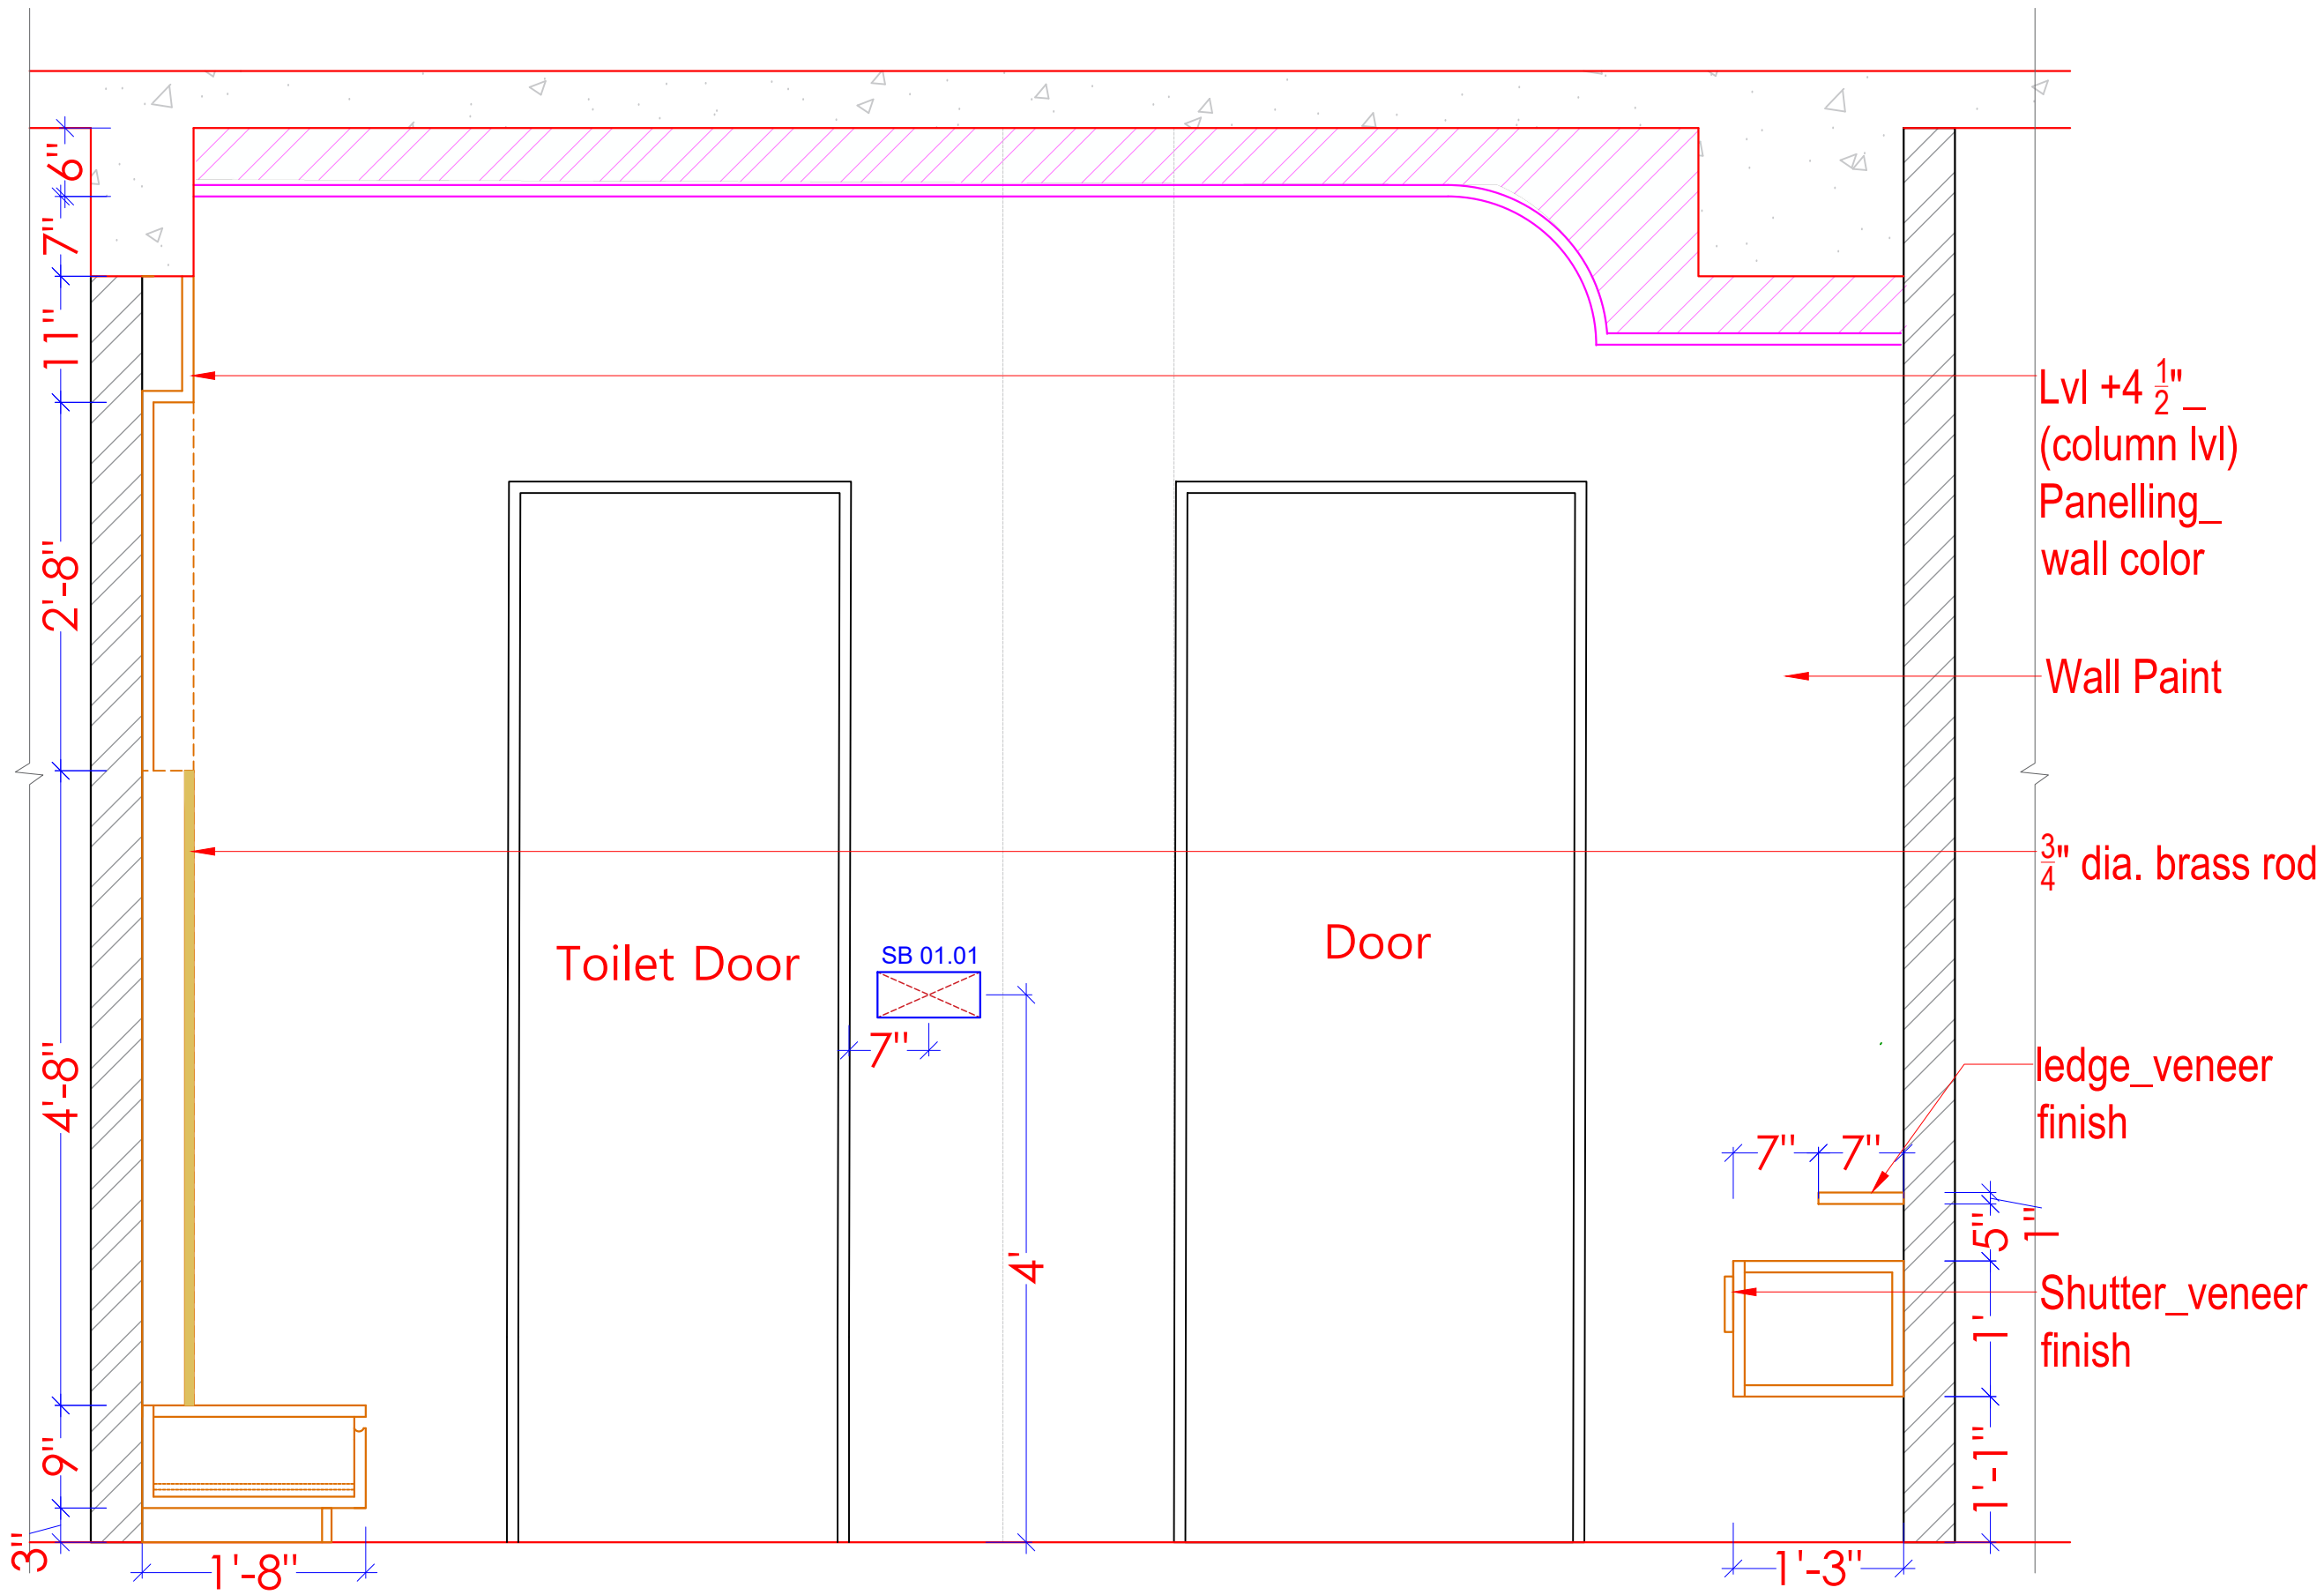

ELEVATION - D

DRAWING TITLE :

PARENTS BEDROOM
ELEVATION D

NOTES:

* DO NOT SCALE THE DRAWING.
* ALL DIMENSIONS ARE IN FEET \ INCHES.
* ANY DISCREPANCY IN THE DRAWING
TO BE BROUGHT IN THE DESIGNER'S
NOTICE BEFORE IMPLEMENTATION
ON SITE.

SITE ADDRESS:

SAVAD
VADODARA

CLIENT NAME:

RONAK PANCHOLI

DATE: 02-06-2025

NORTH:

DRAWING DETAIL

REVISION NO.	R1 R2 R3
REVISED DATE:	12/02/26
SCALE:	N.T.S
DRAWN BY:	ARCHANA
CHECKED BY:	MITTAL


www.mayaspace.studio

mayaspace.studio@gmail.com


+918980144077

@mayaspace.studio


Maya
SPACE STUDIO

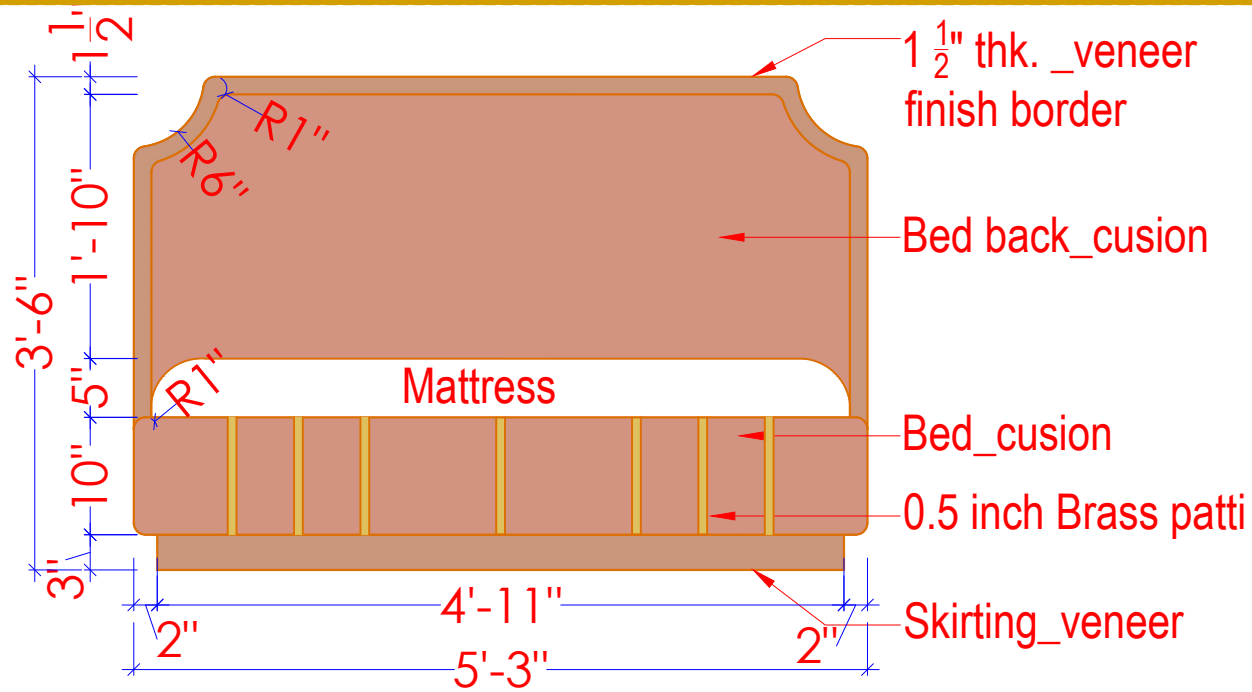


BED ELEVATION

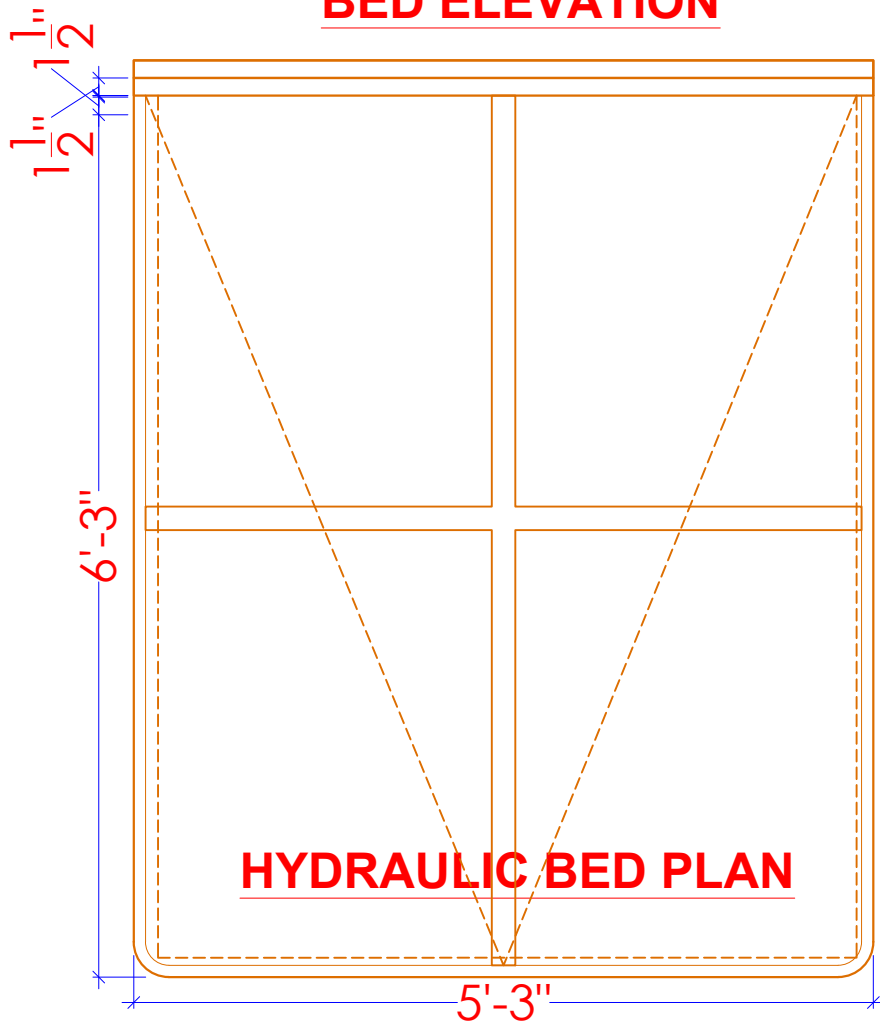


HYDRAULIC BED PLAN

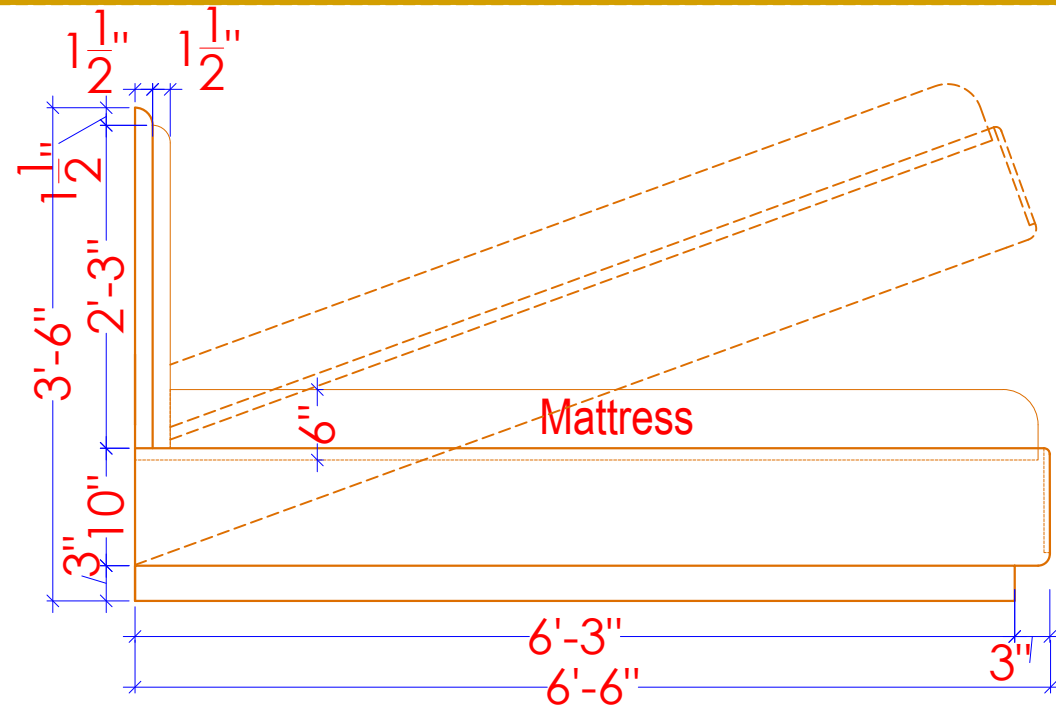


BED SIDE ELEVATION

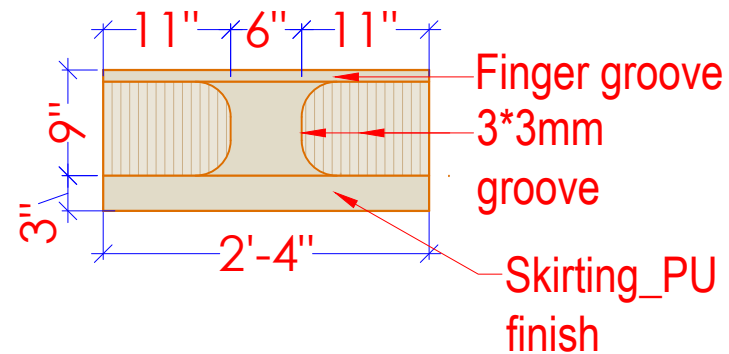


SIDE TABLE ELEVATION

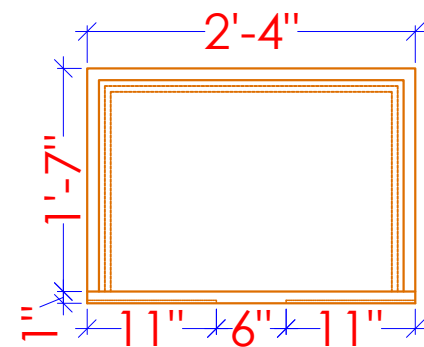

SIDE TABLE PLAN

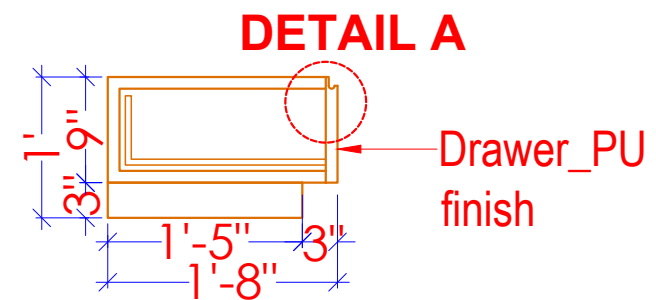

SIDE TABLE SECTION

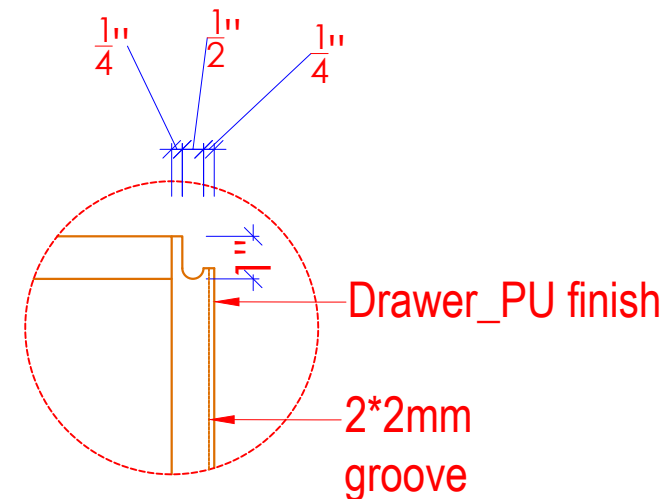

DETAIL A

**PARENTS BEDROOM
BED&SIDE TABLE DETAIL**

NOTES:

- * DO NOT SCALE THE DRAWING.
- * ALL DIMENSIONS ARE IN FEET \ INCHES.
- * ANY DISCREPENCY IN THE DRAWING TO BE BROUGHT IN THE DESIGNER'S NOTICE BEFORE IMPLEMENTATION ON SITE.

SITE ADDRESS:

SAVAD
VADODARA

CLIENT NAME:

RONAK PANCHOLI

DATE:

02-06-2025

NORTH:









DRAWING DETAIL

REVISION NO.	R1	R2	R3
REVISED DATE:	12/02/26		
SCALE:	N.T.S		
DRAWN BY:	ARCHANA		
CHECKED BY:	MITTAL		

	www.mayaspace.studio
	mayaspace.studio@gmail.com
	+918980144077
	@mayaspace.studio



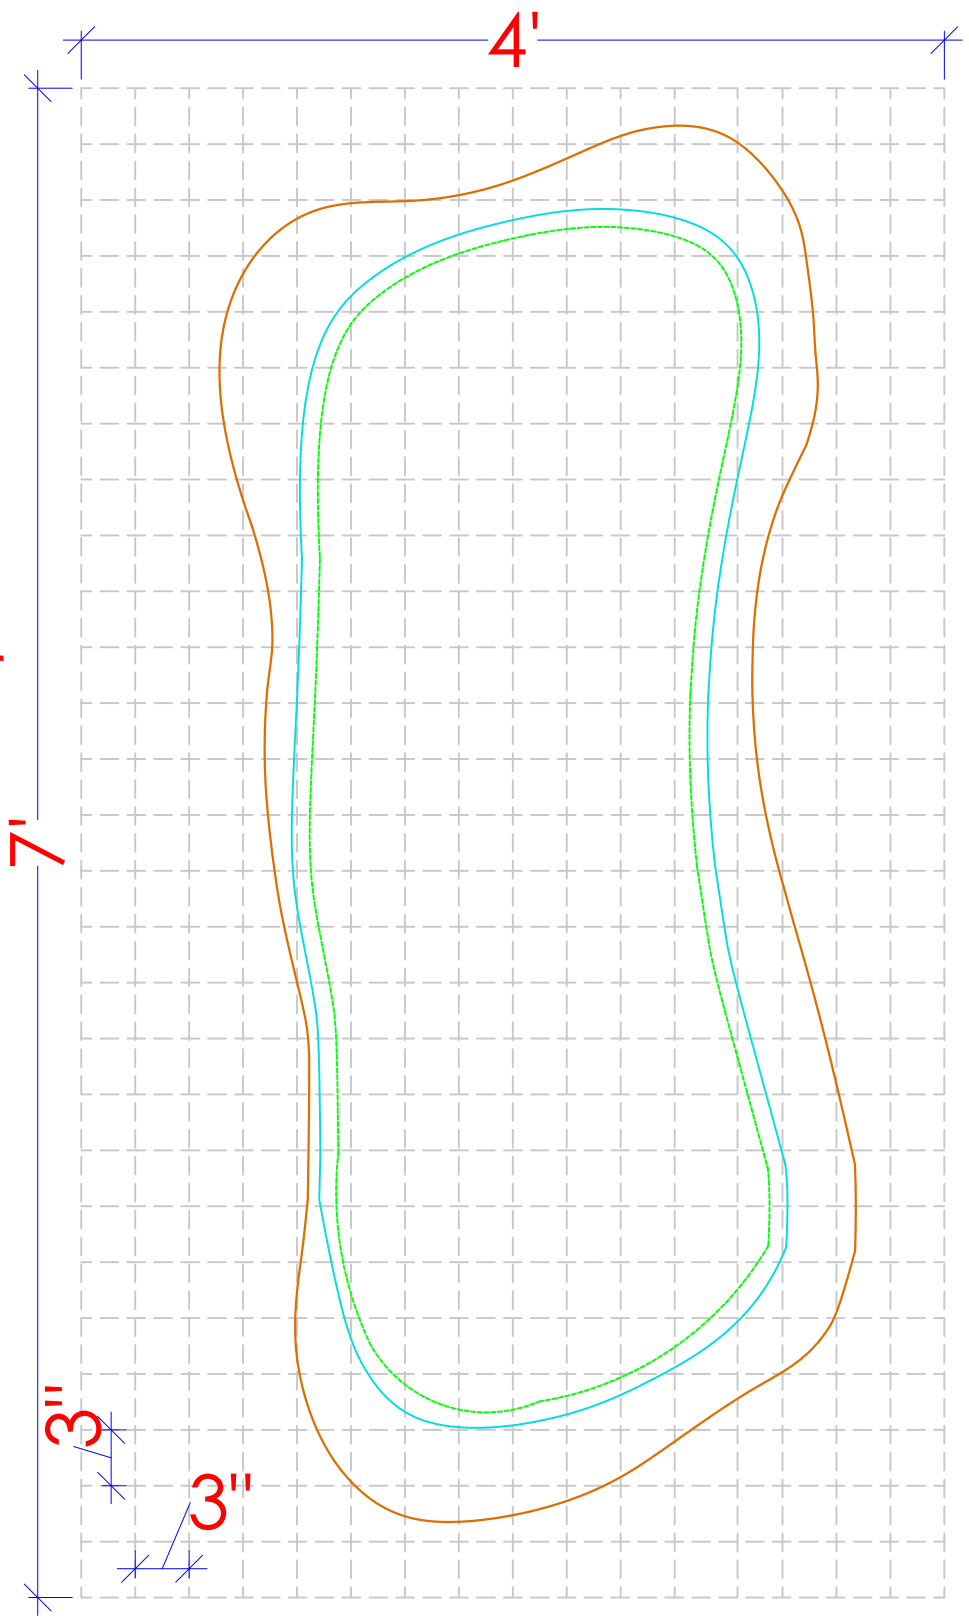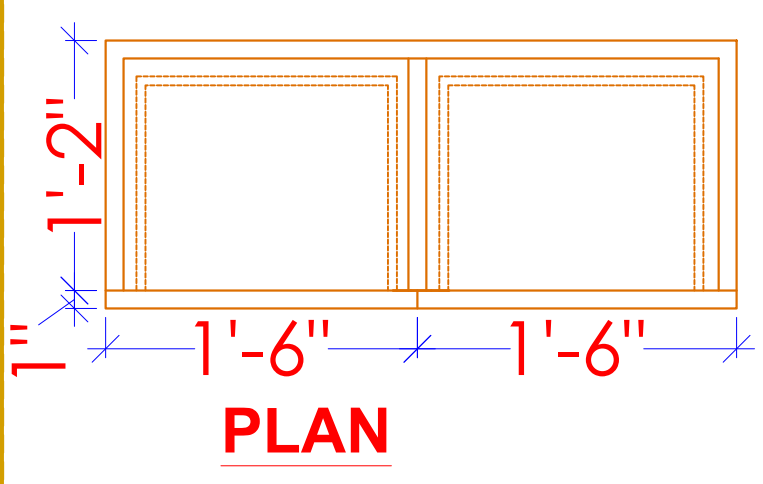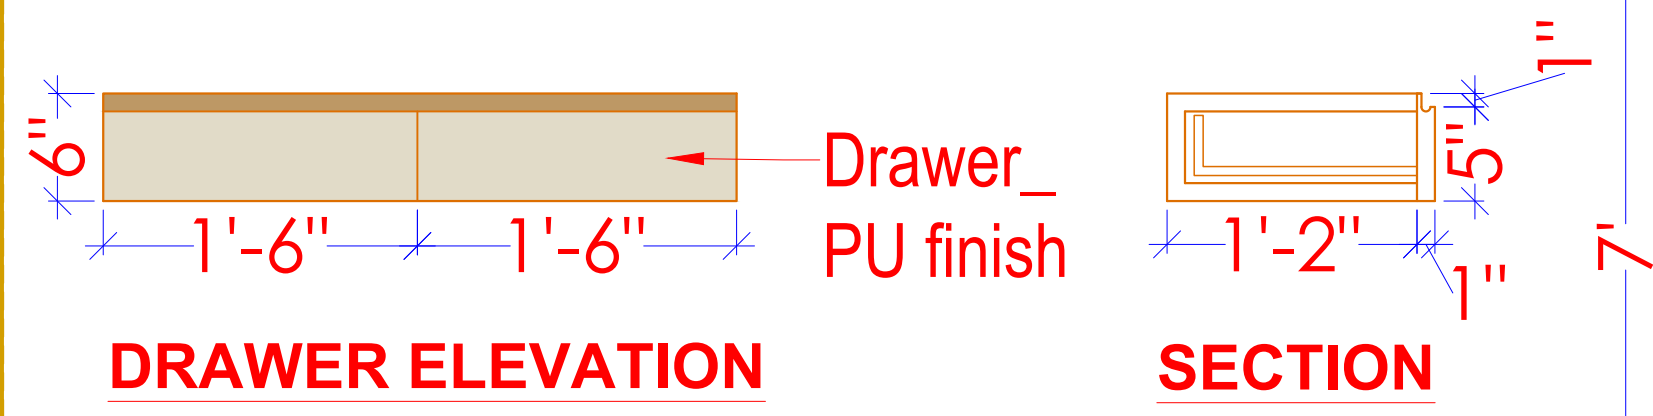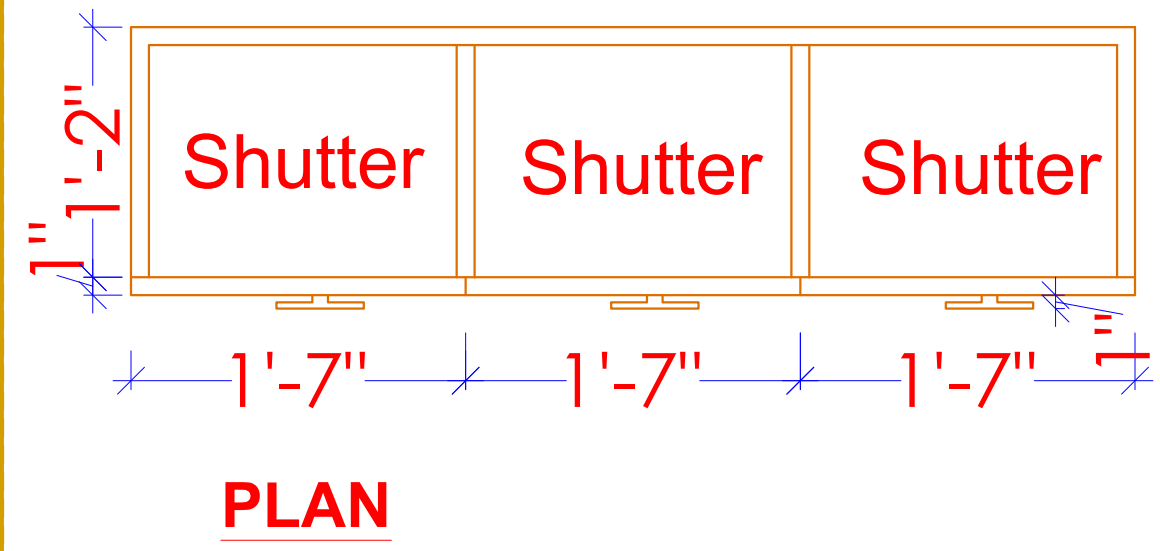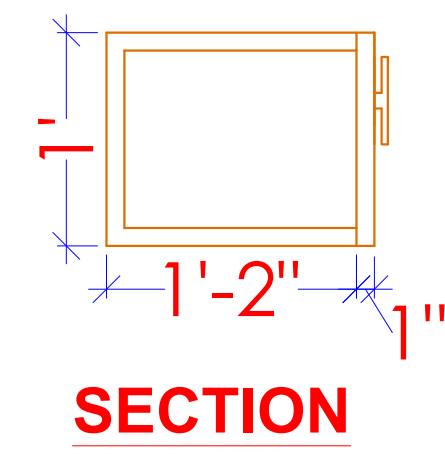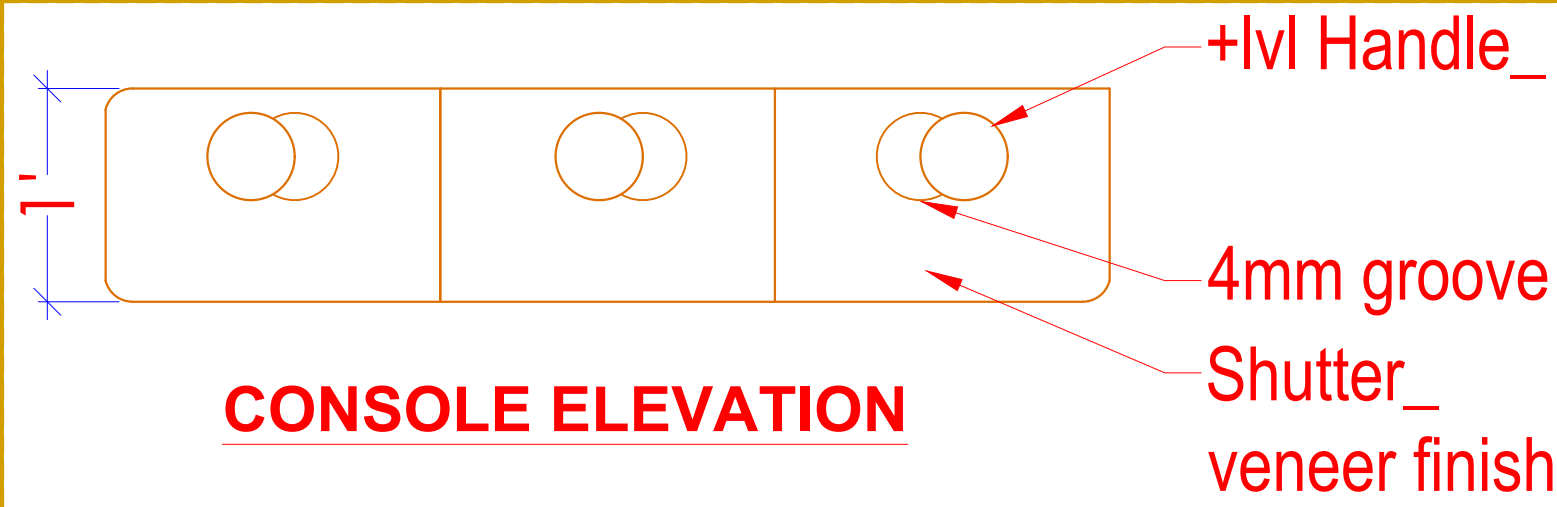

PARENTS BEDROOM
CONSOLE DESTAIL

NOTES:

- * DO NOT SCALE THE DRAWING.
- * ALL DIMENSIONS ARE IN FEET \ INCHES.
- * ANY DISCREPENCY IN THE DRAWING TO BE BROUGHT IN THE DESIGNER'S NOTICE BEFORE IMPLEMENTATION ON SITE.

SITE ADDRESS:

SAVAD
VADODARA

CLIENT NAME:

RONAK PANCHOLI

DATE:

02-06-2025

NORTH:

DRAWING DETAIL

REVISION NO.	R1	R2	R3
REVISED DATE:	12/02/26		
SCALE:	N.T.S		
DRAWN BY:	ARCHANA		
CHECKED BY:	MITTAL		


www.mayaspace.studio

mayaspace.studio@gmail.com

+918980144077

@mayaspace.studio



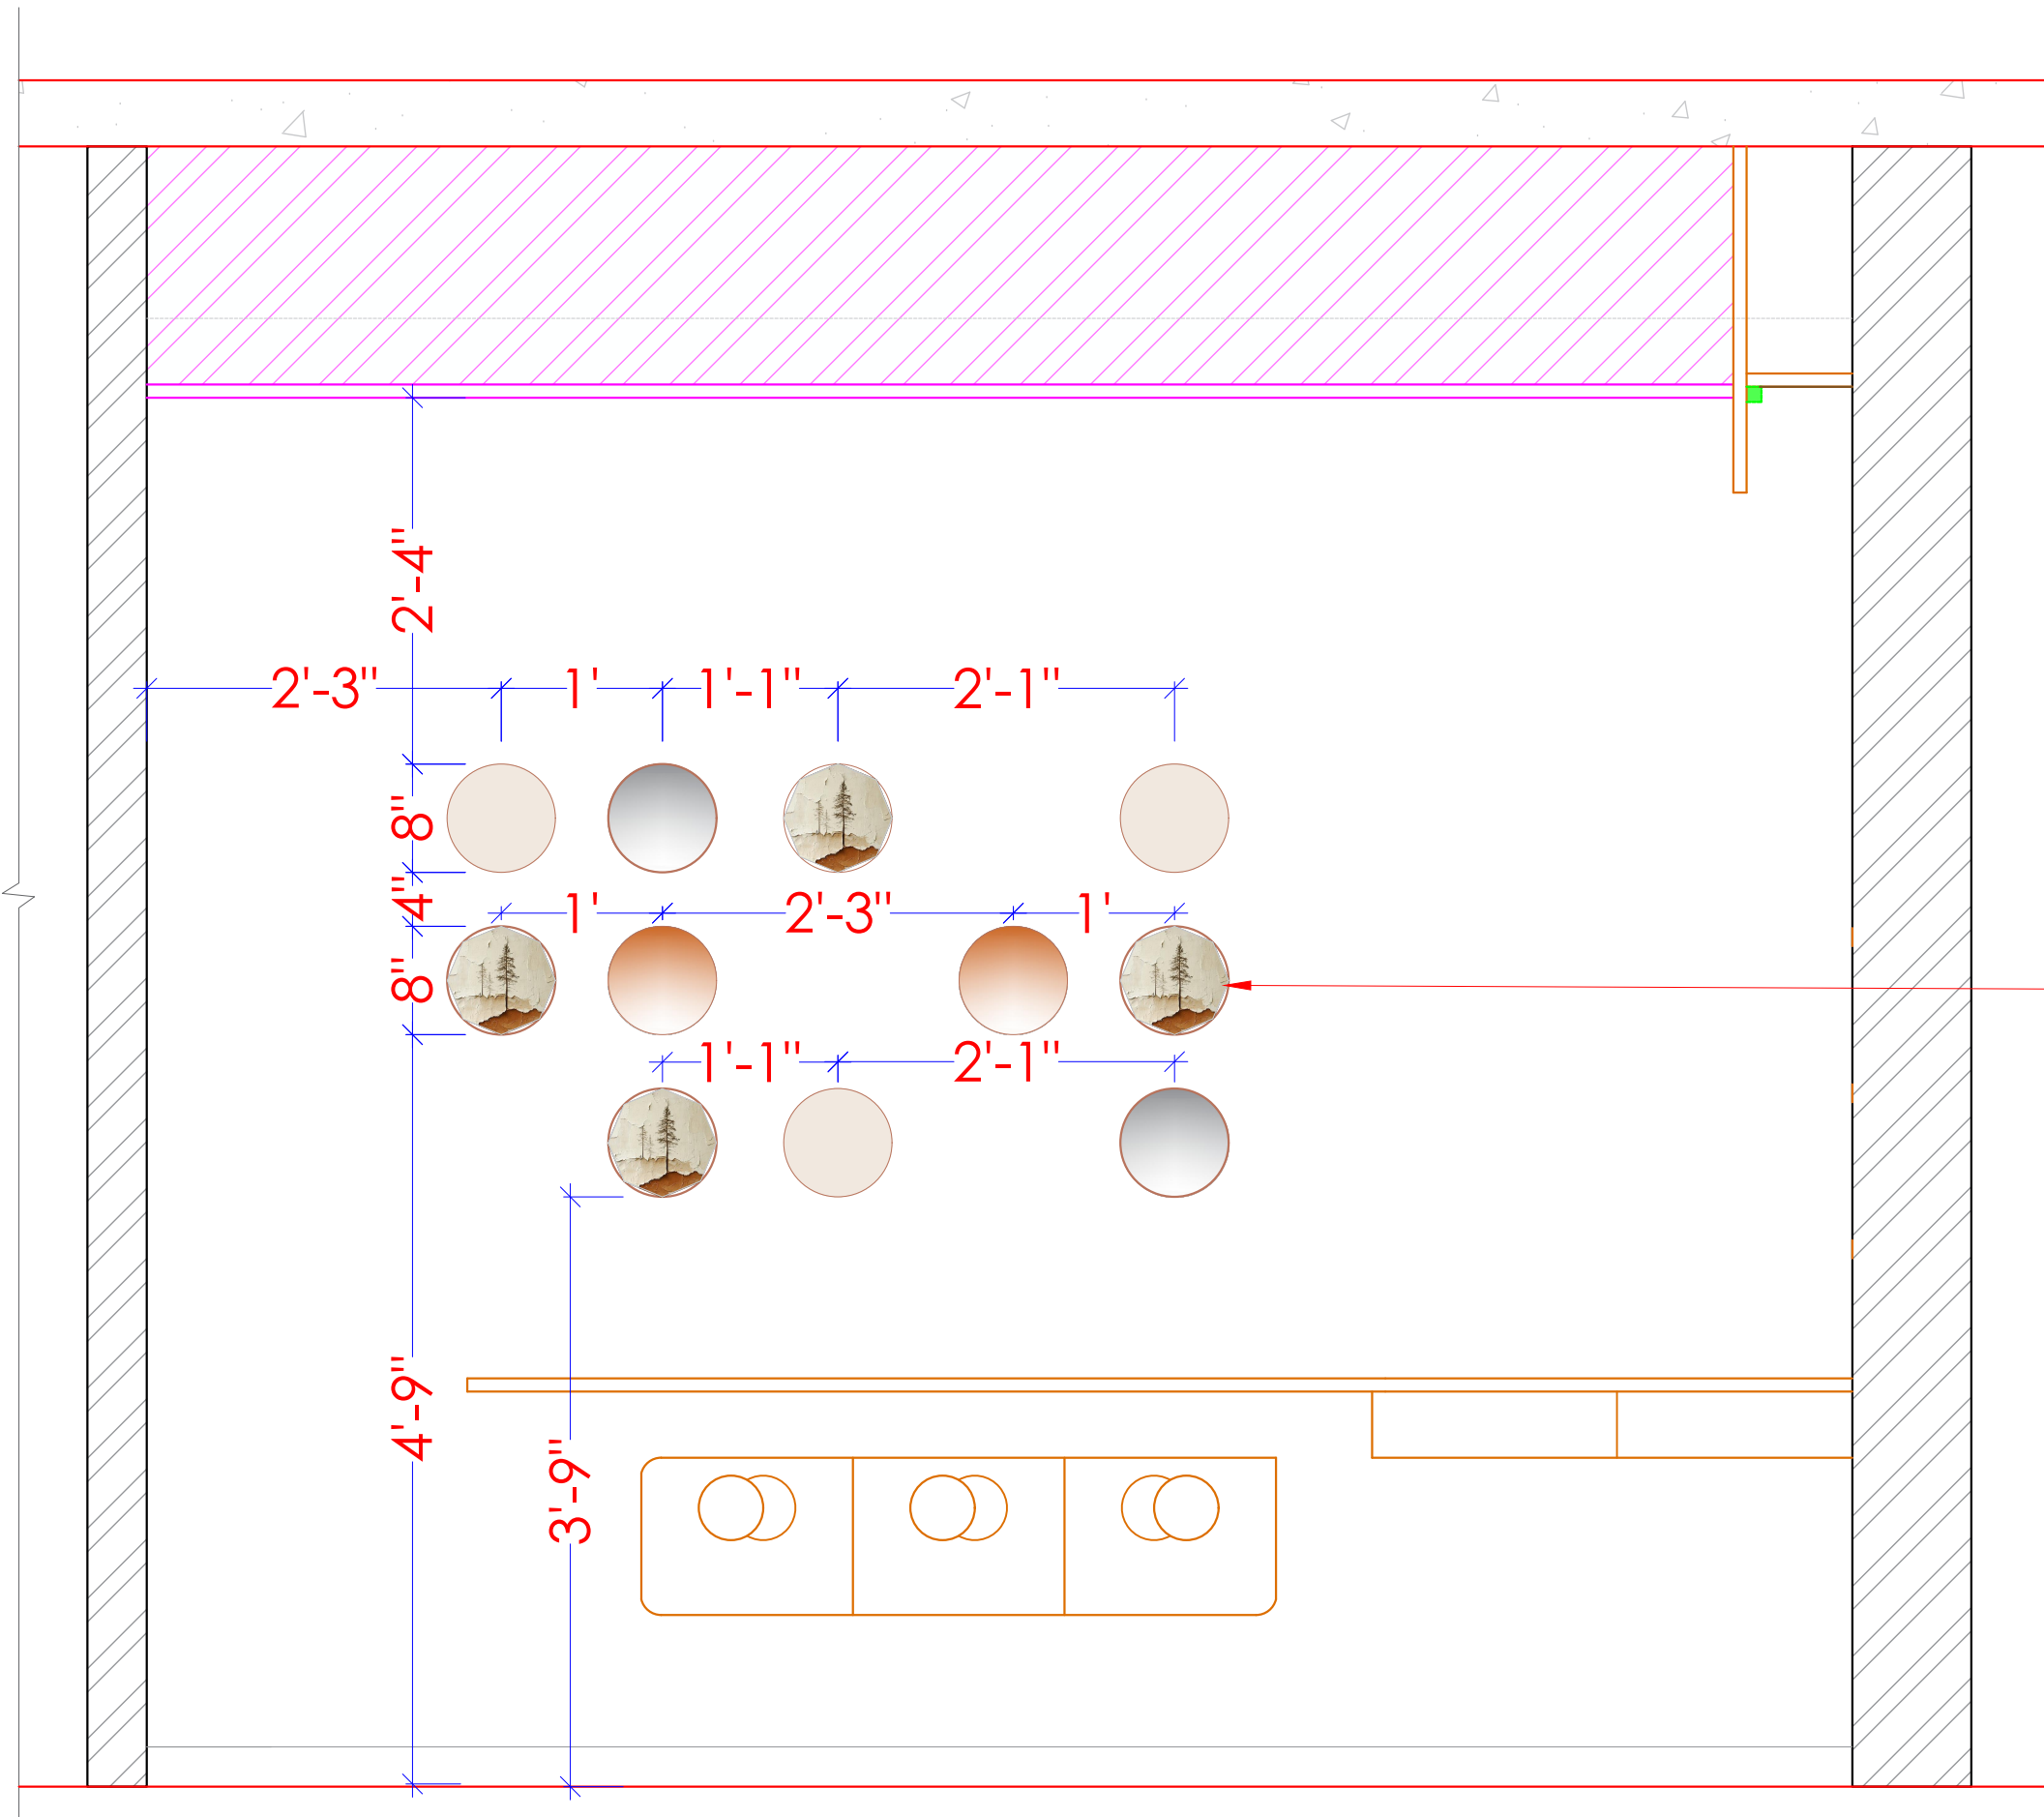

DRAWING TITLE :

PARENTS BEDROOM ARTIFACT WALL

NOTES:

- * DO NOT SCALE THE DRAWING.
- * ALL DIMENSIONS ARE IN FEET \ INCHES.
- * ANY DISCREPENCY IN THE DRAWING TO BE BROUGHT IN THE DESIGNER'S NOTICE BEFORE IMPLEMENTATION ON SITE.

SITE ADDRESS:

SAVAD
VADODARA

CLIENT NAME:

RONAK PANCHOLI

DATE:

02-06-2025


NORTH:

DRAWING DETAIL


REVISION NO.	R1	R2	R3
REVISED DATE:	12/02/26		
SCALE:	N.T.S		
DRAWN BY:	ARCHANA		
CHECKED BY:	MITTAL		

	www.mayaspace.studio
	mayaspace.studio@gmail.com
	+918980144077
	@mayaspace.studio



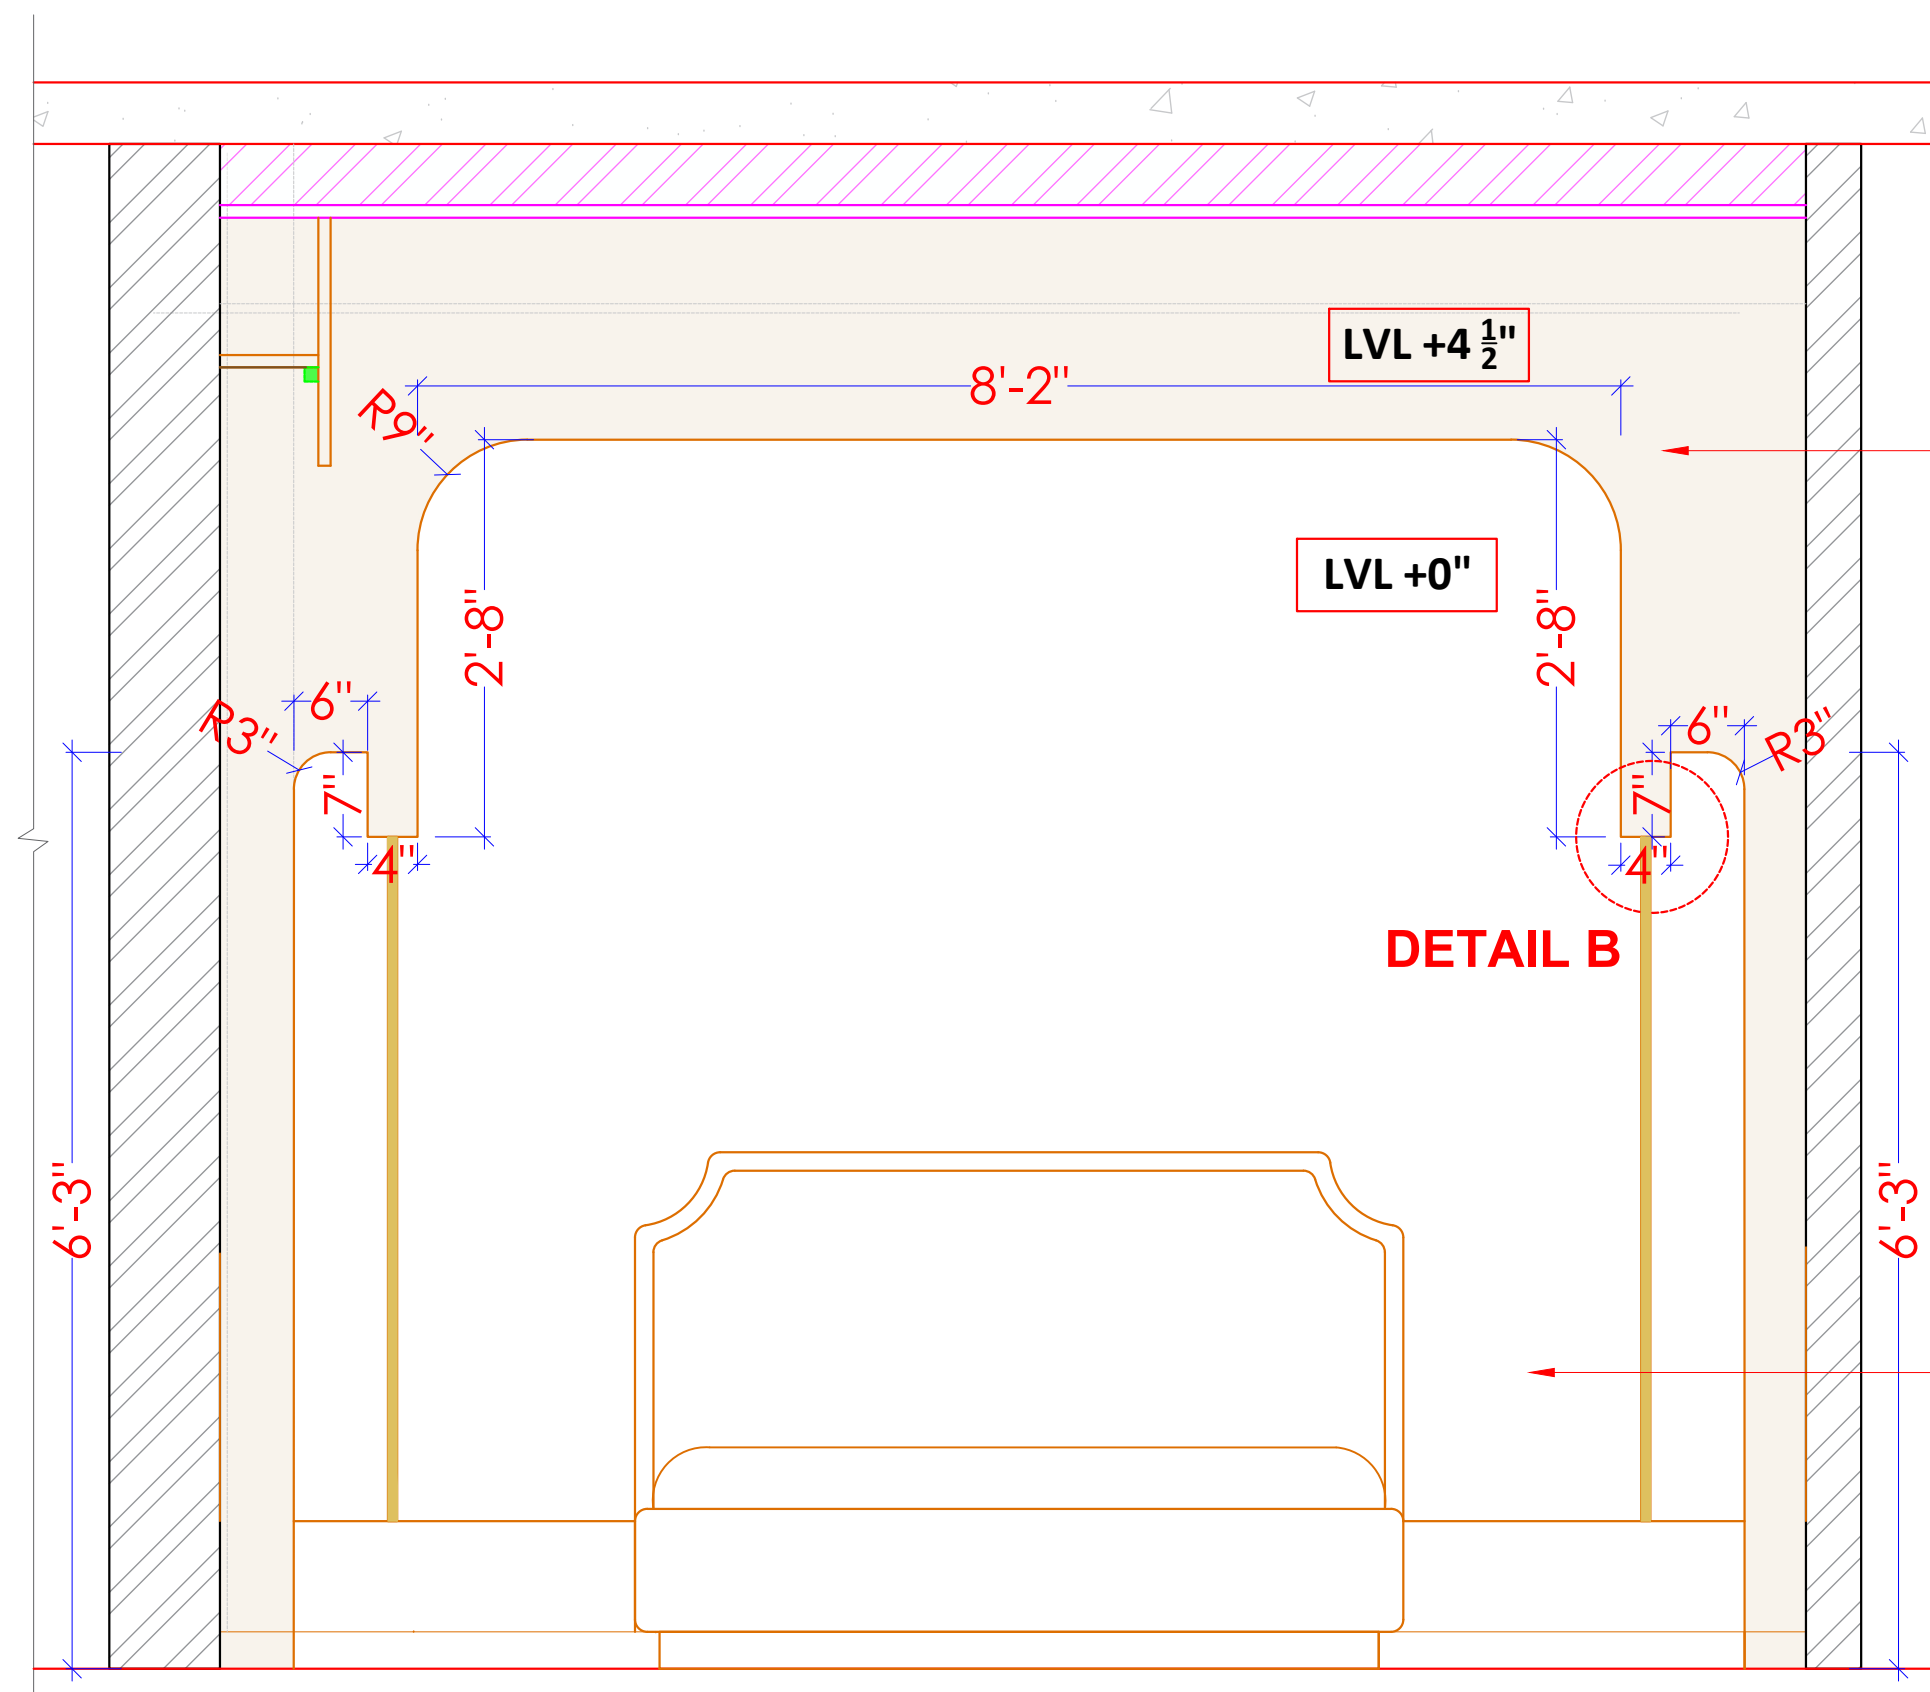

Lvl+4 1/2 inch
Panelling_
paint finish

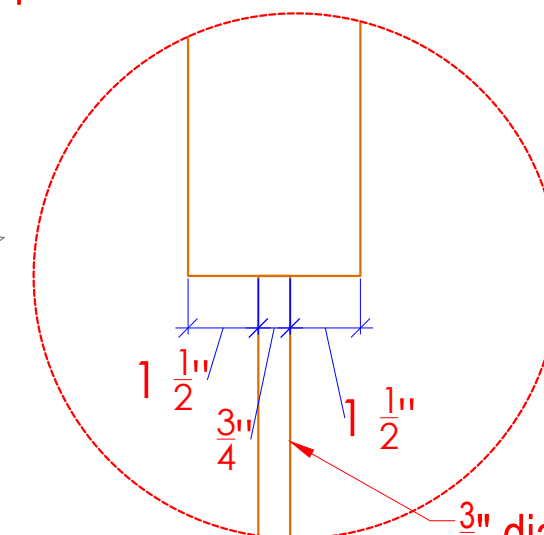

DETAIL B 3/4 inch dia. Brass rod

Texture_
as per
selection

DRAWING TITLE :

PARENTS BEDROOM
PANELLING DETAIL

NOTES:

- * DO NOT SCALE THE DRAWING.
- * ALL DIMENSIONS ARE IN FEET \ INCHES.
- * ANY DISCREPANCY IN THE DRAWING TO BE BROUGHT IN THE DESIGNER'S NOTICE BEFORE IMPLEMENTATION ON SITE.

SITE ADDRESS:

SAVAD
VADODARA

CLIENT NAME:

RONAK PANCHOLI

DATE:

02-06-2025

NORTH:


DRAWING DETAIL

REVISION NO.	R1	R2	R3
REVISED DATE:	12/02/26		
SCALE:	N.T.S		
DRAWN BY:	ARCHANA		
CHECKED BY:	MITTAL		


	www.mayaspace.studio
	mayaspace.studio@gmail.com
	+918980144077
	@mayaspace.studio




PANELLING DETAIL

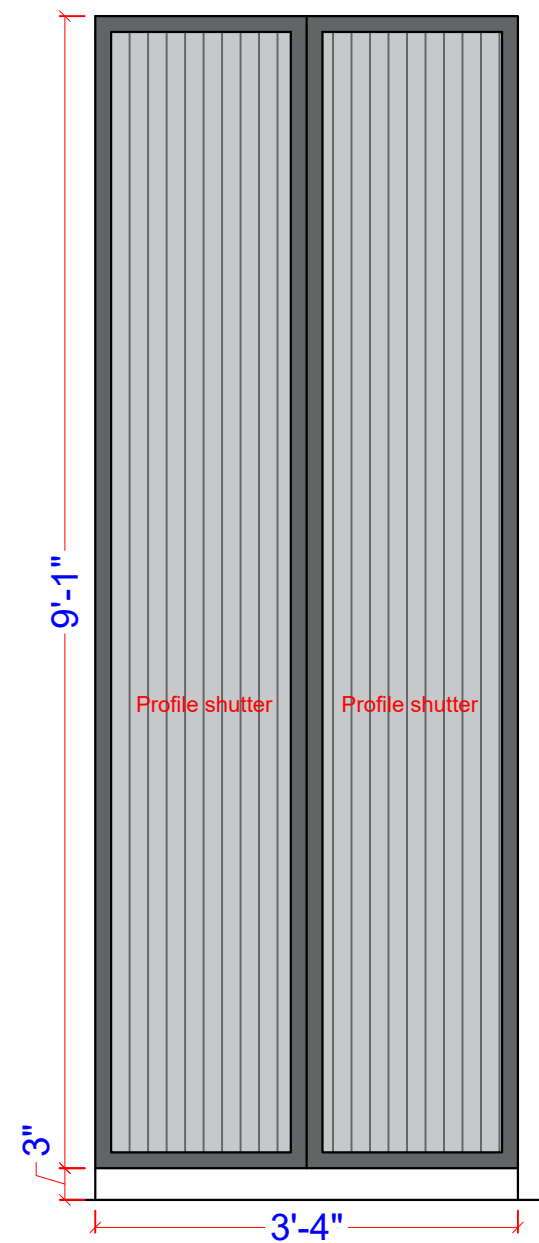


HIS AND HER EXTERNAL WARDROBE

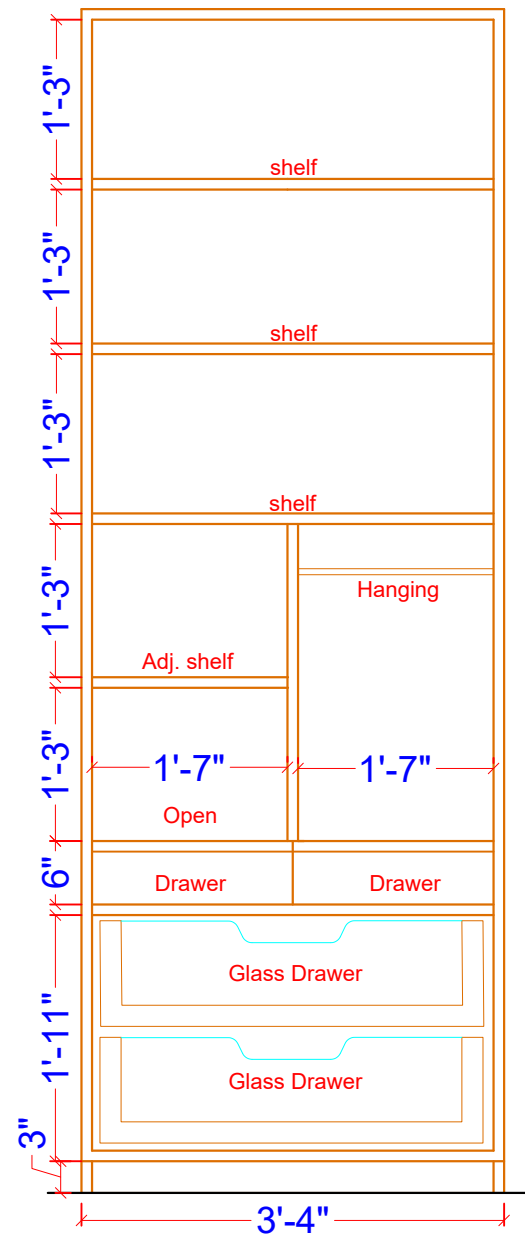


HER WARDROBE INTERNAL DETAIL

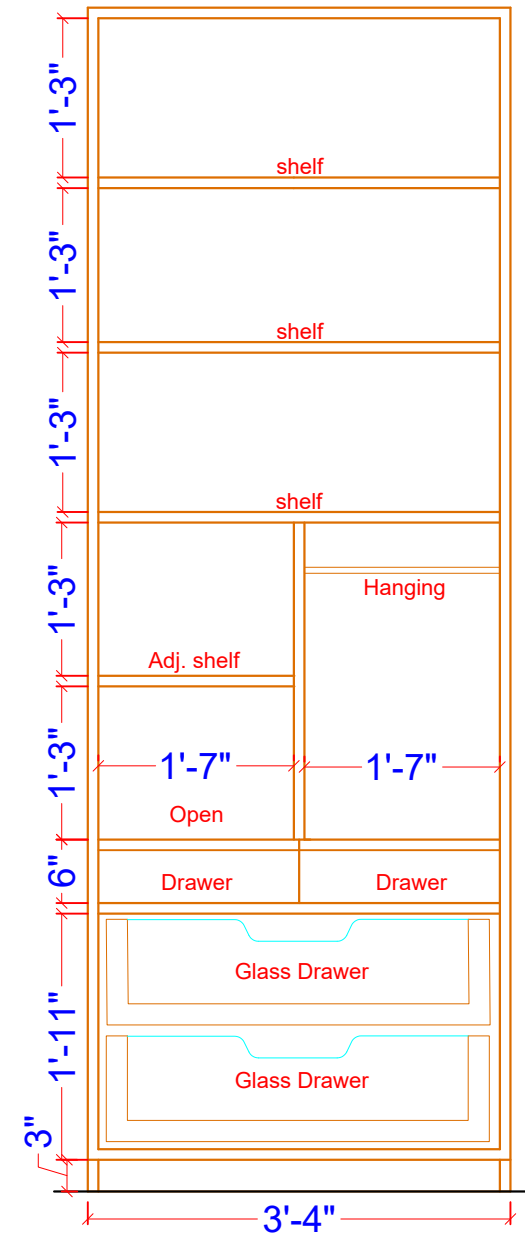

HIS WARDROBE INTERNAL DETAIL

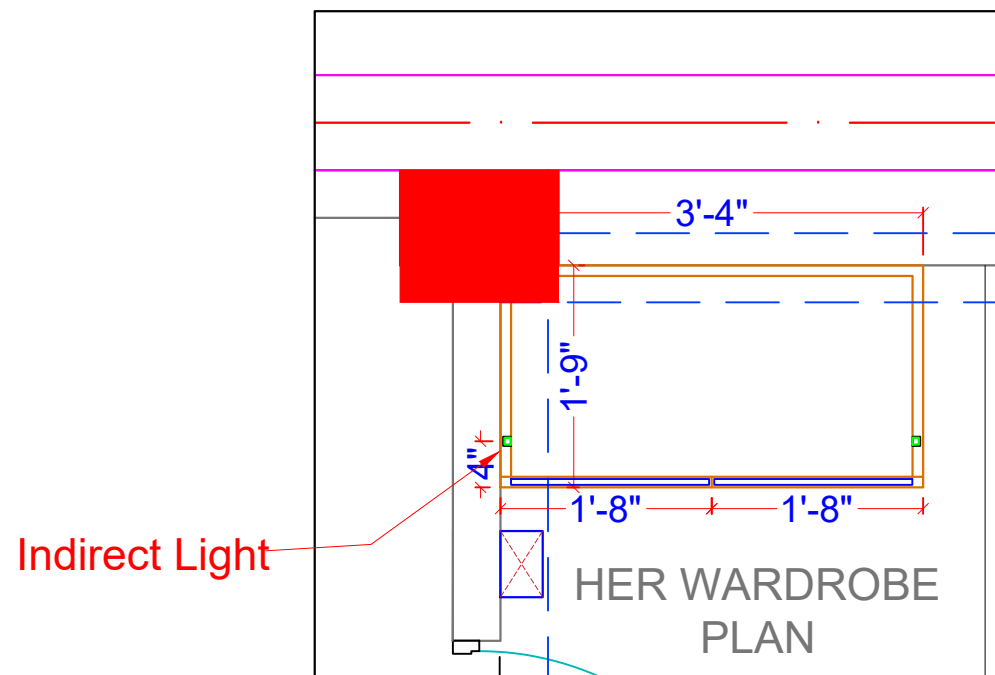

HER WARDROBE PLAN

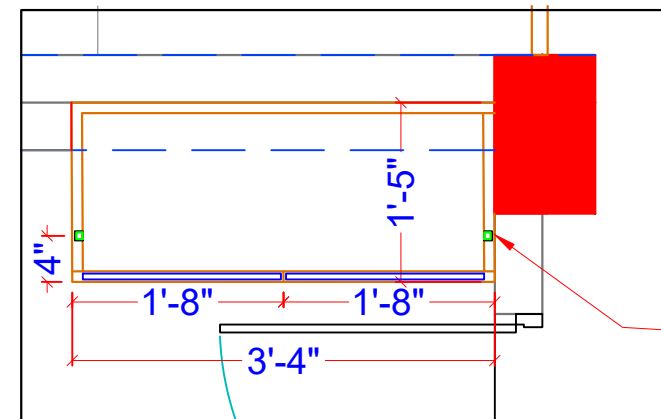

HIS WARDROBE PLAN

NOTES:

- * DO NOT SCALE THE DRAWING.
- * ALL DIMENSIONS ARE IN FEET \ INCHES.
- * ANY DISCREPANCY IN THE DRAWING TO BE BROUGHT IN THE DESIGNER'S NOTICE BEFORE IMPLEMENTATION ON SITE.

DRAWING TITLE :

PARENTS WALKING WARDROBE

SITE ADDRESS:

SAVAD
VADODARA

CLIENT NAME:

RONAK PANCHOLI

DATE:

02-06-2025

NORTH:

DRAWING DETAIL

REVISION NO.	R1 R2 R3
REVISED DATE:	11-02-2026
SCALE:	N.T.S
DRAWN BY:	ARCHANA
CHECKED BY:	MITTAL

	www.mayaspace.studio
	mayaspace.studio@gmail.com
	+918980144077
	@mayaspace.studio

