


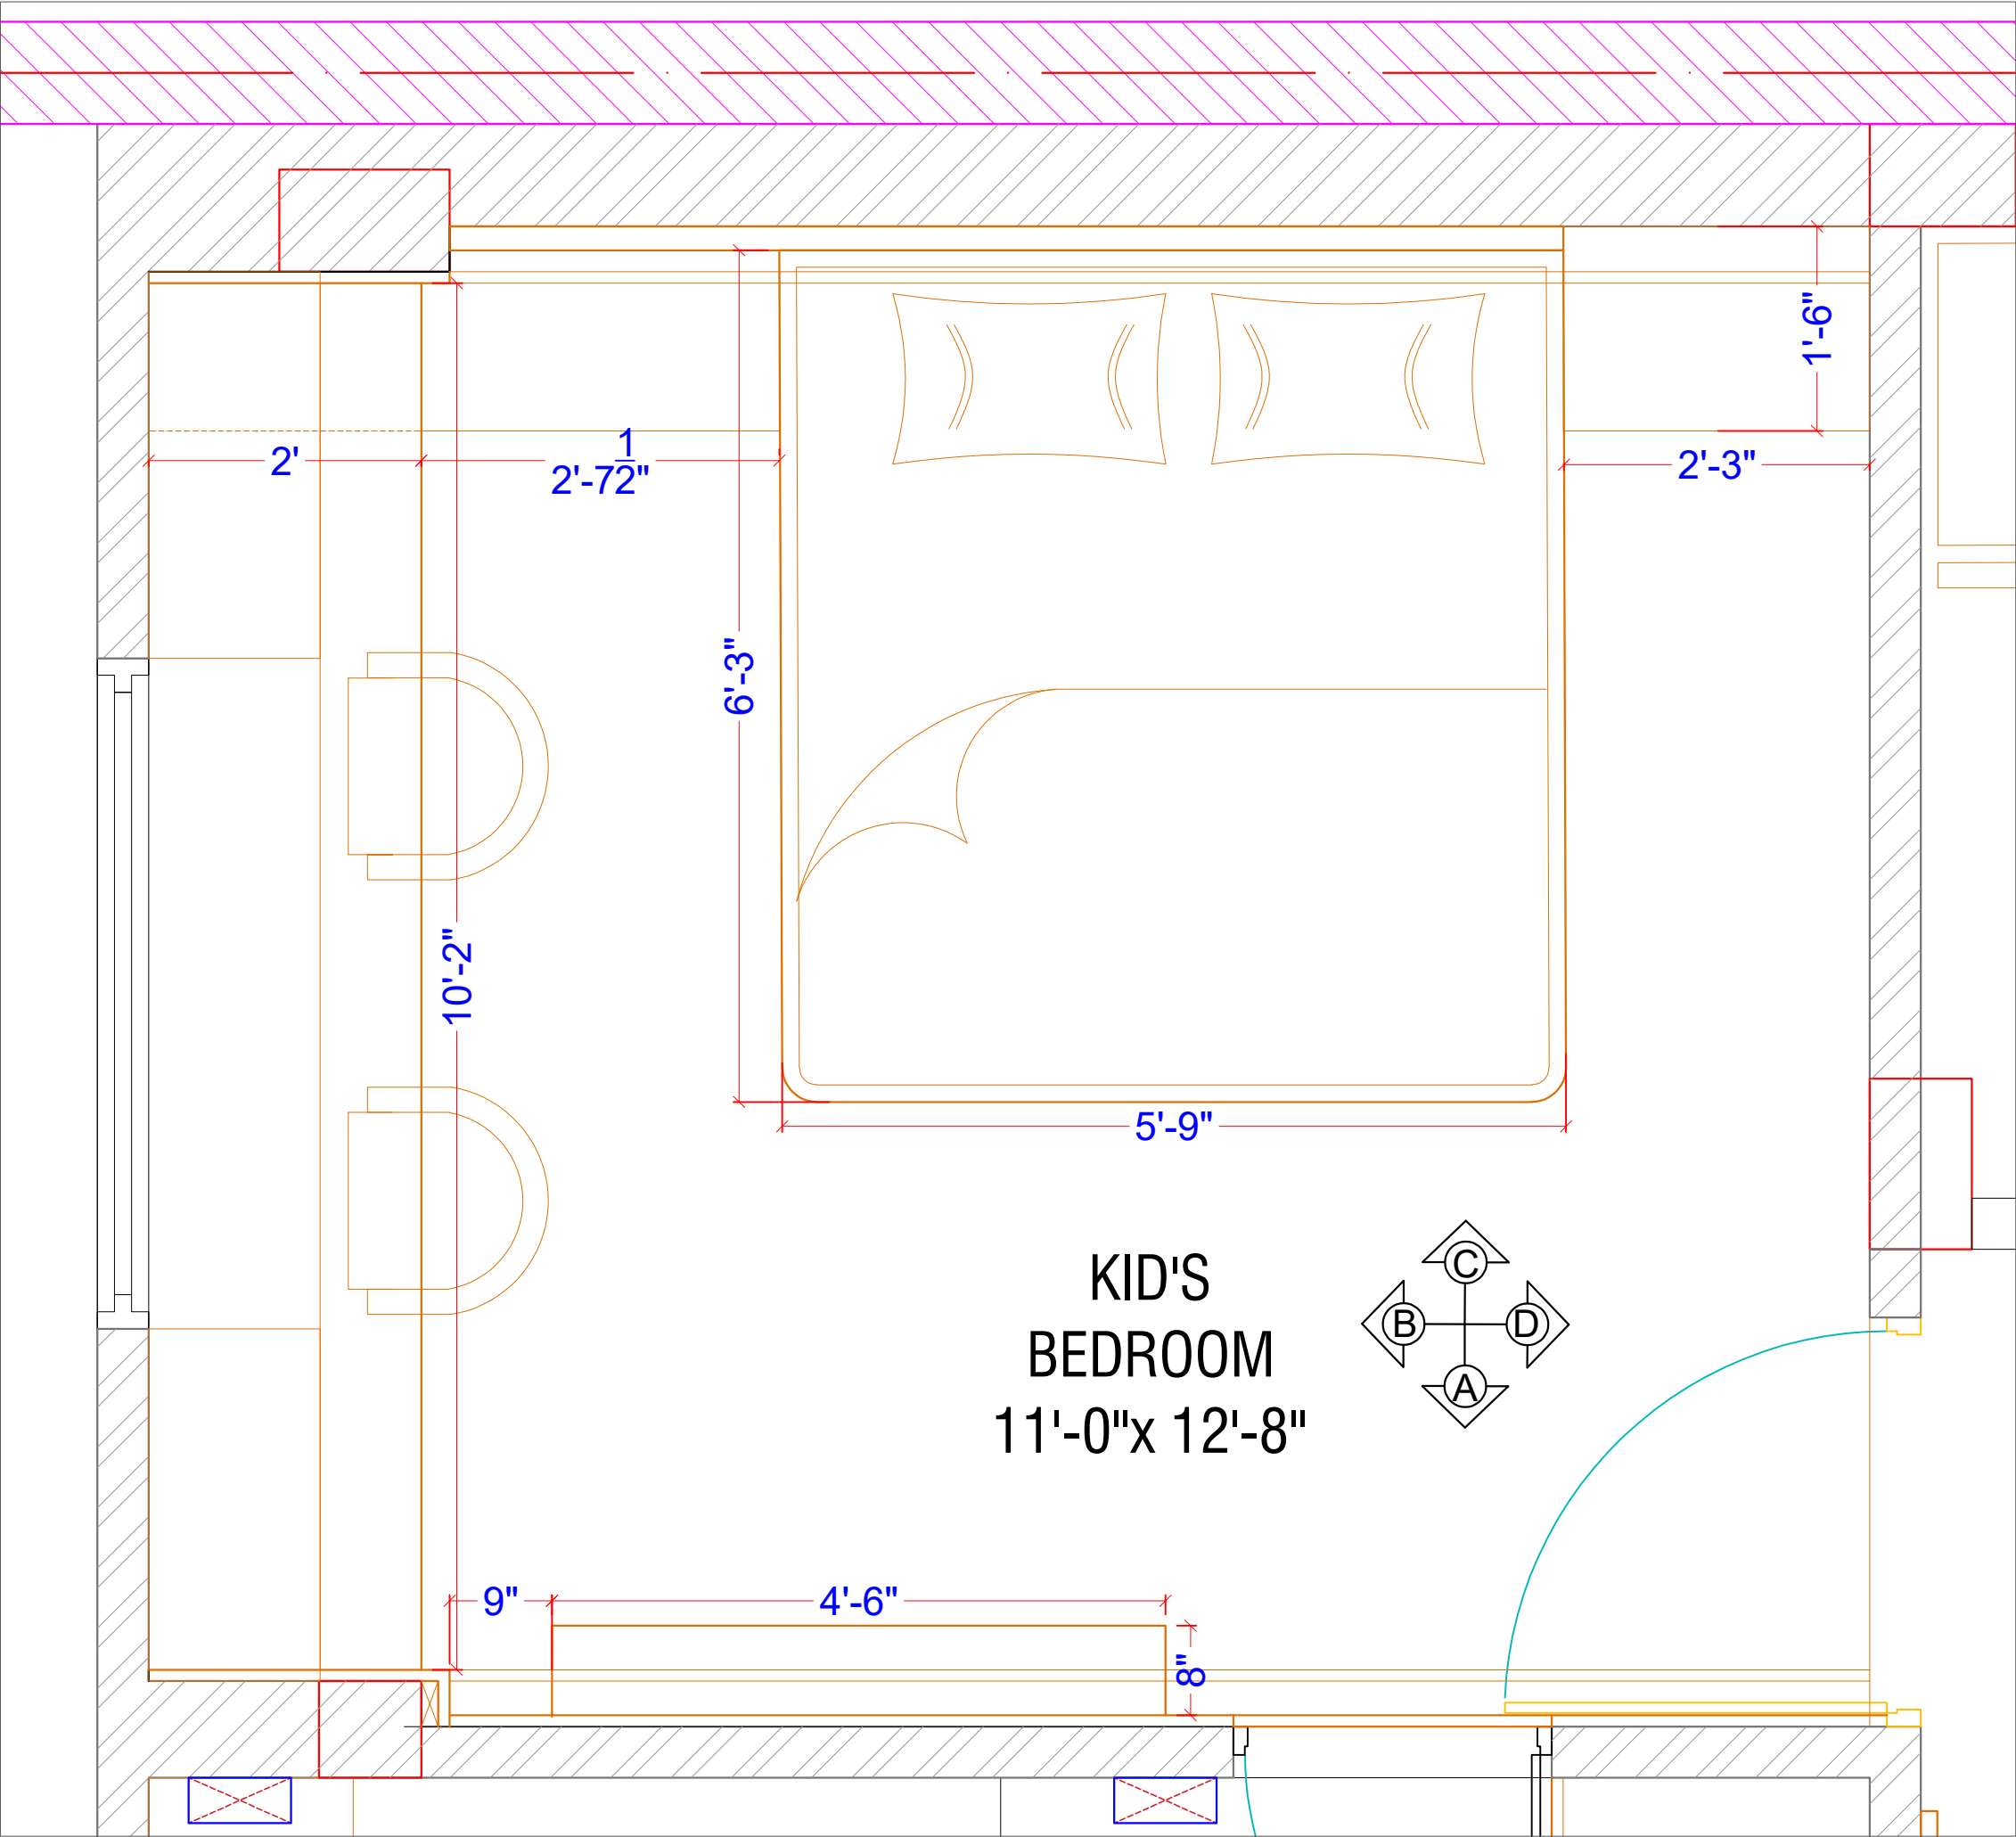

DRAWING TITLE :

KID'S BEDROOM
FURNITURE LAYOUT

NOTES:

- * DO NOT SCALE THE DRAWING.
- * ALL DIMENSIONS ARE IN FEET \ INCHES.
- * ANY DISCREPENCY IN THE DRAWING TO BE BROUGHT IN THE DESIGNER'S NOTICE BEFORE IMPLEMENTATION ON SITE.

SITE ADDRESS:

Vadodara

CLIENT NAME:

PANCHOLI'S

DATE:

06-06-2024

NORTH:

DRAWING DETAIL

REVISION NO.	R1	R2	R3
REVISED DATE:	05/03/26		
SCALE:	N.T.S		
DRAWN BY:	PRASANNA		
CHECKED BY:	MITTAL		

	www.mayaspace.studio
	mayaspace.studio@gmail.com
	+918980144077
	@mayaspace.studio



KID'S BEDROOM WALL ELEVATION

- * DO NOT SCALE THE DRAWING.
- * ALL DIMENSIONS ARE IN FEET \ INCHES.
- * ANY DISCREPANCY IN THE DRAWING TO BE BROUGHT IN THE DESIGNER'S NOTICE BEFORE IMPLEMENTATION ON SITE.

Vadodara

PANCHOLI'S

06-06-2024

DRAWING DETAIL

R1 R2 R3


05/03/26


N.T.S

PRASANNA

MITTAL

 @mayaspace.studio

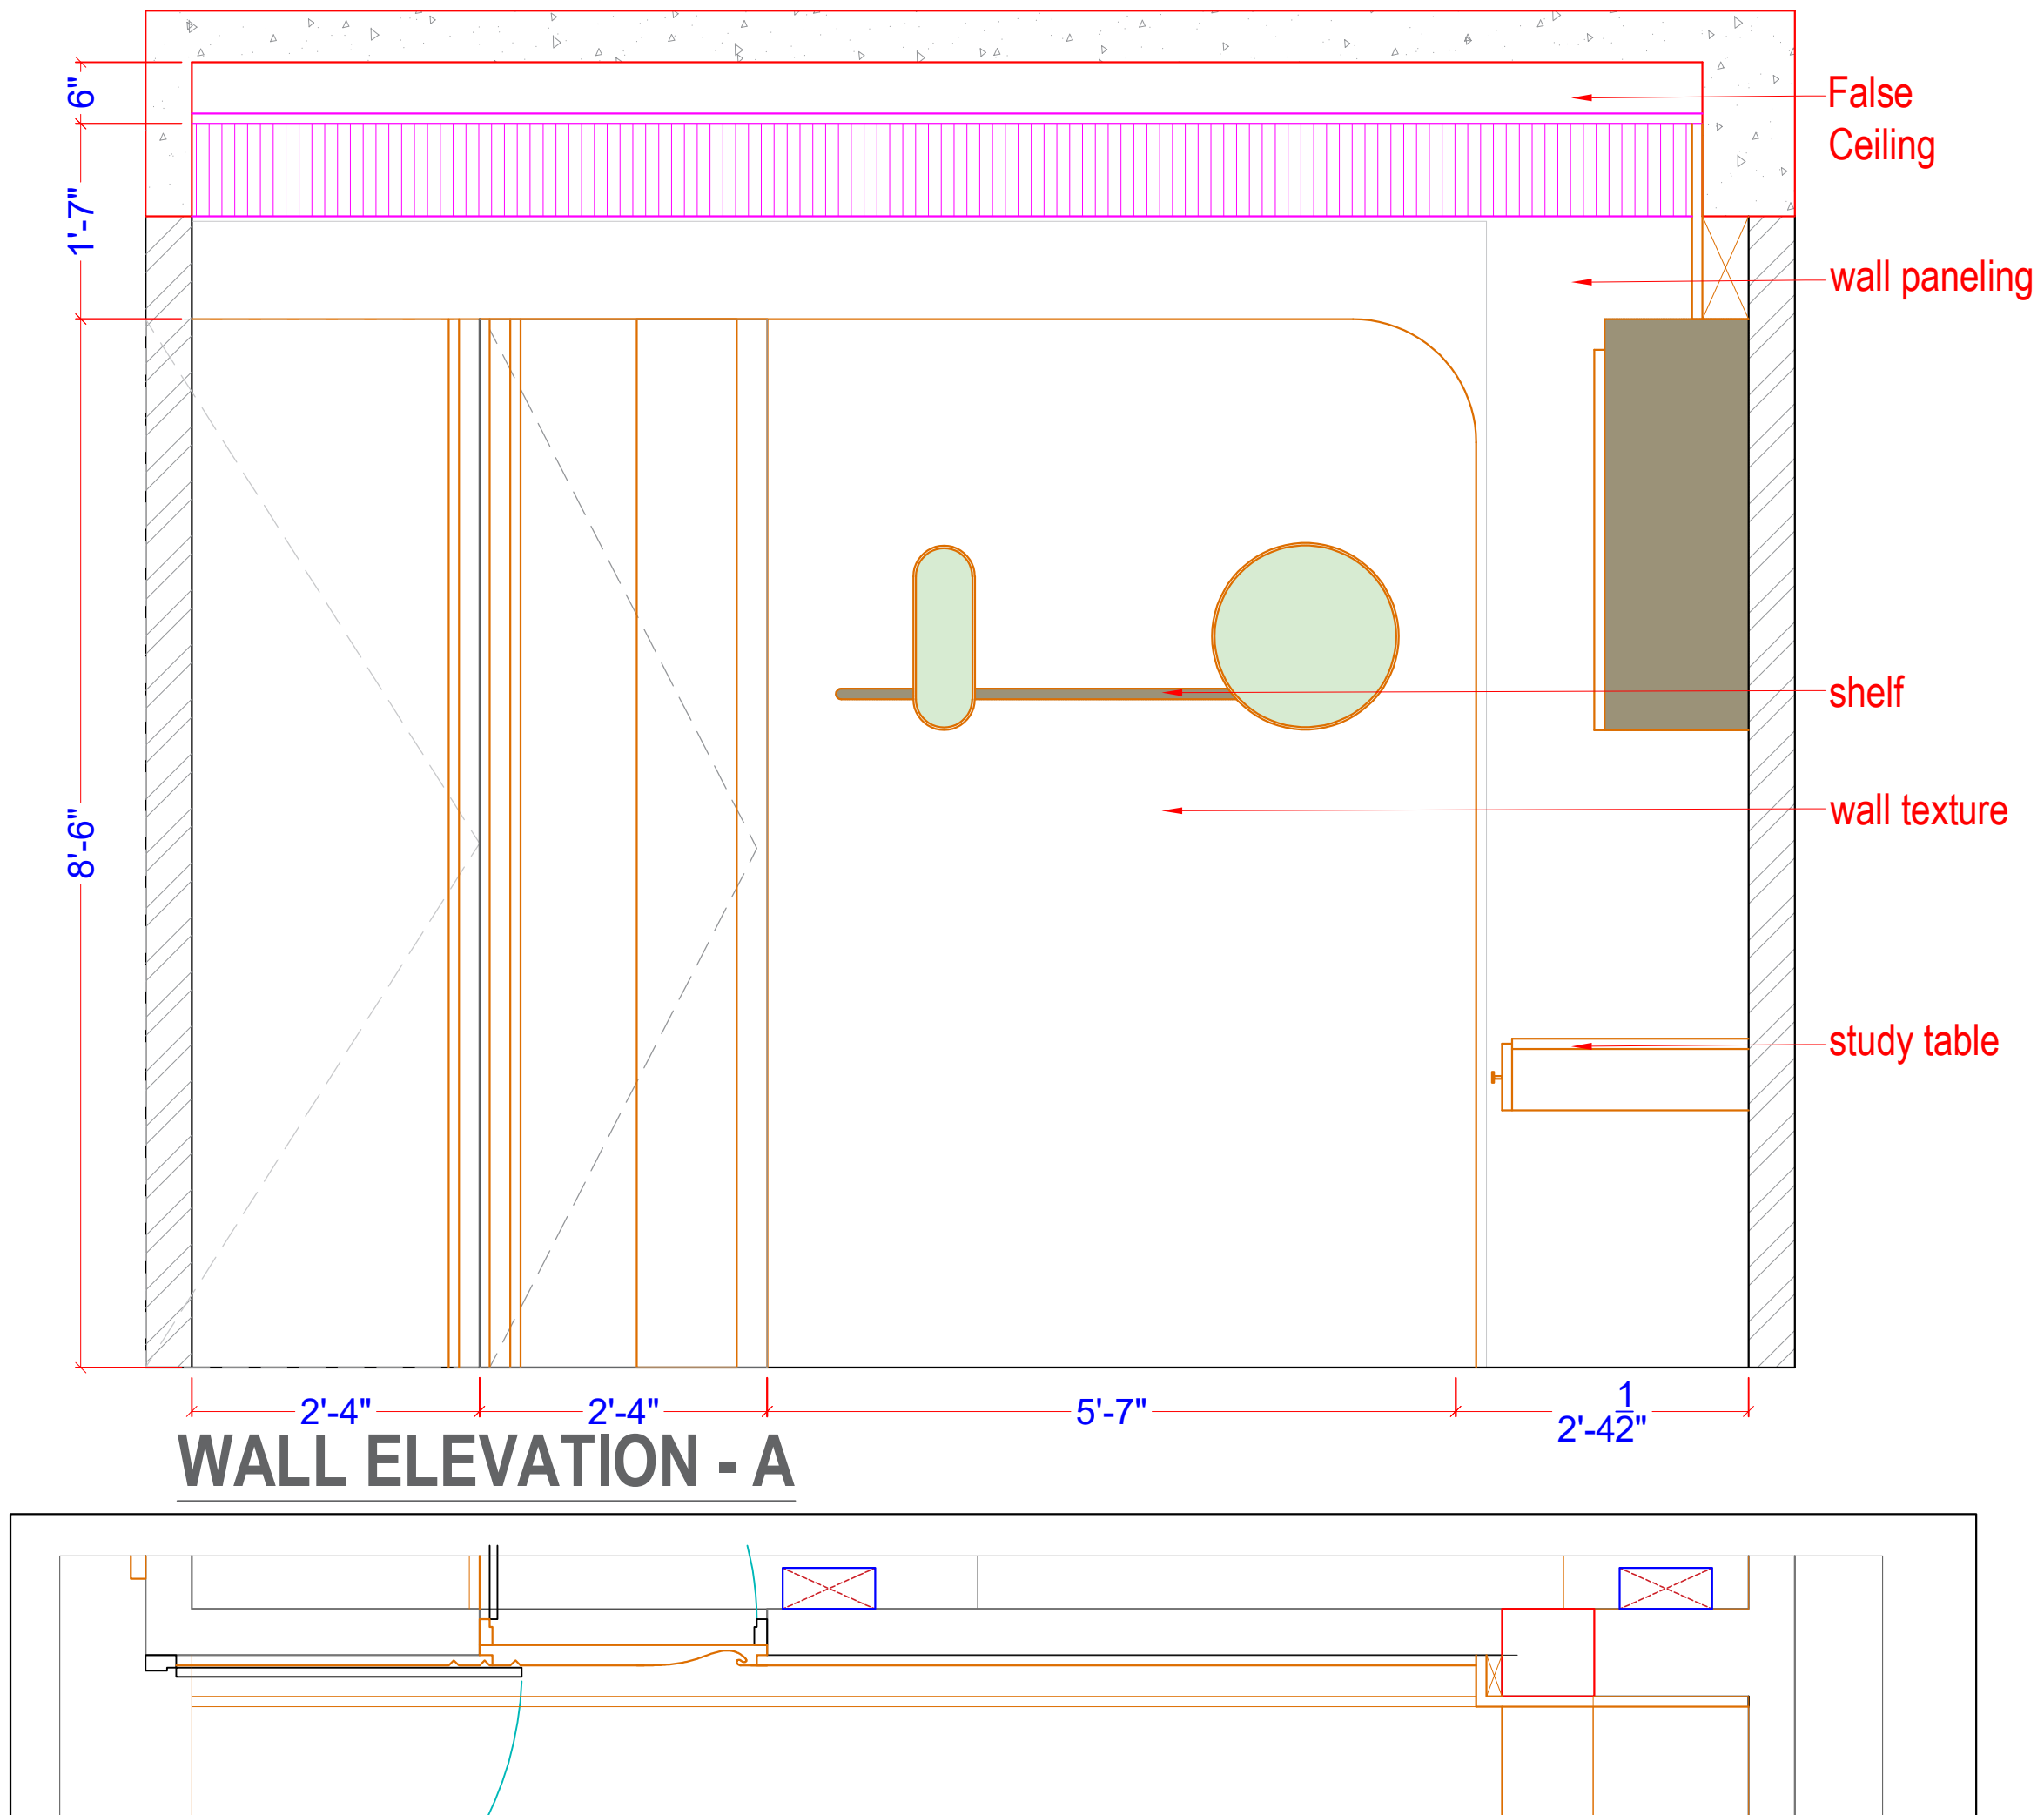

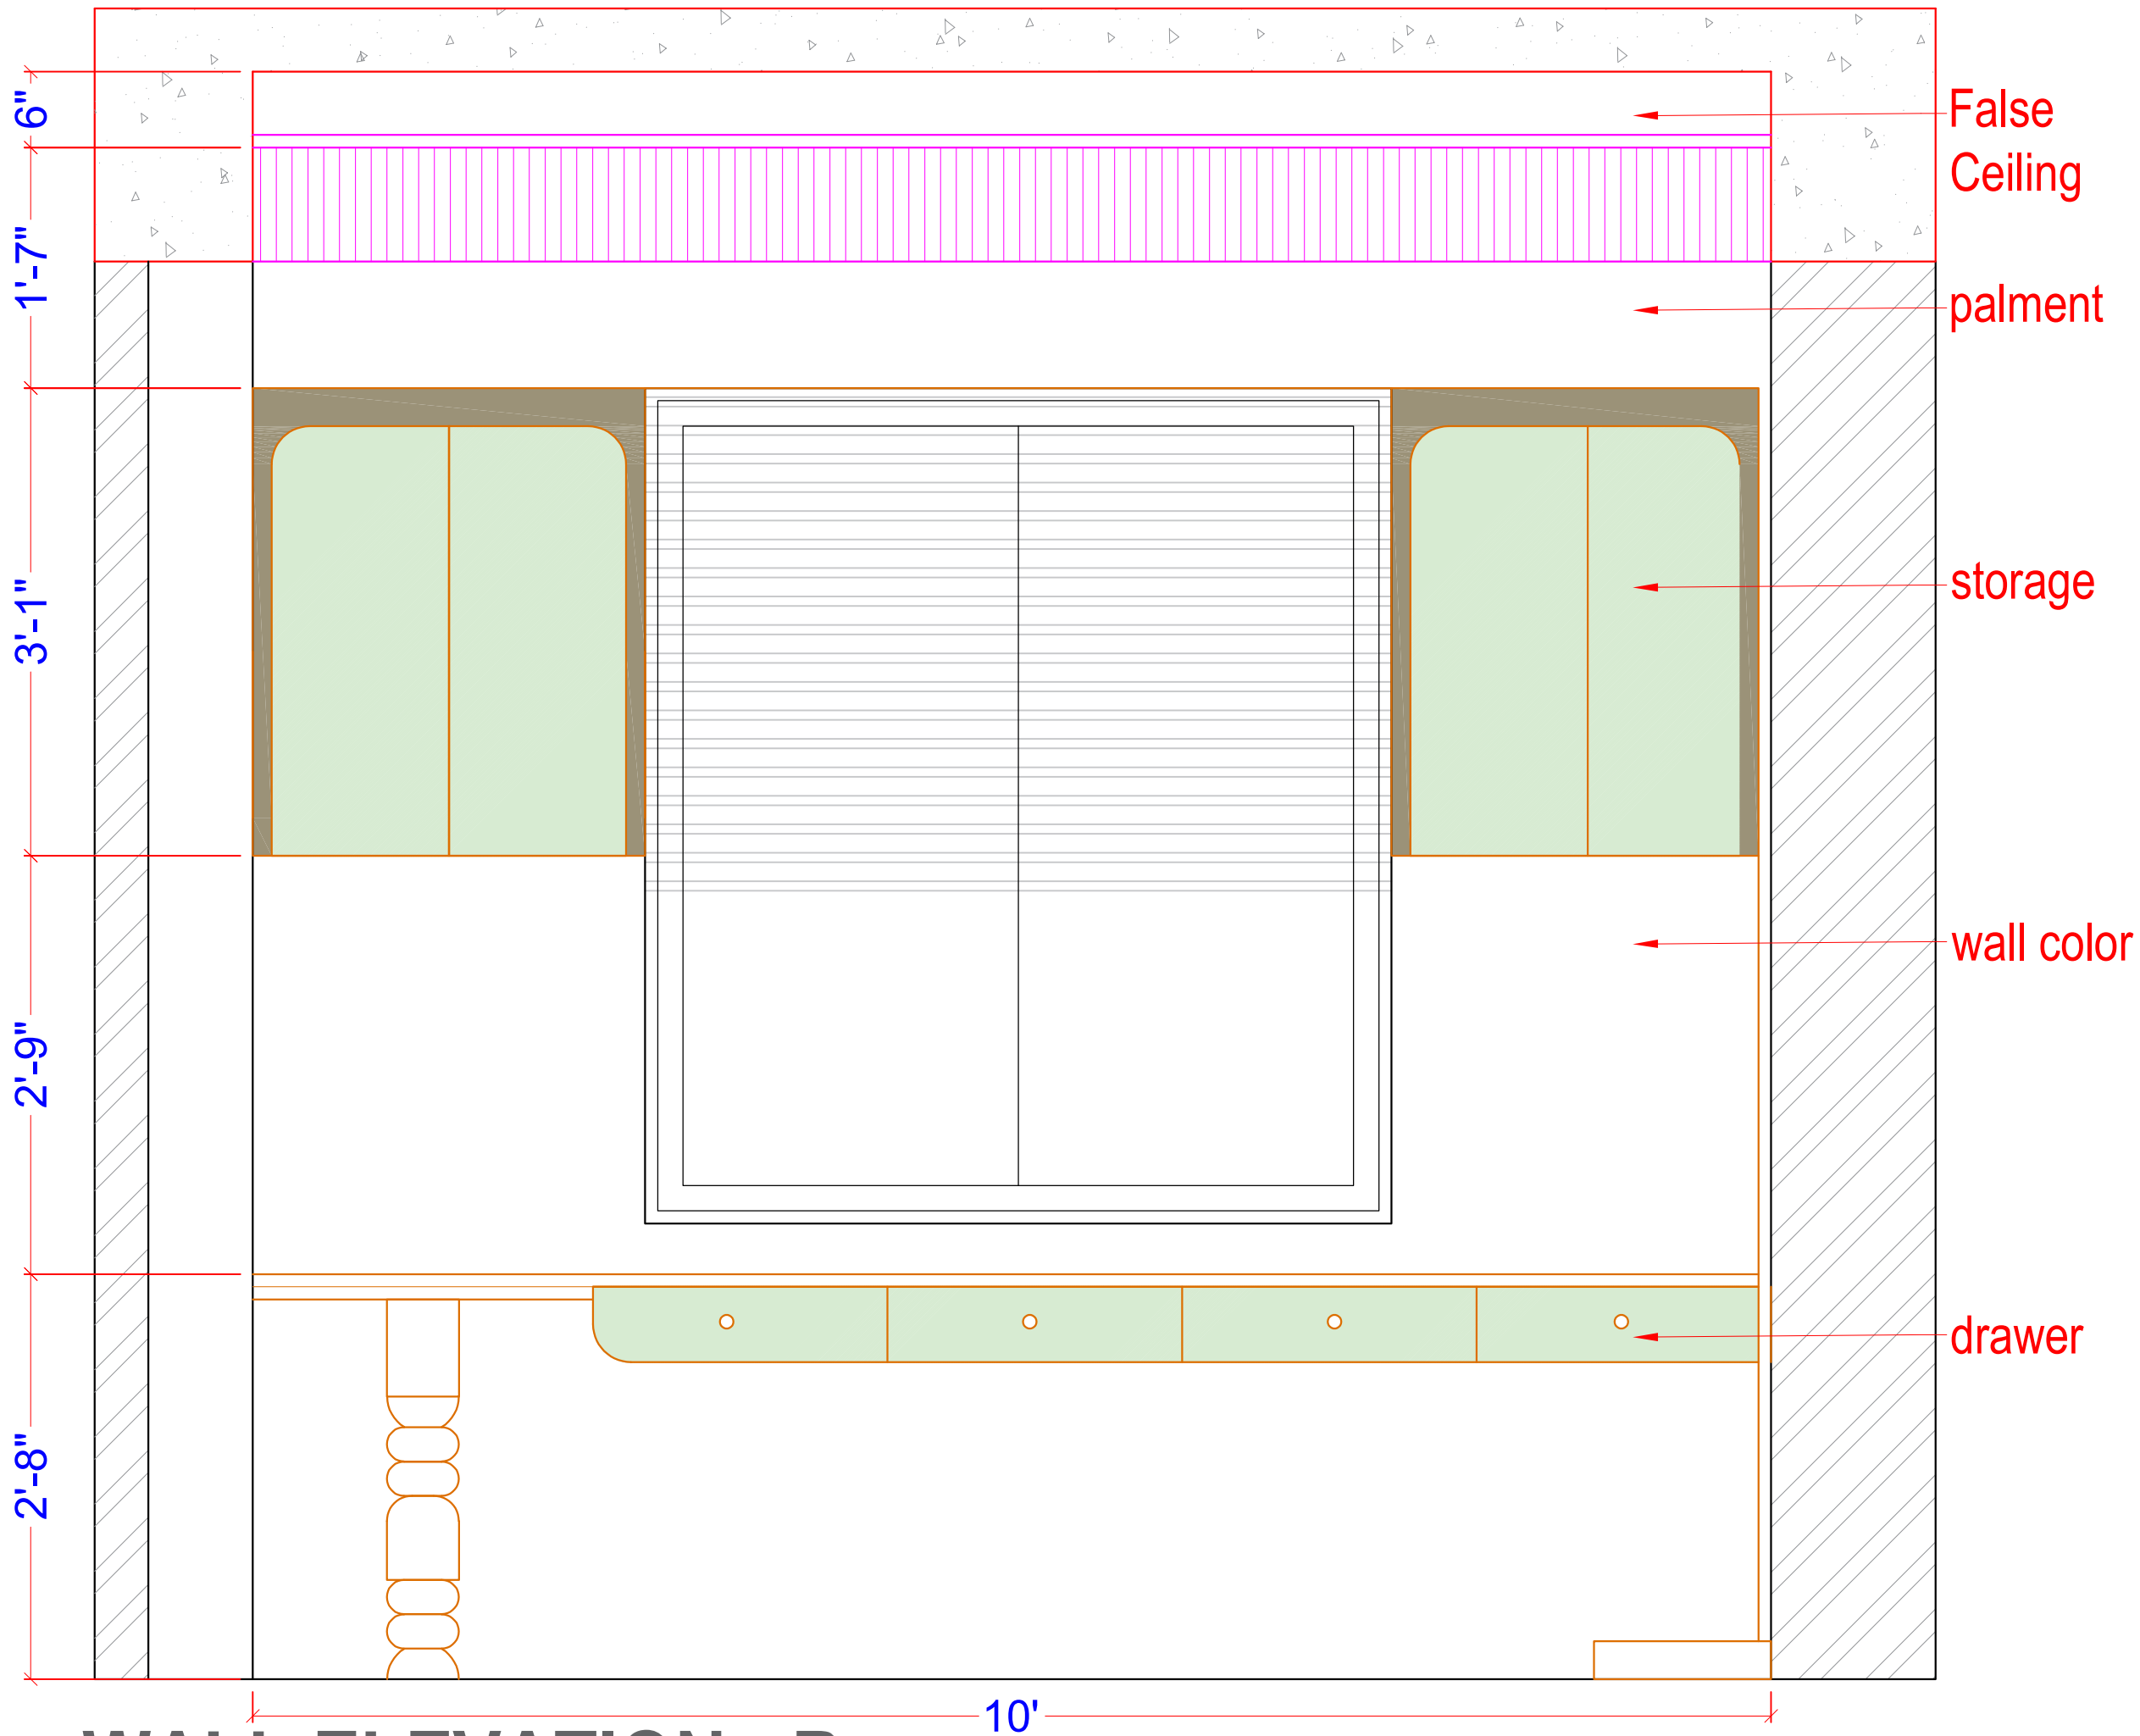

DRAWING TITLE :

KID'S BEDROOM
WALL ELEVATION

NOTES:

* DO NOT SCALE THE DRAWING.

* ALL DIMENSIONS ARE IN FEET \ INCHES.

* ANY DISCREPENCY IN THE DRAWING
TO BE BROUGHT IN THE DESIGNER'S
NOTICE BEFORE IMPLEMENTATION
ON SITE.

SITE ADDRESS:

Vadodara

CLIENT NAME:

PANCHOLI'S

DATE:

06-06-2024

NORTH:

DRAWING DETAIL

REVISION NO.

R1

R2

R3

REVISED DATE:

05/03/26

SCALE:

N.T.S

DRAWN BY:

PRASANNA

CHECKED BY:

MITTAL



www.mayaspace.studio



mayaspace.studio@gmail.com




+918980144077



@mayaspace.studio



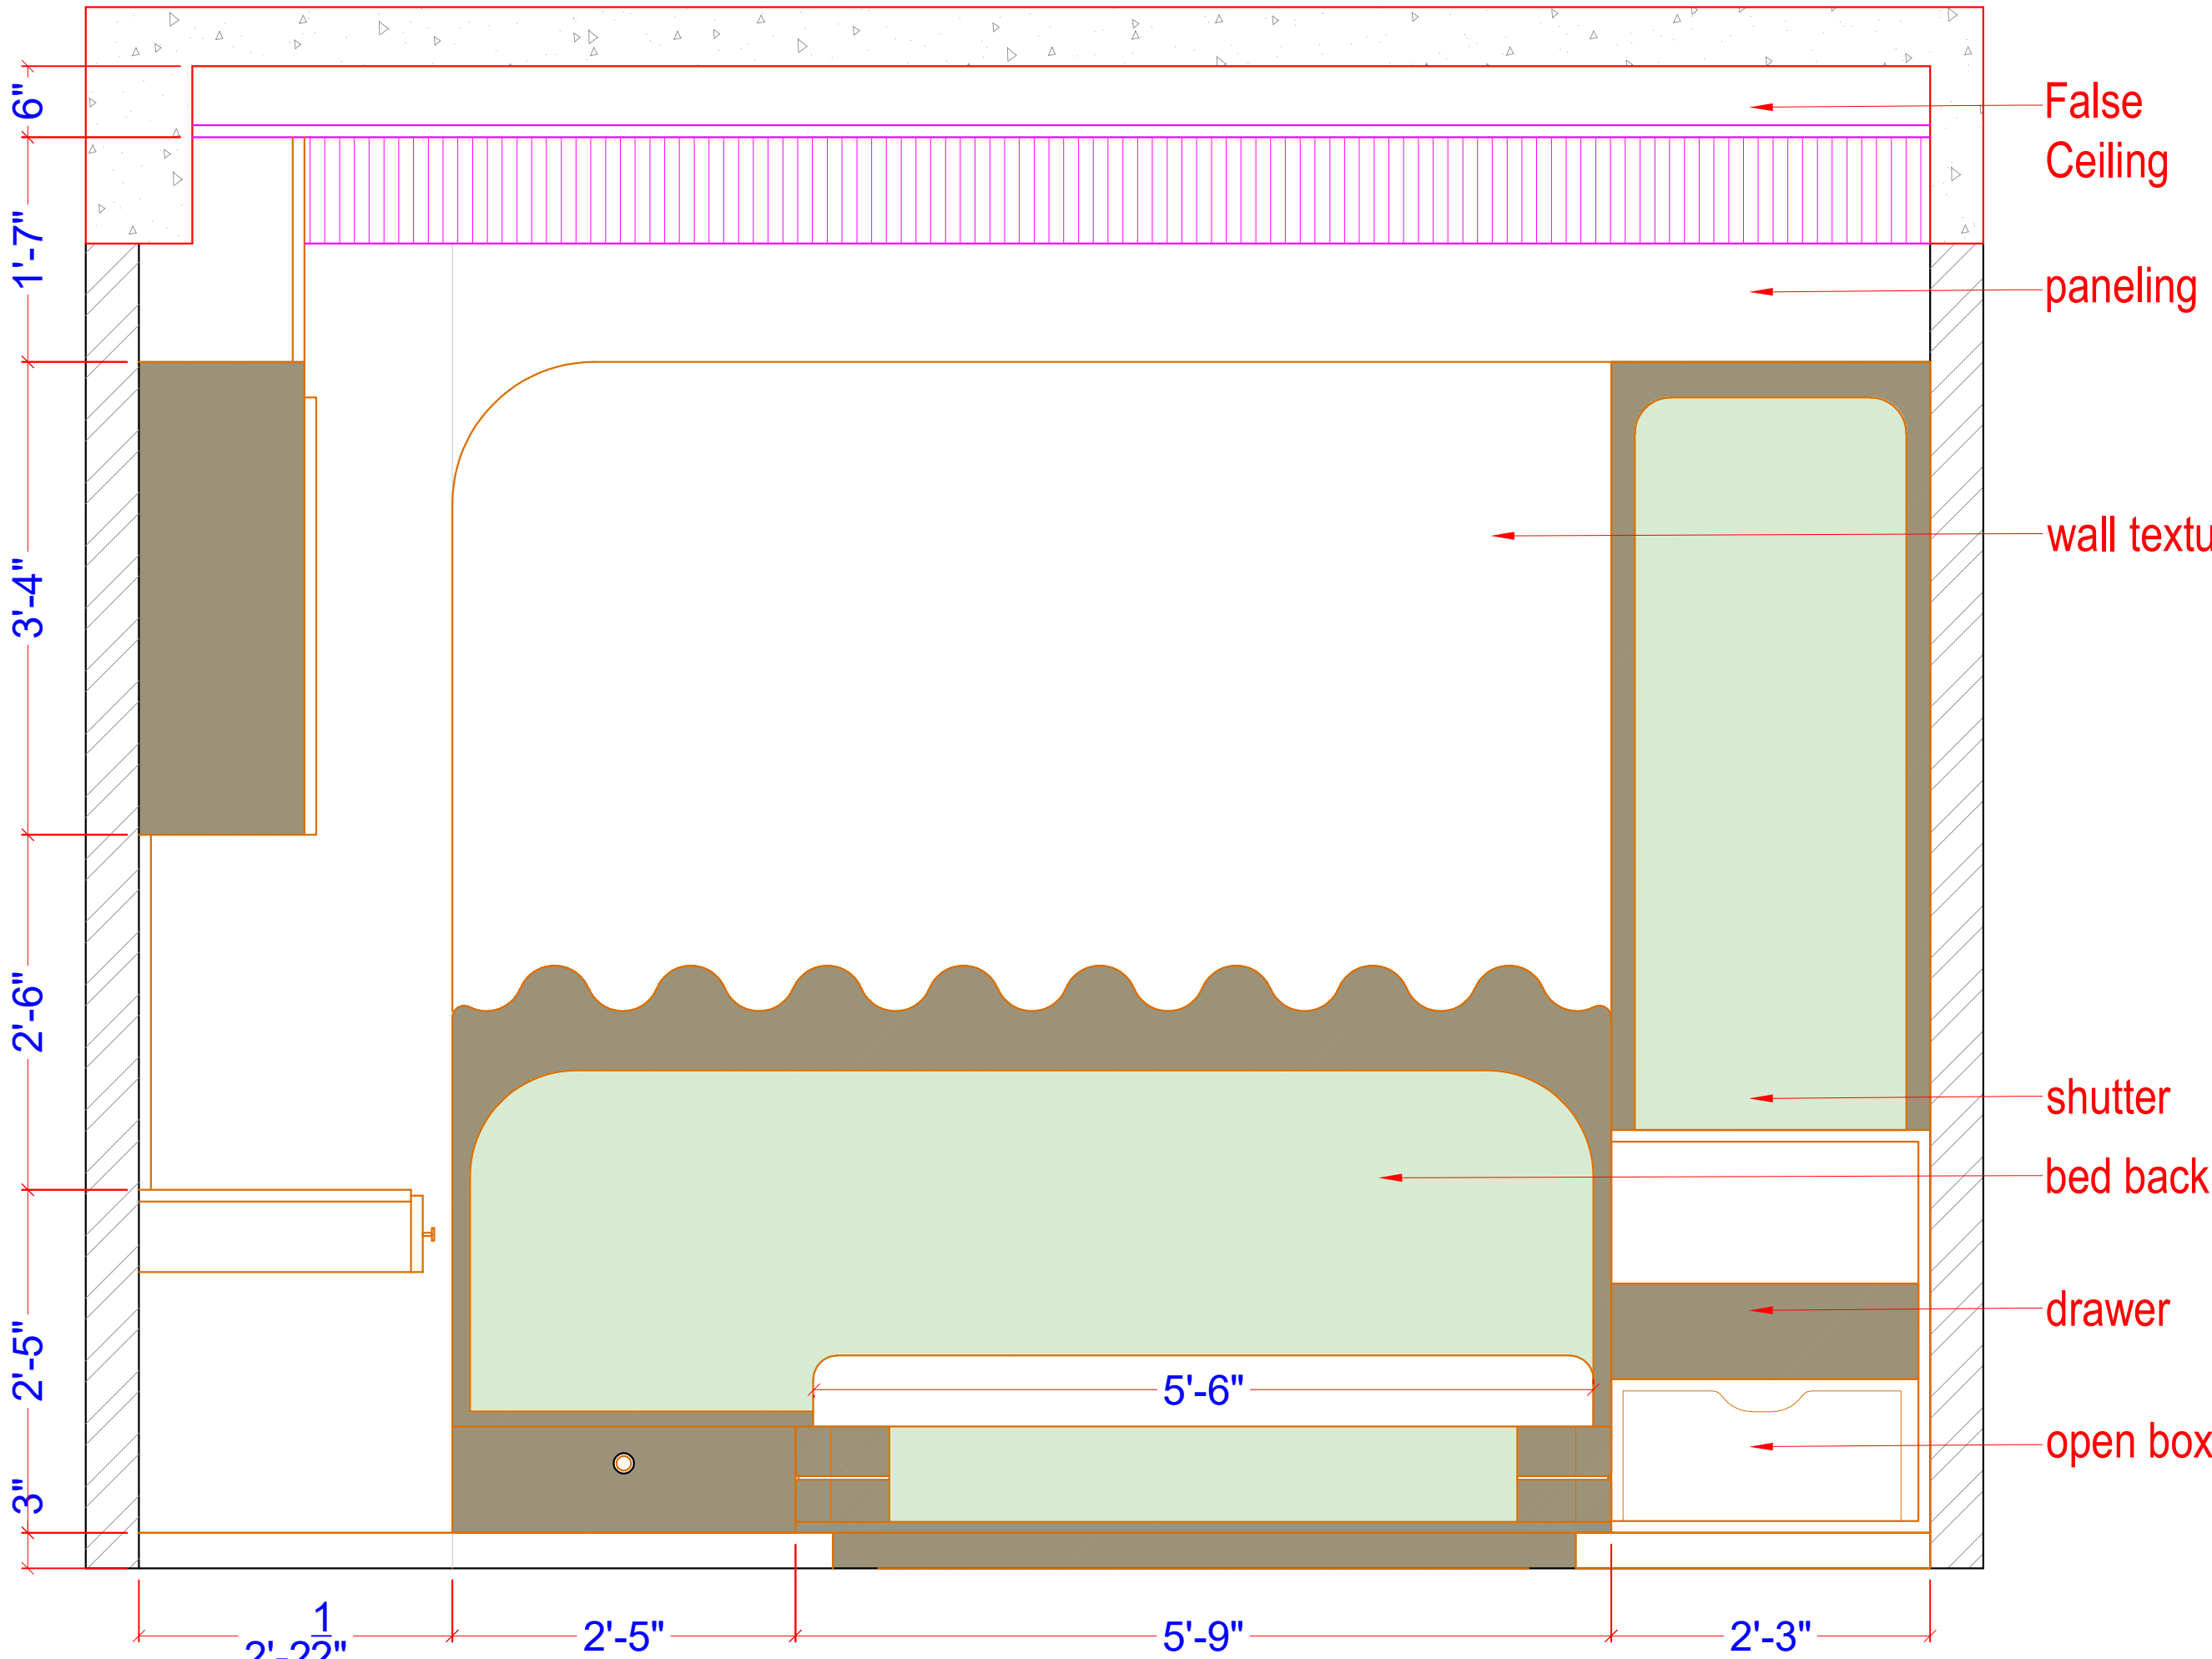

DRAWING TITLE :

KID'S BEDROOM
WALL ELEVATION

NOTES:

* DO NOT SCALE THE DRAWING.

* ALL DIMENSIONS ARE IN FEET \ INCHES.

* ANY DISCREPENCY IN THE DRAWING
TO BE BROUGHT IN THE DESIGNER'S
NOTICE BEFORE IMPLEMENTATION
ON SITE.

SITE ADDRESS:

Vadodara

CLIENT NAME:

PANCHOLI'S

DATE:

06-06-2024

NORTH:

DRAWING DETAIL

REVISION NO.

R1

R2

R3

REVISED DATE:

05/03/26

SCALE:

N.T.S

DRAWN BY:

PRASANNA

CHECKED BY:

MITTAL



www.mayaspace.studio




mayaspace.studio@gmail.com




+918980144077



@mayaspace.studio

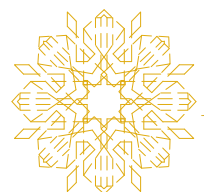

Maya
SPACE STUDIO

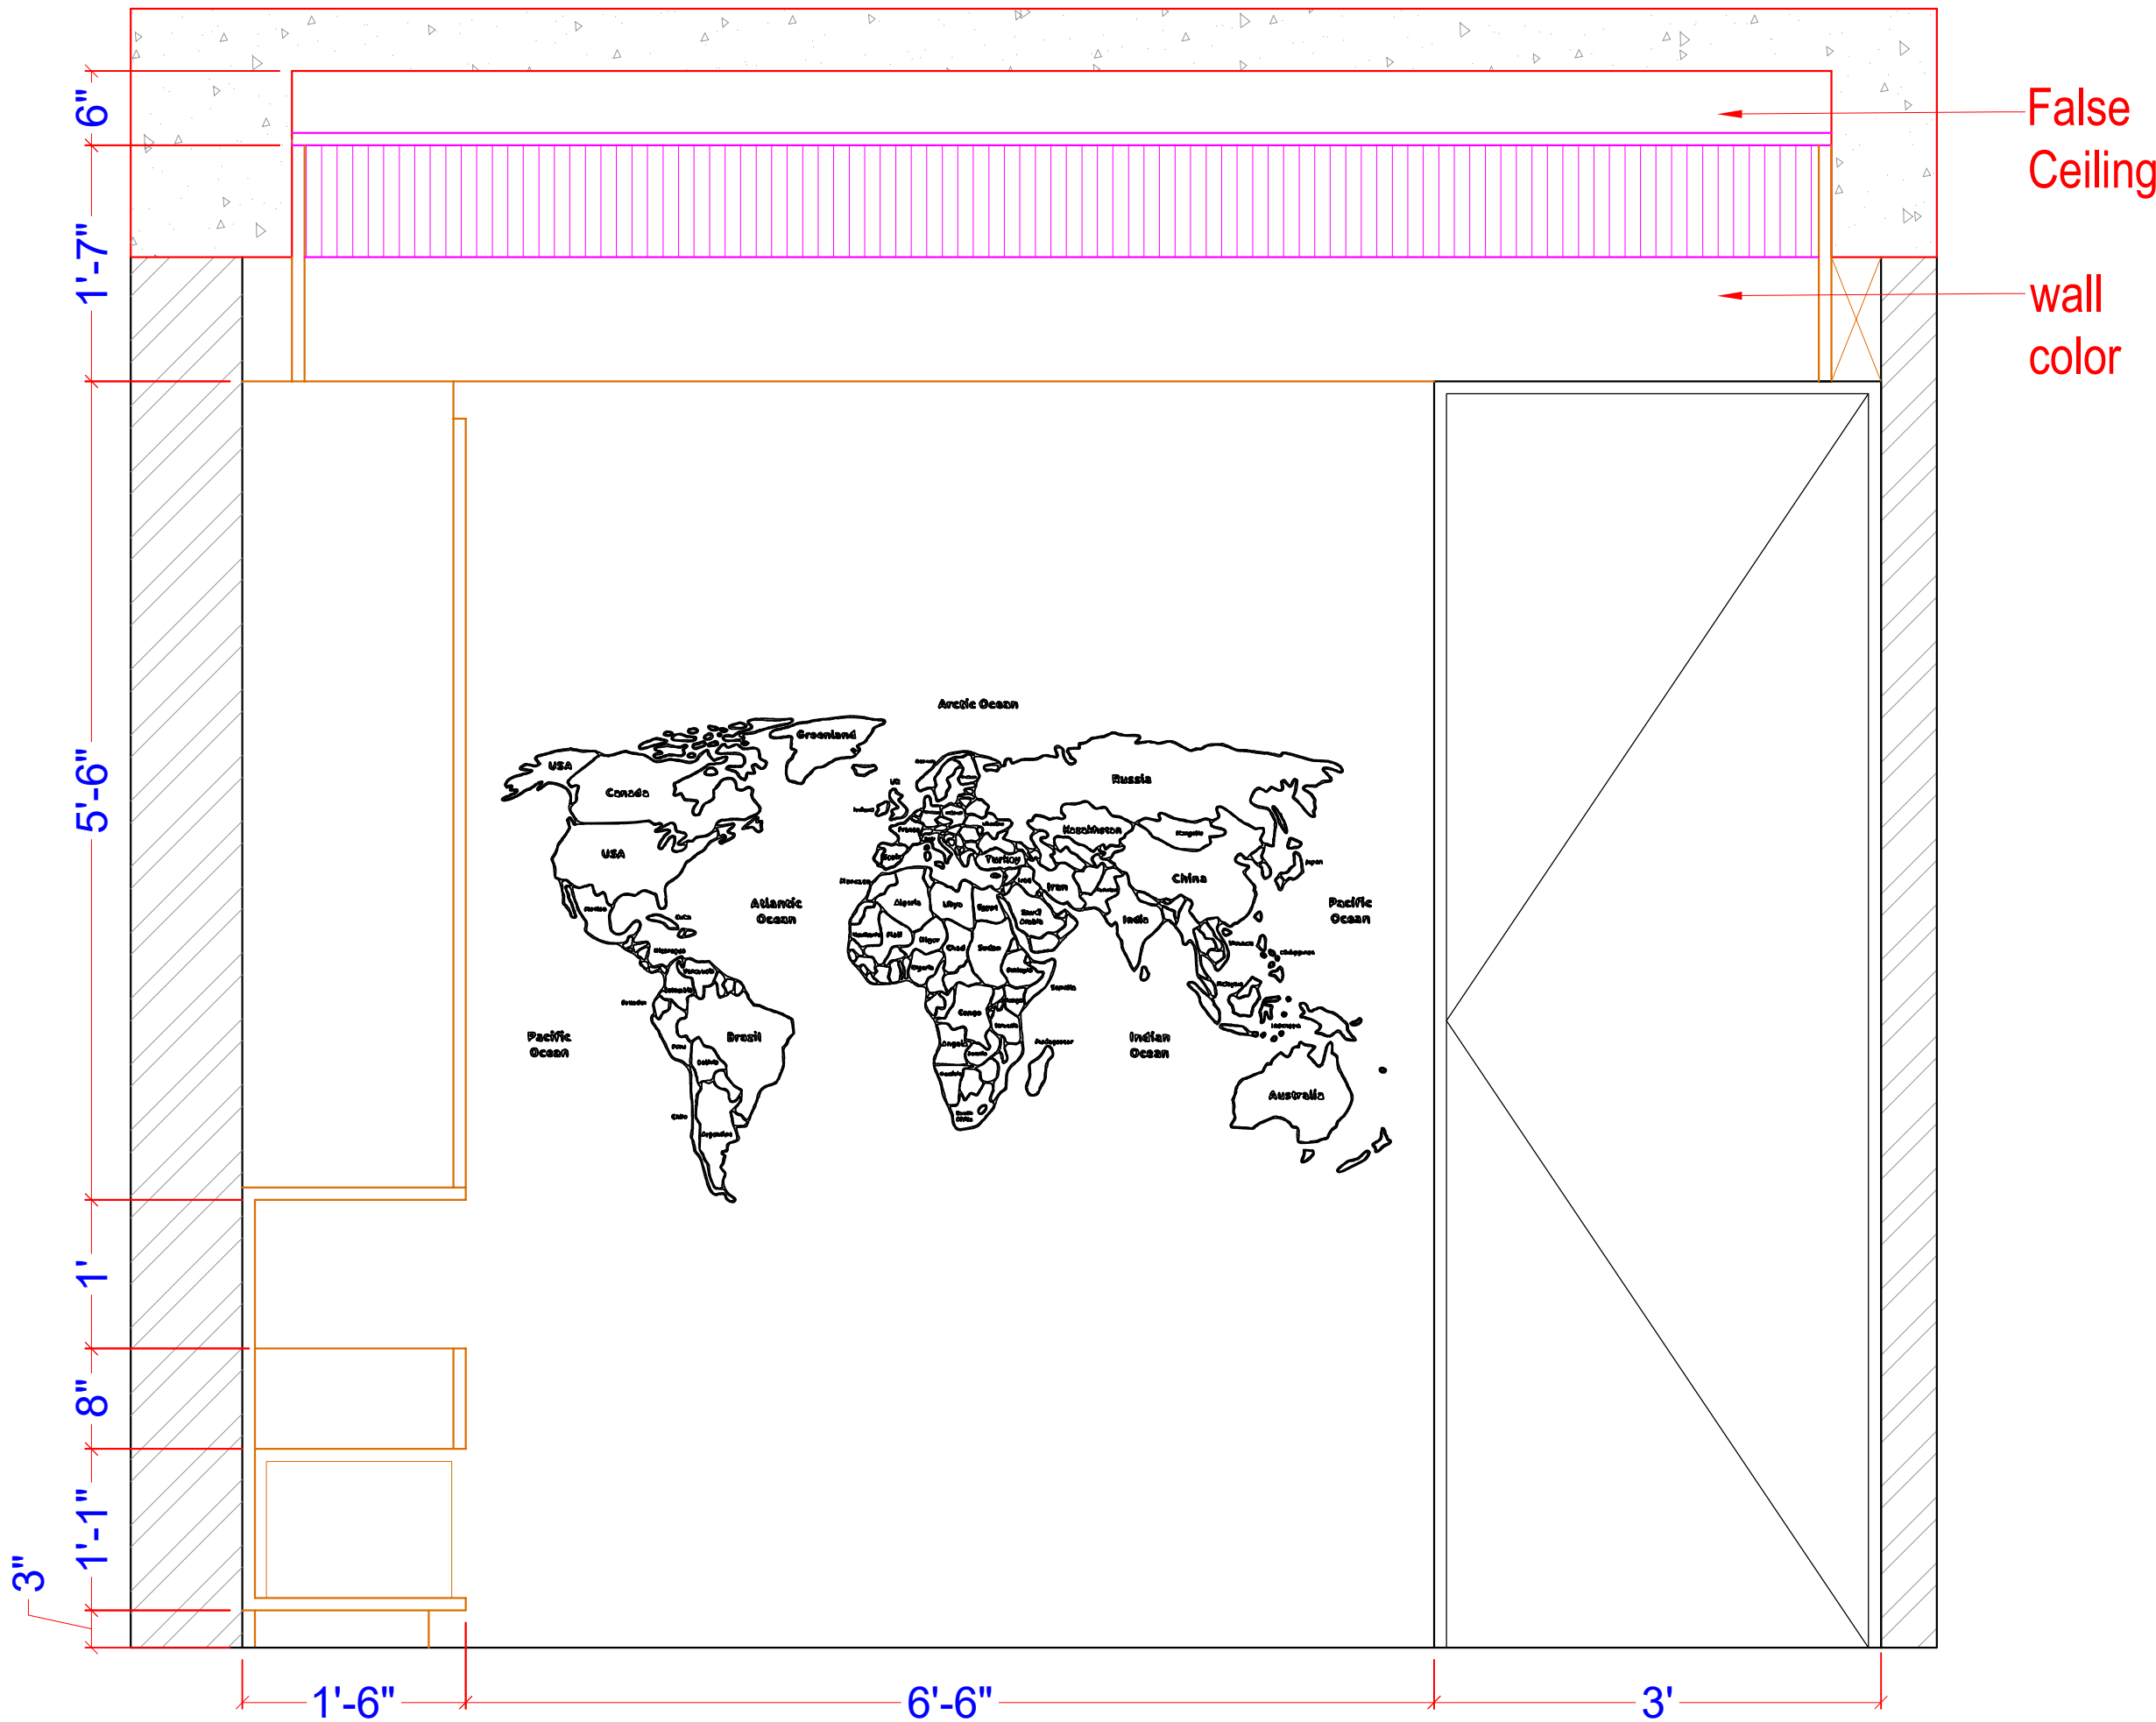

WALL ELEVATION - D

DRAWING TITLE :

KID'S BEDROOM
WALL ELEVATION

NOTES:

* DO NOT SCALE THE DRAWING.

* ALL DIMENSIONS ARE IN FEET \ INCHES.

* ANY DISCREPANCY IN THE DRAWING
TO BE BROUGHT IN THE DESIGNER'S
NOTICE BEFORE IMPLEMENTATION
ON SITE.

SITE ADDRESS:

Vadodara

CLIENT NAME:

PANCHOLI'S

DATE:

06-06-2024

NORTH:

DRAWING DETAIL

REVISION NO.

R1

R2

R3

REVISED DATE:

05/03/26

SCALE:

N.T.S

DRAWN BY:

PRASANNA

CHECKED BY:

MITTAL



www.mayaspace.studio



mayaspace.studio@gmail.com



+918980144077



@mayaspace.studio

