


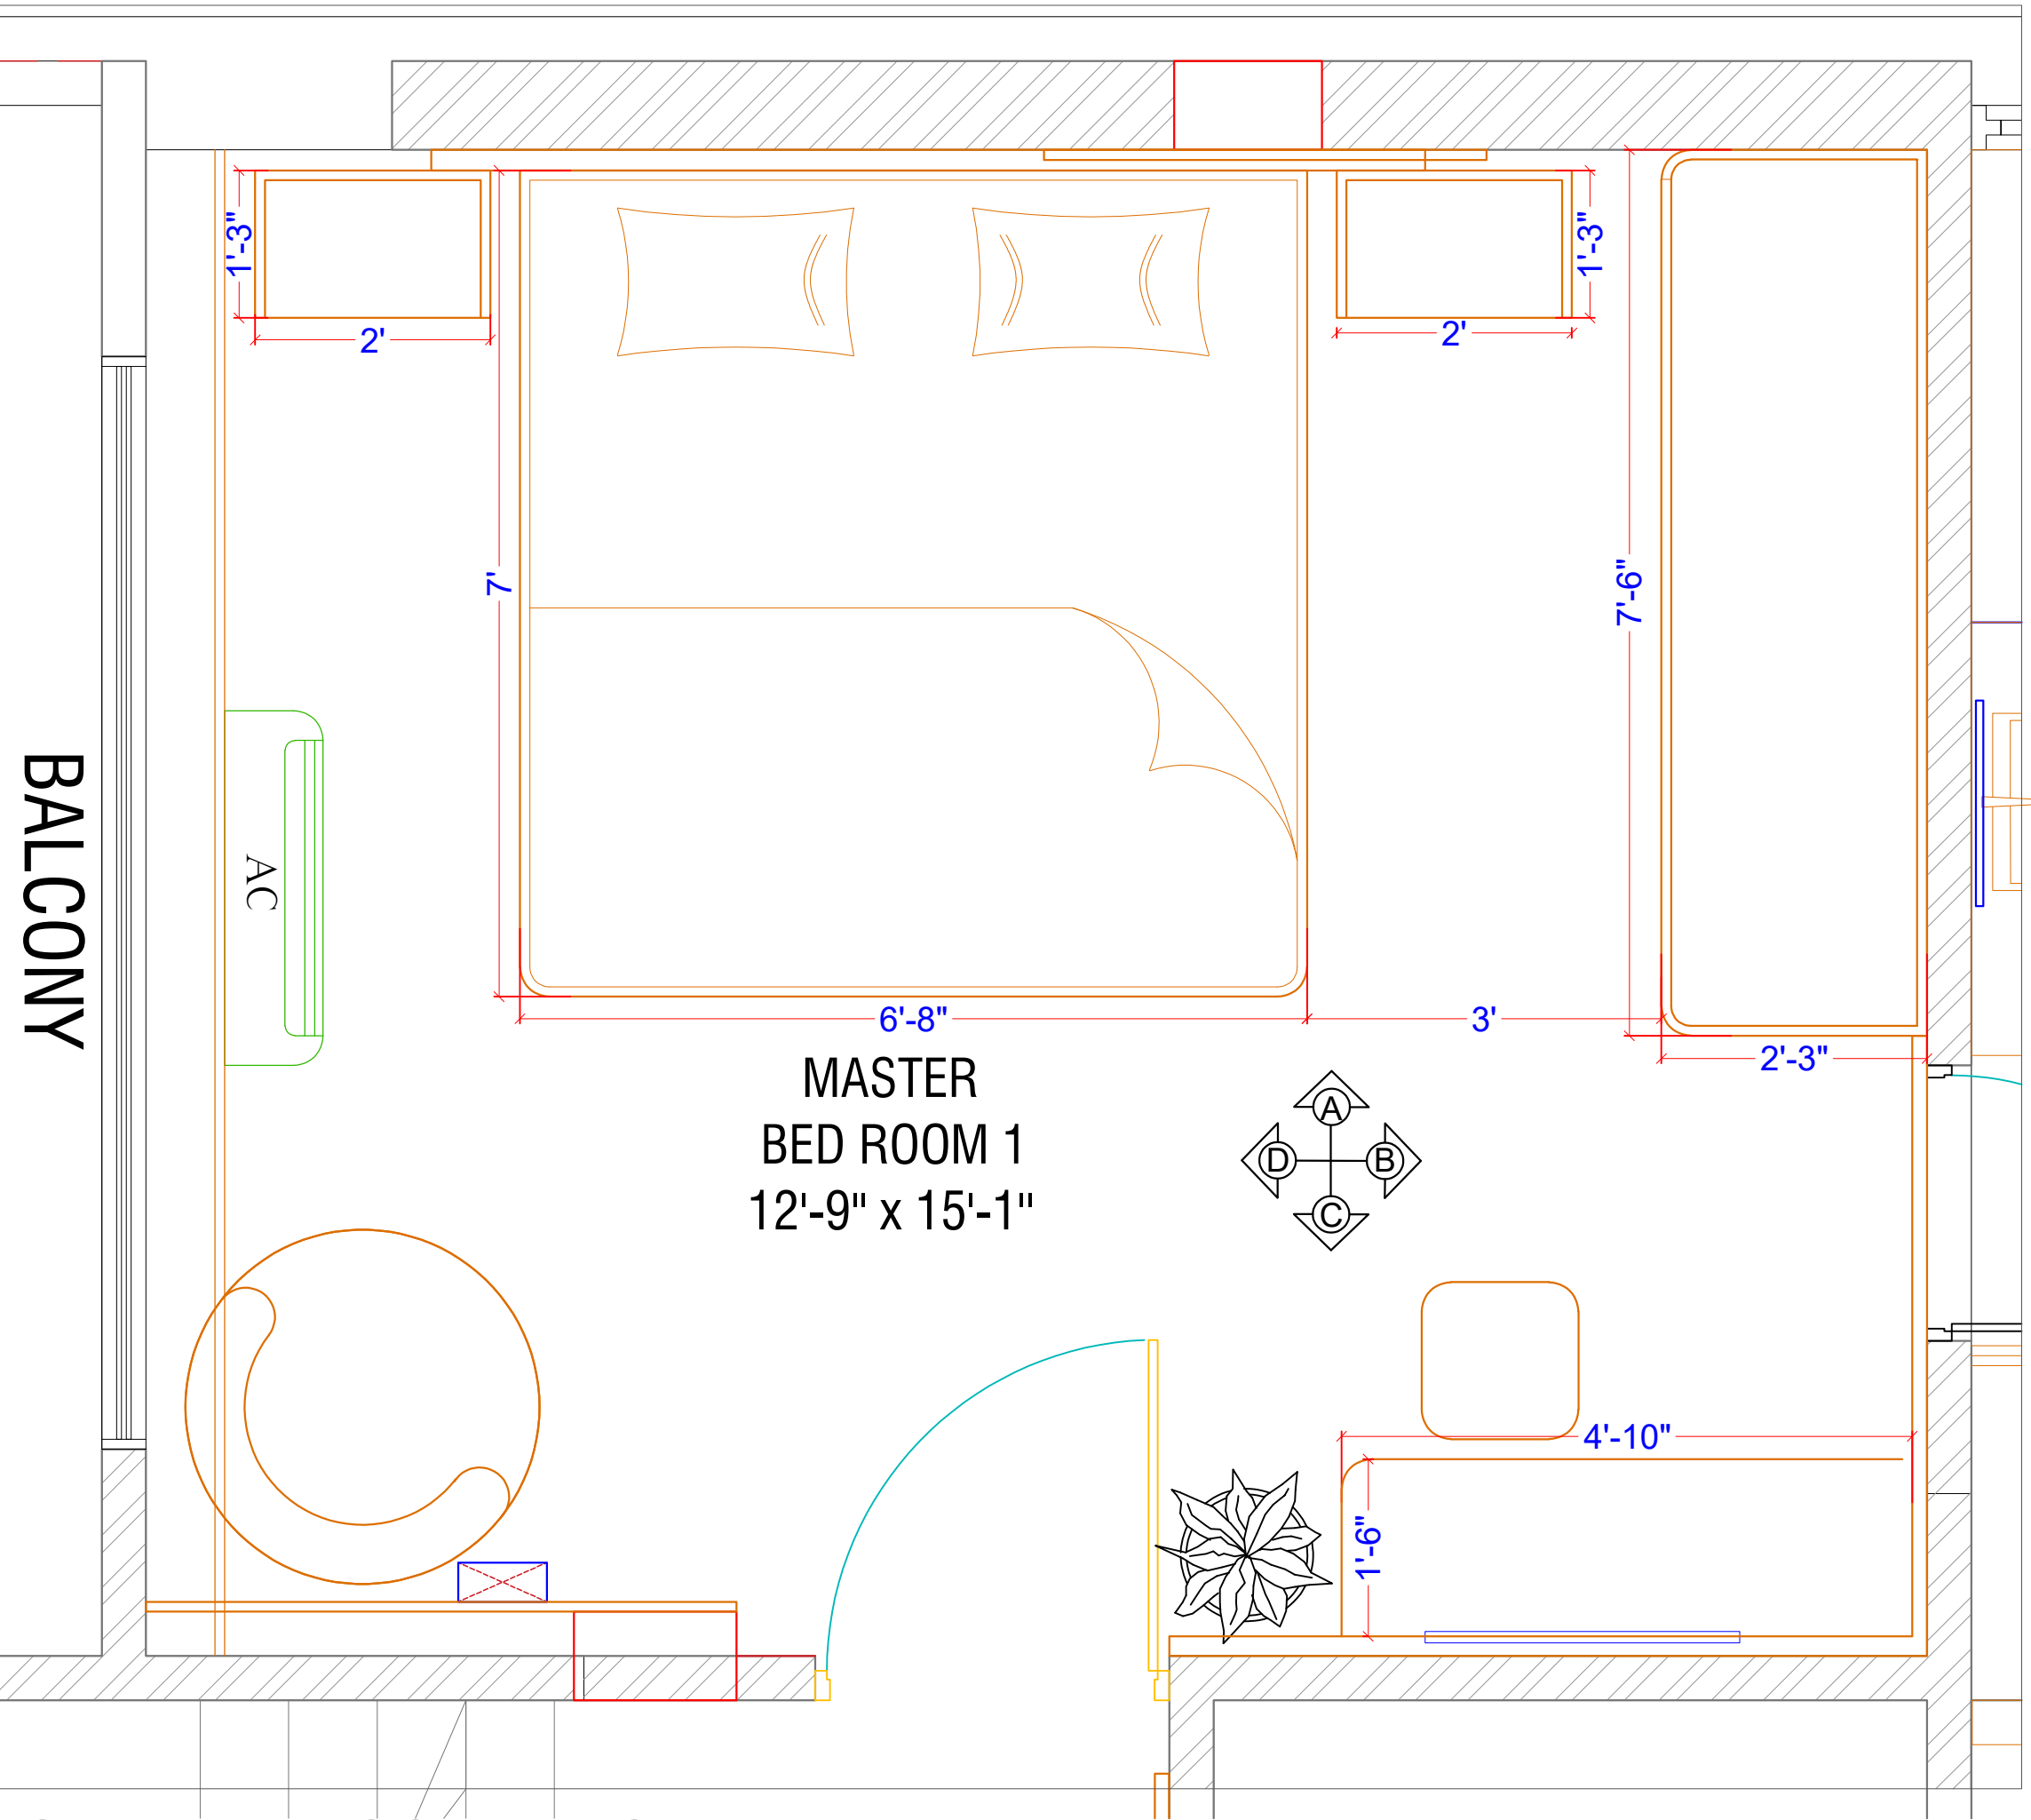

DRAWING TITLE :

MASTER BEDROOM-1
FURNITURE LAYOUT

NOTES:

- * DO NOT SCALE THE DRAWING.
- * ALL DIMENSIONS ARE IN FEET \ INCHES.
- * ANY DISCREPANCY IN THE DRAWING TO BE BROUGHT IN THE DESIGNER'S NOTICE BEFORE IMPLEMENTATION ON SITE.

SITE ADDRESS:

Vadodara

CLIENT NAME:

PANCHOLI'S

DATE: 06-06-2024

NORTH:


DRAWING DETAIL

REVISION NO.	R1	R2	R3
REVISED DATE:	05/03/26		
SCALE:	N.T.S		
DRAWN BY:	PRASANNA		
CHECKED BY:	MITTAL		

	www.mayaspace.studio
	mayaspace.studio@gmail.com
	+918980144077
	@mayaspace.studio



MASTER BEDROOM LAYOUT

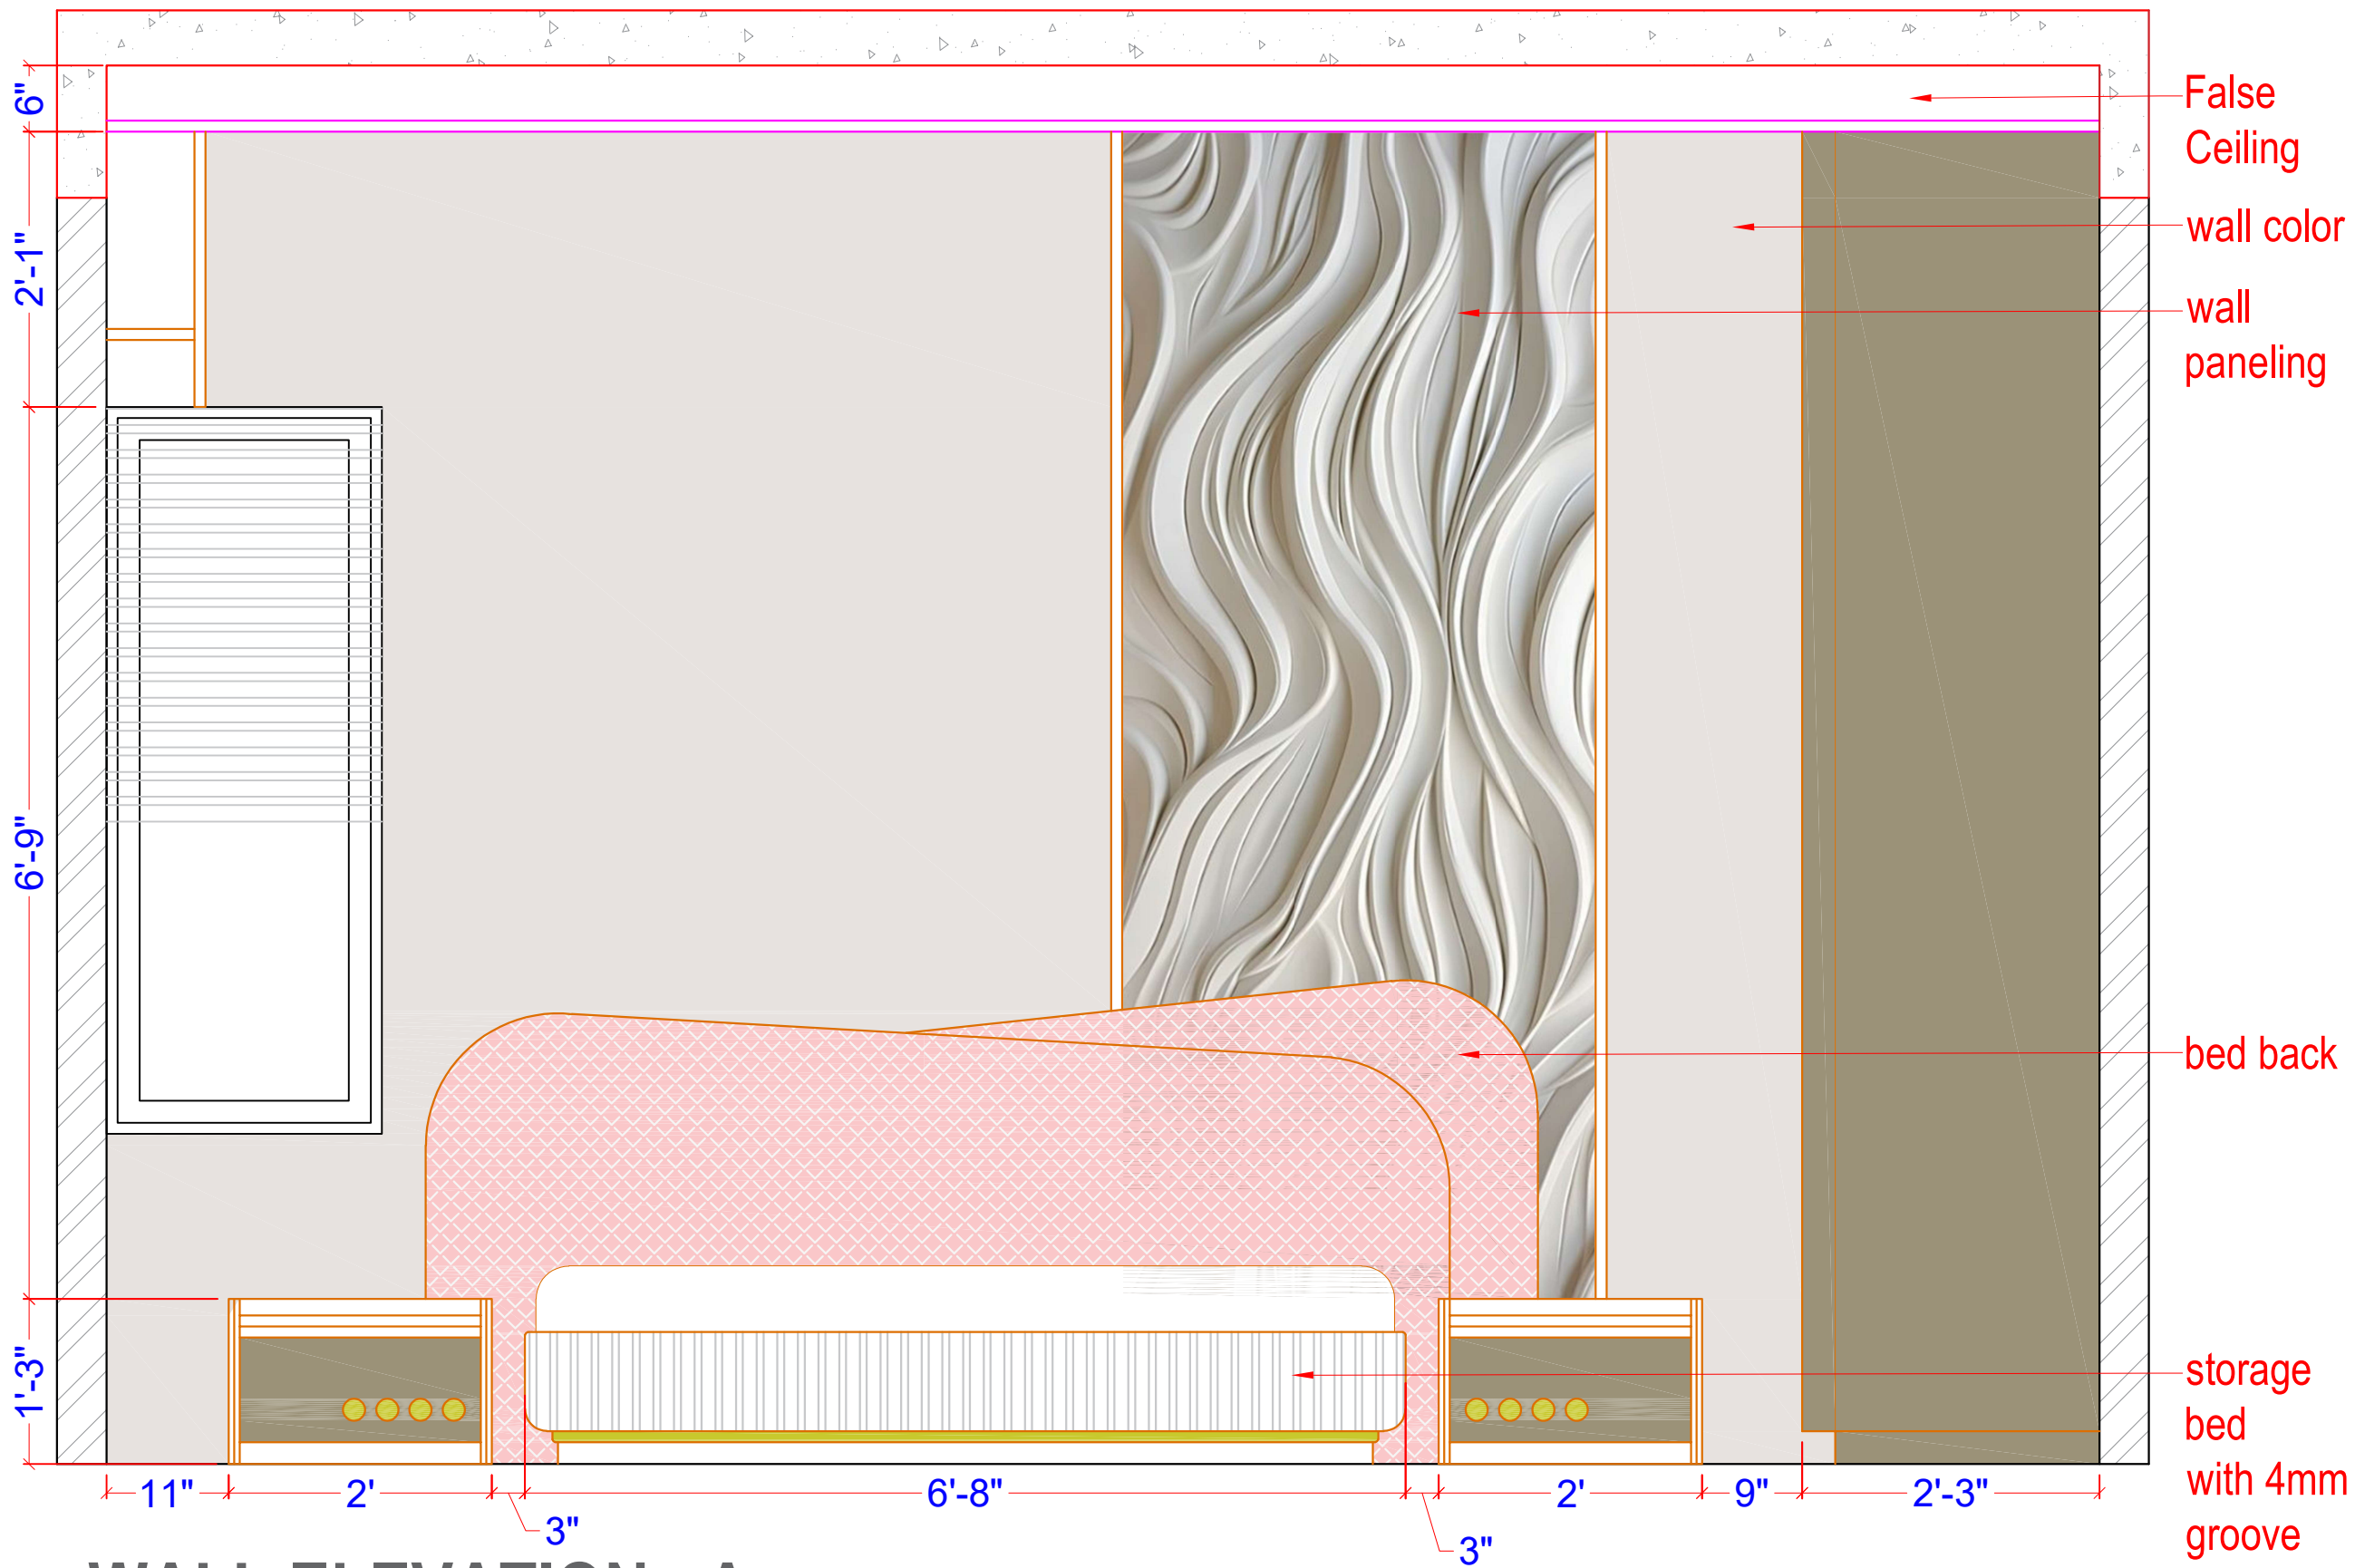

WALL ELEVATION - A

DRAWING TITLE :

MASTER BEDROOM-1
WALL ELEVATION

NOTES:

* DO NOT SCALE THE DRAWING.
* ALL DIMENSIONS ARE IN FEET \ INCHES.
* ANY DISCREPENCY IN THE DRAWING
TO BE BROUGHT IN THE DESIGNER'S
NOTICE BEFORE IMPLEMENTATION
ON SITE.

SITE ADDRESS:

Vadodara

CLIENT NAME:

PANCHOLI'S

DATE:

06-06-2024


NORTH:

DRAWING DETAIL

REVISION NO.	R1	R2	R3
REVISED DATE:	05/03/26		
SCALE:	N.T.S		
DRAWN BY:	PRASANNA		
CHECKED BY:	MITTAL		

	www.mayaspace.studio
	mayaspace.studio@gmail.com
	+918980144077
	@mayaspace.studio



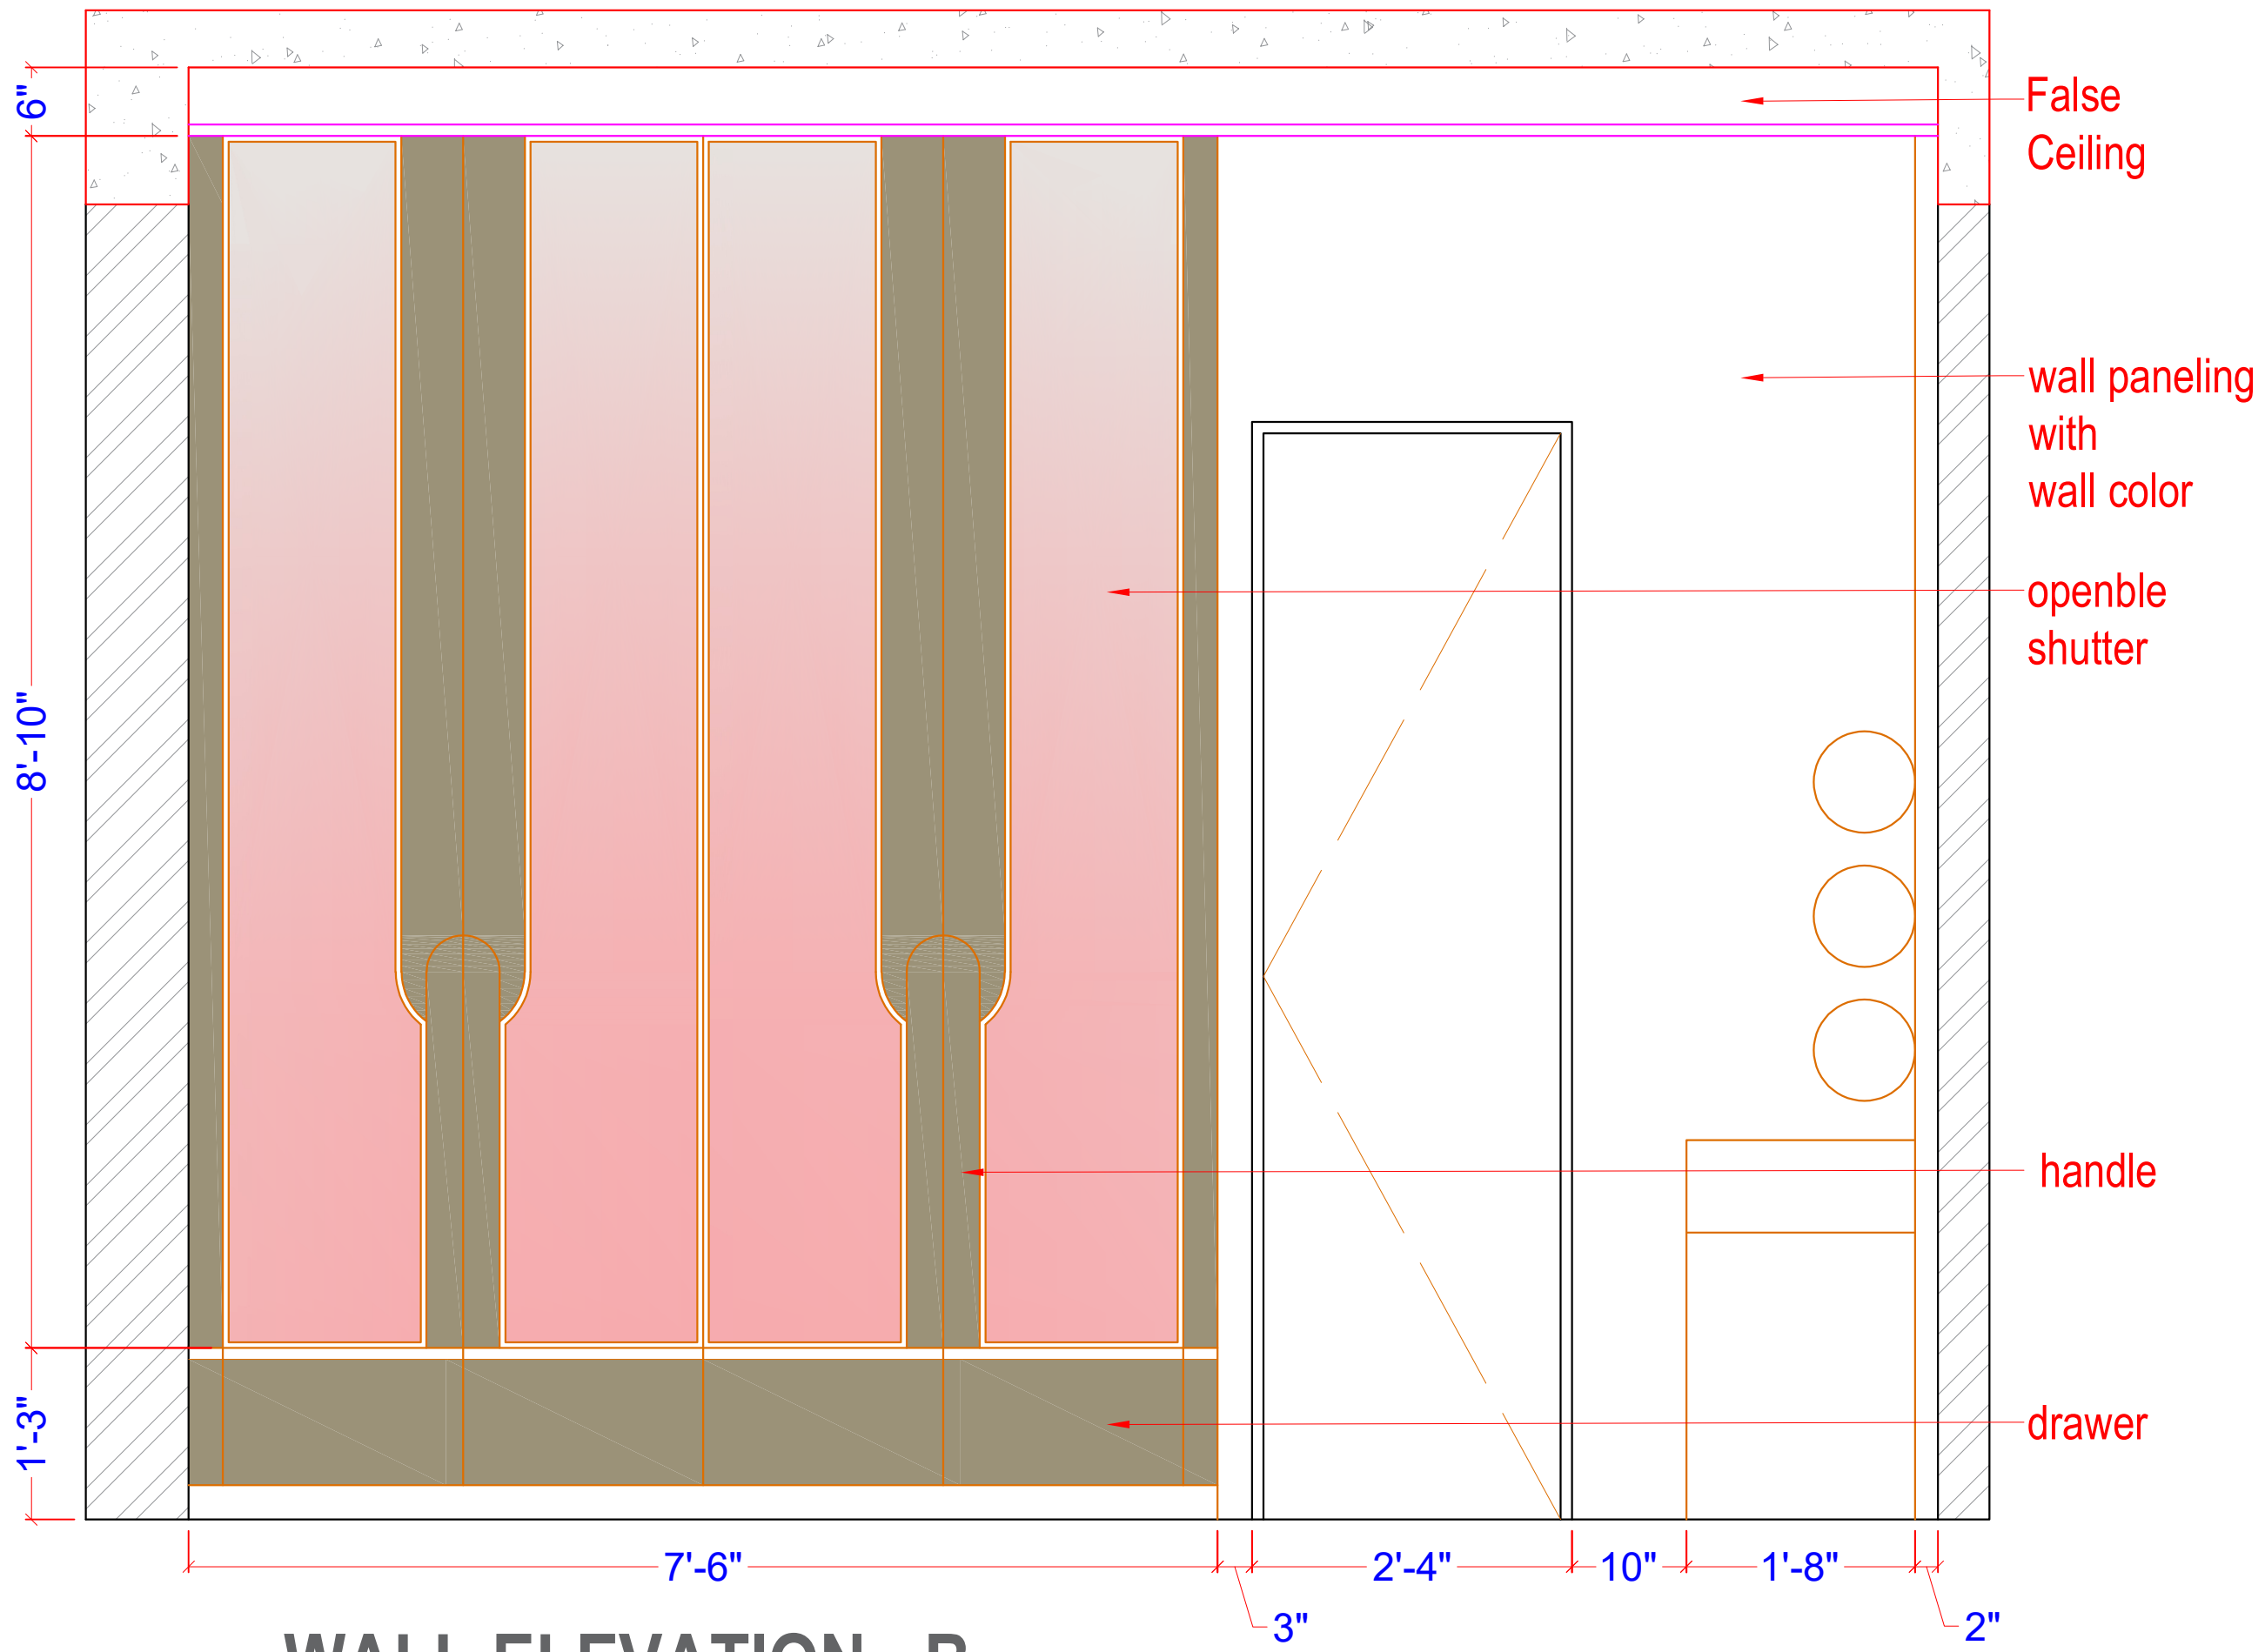

WALL ELEVATION - B

DRAWING TITLE :

**MASTER BEDROOM-1
WALL ELEVATION**

NOTES:

- * DO NOT SCALE THE DRAWING.
- * ALL DIMENSIONS ARE IN FEET \ INCHES.
- * ANY DISCREPENCY IN THE DRAWING TO BE BROUGHT IN THE DESIGNER'S NOTICE BEFORE IMPLEMENTATION ON SITE.

SITE ADDRESS:

Vadodara

CLIENT NAME:

PANCHOLI'S

DATE: 06-06-2024


NORTH:

DRAWING DETAIL

REVISION NO.	☐ R1 ☐ R2 ☐ R3
REVISED DATE:	05/03/26
SCALE:	N.T.S
DRAWN BY:	PRASANNA
CHECKED BY:	MITTAL

- www.mayaspace.studio
- mayaspace.studio@gmail.com
- +918980144077
- @mayaspace.studio



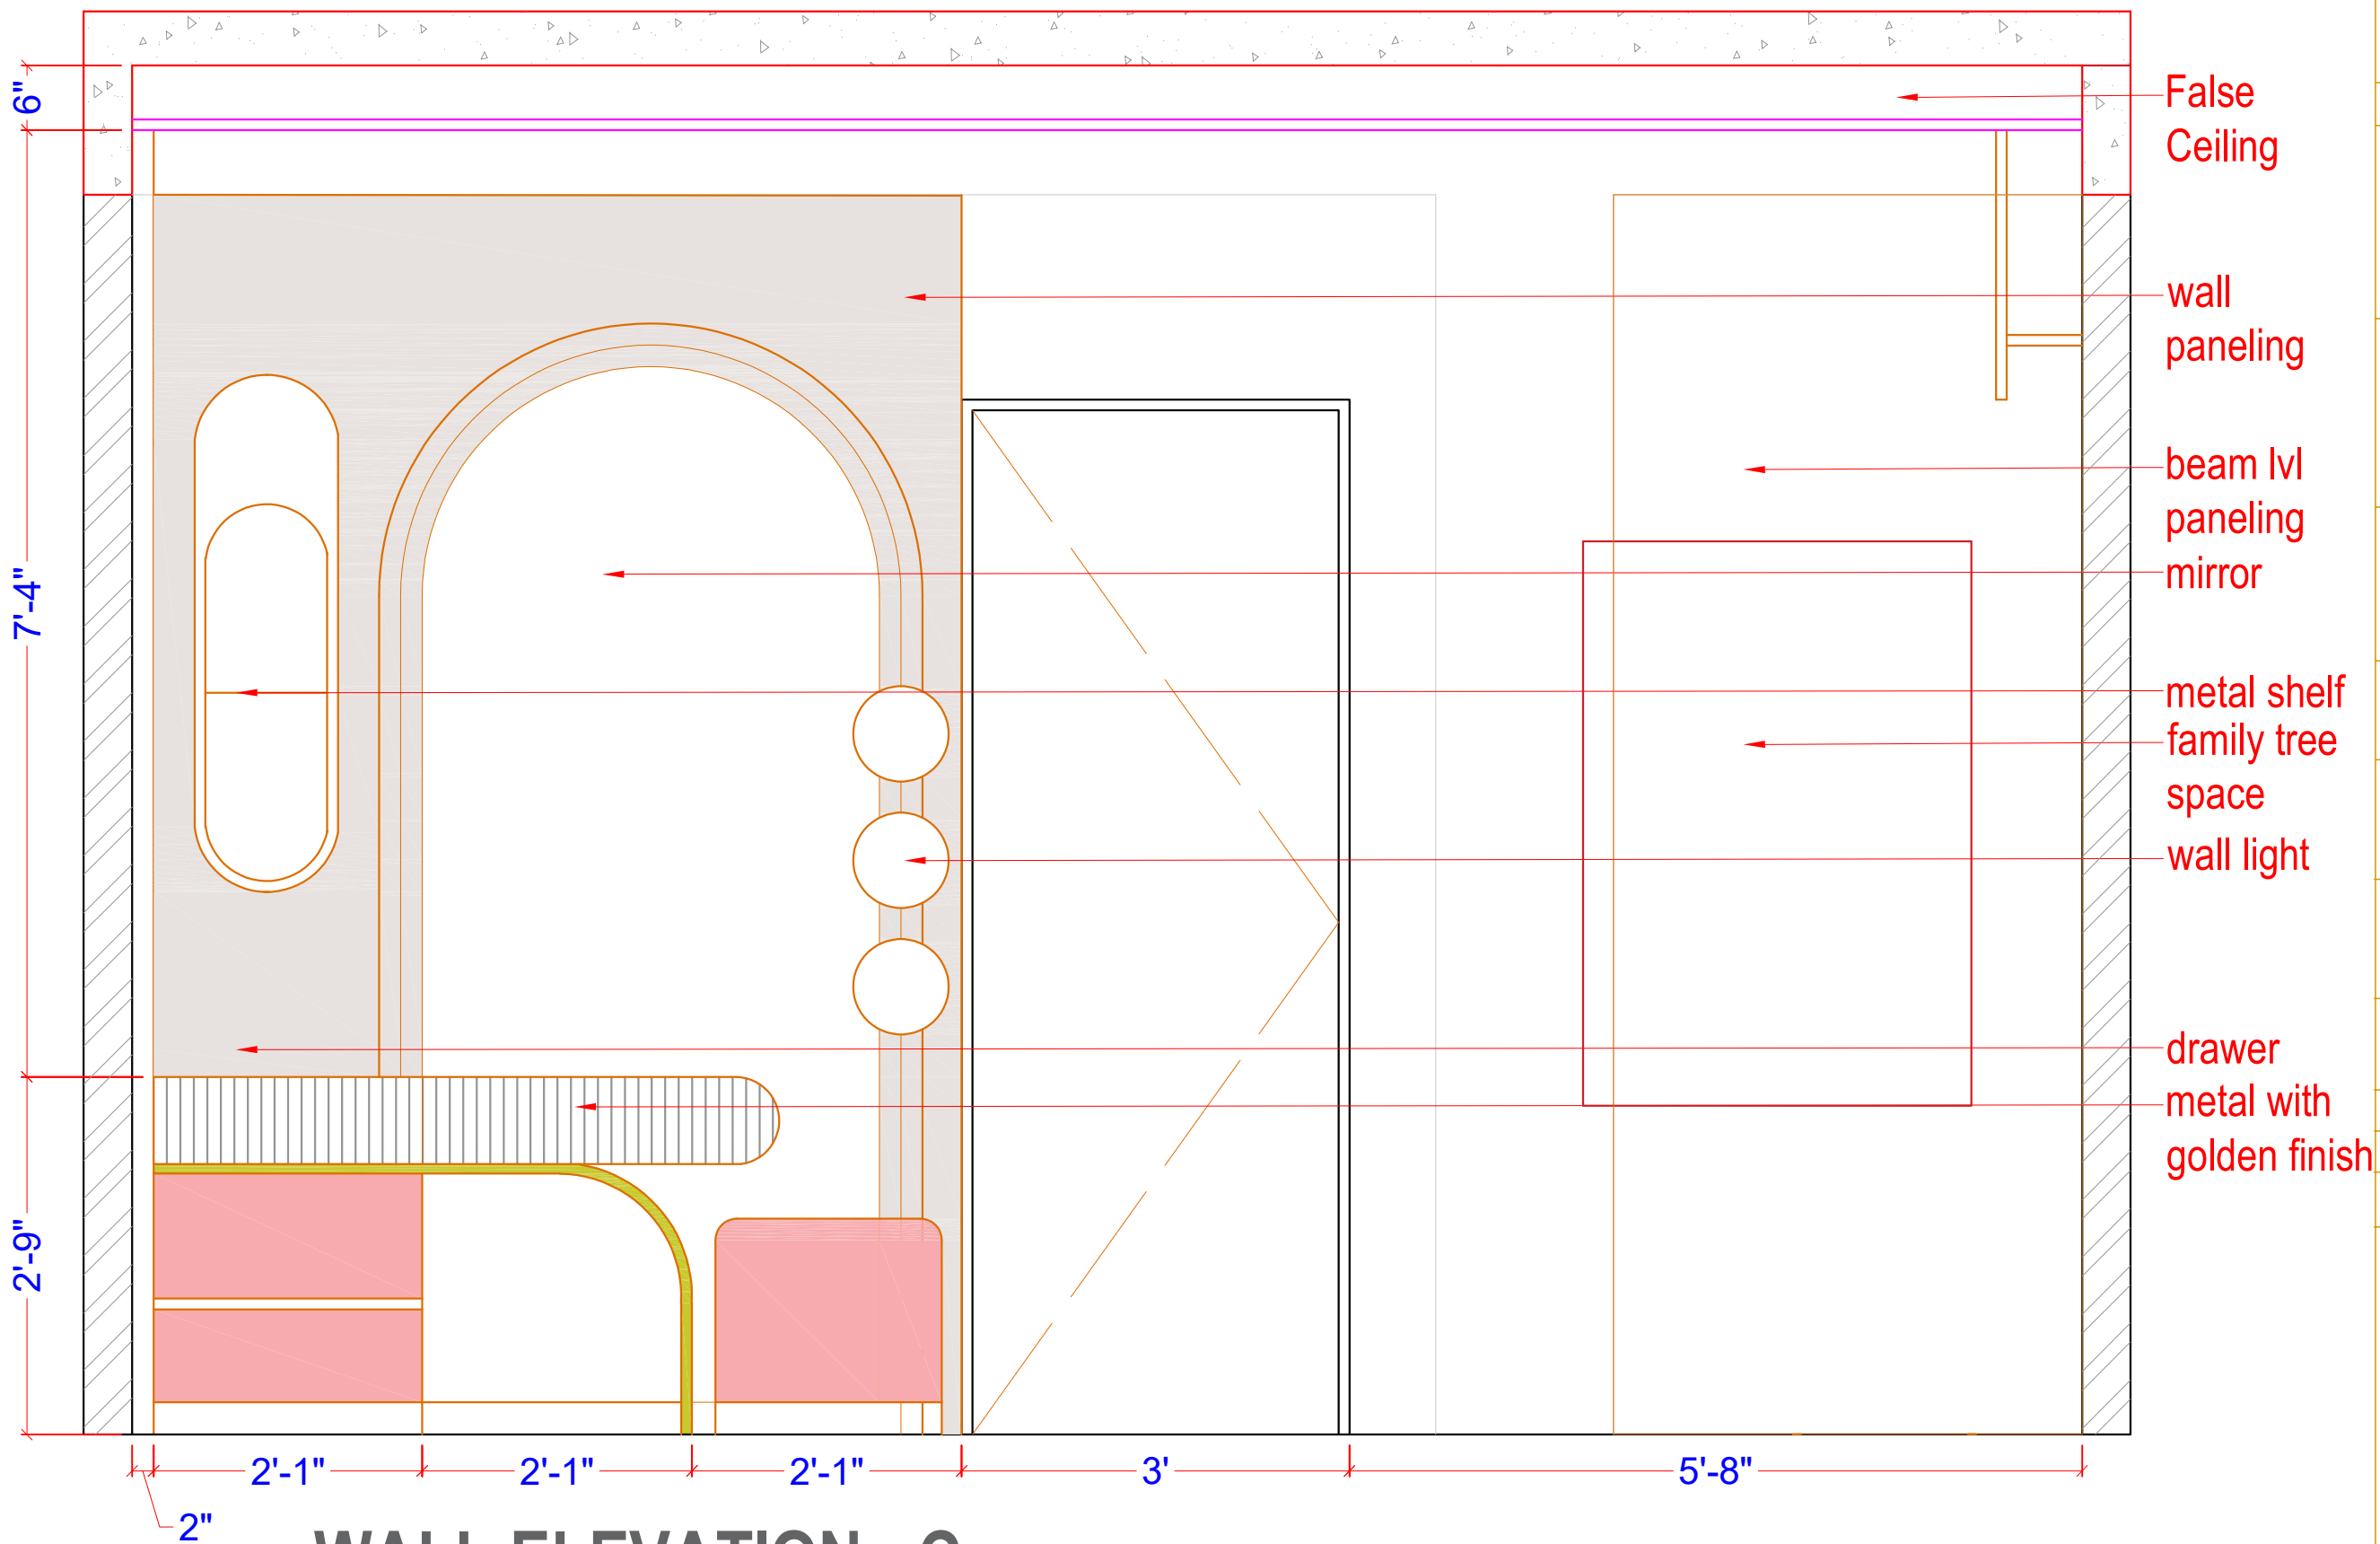

WALL ELEVATION - C

DRAWING TITLE :

MASTER BEDROOM-1
WALL ELEVATION

NOTES:

* DO NOT SCALE THE DRAWING.

* ALL DIMENSIONS ARE IN FEET \ INCHES.

* ANY DISCREPENCY IN THE DRAWING TO BE BROUGHT IN THE DESIGNER'S NOTICE BEFORE IMPLEMENTATION ON SITE.

SITE ADDRESS:

Vadodara

CLIENT NAME:

PANCHOLI'S

DATE:

06-06-2024

NORTH:

DRAWING DETAIL

REVISION NO.	R1 R2 R3
REVISED DATE:	05/03/26
SCALE:	N.T.S
DRAWN BY:	PRASANNA
CHECKED BY:	MITTAL

www.mayaspace.studio


mayaspace.studio@gmail.com

+918980144077

@mayaspace.studio

Maya

SPACE STUDIO

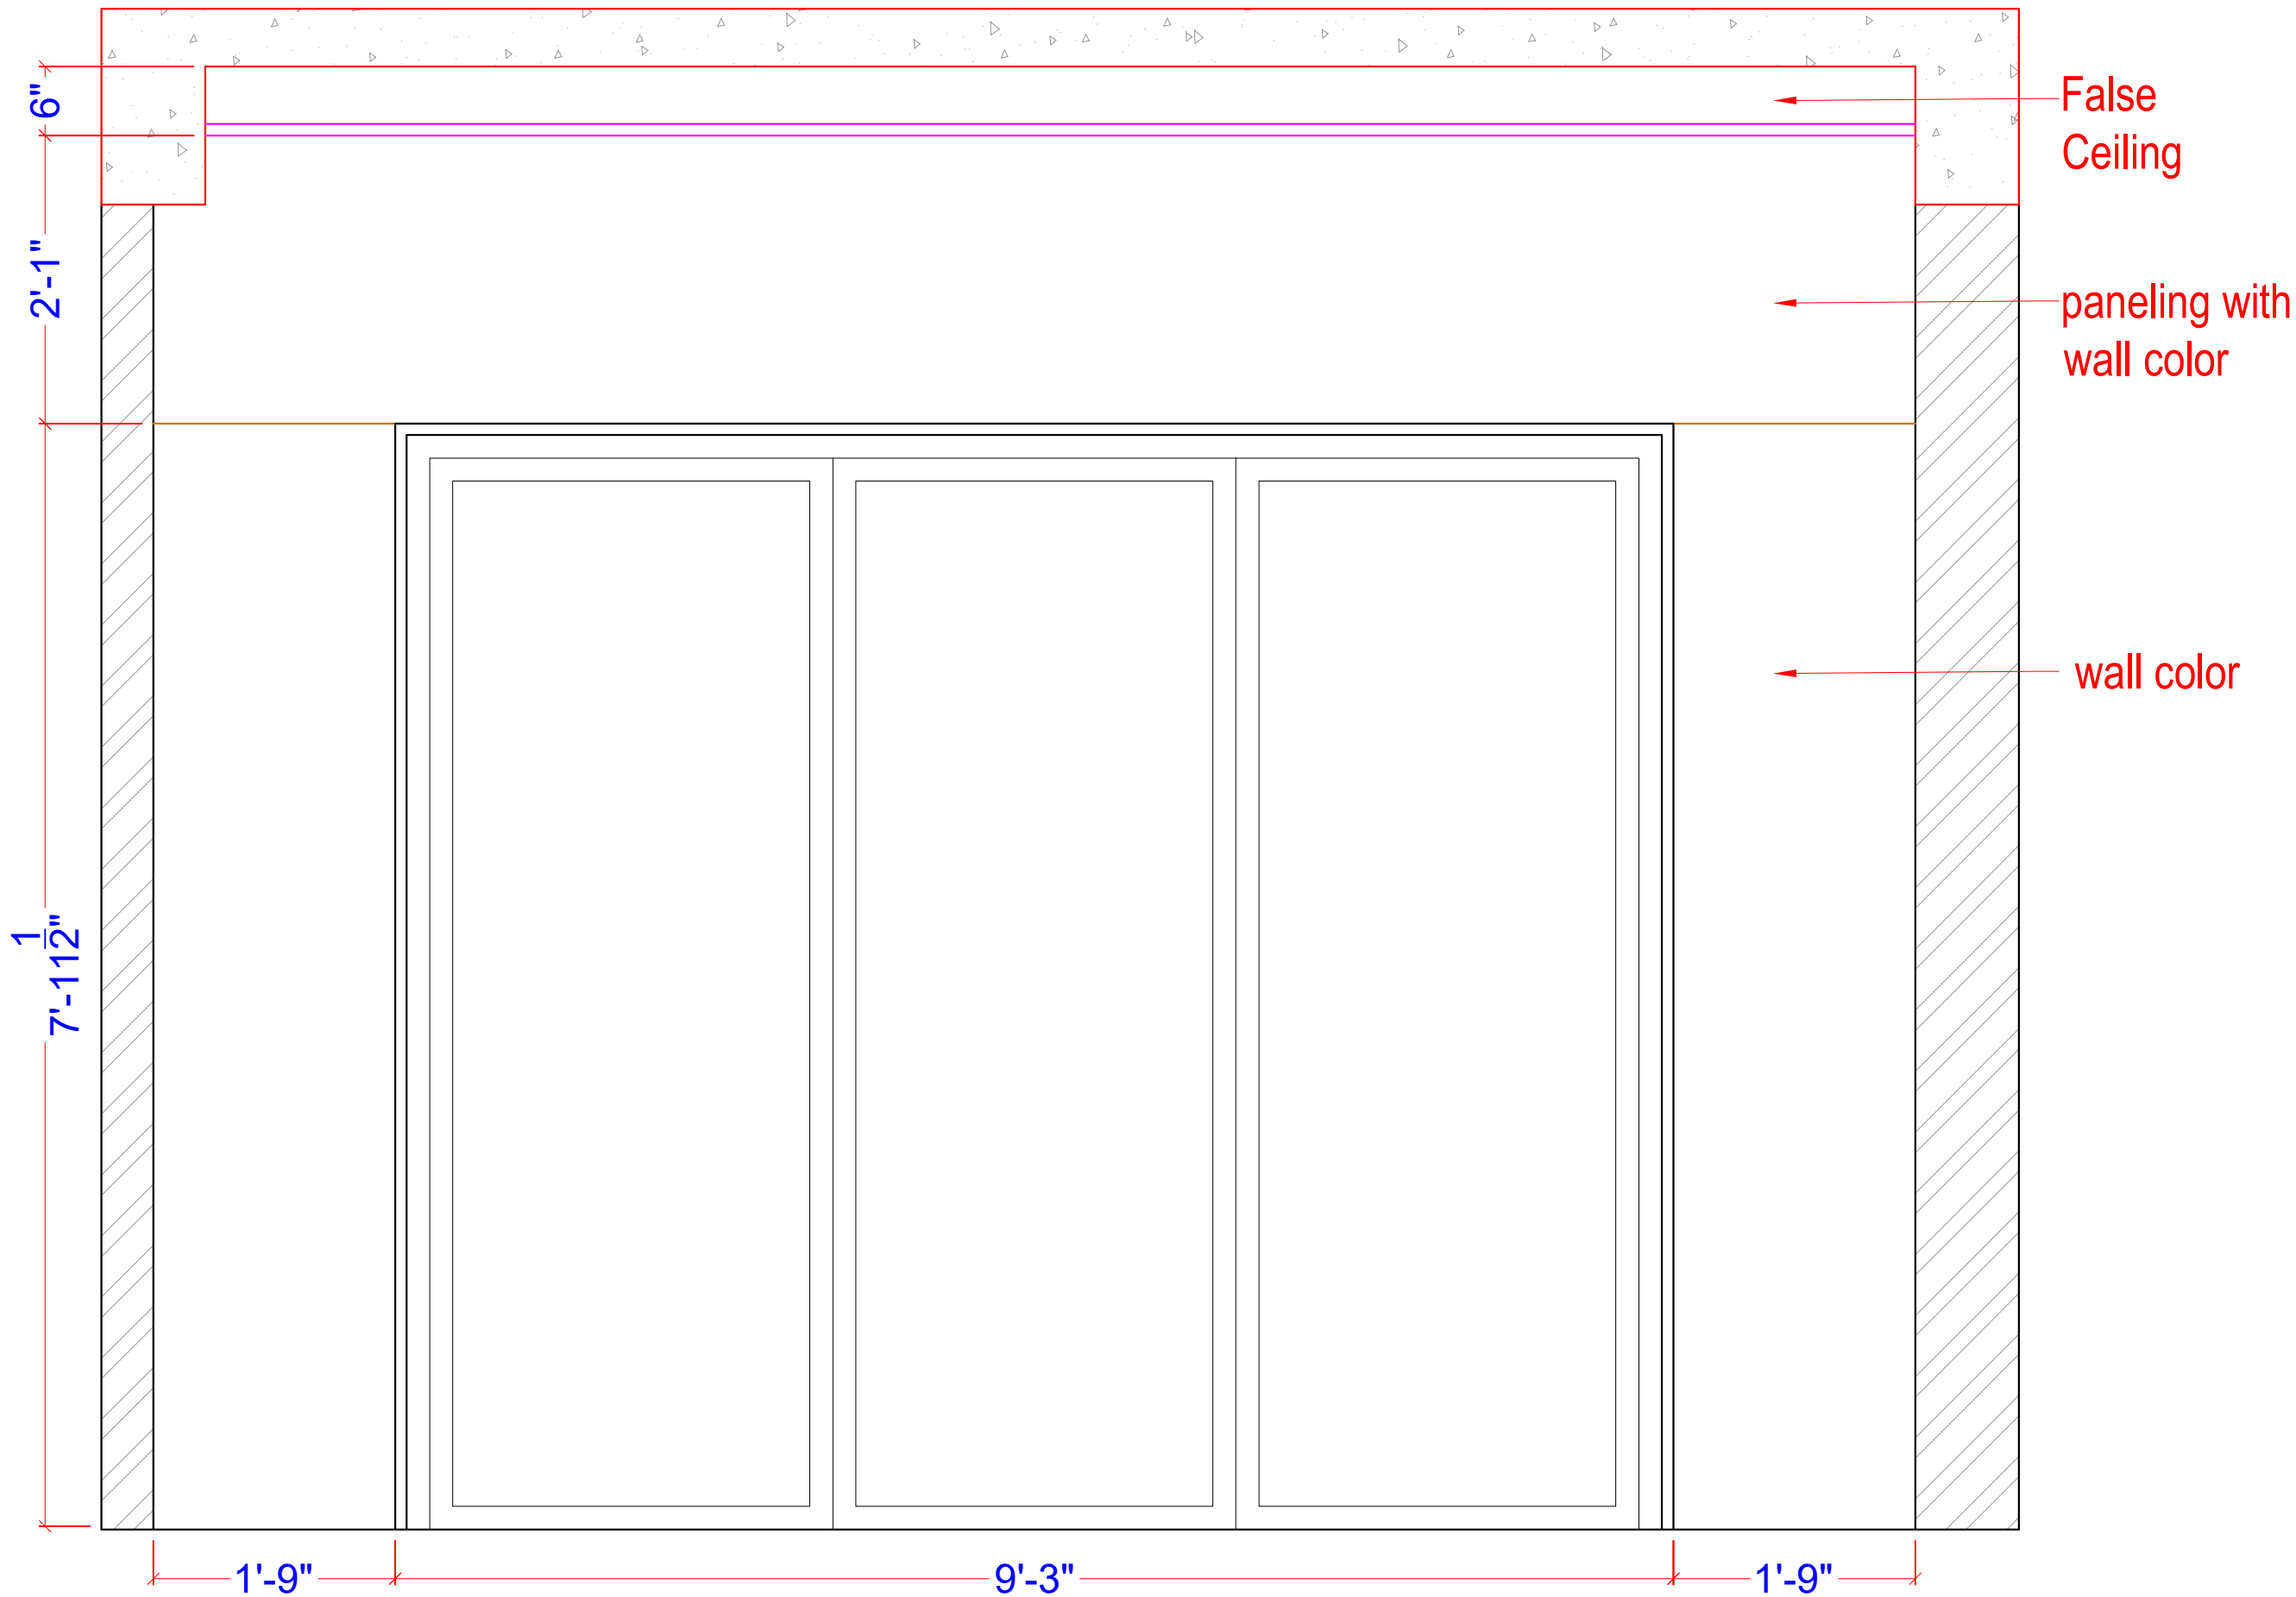

WALL ELEVATION - D

DRAWING TITLE :

MASTER BEDROOM-1
WALL ELEVATION

NOTES:

* DO NOT SCALE THE DRAWING.

* ALL DIMENSIONS ARE IN FEET \ INCHES.

* ANY DISCREPENCY IN THE DRAWING TO BE BROUGHT IN THE DESIGNER'S NOTICE BEFORE IMPLEMENTATION ON SITE.

SITE ADDRESS:

Vadodara

CLIENT NAME:

PANCHOLI'S

DATE:

06-06-2024

NORTH:

DRAWING DETAIL

REVISION NO.

R1

R2

R3

REVISED DATE:

05/03/26

SCALE:

N.T.S

DRAWN BY:

PRASANNA

CHECKED BY:

MITTAL

www.mayaspace.studio

mayaspace.studio@gmail.com

+918980144077

@mayaspace.studio

Maya
SPACE STUDIO