

DRAWING TITLE :

MASTER BEDROOM-1
WALL ELEVATION

NOTES:

- * DO NOT SCALE THE DRAWING.
- * ALL DIMENSIONS ARE IN FEET \ INCHES.
- * ANY DISCREPANCY IN THE DRAWING TO BE BROUGHT IN THE DESIGNERS NOTICE BEFORE IMPLEMENTATION ON SITE.

SITE ADDRESS:

Vadodara

CLIENT NAME:

PANCHOLI'S

DATE: 06-06-2024

NORTH:

DRAWING DETAIL


REVISION NO.	R1	R2	R3
REVISED DATE:	05/03/26		
SCALE:	N.T.S		
DRAWN BY:	PRASANNA		
CHECKED BY:	MITTAL		

www.mayaspace.studio

mayaspace.studio@gmail.com

[+918980144077](tel:+918980144077)

[@mayaspace.studio](https://www.instagram.com/mayaspace.studio)

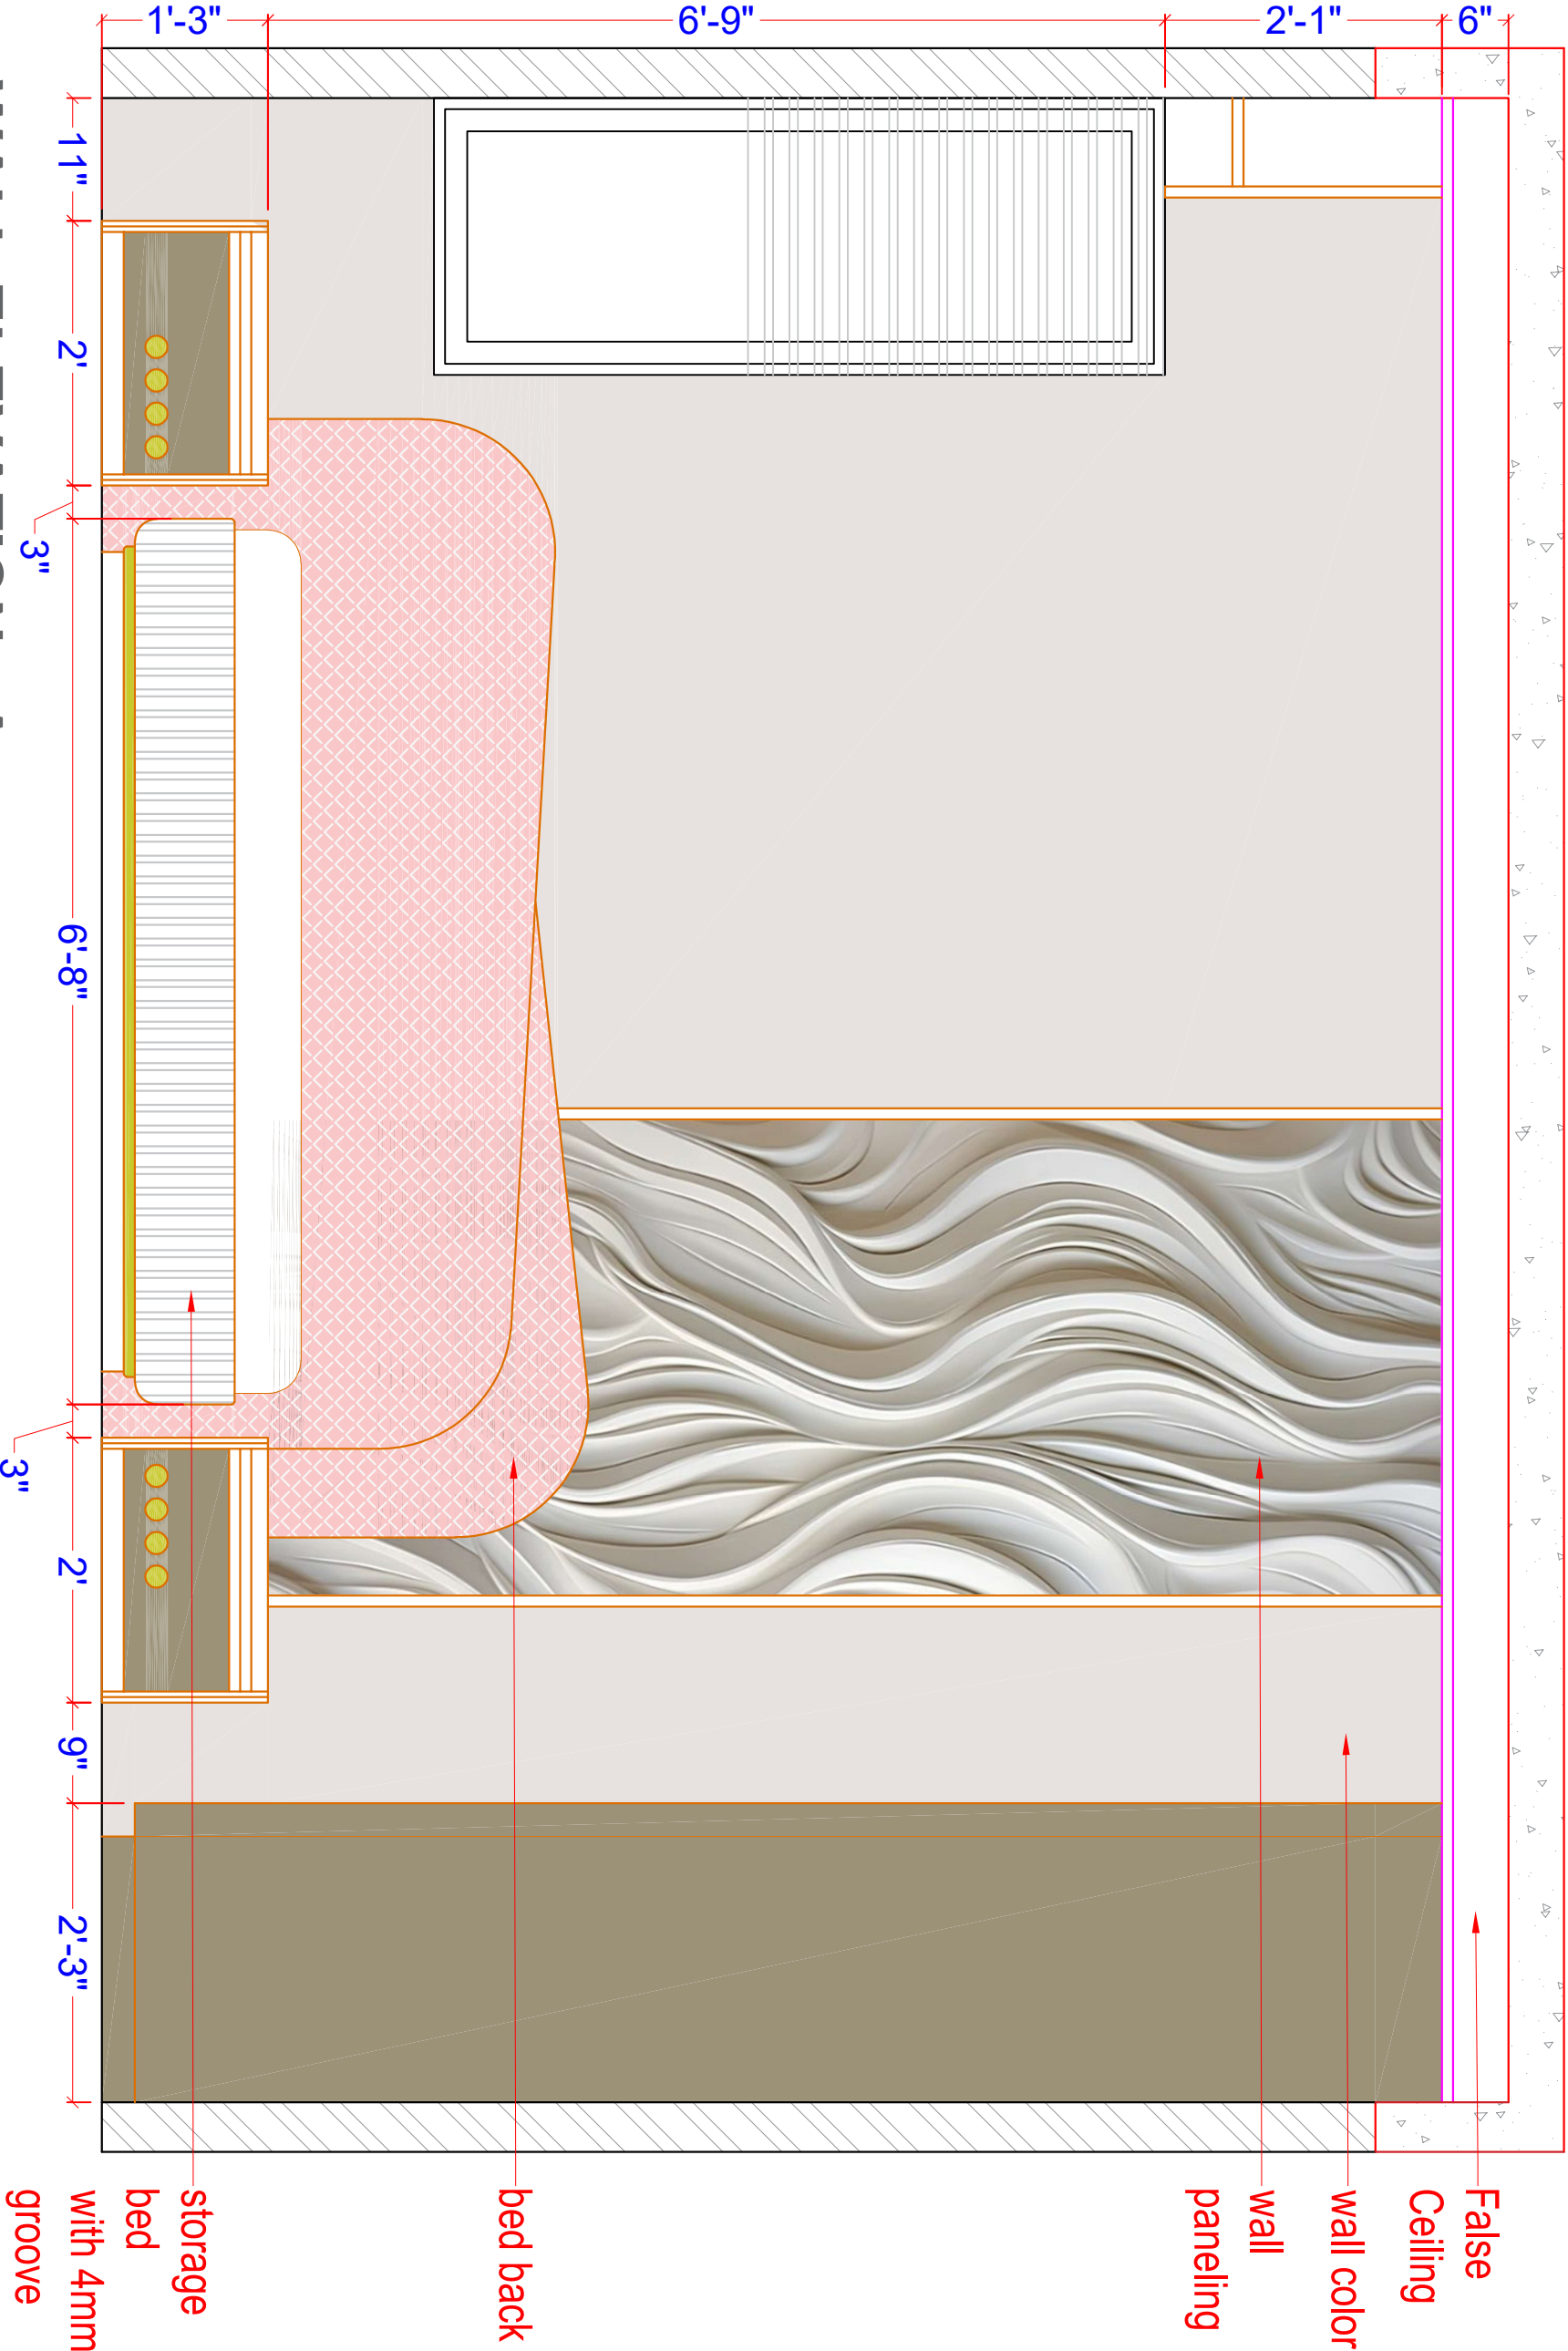

WALL ELEVATION - A