


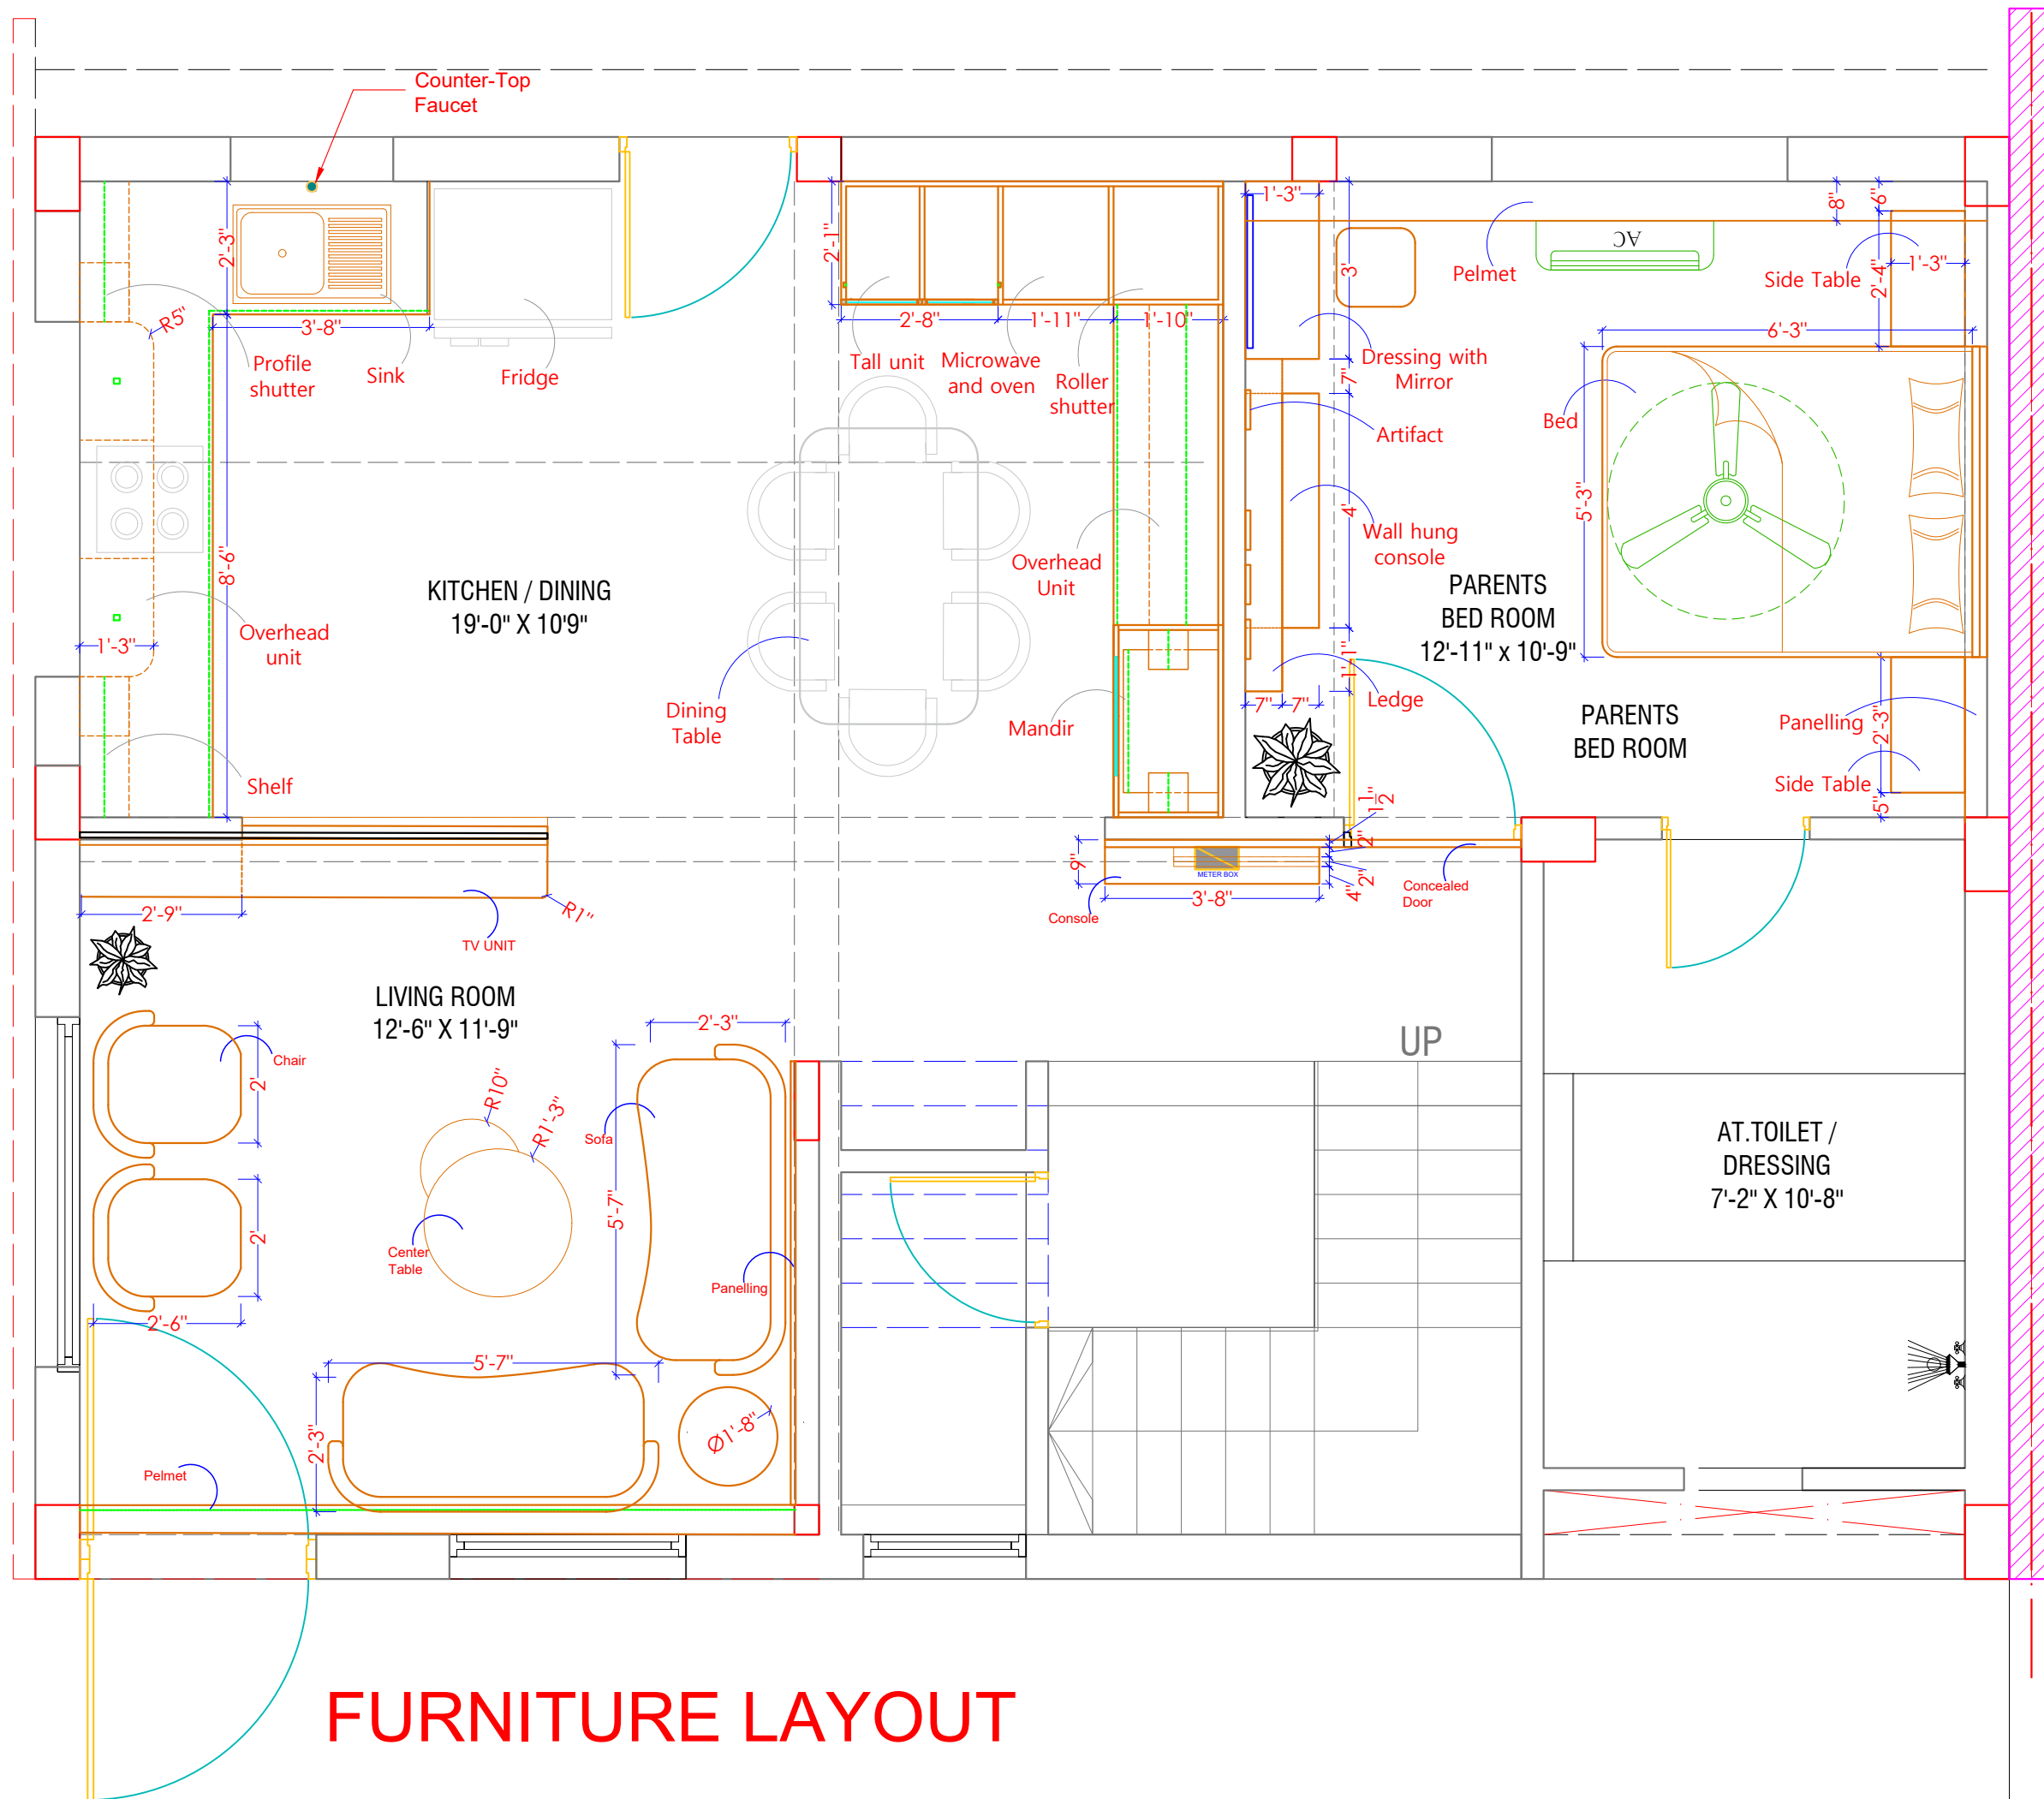

NOTES:

- * DO NOT SCALE THE DRAWING.
- * ALL DIMENSIONS ARE IN FEET \ INCHES.
- * ANY DISCREPANCY IN THE DRAWING TO BE BROUGHT IN THE DESIGNER'S NOTICE BEFORE IMPLEMENTATION ON SITE.

DRAWING TITLE :

LIVING ROOM FURNITURE LAYOUT

SITE ADDRESS:

SAVAD
VADODARA

CLIENT NAME:

RONAK PANCHOLI

DATE:

02-06-2025

NORTH:




DRAWING DETAIL

REVISION NO.	R1	R2	R3
REVISED DATE:	07/02/2026		
SCALE:	N.T.S		
DRAWN BY:	ARCHANA		
CHECKED BY:	MITTAL		

	www.mayaspace.studio
	mayaspace.studio@gmail.com
	+918980144077
	@mayaspace.studio



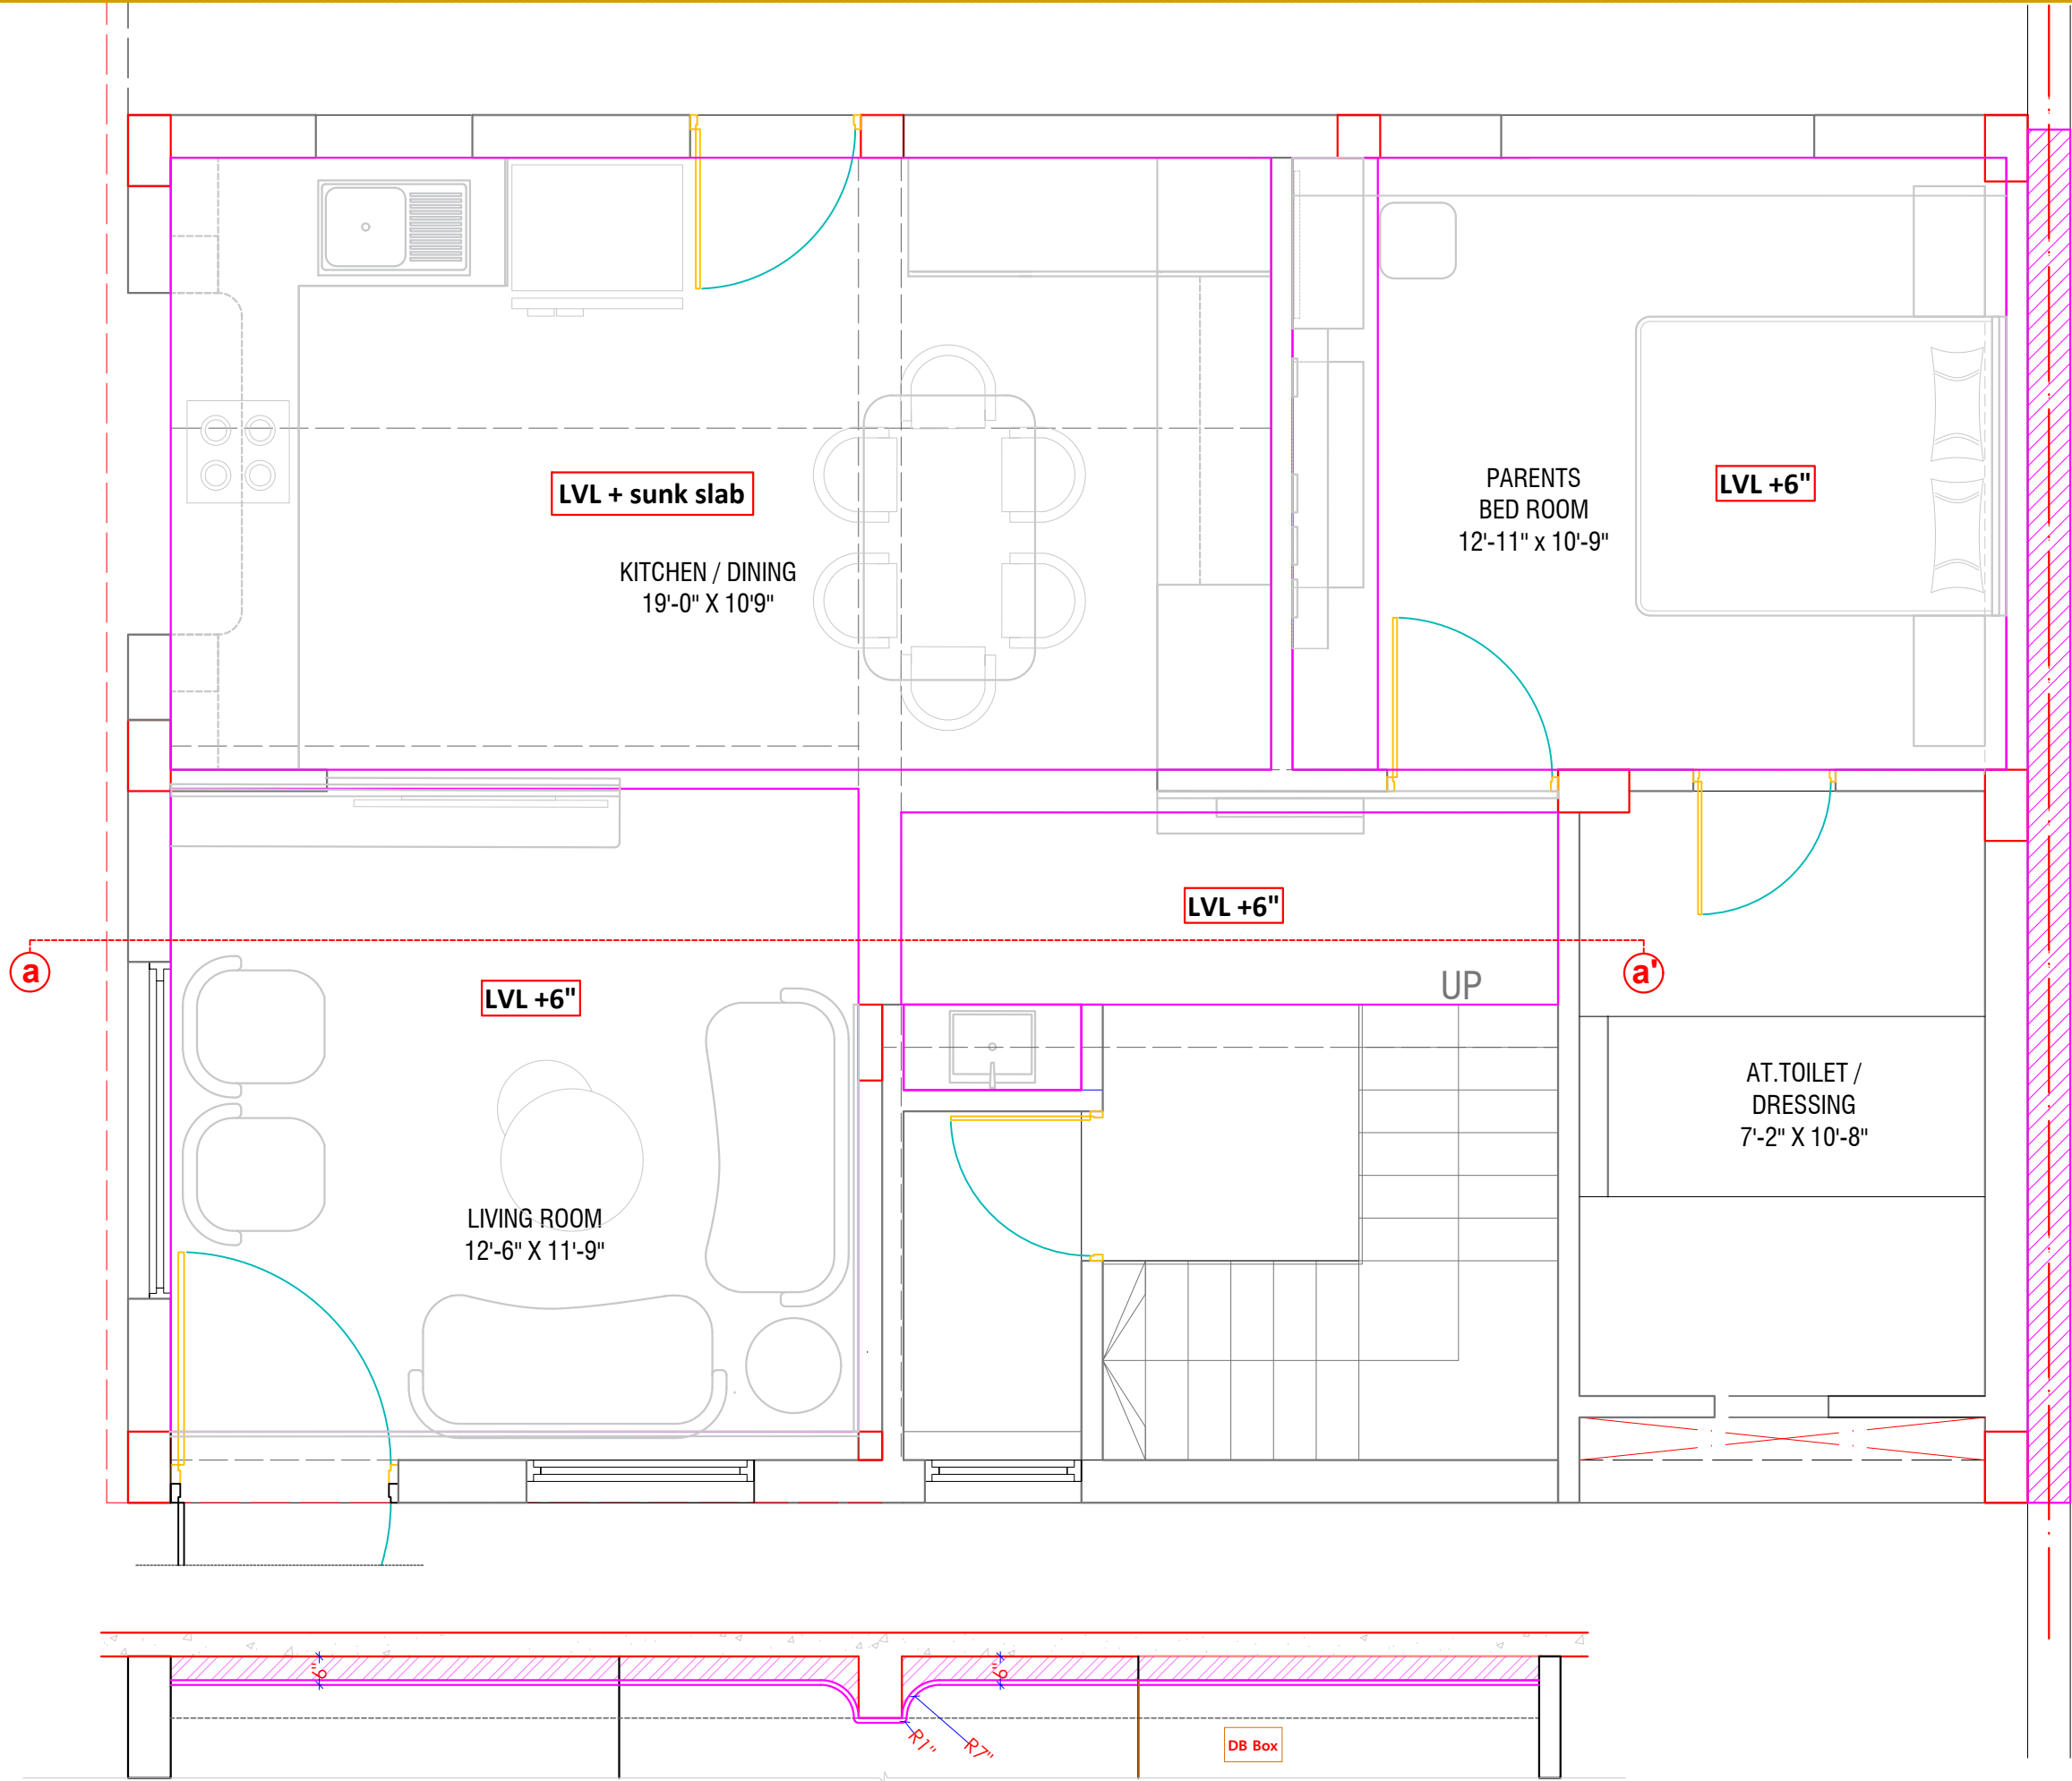

SECTION aa'

FALSE CEILING LAYOUT

DRAWING TITLE :

LIVING ROOM
FALSE CEILING LAYOUT

NOTES:

- * DO NOT SCALE THE DRAWING.
- * ALL DIMENSIONS ARE IN FEET \ INCHES.
- * ANY DISCREPENCY IN THE DRAWING TO BE BROUGHT IN THE DESIGNER'S NOTICE BEFORE IMPLEMENTATION ON SITE.

SITE ADDRESS:

SAVAD
VADODARA

CLIENT NAME:

RONAK PANCHOLI

DATE: 02-06-2025

NORTH:

DRAWING DETAIL

REVISION NO.	R1	R2	R3
REVISED DATE:	07/02/2026		
SCALE:	N.T.S		
DRAWN BY:	ARCHANA		
CHECKED BY:	MITTAL		

- www.mayaspace.studio
- mayaspace.studio@gmail.com
- +918980144077
- @mayaspace.studio



LIVING ROOM LIGHTING LAYOUT

- * DO NOT SCALE THE DRAWING.
- * ALL DIMENSIONS ARE IN FEET \ INCHES.
- * ANY DISCREPANCY IN THE DRAWING TO BE BROUGHT IN THE DESIGNER'S NOTICE BEFORE IMPLEMENTATION ON SITE.

SAVAD
VADODARA

RONAK PANCHOLI

NORTH:


DRAWING DETAIL

REVISION NO.	R1	R2	R3
REVISED DATE:	07/02/2026		
SCALE:	N.T.S		
DRAWN BY:	ARCHANA		
CHECKED BY:	MITTAL		

-  www.mayaspace.studio
-  mayaspace.studio@gmail.com
-  +918980144077
-  @mayaspace.studio



LIGHTING LAYOUT

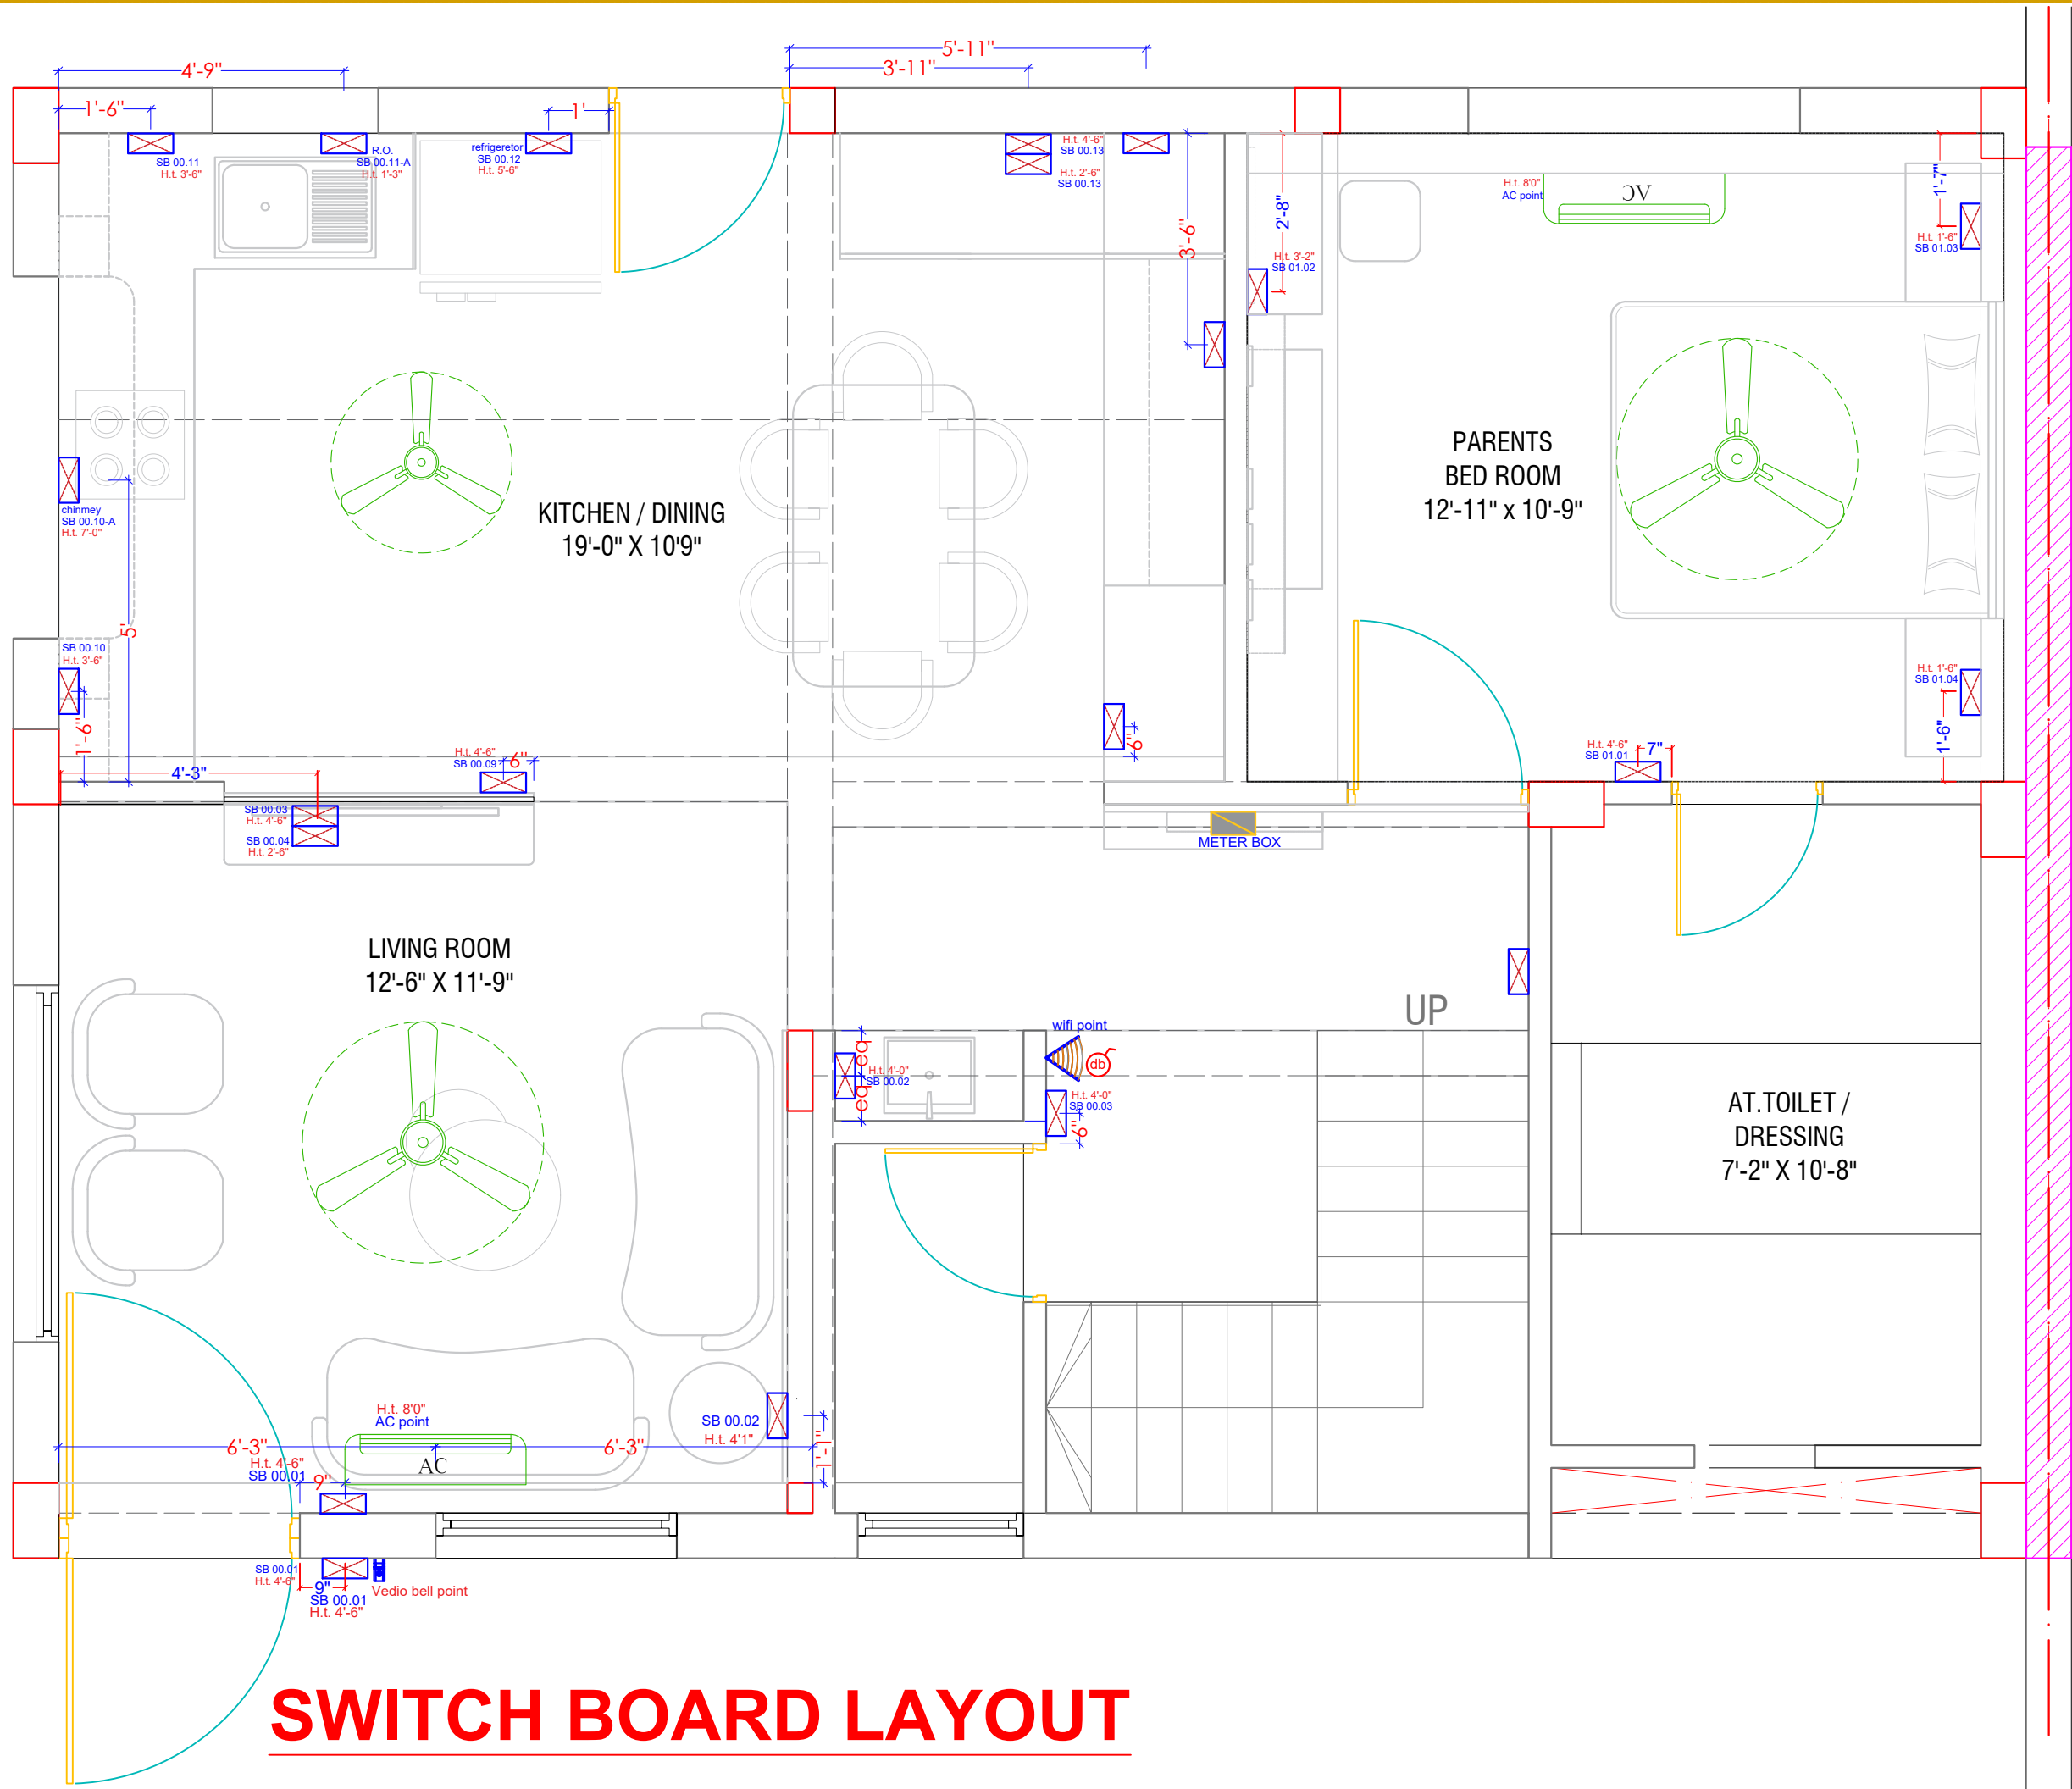

SWITCH BOARD LAYOUT

DRAWING TITLE :

LIVING ROOM
SWITCH BOARD LAYOUT

NOTES:

* DO NOT SCALE THE DRAWING.
* ALL DIMENSIONS ARE IN FEET \ INCHES.
* ANY DISCREPENCY IN THE DRAWING
TO BE BROUGHT IN THE DESIGNER'S
NOTICE BEFORE IMPLEMENTATION
ON SITE.

SITE ADDRESS:

SAVAD
VADODARA

CLIENT NAME:

RONAK PANCHOLI


DATE:	02-06-2025
NORTH:	

DRAWING DETAIL

REVISION NO.	R1 R2 R3
REVISED DATE:	07/02/2026
SCALE:	N.T.S
DRAWN BY:	ARCHANA
CHECKED BY:	MITTAL

- www.mayaspace.studio
- mayaspace.studio@gmail.com
- +918980144077
- @mayaspace.studio



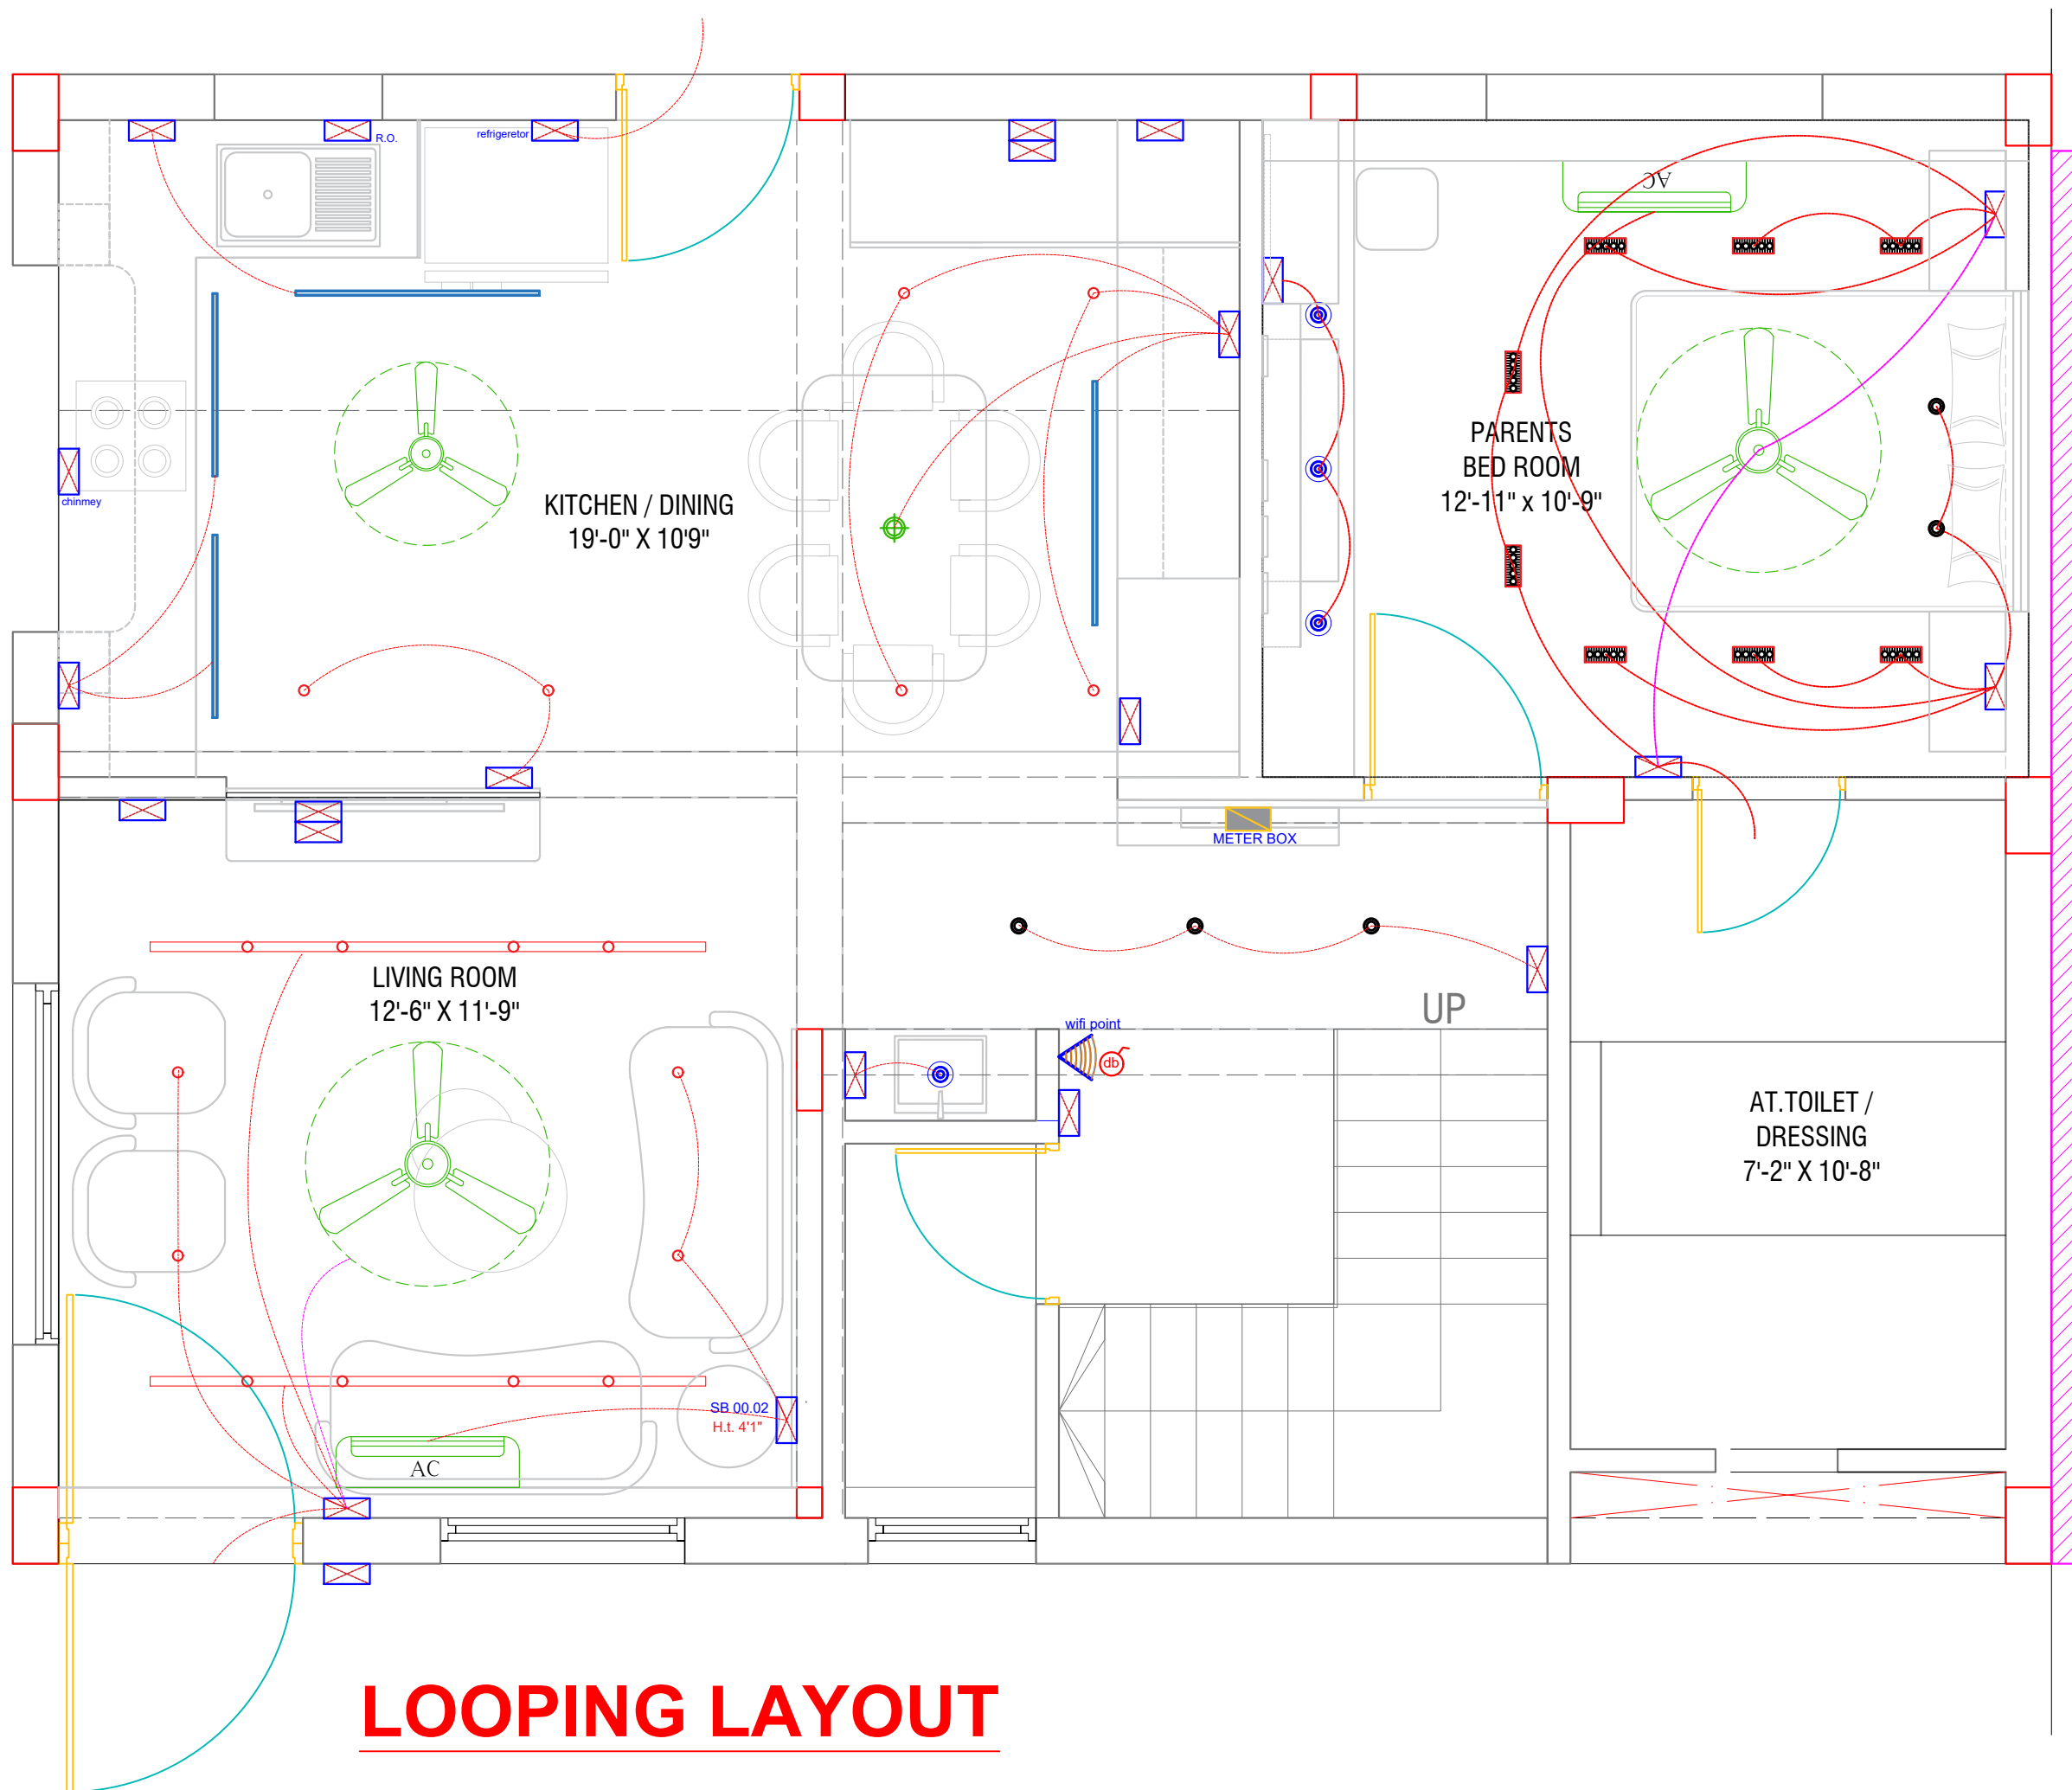

LOOPING LAYOUT

DRAWING TITLE :

LIVING ROOM
LOOPING LAYOUT

NOTES:

- * DO NOT SCALE THE DRAWING.
- * ALL DIMENSIONS ARE IN FEET \ INCHES.
- * ANY DISCREPANCY IN THE DRAWING TO BE BROUGHT IN THE DESIGNER'S NOTICE BEFORE IMPLEMENTATION ON SITE.

SITE ADDRESS:

SAVAD
VADODARA

CLIENT NAME:

RONAK PANCHOLI

DATE: 02-06-2025


NORTH:

DRAWING DETAIL

REVISION NO.	R1	R2	R3
REVISED DATE:	07/02/2026		
SCALE:	N.T.S		
DRAWN BY:	ARCHANA		
CHECKED BY:	MITTAL		

www.mayaspace.studio
mayaspace.studio@gmail.com
+918980144077
@mayaspace.studio



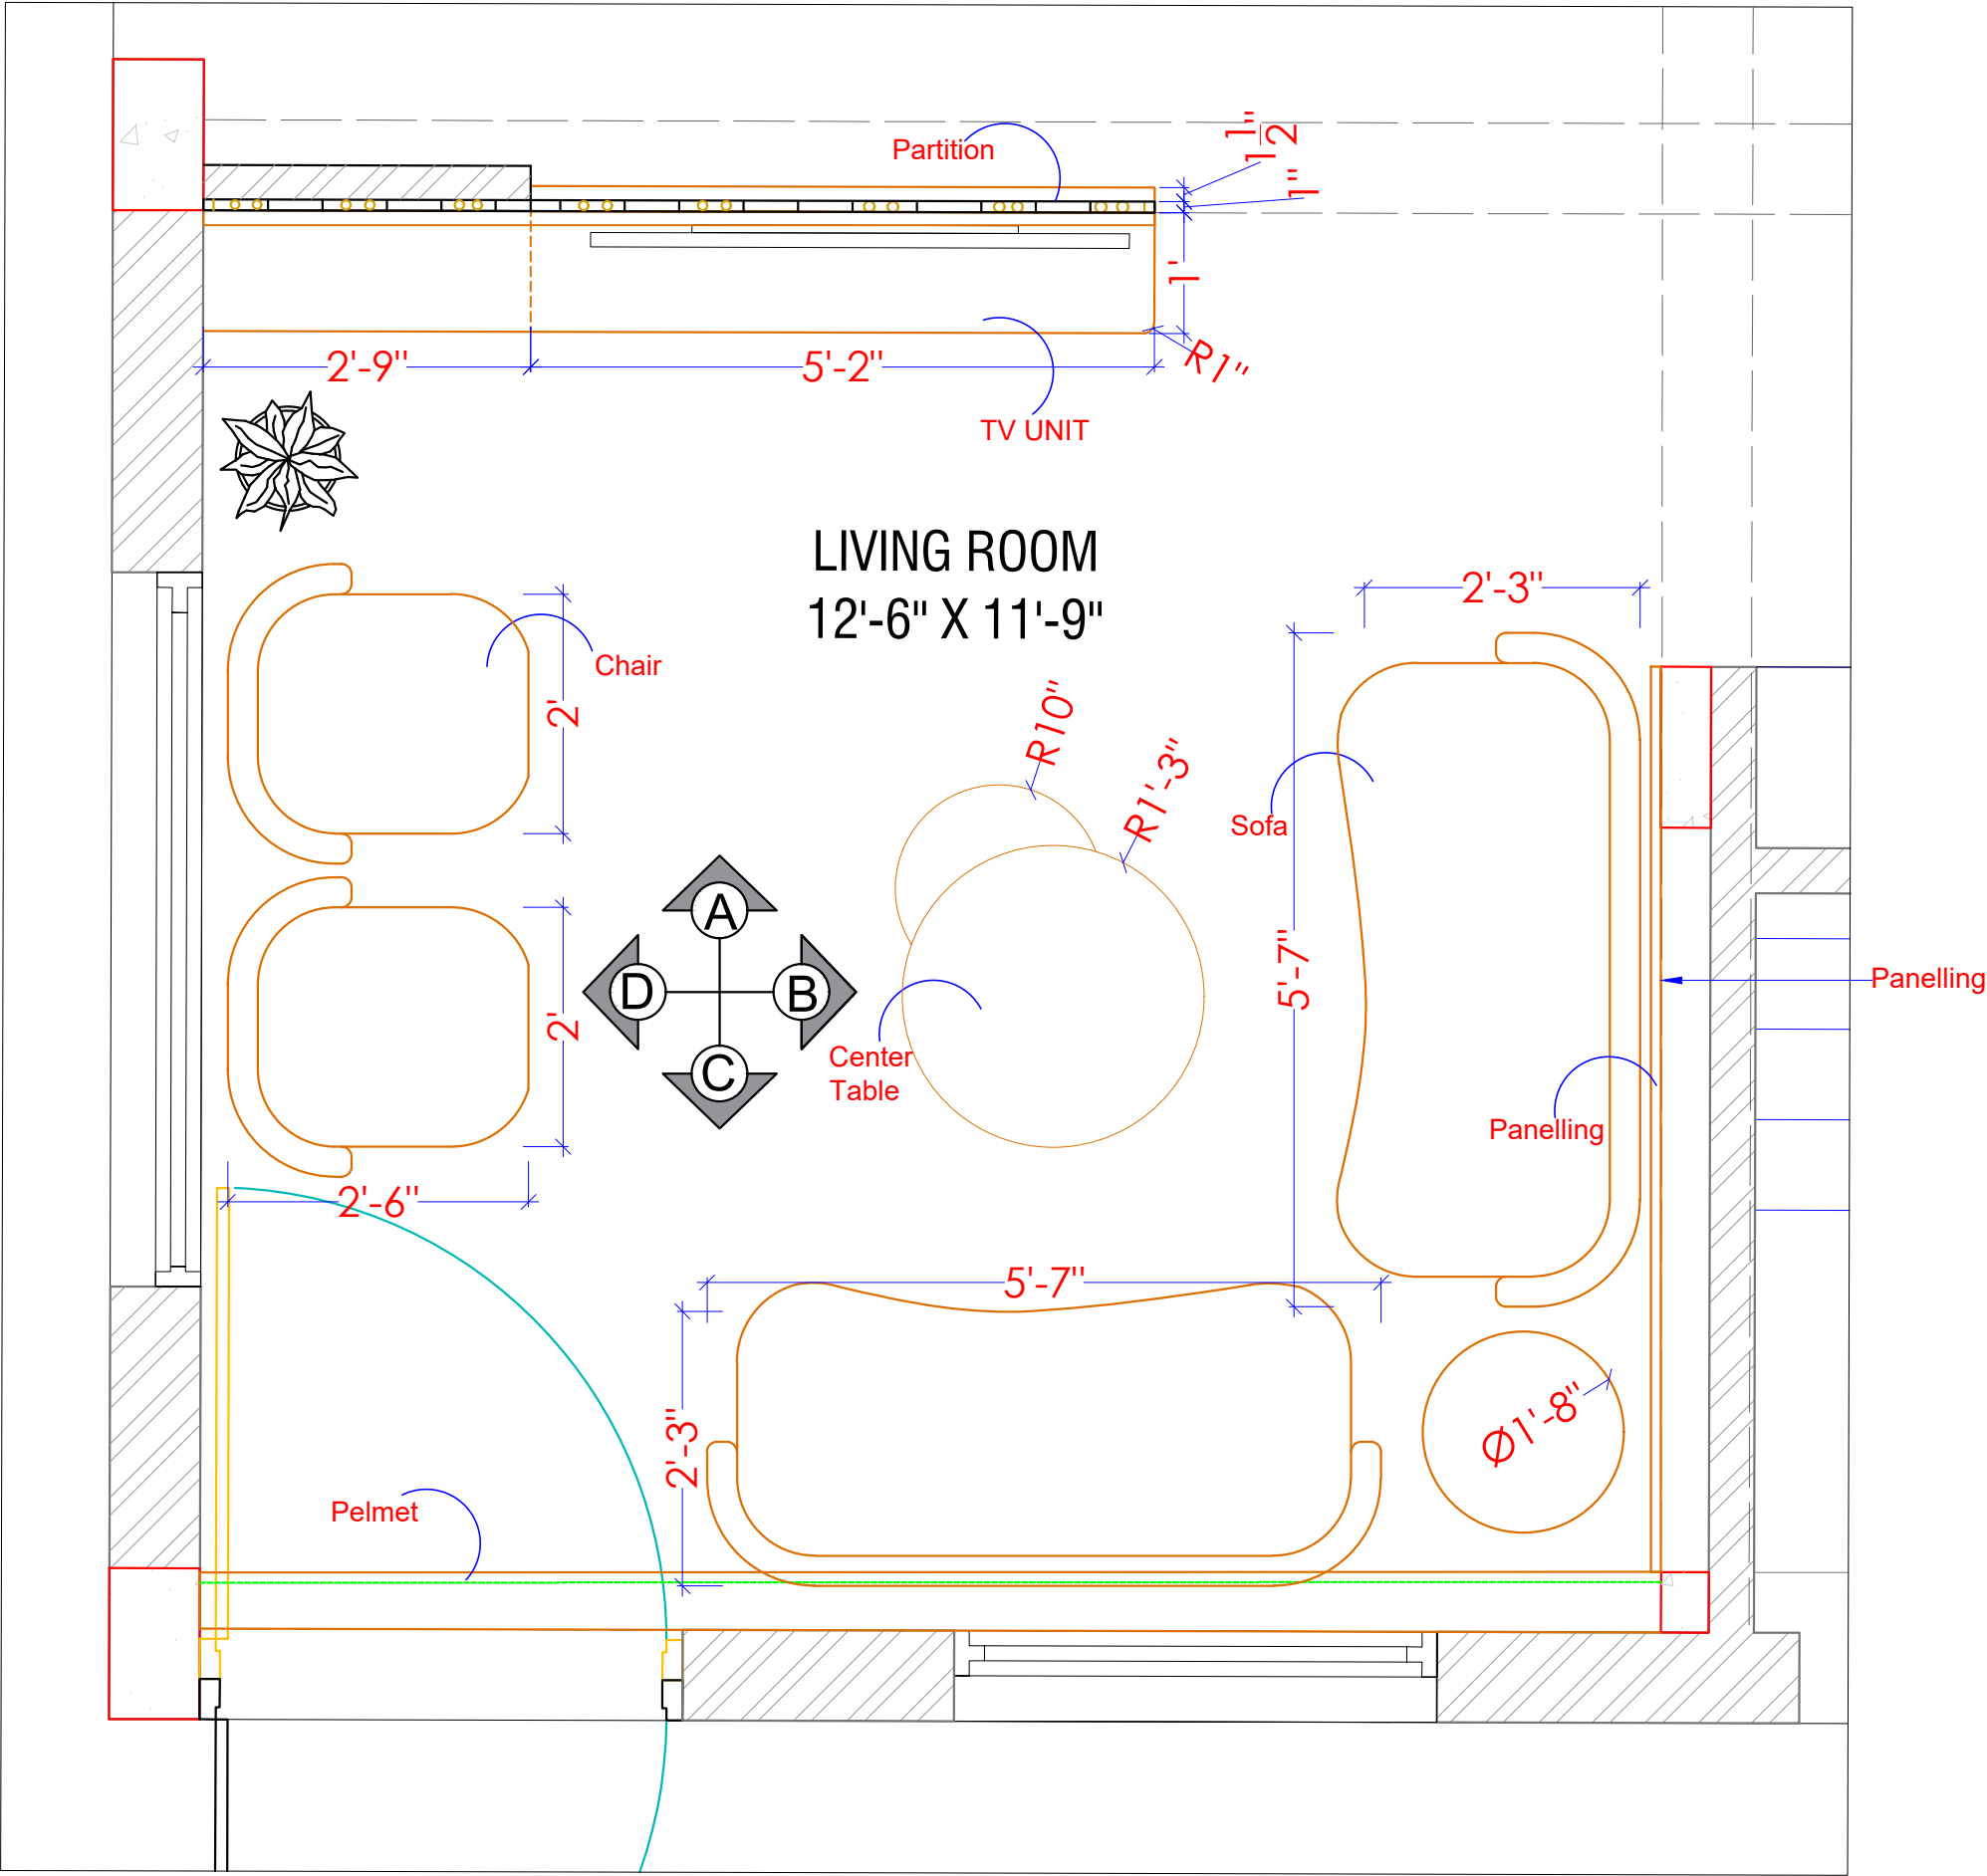

PLAN

DRAWING TITLE :

LIVING ROOM
FURNITURE LAYOUT

NOTES:

- * DO NOT SCALE THE DRAWING.
- * ALL DIMENSIONS ARE IN FEET \ INCHES.
- * ANY DISCREPANCY IN THE DRAWING TO BE BROUGHT IN THE DESIGNER'S NOTICE BEFORE IMPLEMENTATION ON SITE.

SITE ADDRESS:

SAVAD
VADODARA

CLIENT NAME:

RONAK PANCHOLI

DATE: 02-06-2025



NORTH:

DRAWING DETAIL

REVISION NO.	R1	R2	R3
REVISED DATE:	07/02/2026		
SCALE:	N.T.S		
DRAWN BY:	ARCHANA		
CHECKED BY:	MITTAL		

	www.mayaspace.studio
	mayaspace.studio@gmail.com
	+918980144077
	@mayaspace.studio



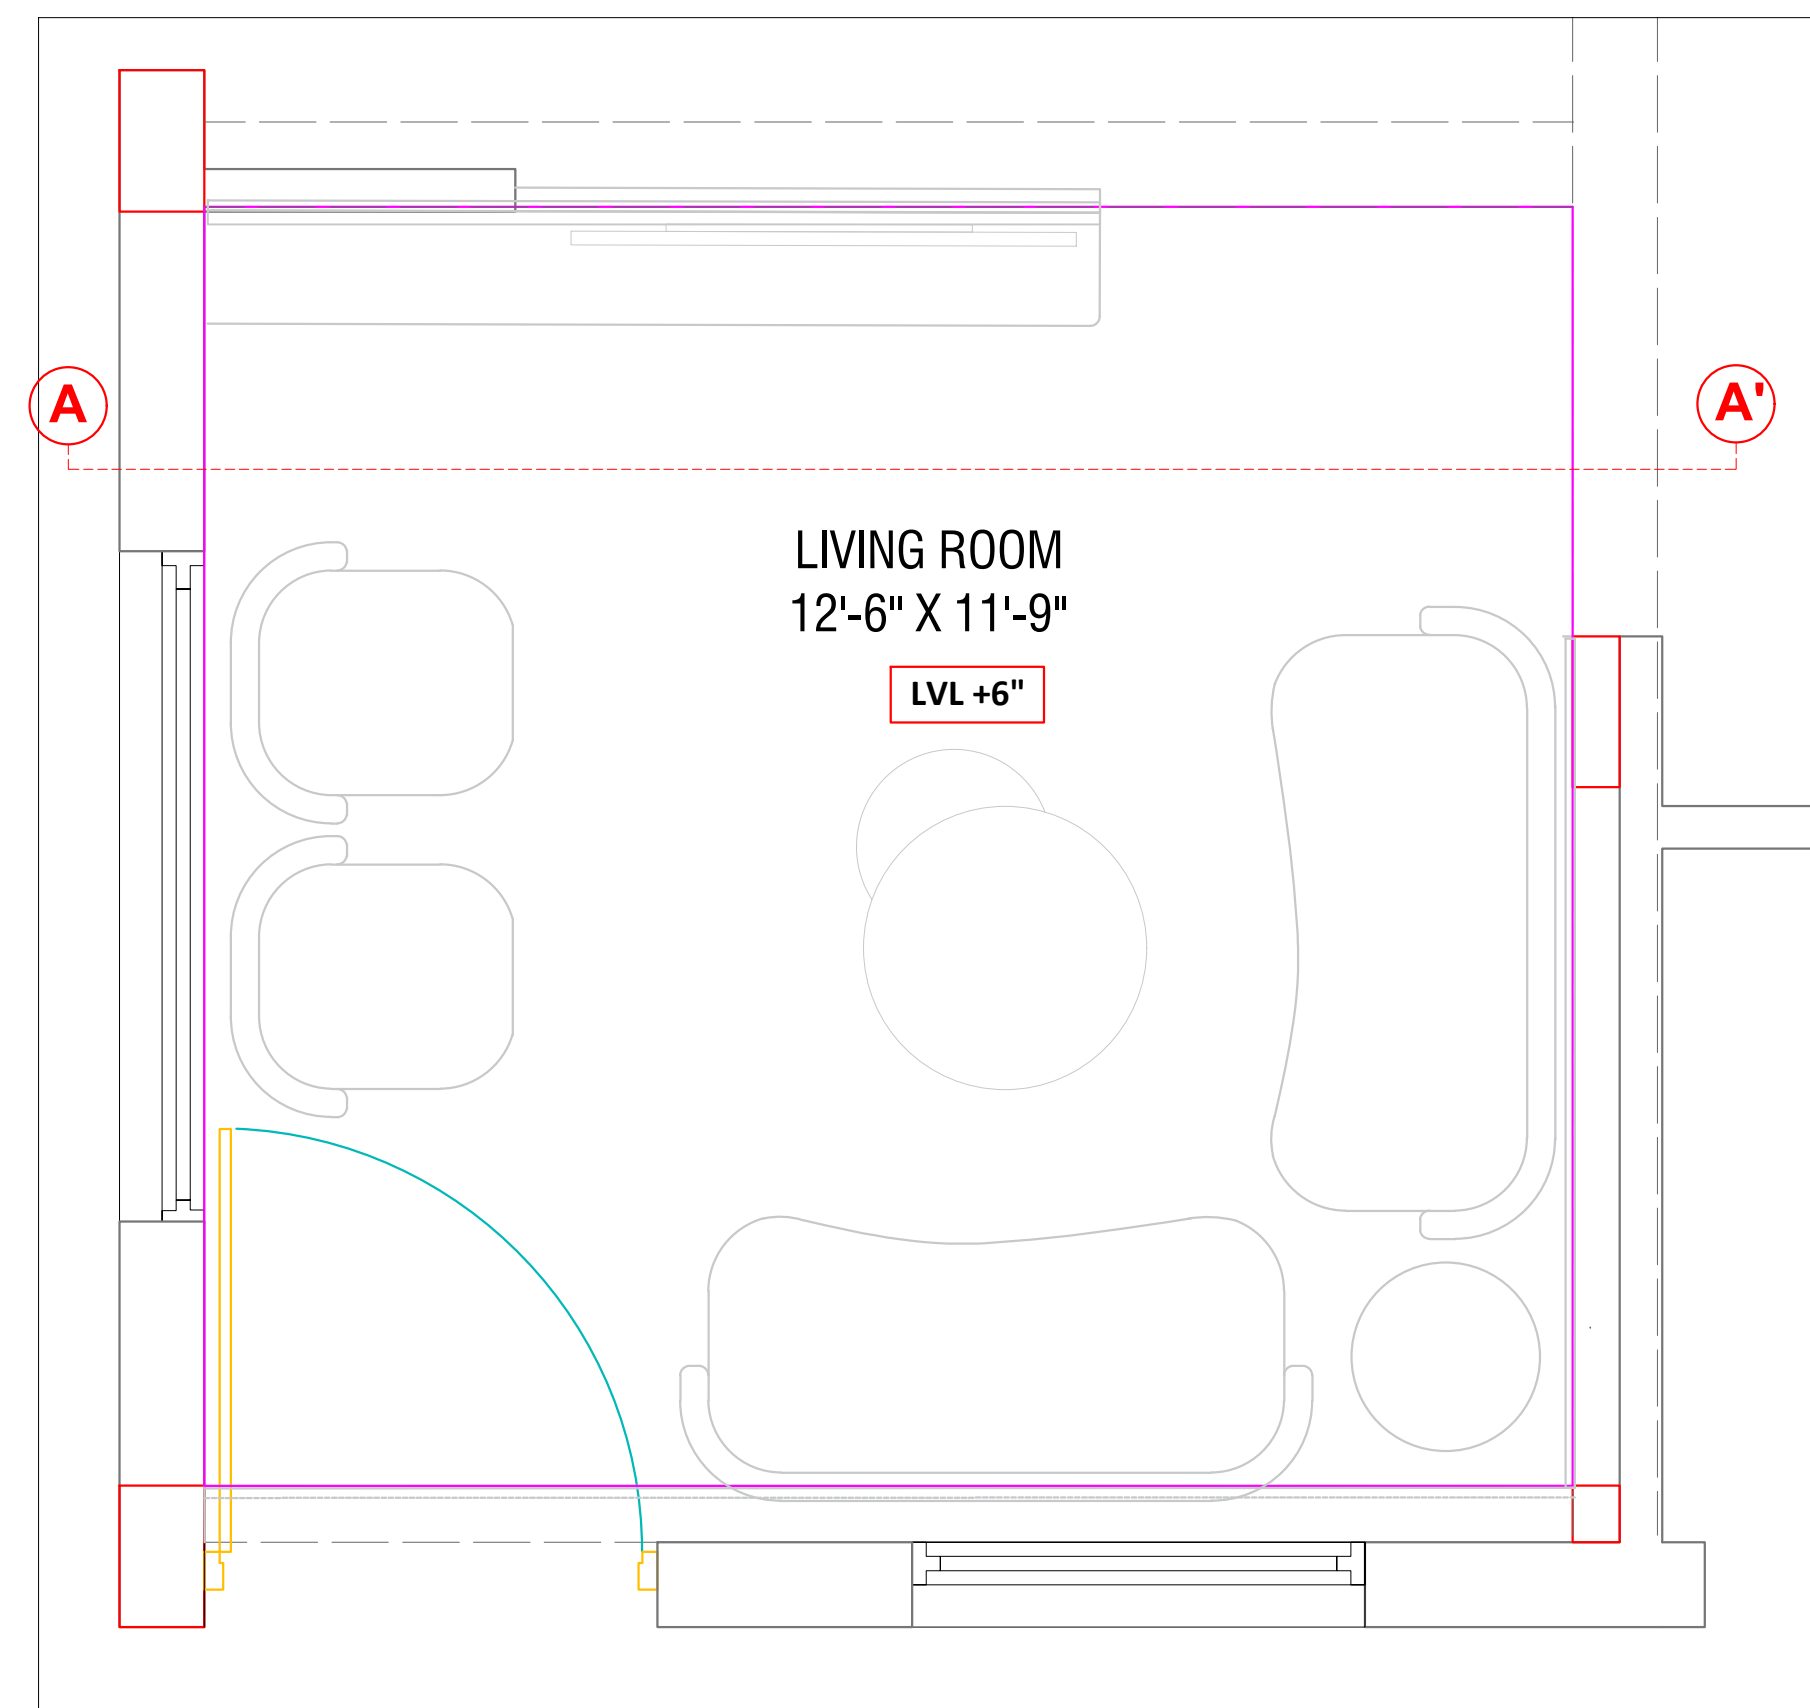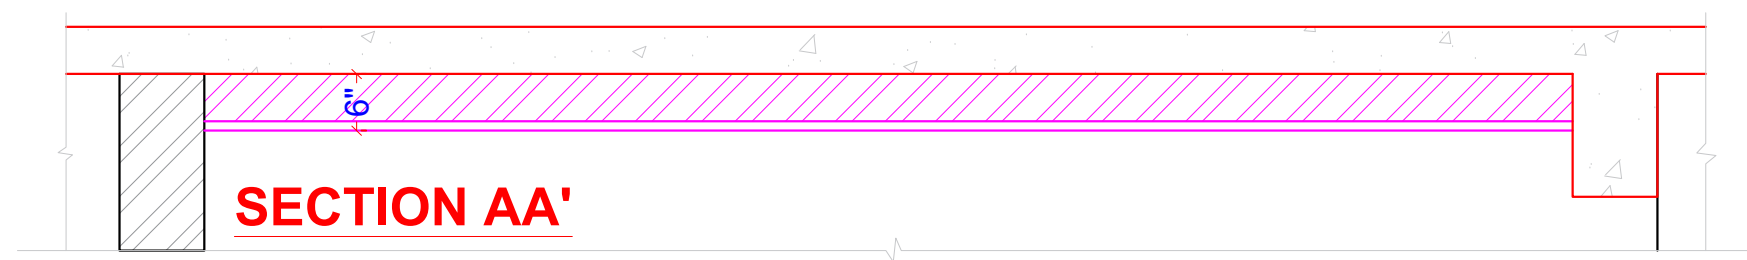

FALSE CEILING LAYOUT

DRAWING TITLE :

**LIVING ROOM
FALSE CEILING LAYOUT**

NOTES:

- * DO NOT SCALE THE DRAWING.
- * ALL DIMENSIONS ARE IN FEET \ INCHES.
- * ANY DISCREPENCY IN THE DRAWING TO BE BROUGHT IN THE DESIGNER'S NOTICE BEFORE IMPLEMENTATION ON SITE.

SITE ADDRESS:

**SAVAD
VADODARA**

CLIENT NAME:

RONAK PANCHOLI

DATE:

02-06-2025


NORTH:

DRAWING DETAIL

REVISION NO.	☐ R1 ☐ R2 ☐ R3
REVISED DATE:	07/02/2026
SCALE:	N.T.S
DRAWN BY:	ARCHANA
CHECKED BY:	MITTAL

	www.mayaspace.studio
	mayaspace.studio@gmail.com
	+918980144077
	@mayaspace.studio



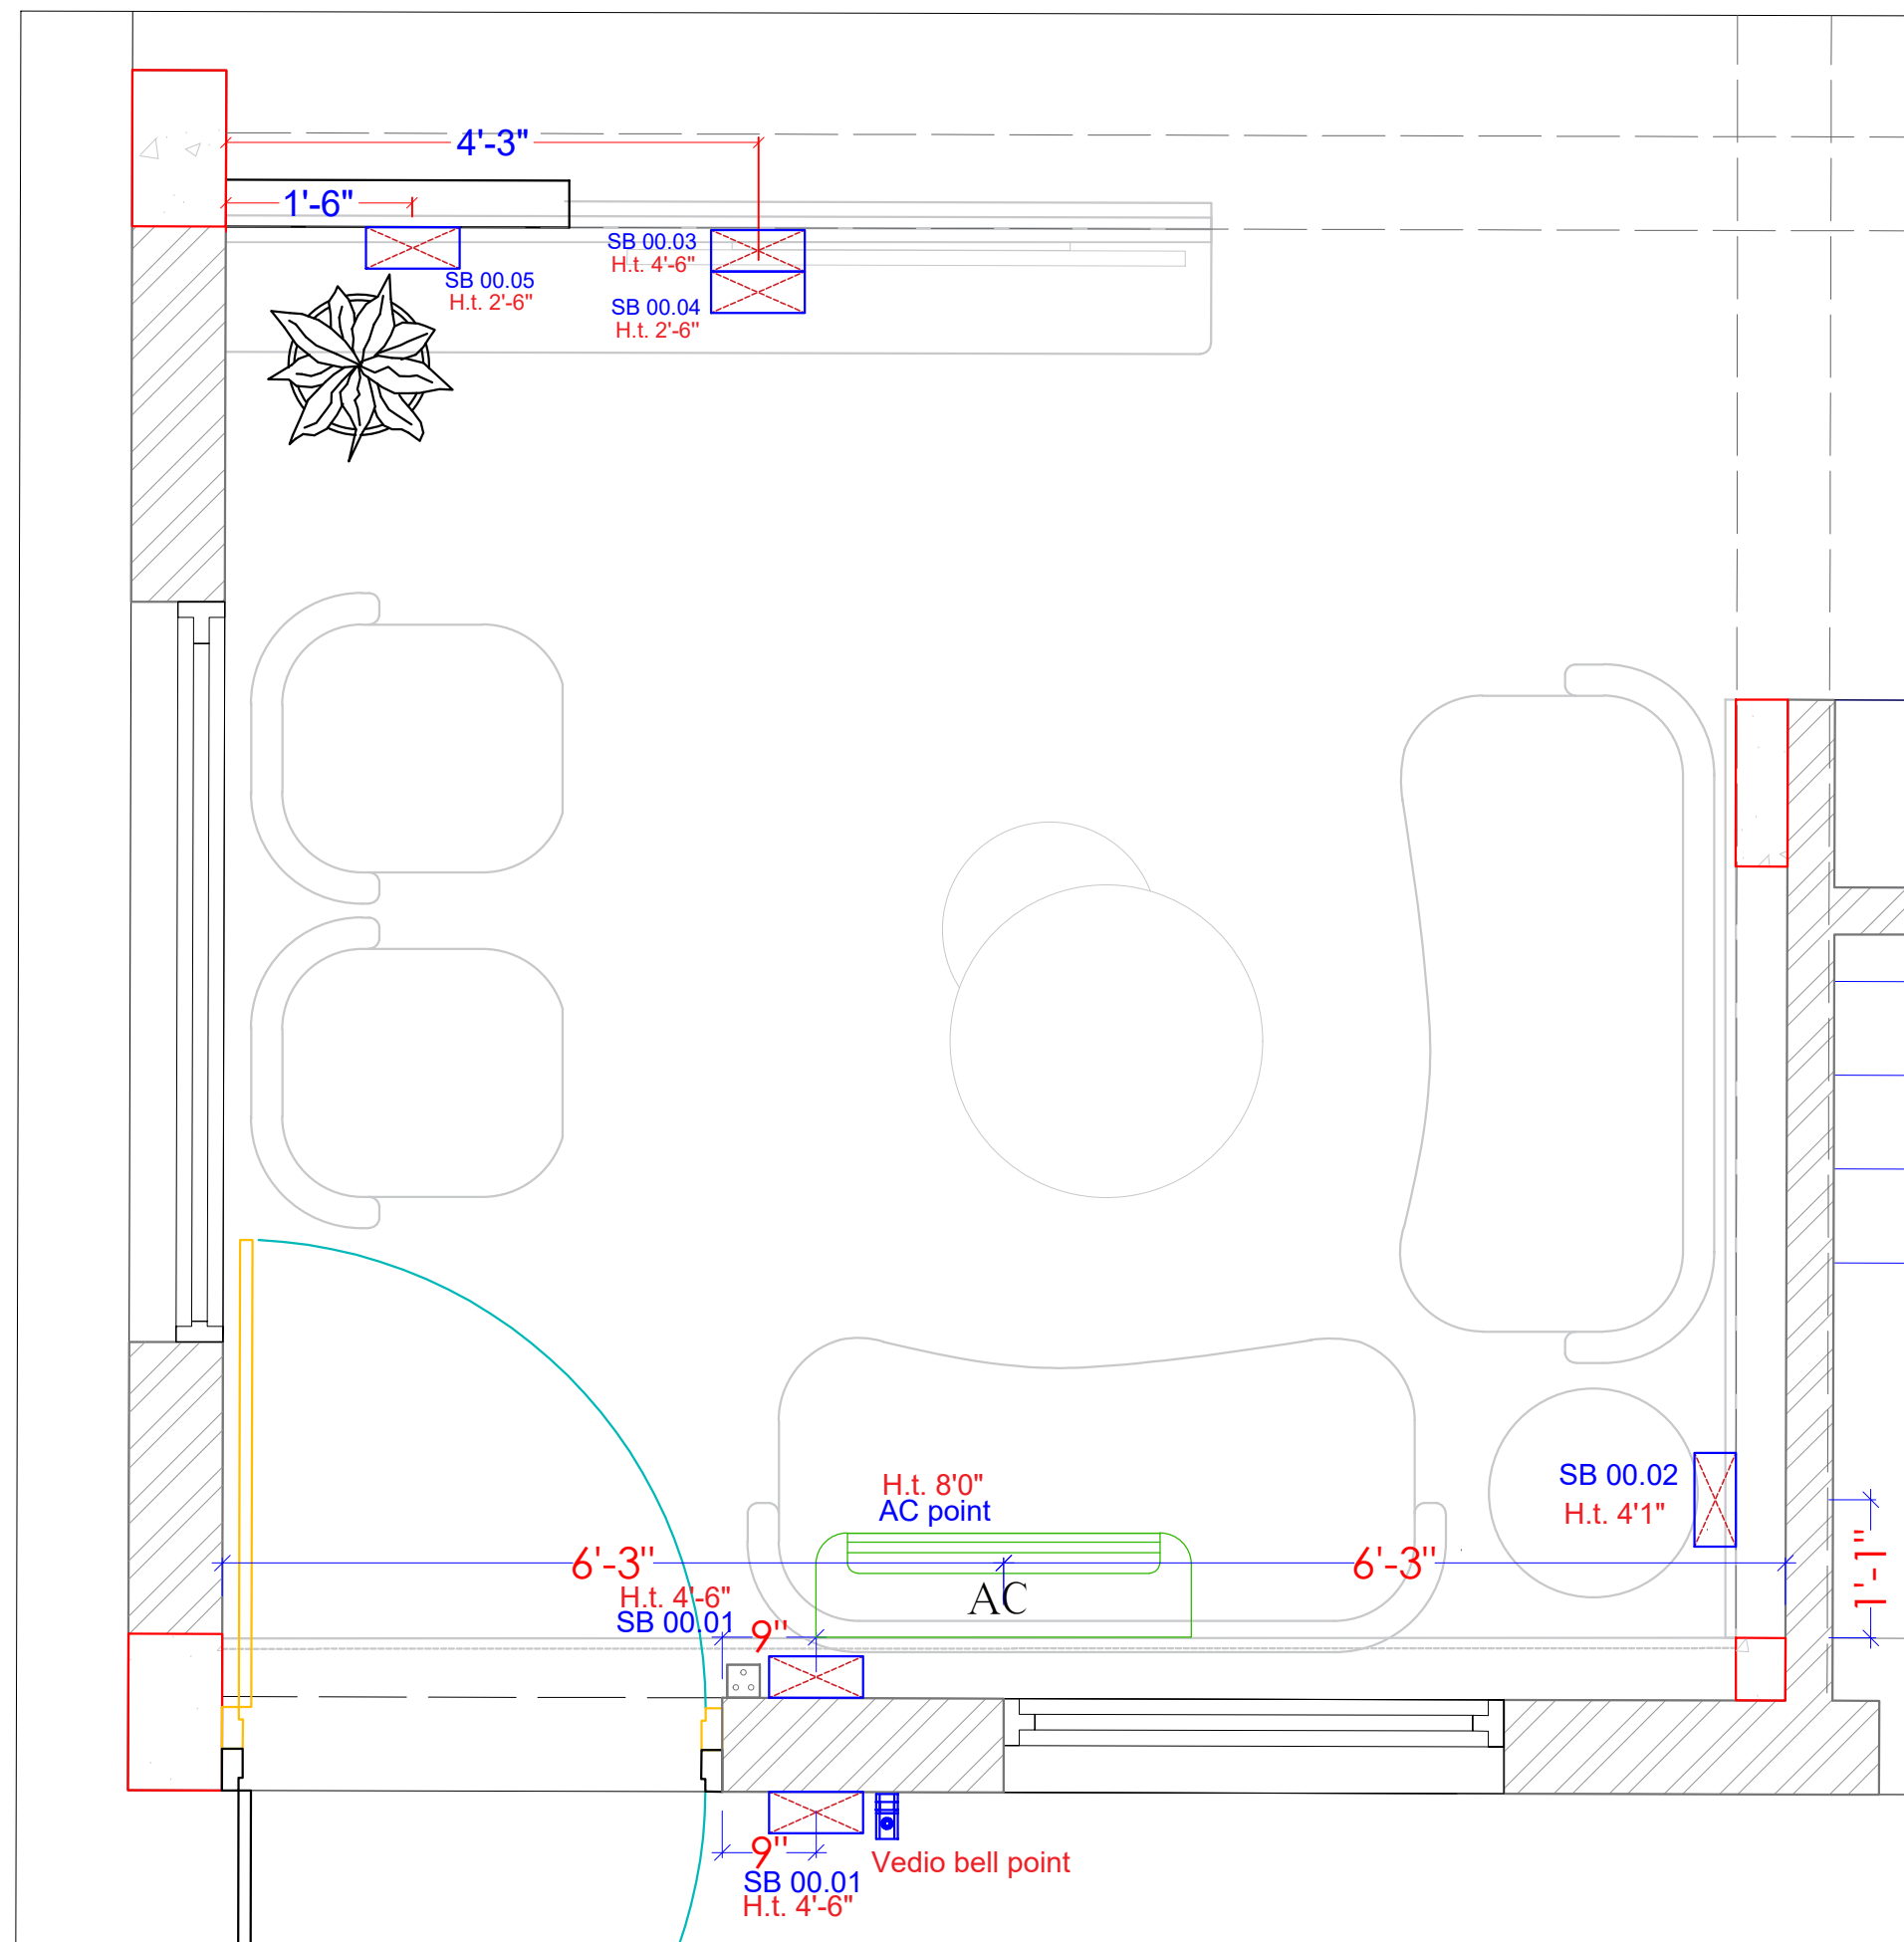

SWITCH BOARD LAYOUT

DRAWING TITLE :

LIVING ROOM SWITCH BOARD LAYOUT

NOTES:

- * DO NOT SCALE THE DRAWING.
- * ALL DIMENSIONS ARE IN FEET \ INCHES.
- * ANY DISCREPANCY IN THE DRAWING TO BE BROUGHT IN THE DESIGNER'S NOTICE BEFORE IMPLEMENTATION ON SITE.

SITE ADDRESS:

SAVAD
VADODARA

CLIENT NAME:

RONAK PANCHOLI

DATE: 02-06-2025

NORTH:

DRAWING DETAIL

REVISION NO. R1 R2 R3

REVISED DATE: 07/02/2026


SCALE: N.T.S

DRAWN BY: ARCHANA

CHECKED BY: MITTAL

www.mayaspace.studio
mayaspace.studio@gmail.com
+918980144077
@mayaspace.studio



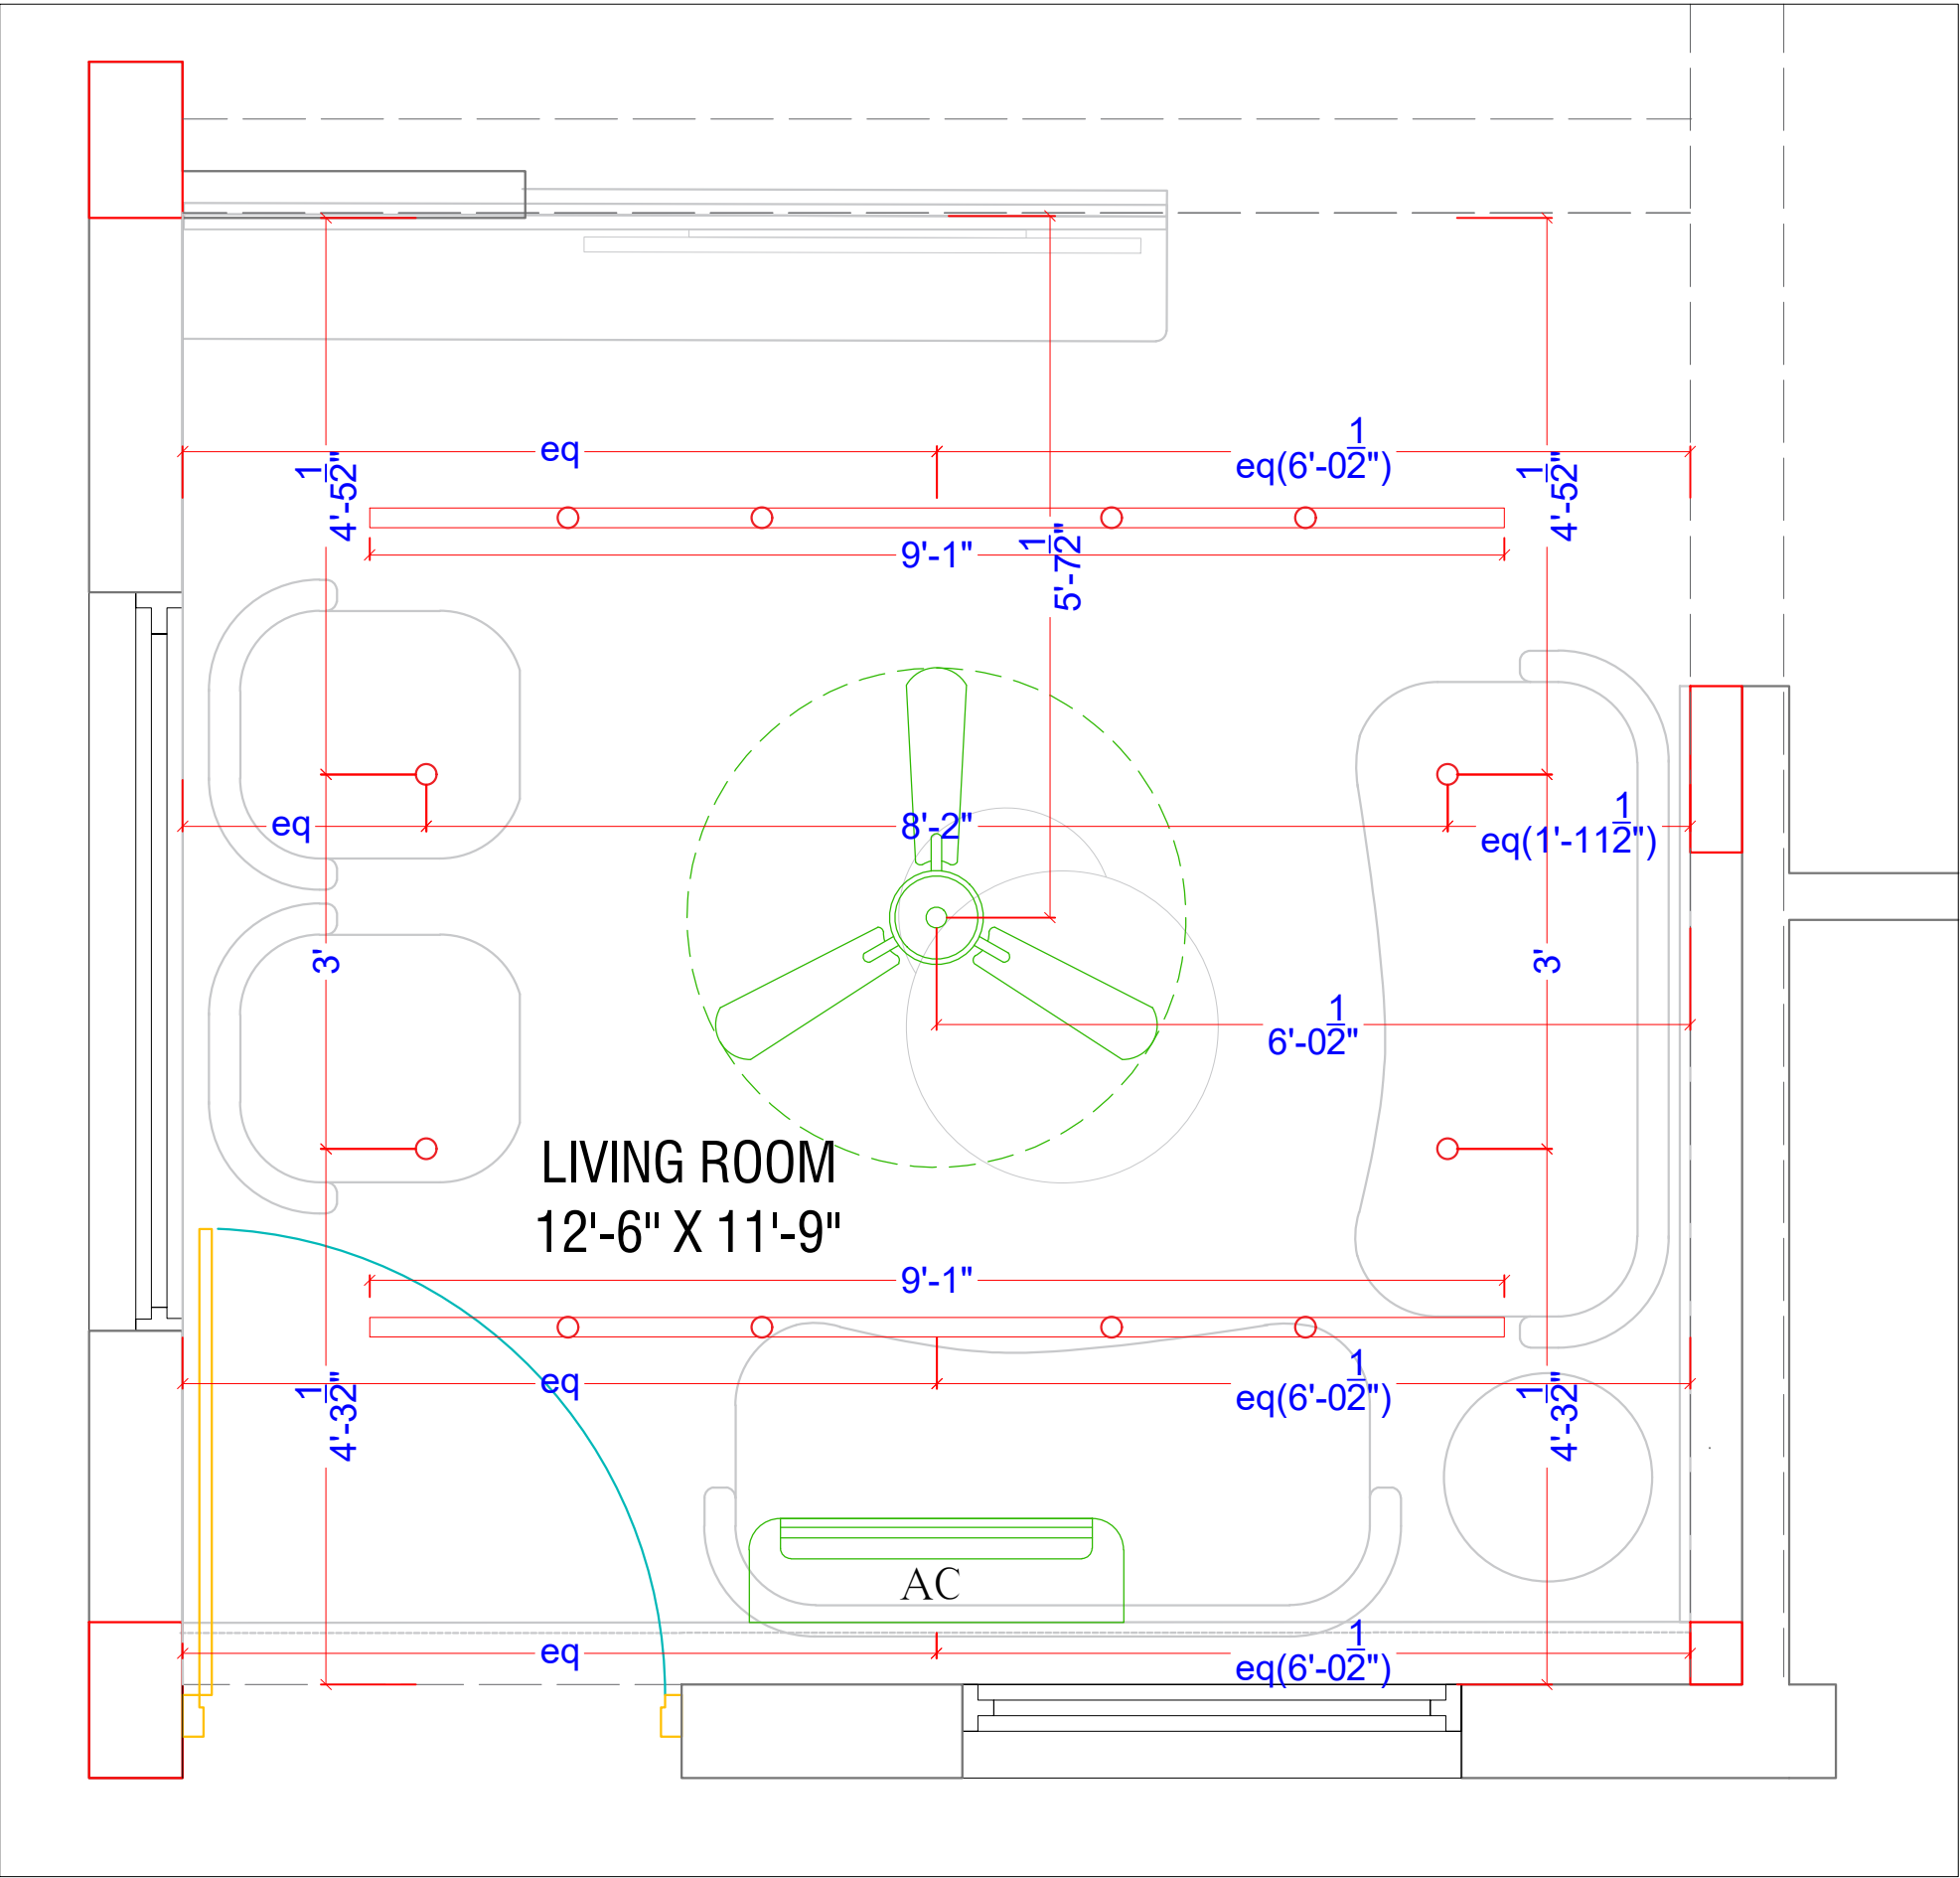

LIGHTING LAYOUT

DRAWING TITLE :

LIVING ROOM
LIGHTING LAYOUT

NOTES:

* DO NOT SCALE THE DRAWING.
* ALL DIMENSIONS ARE IN FEET \ INCHES.
* ANY DISCREPENCY IN THE DRAWING
TO BE BROUGHT IN THE DESIGNER'S
NOTICE BEFORE IMPLEMENTATION
ON SITE.

SITE ADDRESS:

SAVAD
VADODARA

CLIENT NAME:

RONAK PANCHOLI

DATE:

02-06-2025

NORTH:

DRAWING DETAIL

REVISION NO.

R1 R2 R3

REVISED DATE:

07/02/2026

SCALE:

N.T.S

DRAWN BY:

ARCHANA

CHECKED BY:

MITTAL


 www.mayaspace.studio

 mayaspace.studio@gmail.com

 +918980144077

 @mayaspace.studio



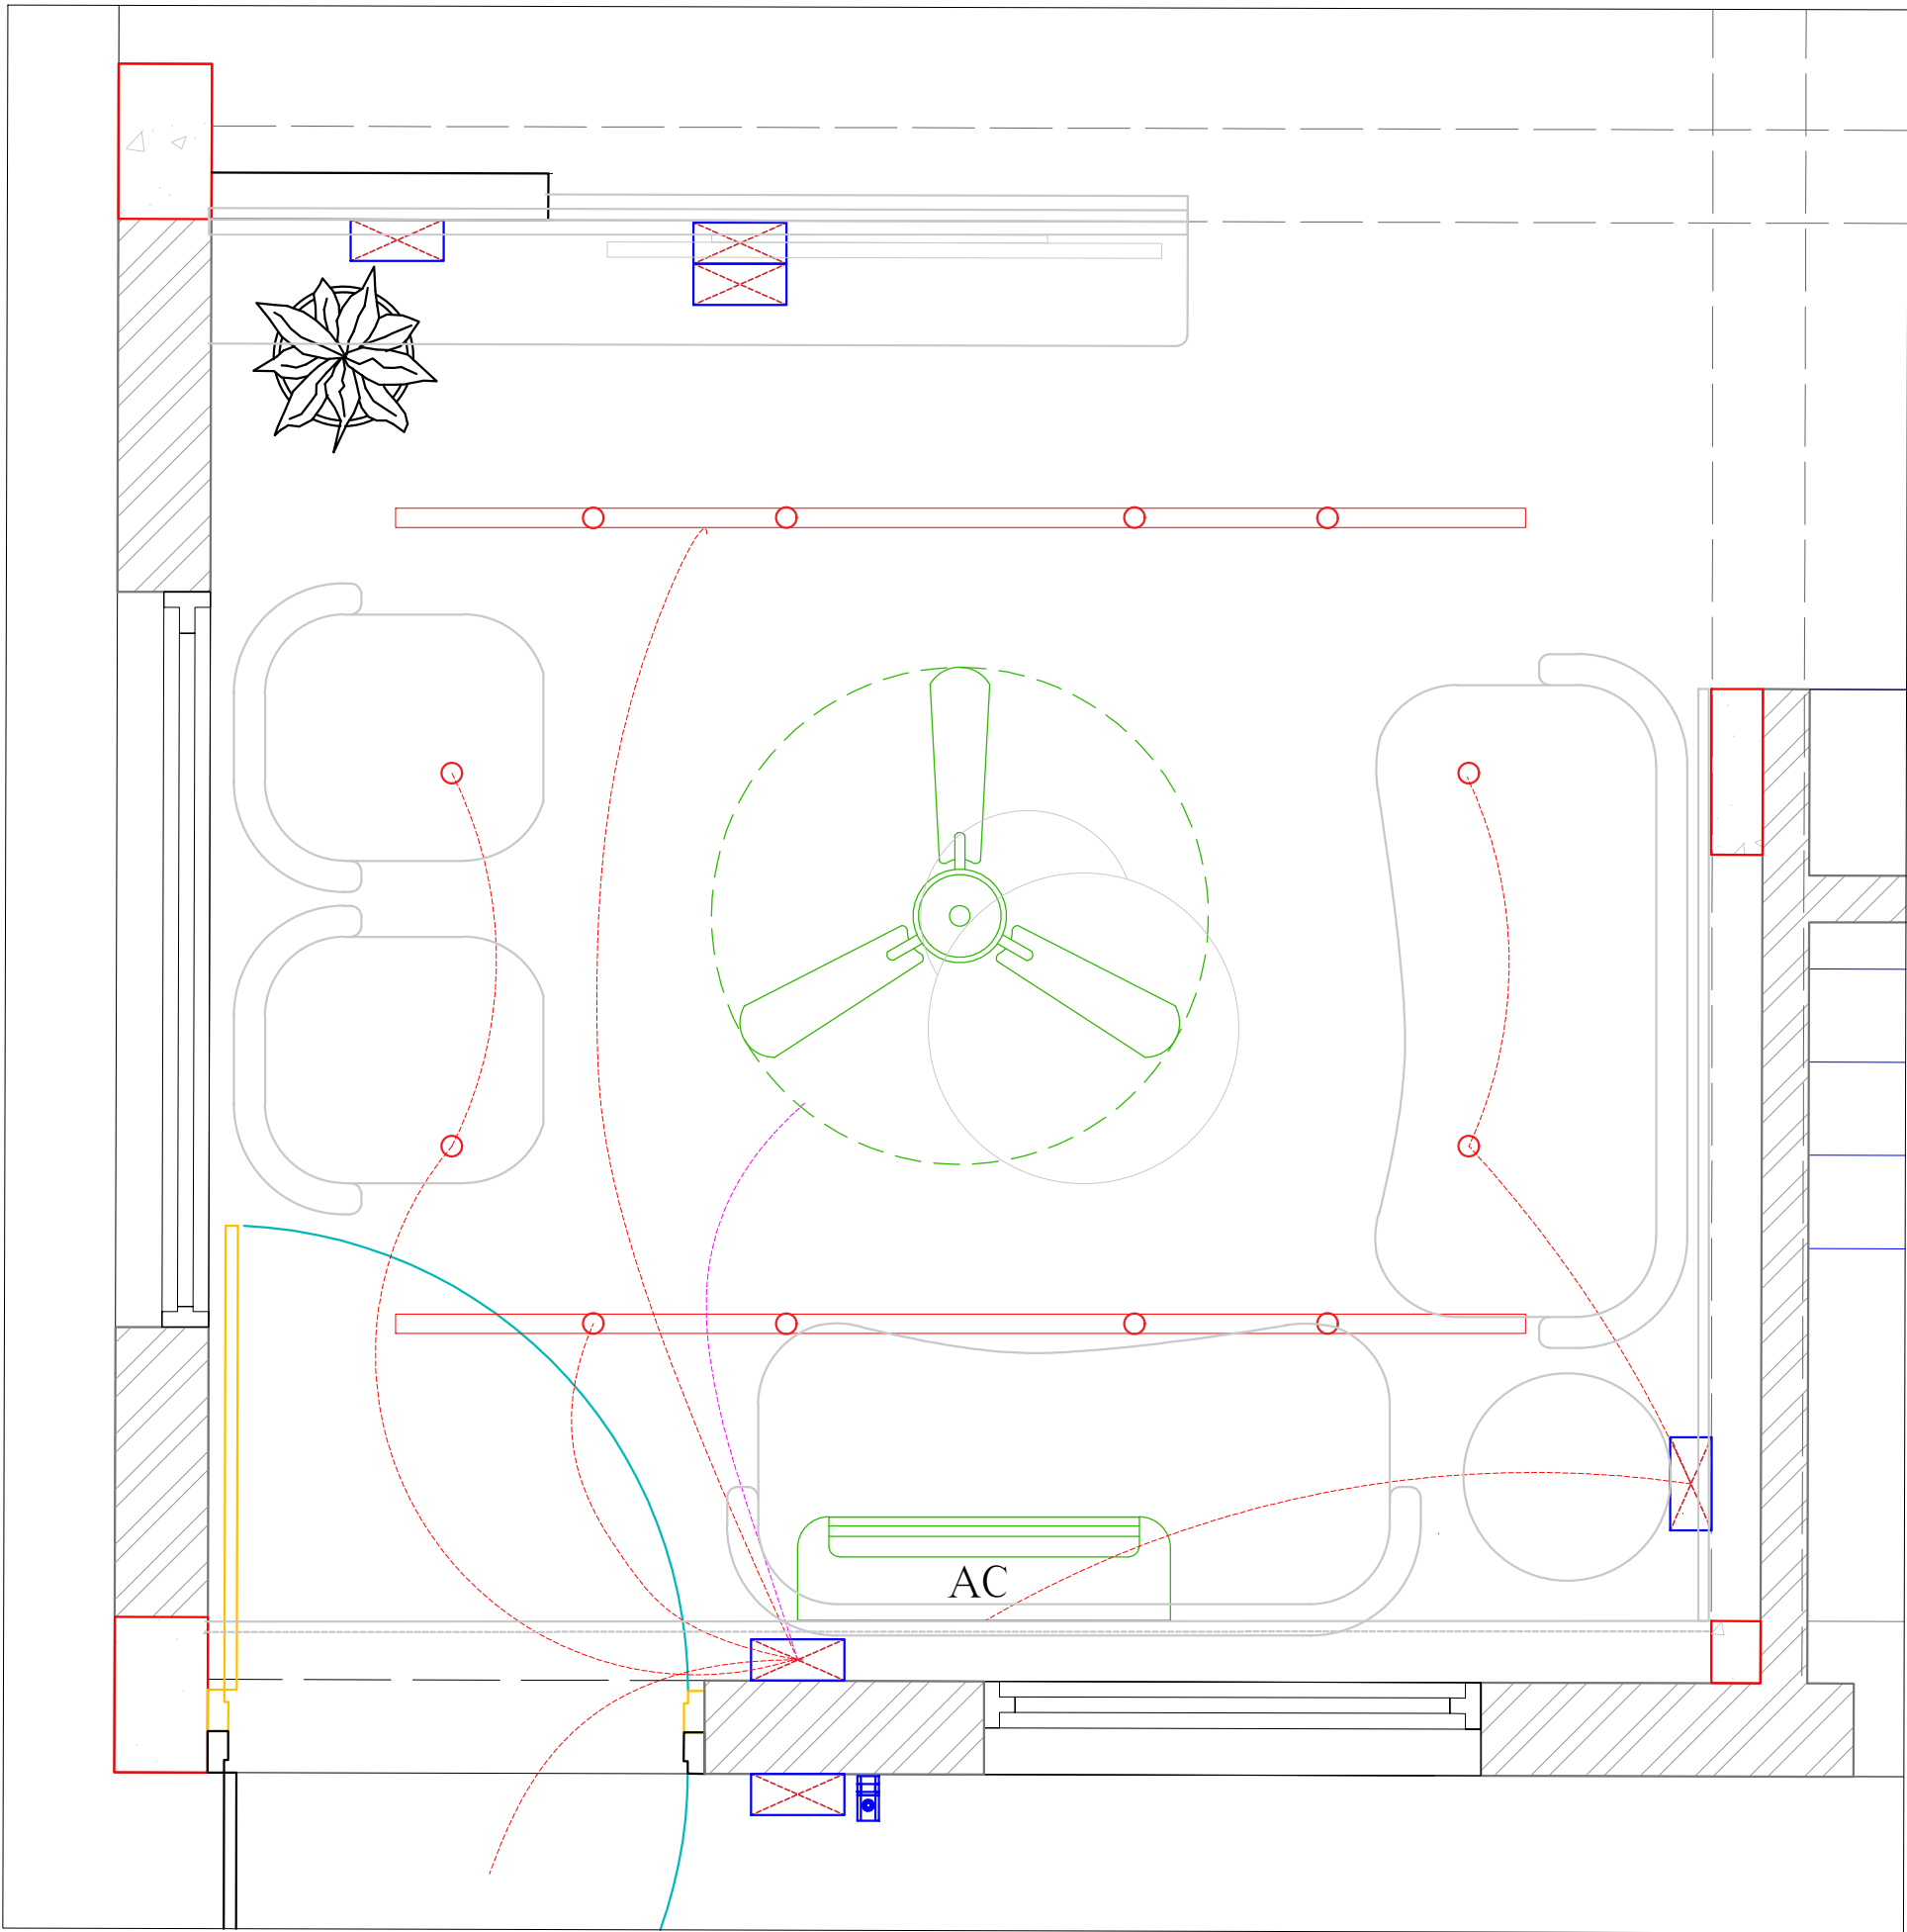

LOOPING LAYOUT

DRAWING TITLE :

LIVING ROOM
LOOPING LAYOUT

NOTES:

- * DO NOT SCALE THE DRAWING.
- * ALL DIMENSIONS ARE IN FEET \ INCHES.
- * ANY DISCREPENCY IN THE DRAWING TO BE BROUGHT IN THE DESIGNER'S NOTICE BEFORE IMPLEMENTATION ON SITE.

SITE ADDRESS:

SAVAD
VADODARA

CLIENT NAME:

RONAK PANCHOLI

DATE: 02-06-2025


NORTH:

DRAWING DETAIL

REVISION NO.	R1	R2	R3
REVISED DATE:	07/02/2026		
SCALE:	N.T.S		
DRAWN BY:	ARCHANA		
CHECKED BY:	MITTAL		

	www.mayaspace.studio
	mayaspace.studio@gmail.com
	+918980144077
	@mayaspace.studio



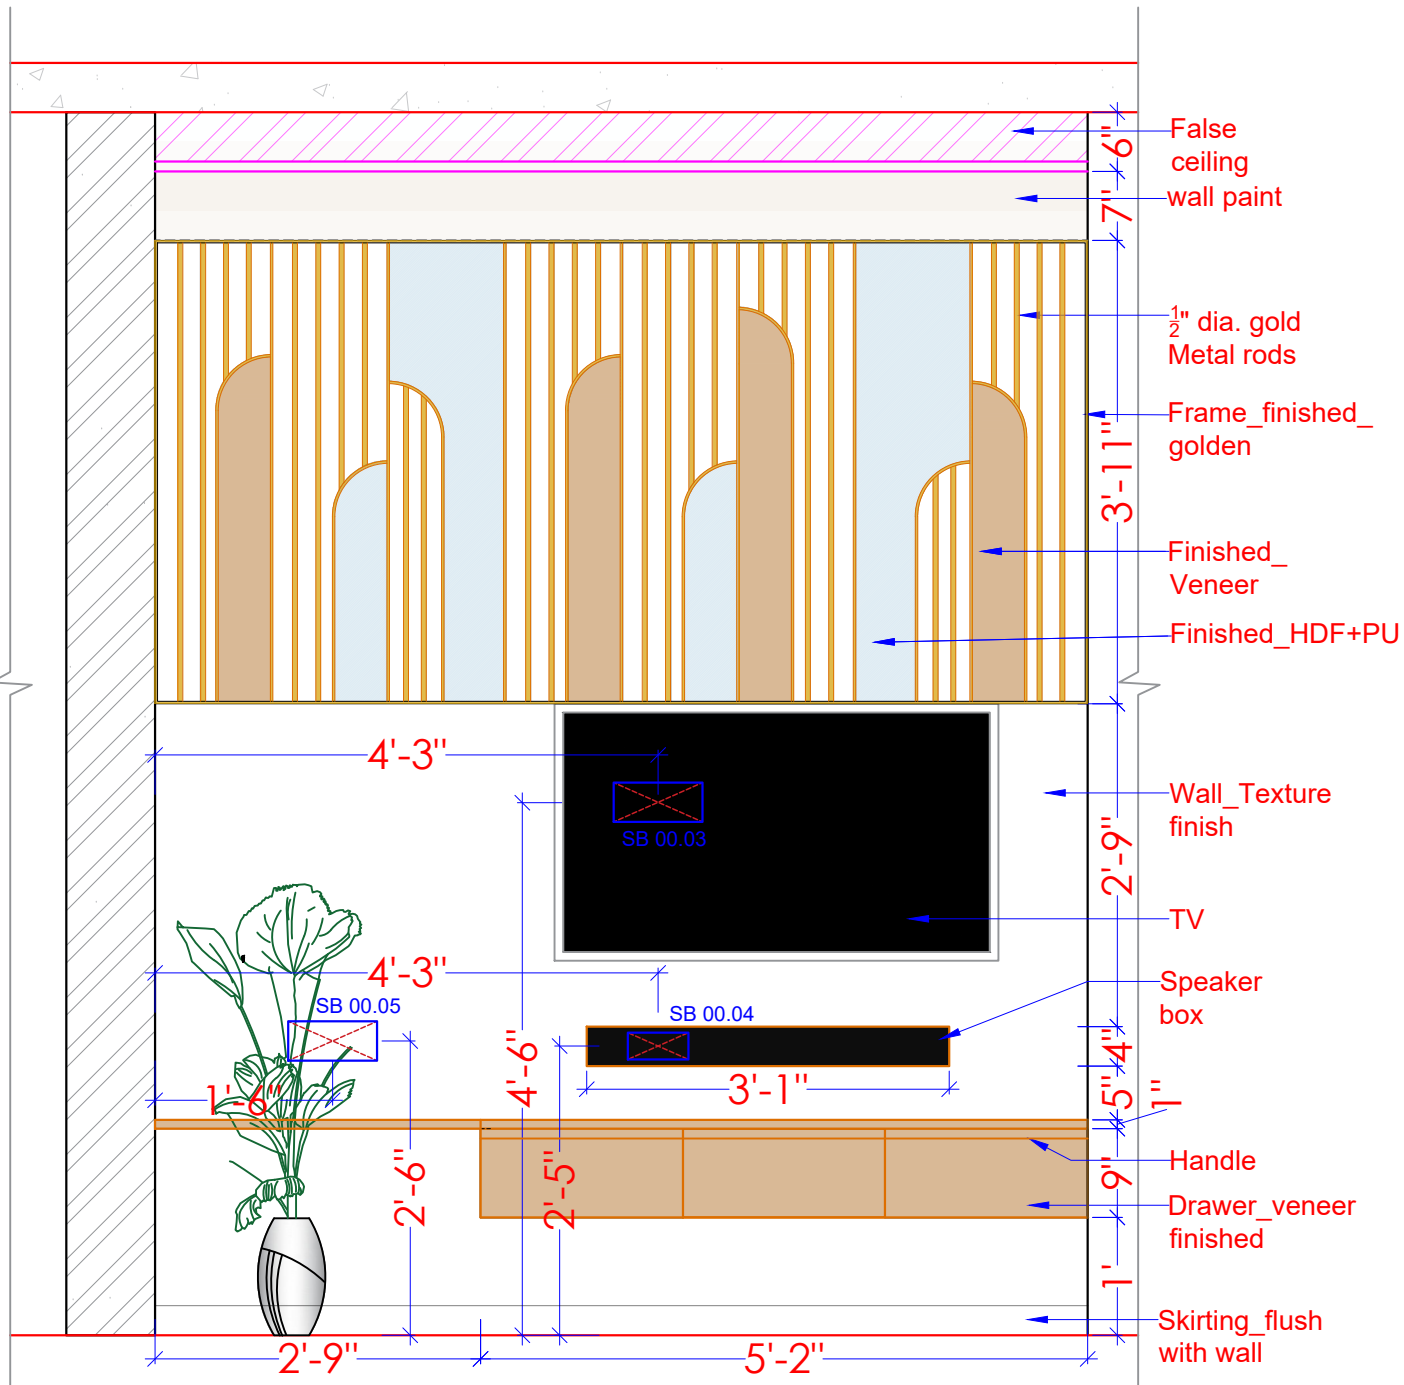

ELEVATION - A

DRAWING TITLE :

LIVING ROOM
ELEVATION- A

NOTES:

- * DO NOT SCALE THE DRAWING.
- * ALL DIMENSIONS ARE IN FEET \ INCHES.
- * ANY DISCREPENCY IN THE DRAWING TO BE BROUGHT IN THE DESIGNER'S NOTICE BEFORE IMPLEMENTATION ON SITE.

SITE ADDRESS:

SAVAD
VADODARA

CLIENT NAME:

RONAK PANCHOLI

DATE:

02-06-2025

NORTH:

DRAWING DETAIL

REVISION NO. R1 R2 R3

REVISED DATE: 07/02/2026


SCALE: N.T.S

DRAWN BY: ARCHANA

CHECKED BY: MITTAL

www.mayaspace.studio
mayaspace.studio@gmail.com
+918980144077
@mayaspace.studio



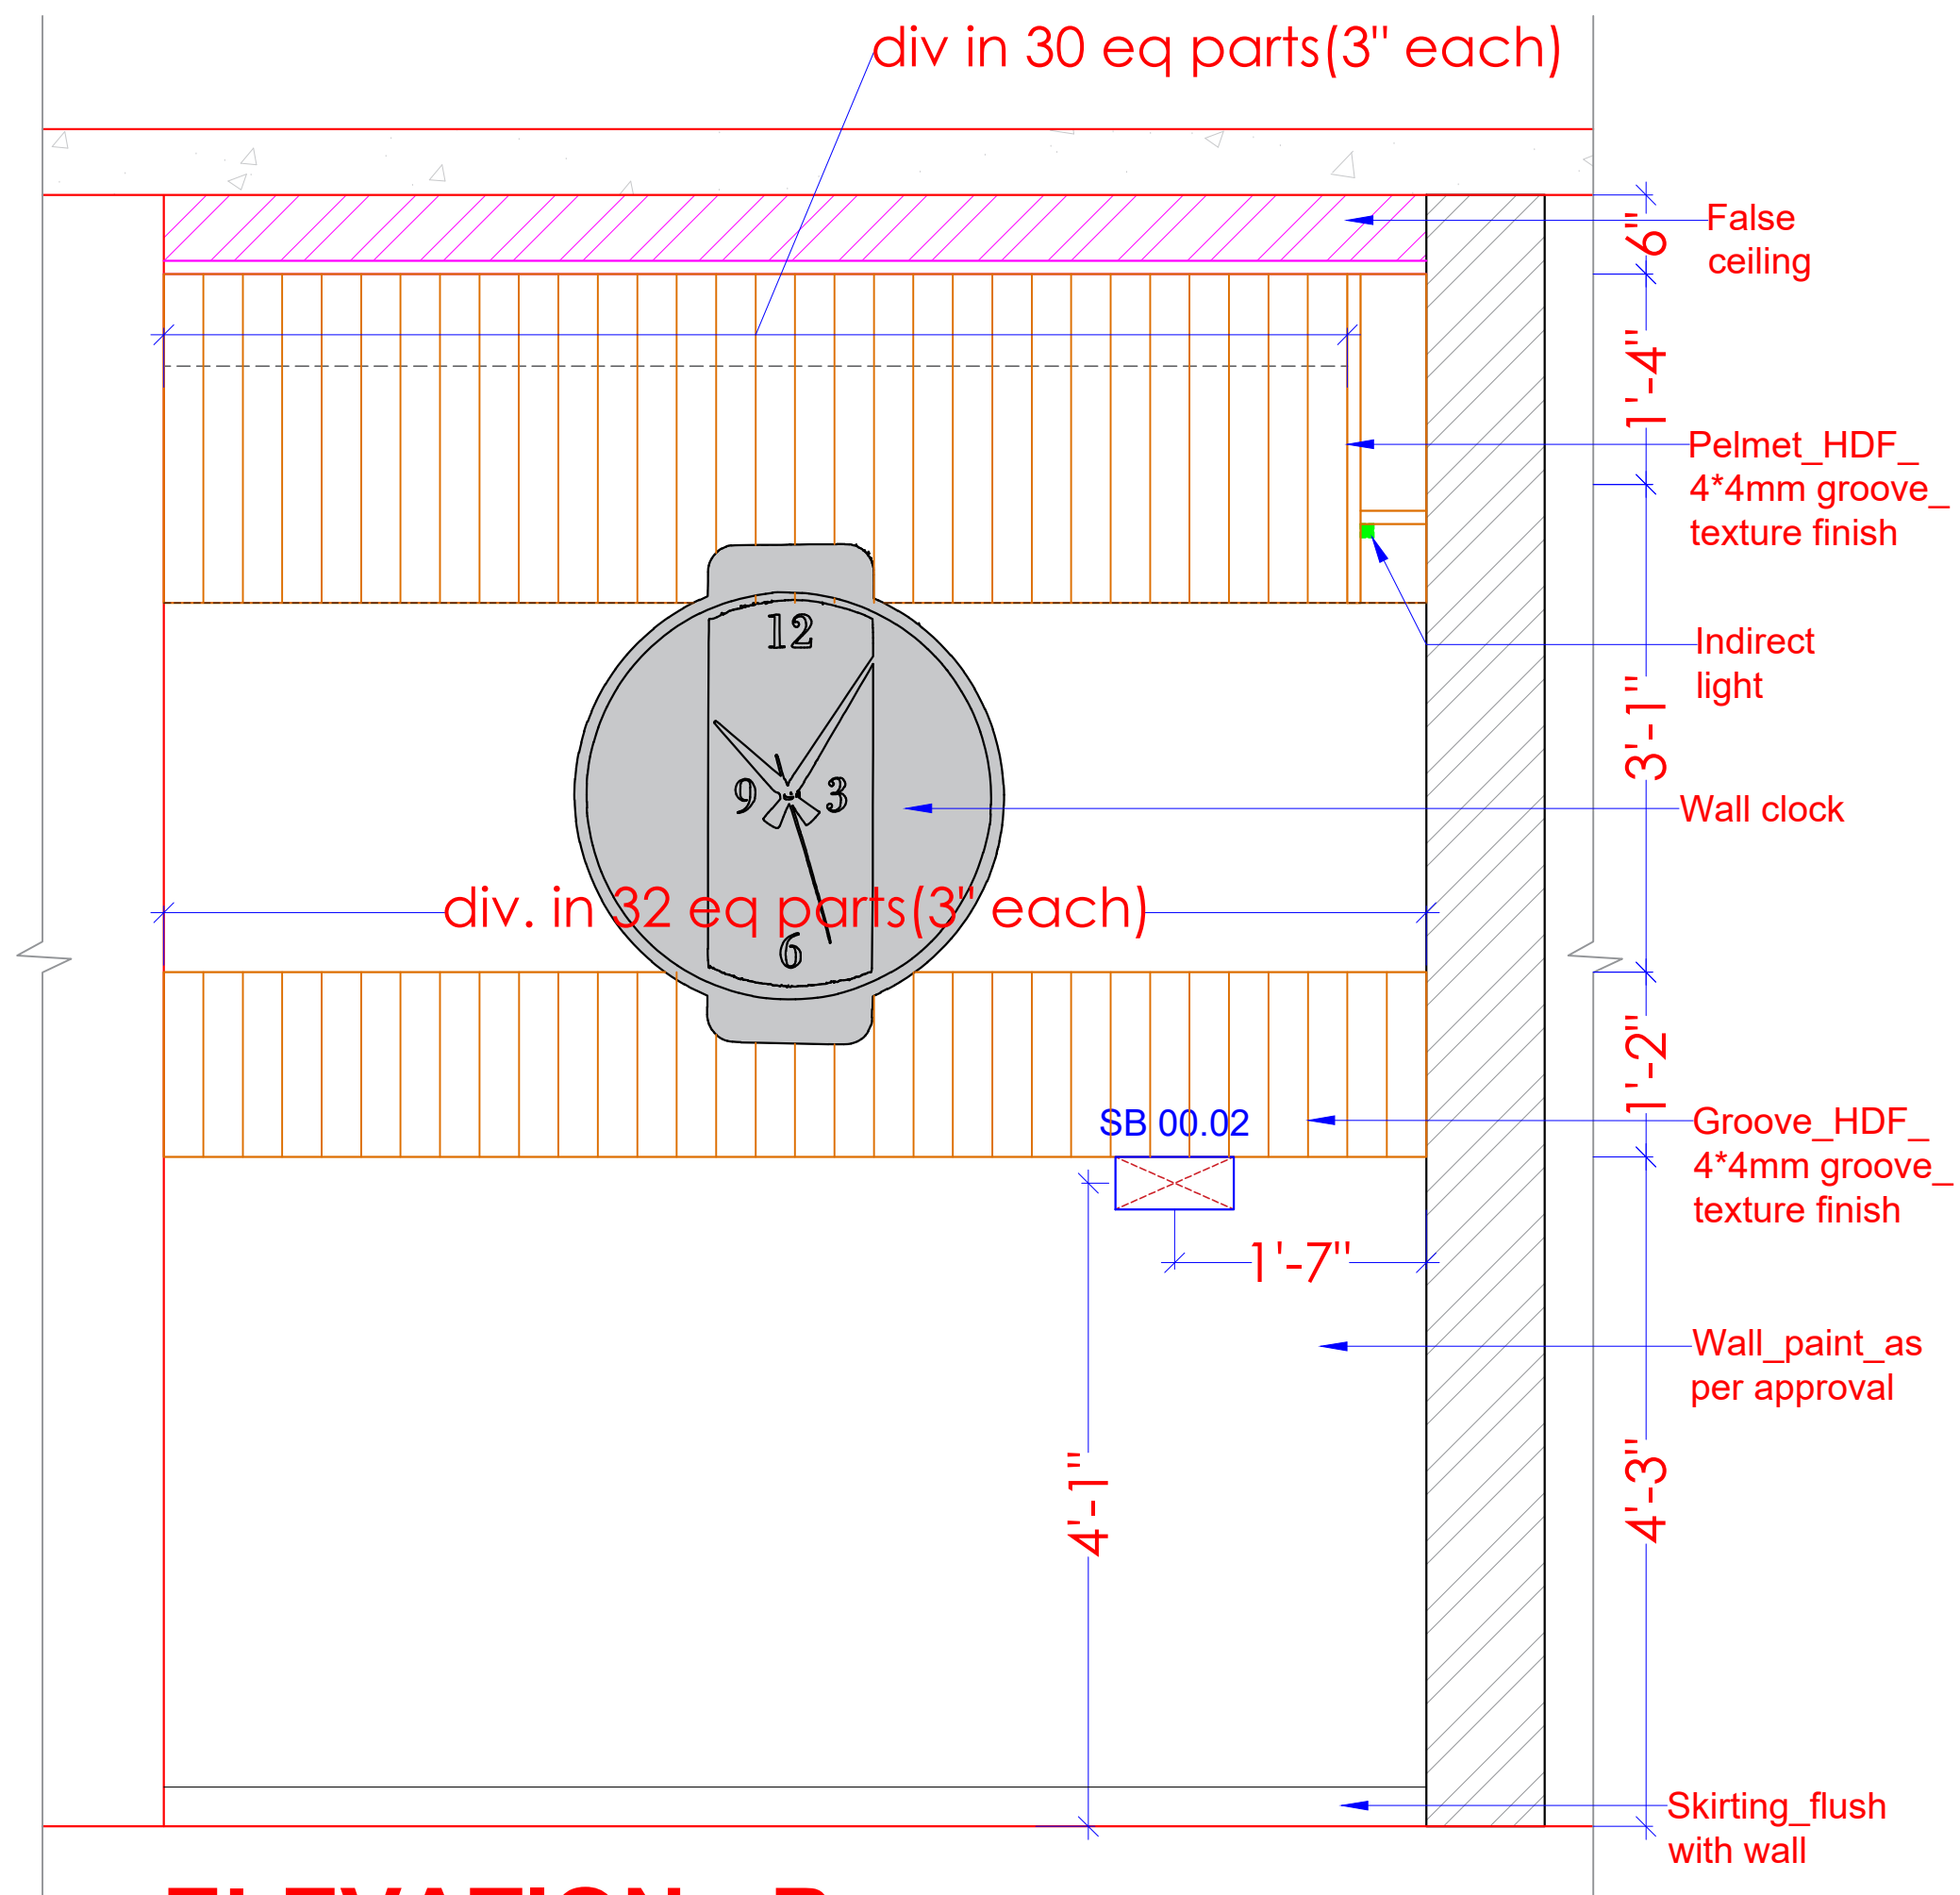

ELEVATION - B

DRAWING TITLE :

LIVING ROOM
ELEVATION- B

NOTES:

- * DO NOT SCALE THE DRAWING.
- * ALL DIMENSIONS ARE IN FEET \ INCHES.
- * ANY DISCREPANCY IN THE DRAWING TO BE BROUGHT IN THE DESIGNER'S NOTICE BEFORE IMPLEMENTATION ON SITE.

SITE ADDRESS:

SAVAD
VADODARA

CLIENT NAME:

RONAK PANCHOLI

DATE:

02-06-2025

NORTH:

DRAWING DETAIL

REVISION NO.

R1 R2 R3

REVISED DATE:

07/02/2026

SCALE:

N.T.S

DRAWN BY:


ARCHANA

CHECKED BY:

MITTAL

	www.mayaspace.studio
	mayaspace.studio@gmail.com
	+918980144077
	@mayaspace.studio



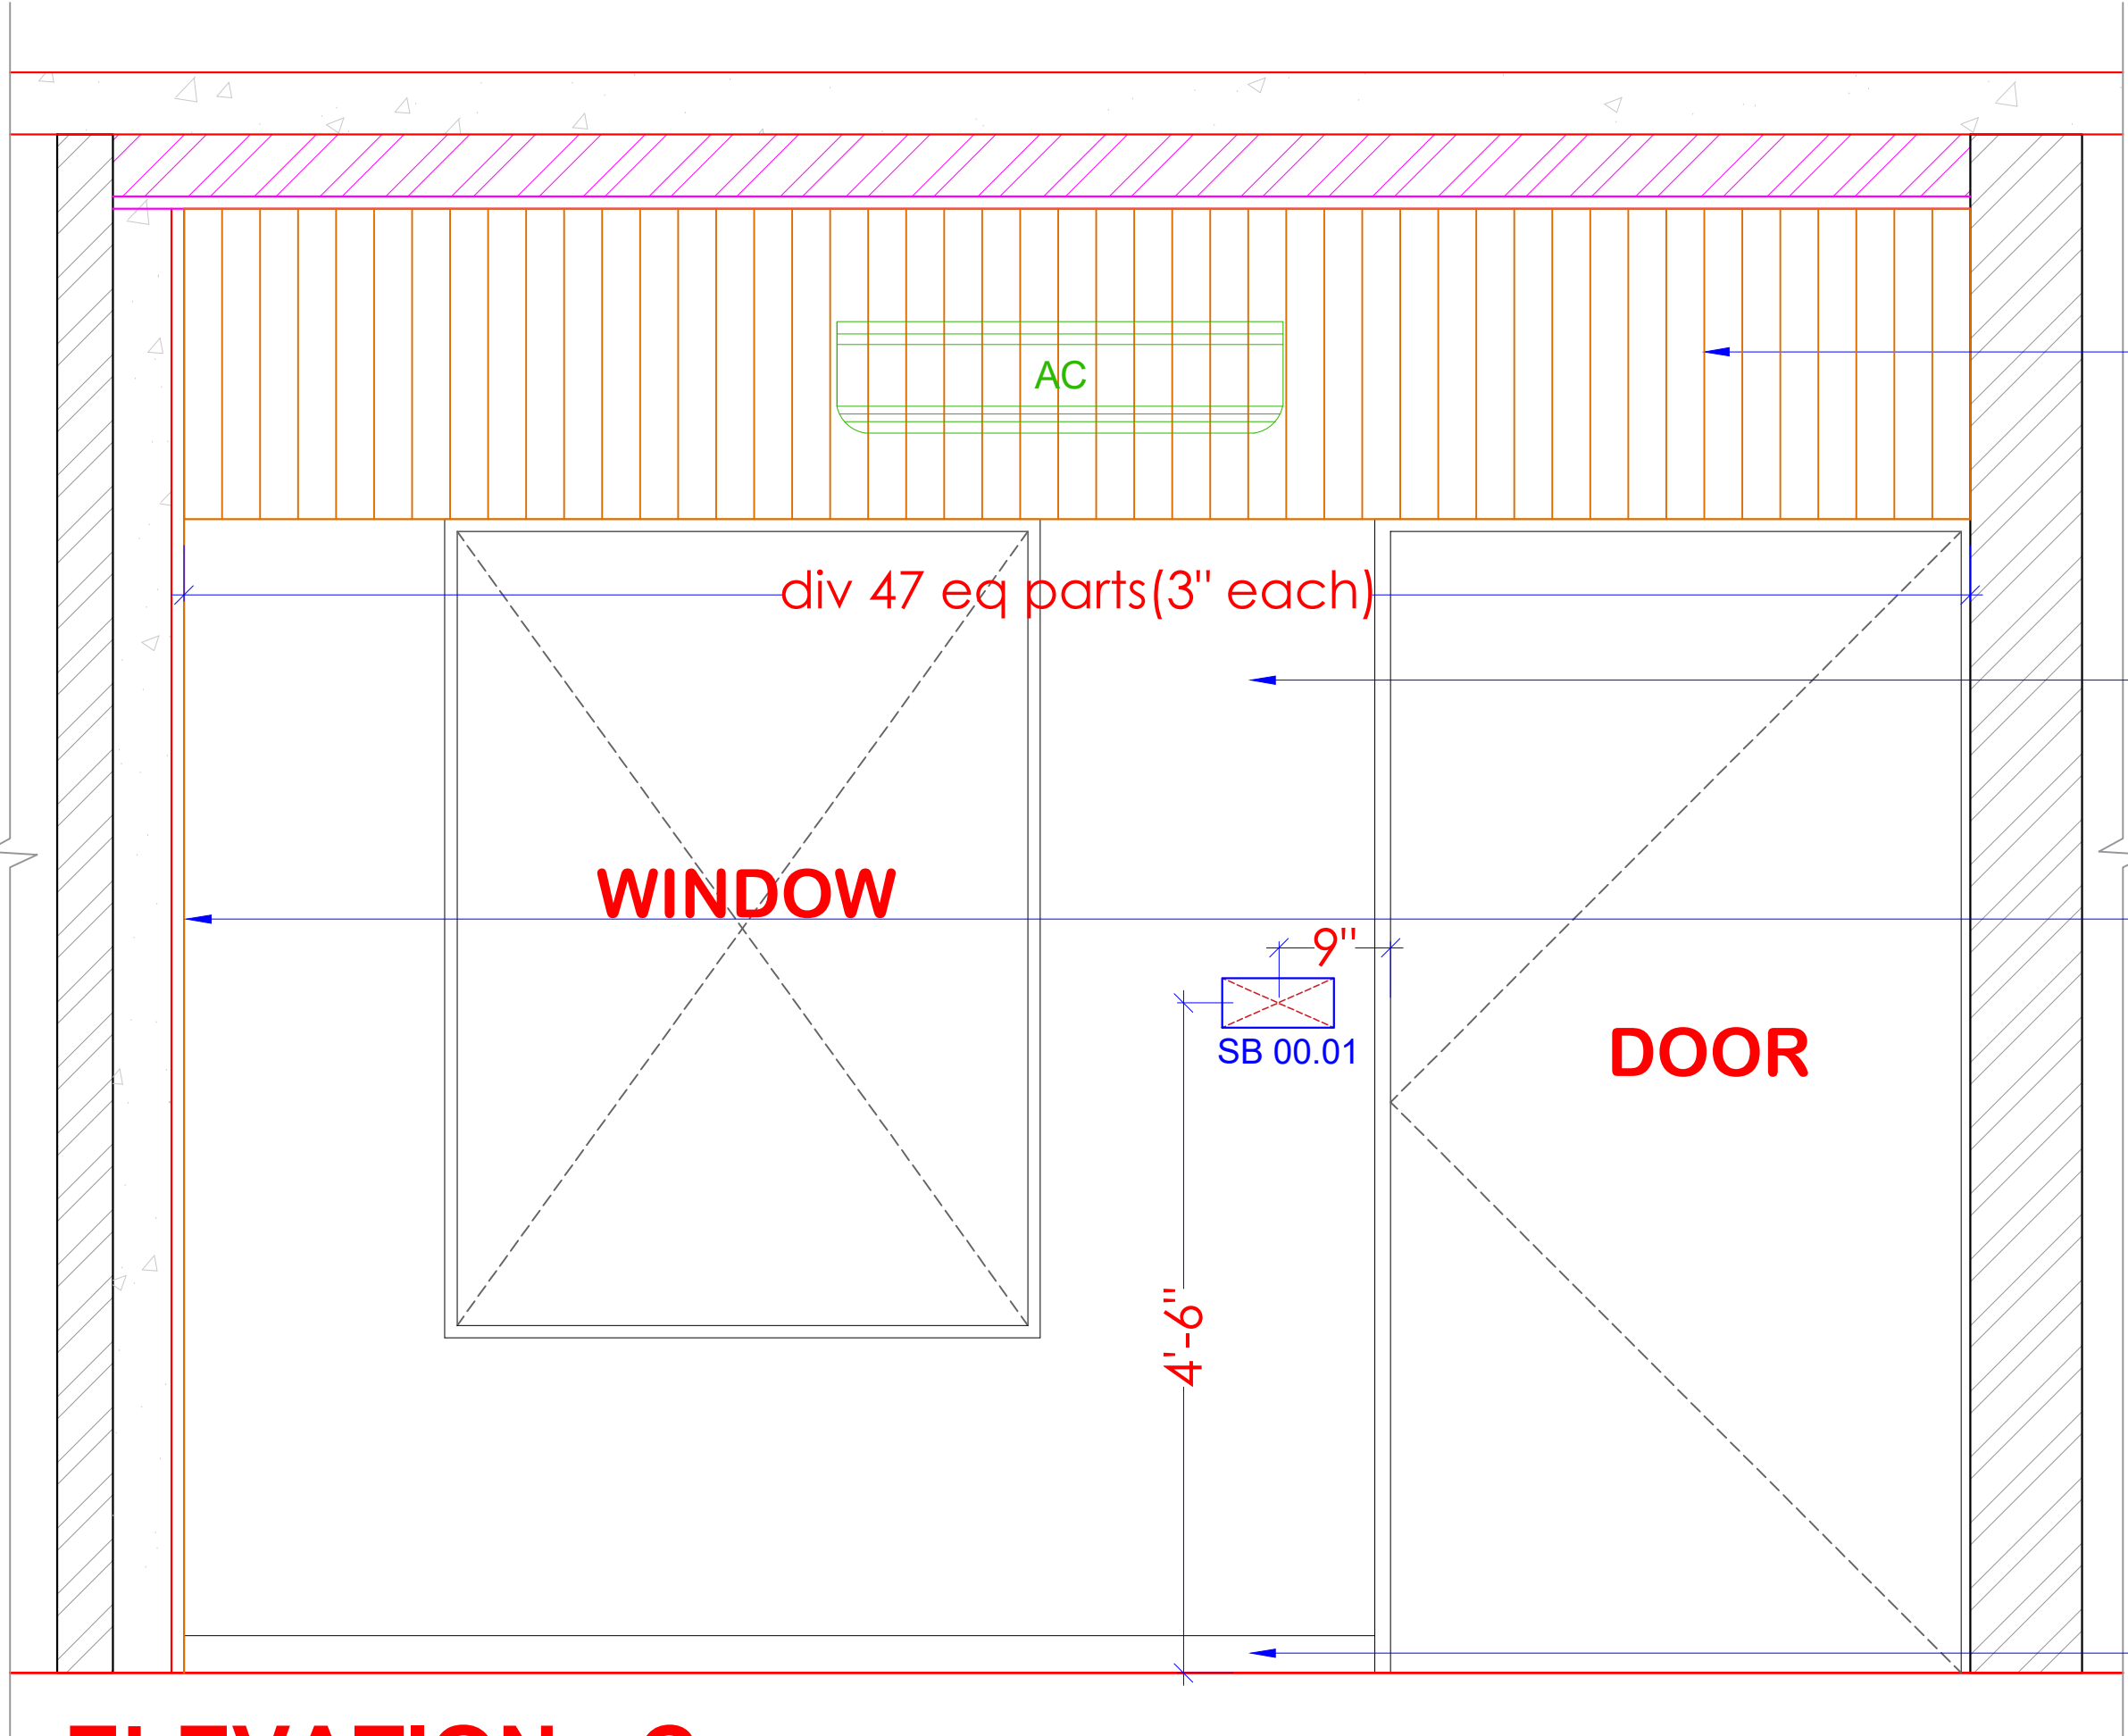

ELEVATION - C

DRAWING TITLE :

LIVING ROOM
ELEVATION- C

NOTES:

- * DO NOT SCALE THE DRAWING.
- * ALL DIMENSIONS ARE IN FEET \ INCHES.
- * ANY DISCREPANCY IN THE DRAWING TO BE BROUGHT IN THE DESIGNER'S NOTICE BEFORE IMPLEMENTATION ON SITE.

SITE ADDRESS:

SAVAD
VADODARA

CLIENT NAME:

RONAK PANCHOLI

DATE:

02-06-2025

NORTH:

DRAWING DETAIL

REVISION NO.

R1 R2 R3

REVISED DATE:

07/02/2026

SCALE:

N.T.S

DRAWN BY:


ARCHANA

CHECKED BY:

MITTAL

- www.mayaspace.studio
- mayaspace.studio@gmail.com
- +918980144077
- @mayaspace.studio



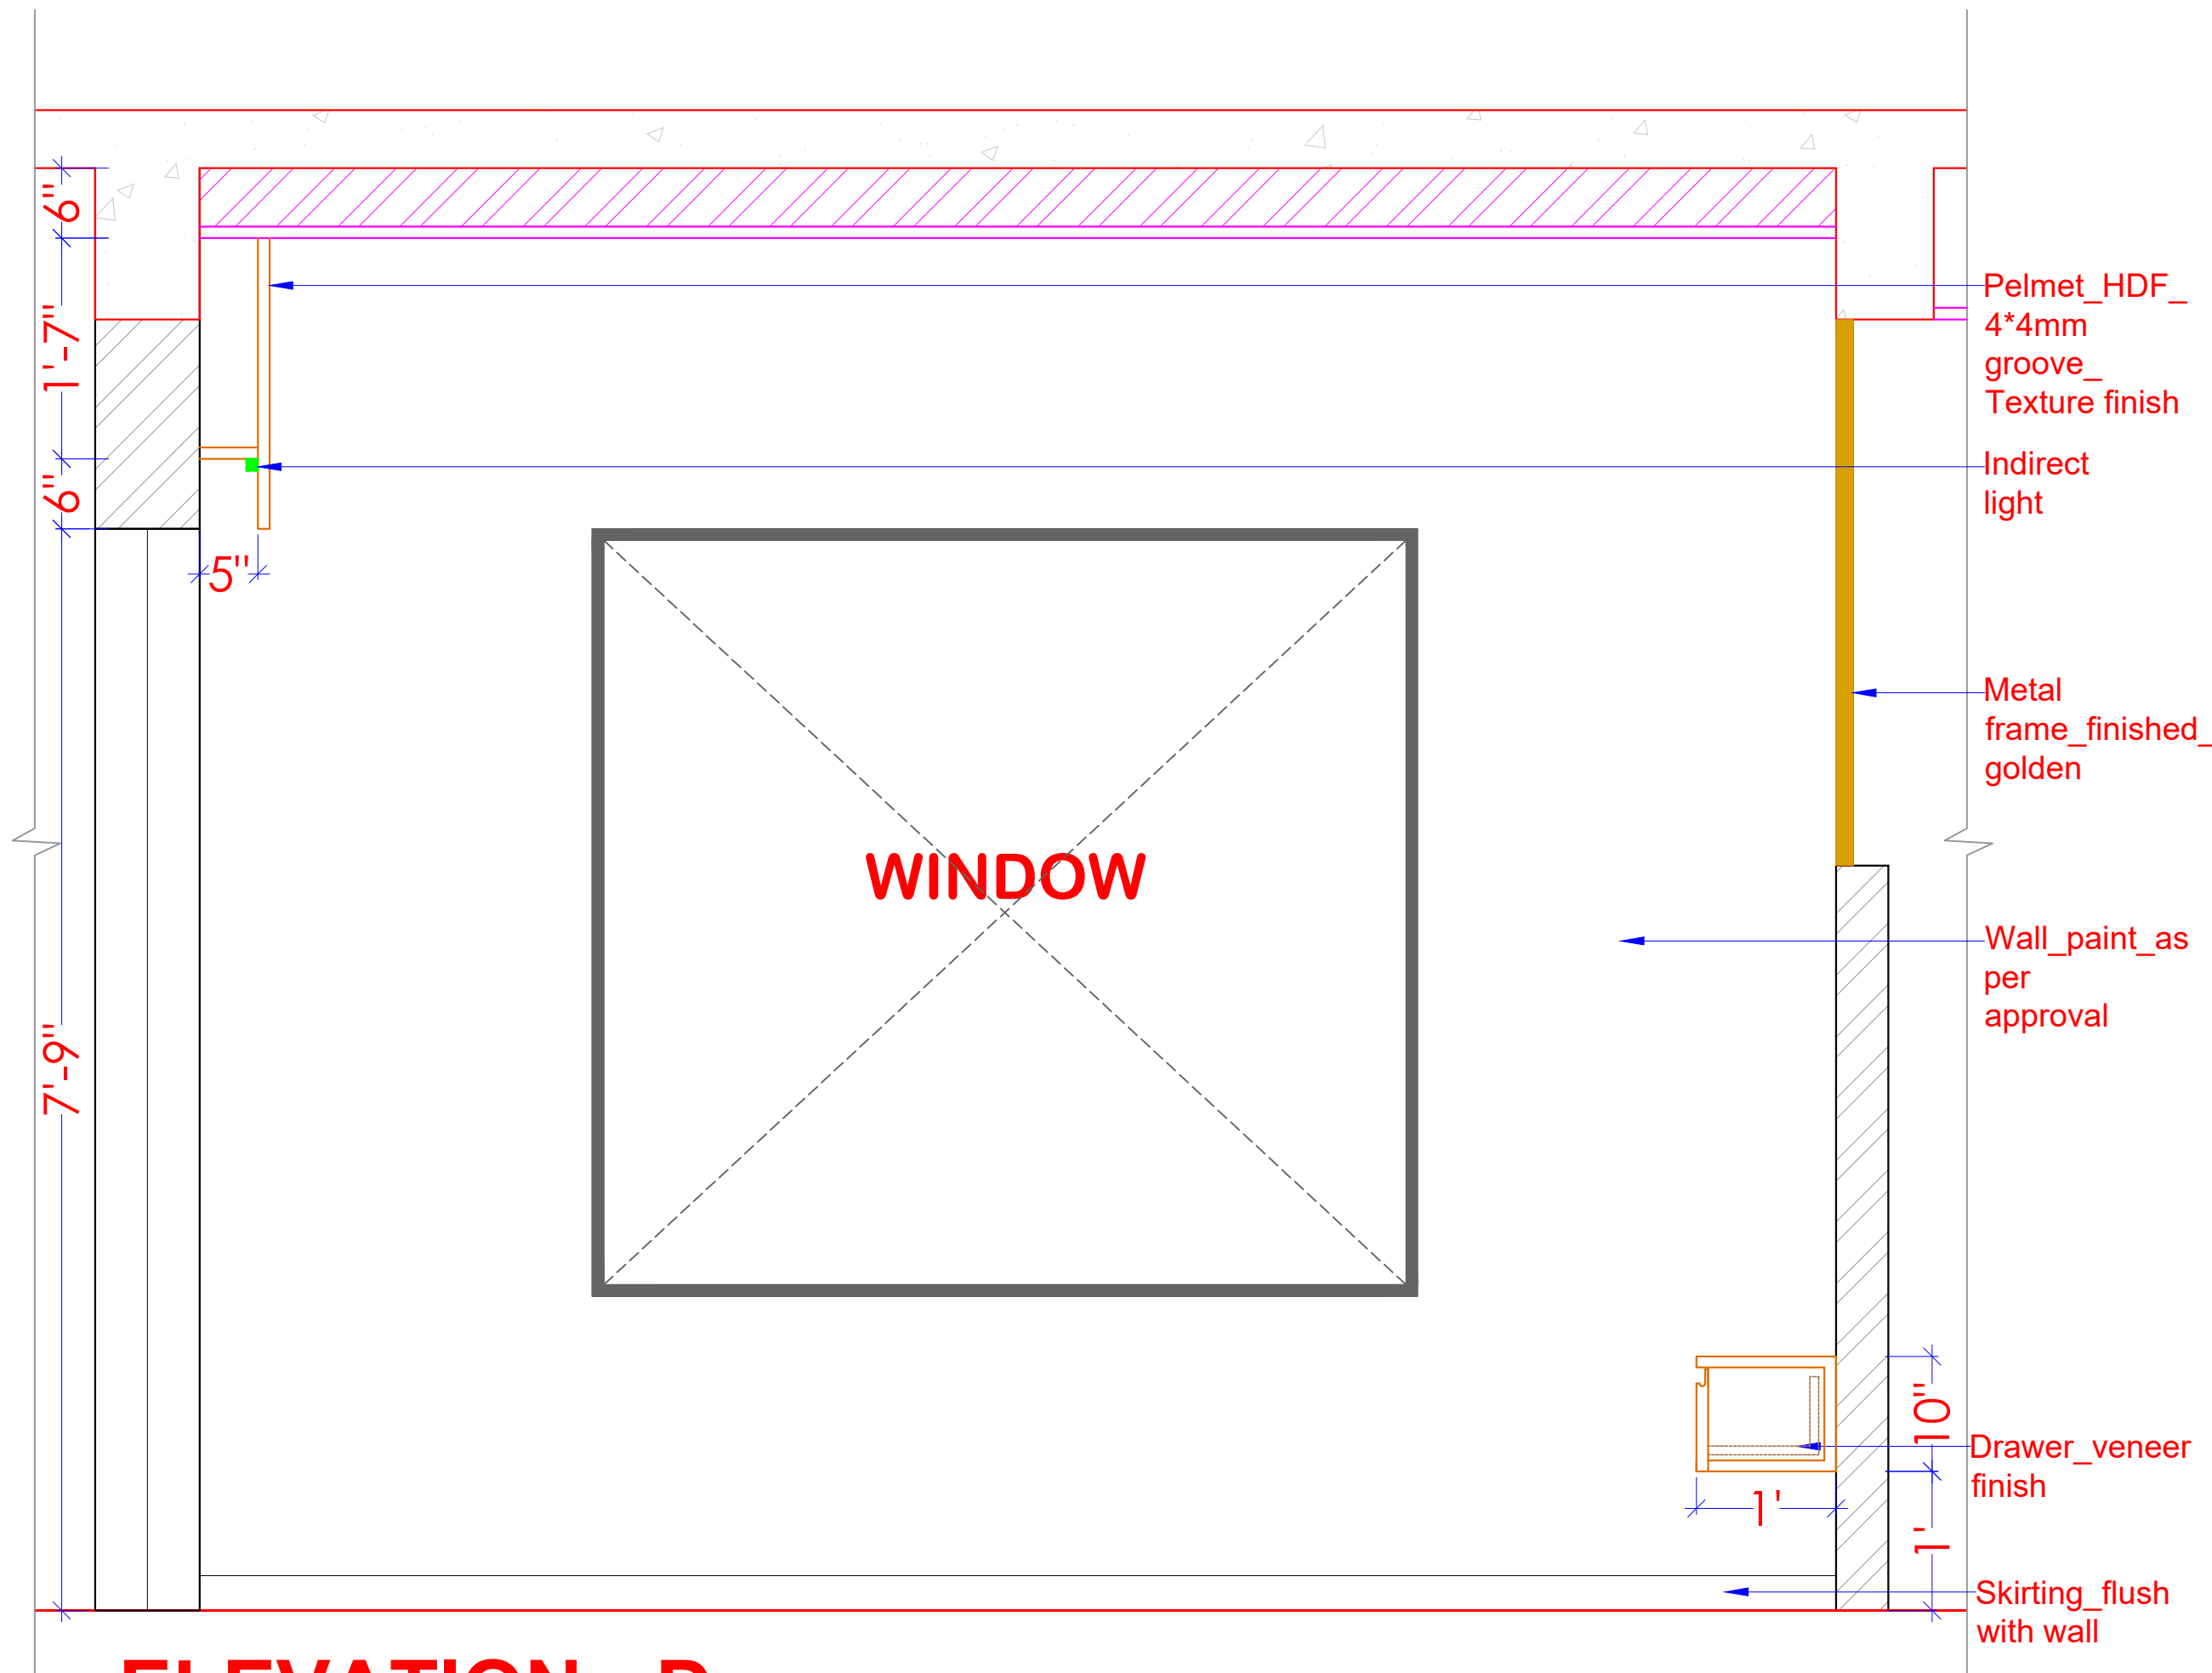

ELEVATION - D

DRAWING TITLE :

LIVING ROOM
ELEVATION- D

NOTES:

* DO NOT SCALE THE DRAWING.

* ALL DIMENSIONS ARE IN FEET \ INCHES.

* ANY DISCREPENCY IN THE DRAWING
TO BE BROUGHT IN THE DESIGNER'S
NOTICE BEFORE IMPLEMENTATION
ON SITE.

SITE ADDRESS:

SAVAD
VADODARA

CLIENT NAME:

RONAK PANCHOLI


DATE:	02-06-2025
NORTH:	

DRAWING DETAIL


REVISION NO.	R1 R2 R3
REVISED DATE:	07/02/2026
SCALE:	N.T.S
DRAWN BY:	ARCHANA
CHECKED BY:	MITTAL

	www.mayaspace.studio
	mayaspace.studio@gmail.com
	+918980144077
	@mayaspace.studio

Maya
SPACE STUDIO

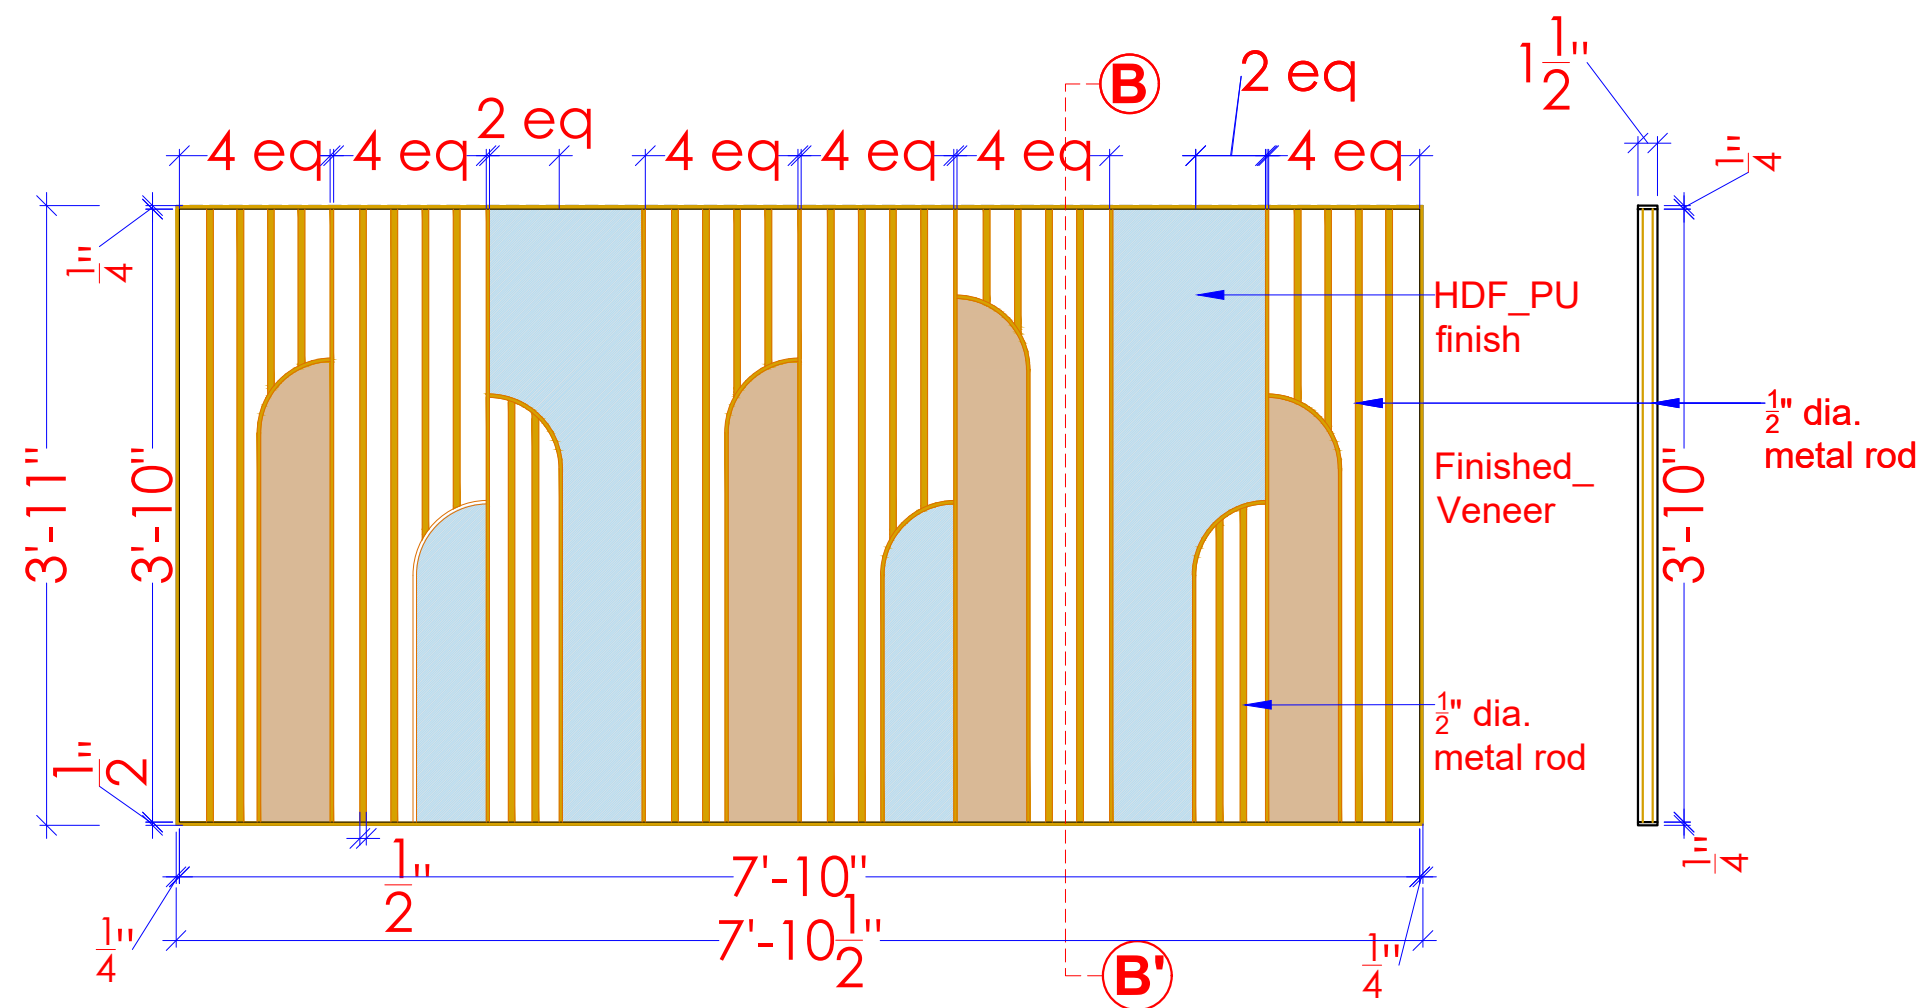

TV WALL PLAN

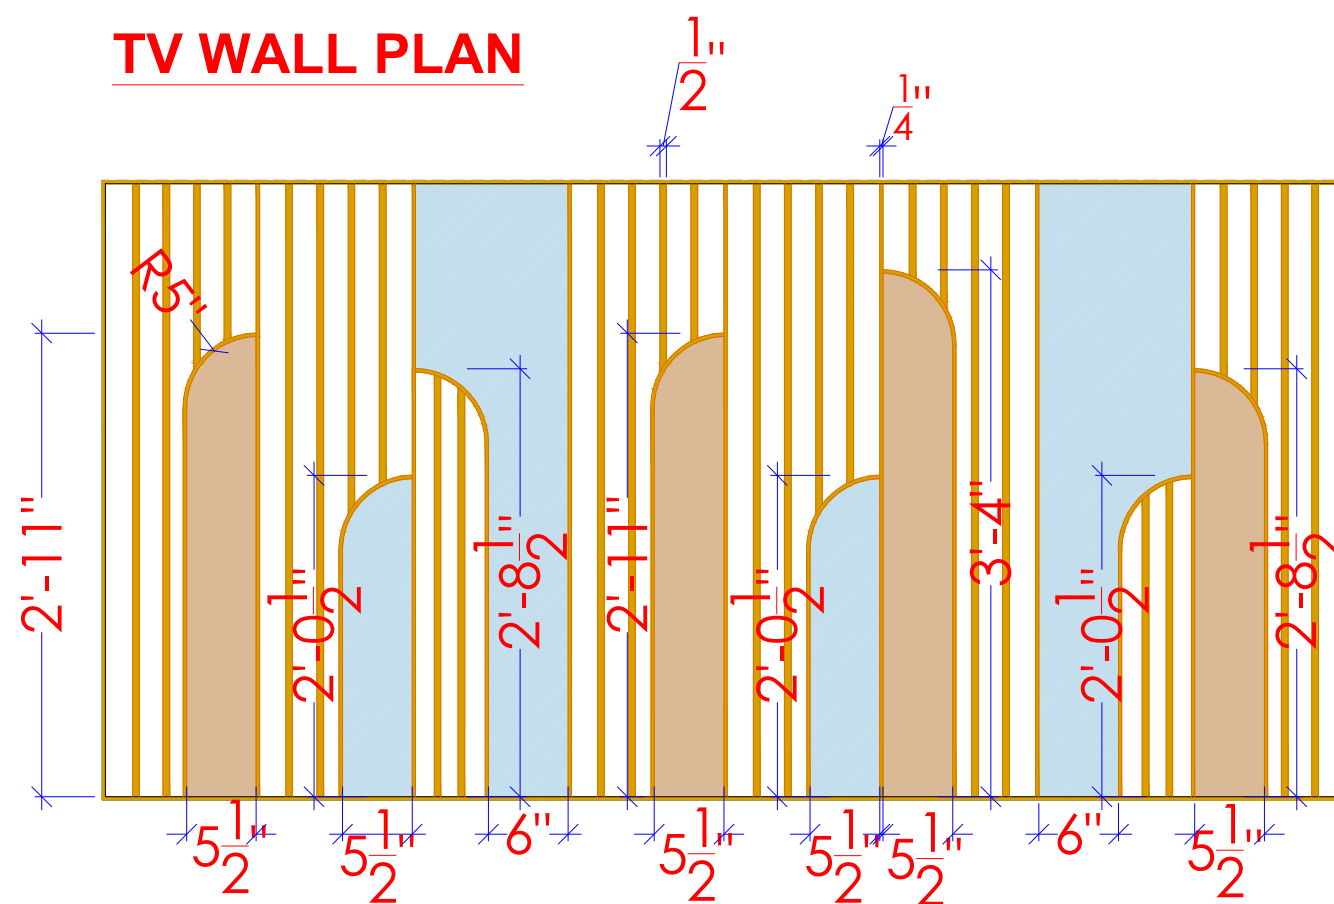

DRAWING TITLE :

LIVING ROOM
TV UNIT DETAIL

NOTES:

- * DO NOT SCALE THE DRAWING.
- * ALL DIMENSIONS ARE IN FEET \ INCHES.
- * ANY DISCREPANCY IN THE DRAWING TO BE BROUGHT IN THE DESIGNER'S NOTICE BEFORE IMPLEMENTATION ON SITE.

SITE ADDRESS:

SAVAD
VADODARA

CLIENT NAME:

RONAK PANCHOLI

DATE:

02-06-2025


NORTH:

DRAWING DETAIL


REVISION NO.	R1	R2	R3
REVISED DATE:	07/02/26		
SCALE:	N.T.S		
DRAWN BY:	ARCHANA		
CHECKED BY:	MITTAL		

	www.mayaspace.studio
	mayaspace.studio@gmail.com
	+918980144077
	@mayaspace.studio




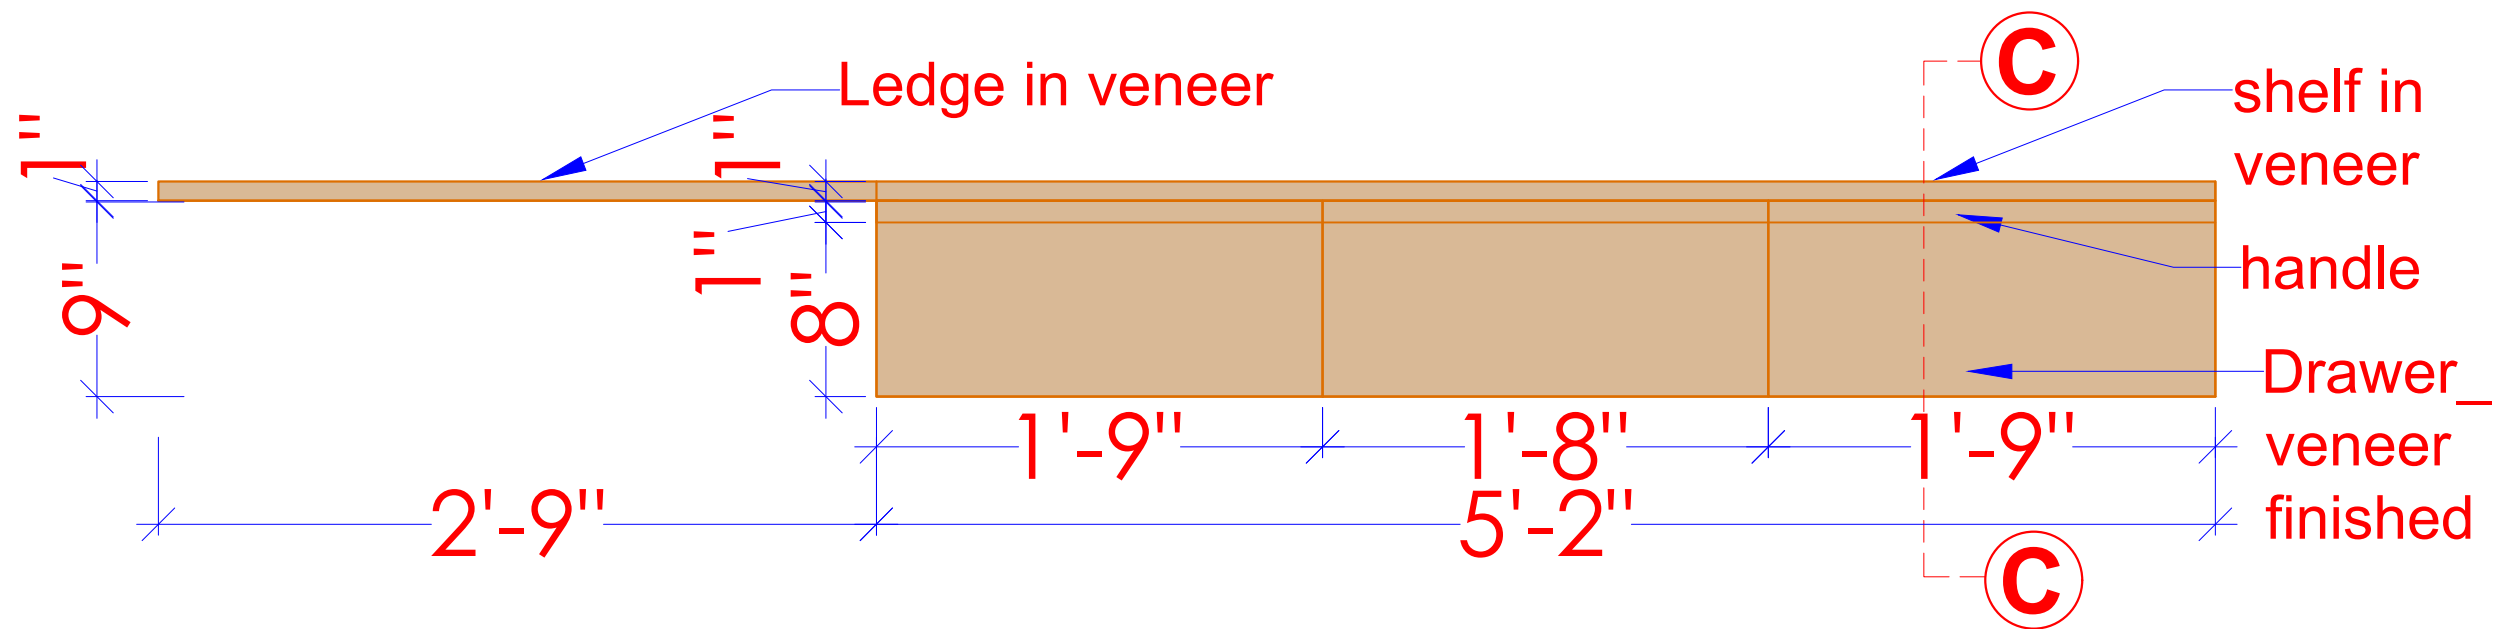


TV UNIT ELEVATION

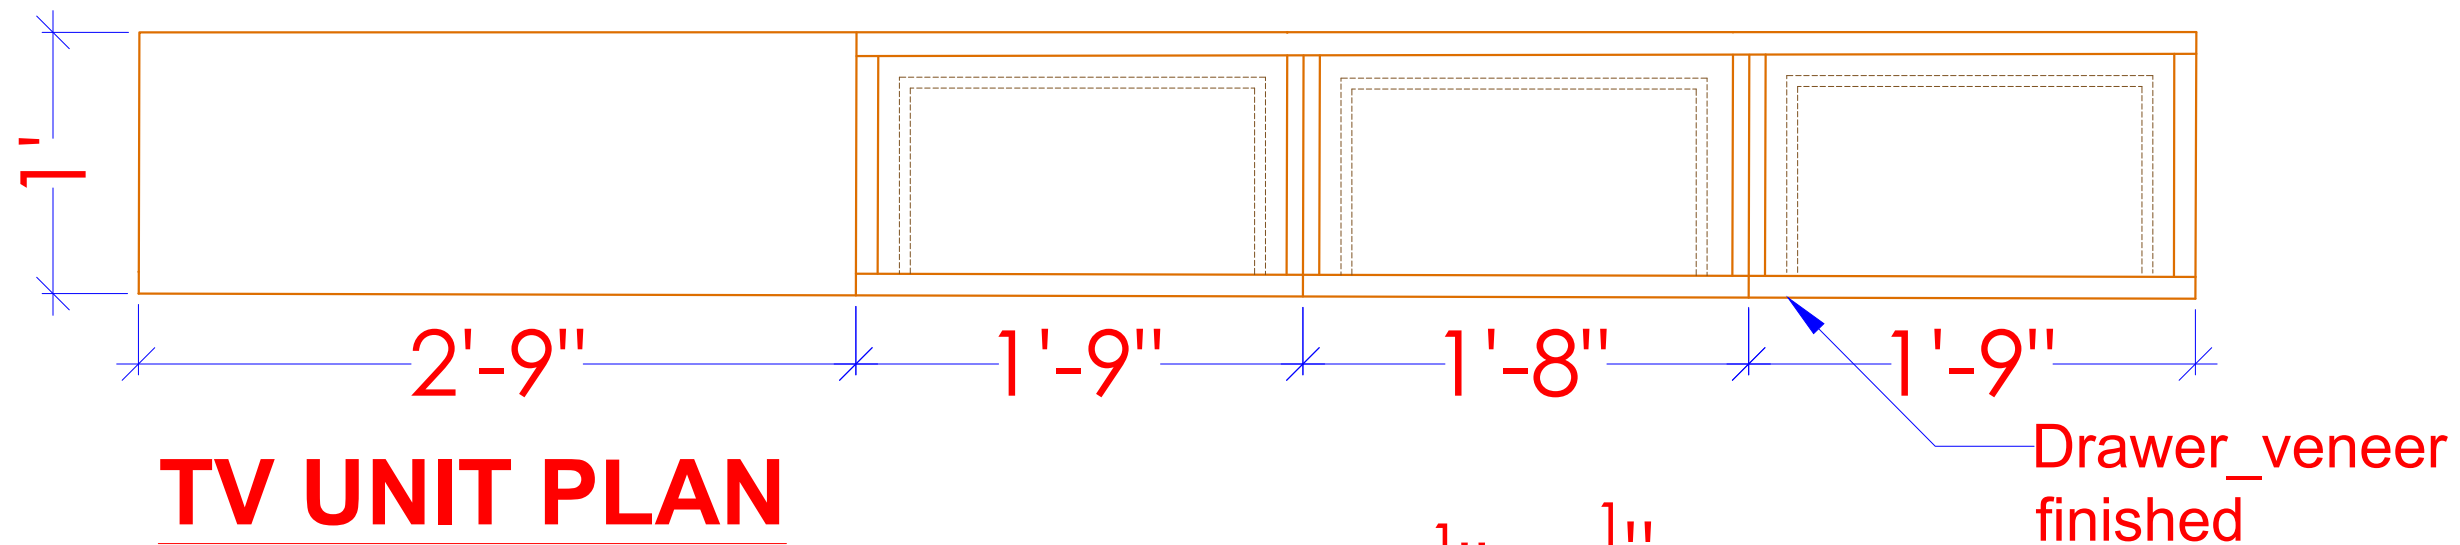

TV UNIT PLAN

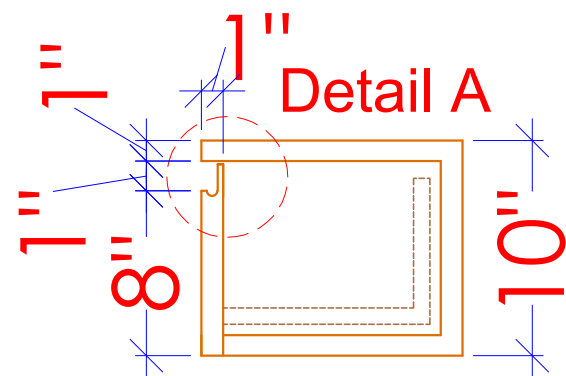

SECTION - CC'

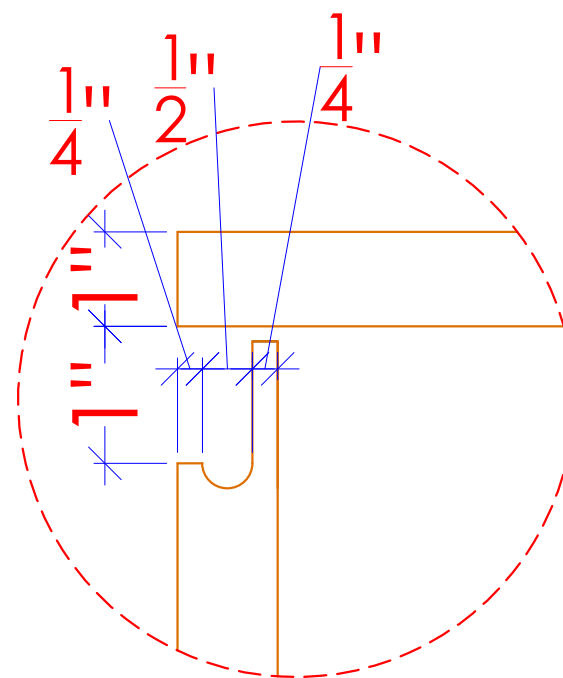

Detail A

DRAWING TITLE :

LIVING ROOM
TV UNIT DETAIL

NOTES:

* DO NOT SCALE THE DRAWING.
* ALL DIMENSIONS ARE IN FEET \ INCHES.
* ANY DISCREPANCY IN THE DRAWING
TO BE BROUGHT IN THE DESIGNER'S
NOTICE BEFORE IMPLEMENTATION
ON SITE.

SITE ADDRESS:

SAVAD
VADODARA

CLIENT NAME:

RONAK PANCHOLI

DATE:

02-06-2025

NORTH:

DRAWING DETAIL

REVISION NO.

R1 R2 R3

REVISED DATE:

07/02/26

SCALE:

N.T.S

DRAWN BY:

ARCHANA

CHECKED BY:

MITTAL

www.mayaspace.studio

mayaspace.studio@gmail.com

+918980144077

@mayaspace.studio



KITCHEN FURNITURE LAYOUT

- * DO NOT SCALE THE DRAWING.
- * ALL DIMENSIONS ARE IN FEET \ INCHES.
- * ANY DISCREPANCY IN THE DRAWING TO BE BROUGHT IN THE DESIGNER'S NOTICE BEFORE IMPLEMENTATION ON SITE.


SAVAD
VADODARA

RONAK PANCHOLI

NORTH: 


REVISION NO.	R1	R2	R3
REVISED DATE:	07/02/26		
SCALE:	N.T.S		
DRAWN BY:	ARCHANA		
CHECKED BY:	MITTAL		

	www.mayaspace.studio
	mayaspace.studio@gmail.com
	+918980144077
	@mayaspace.studio

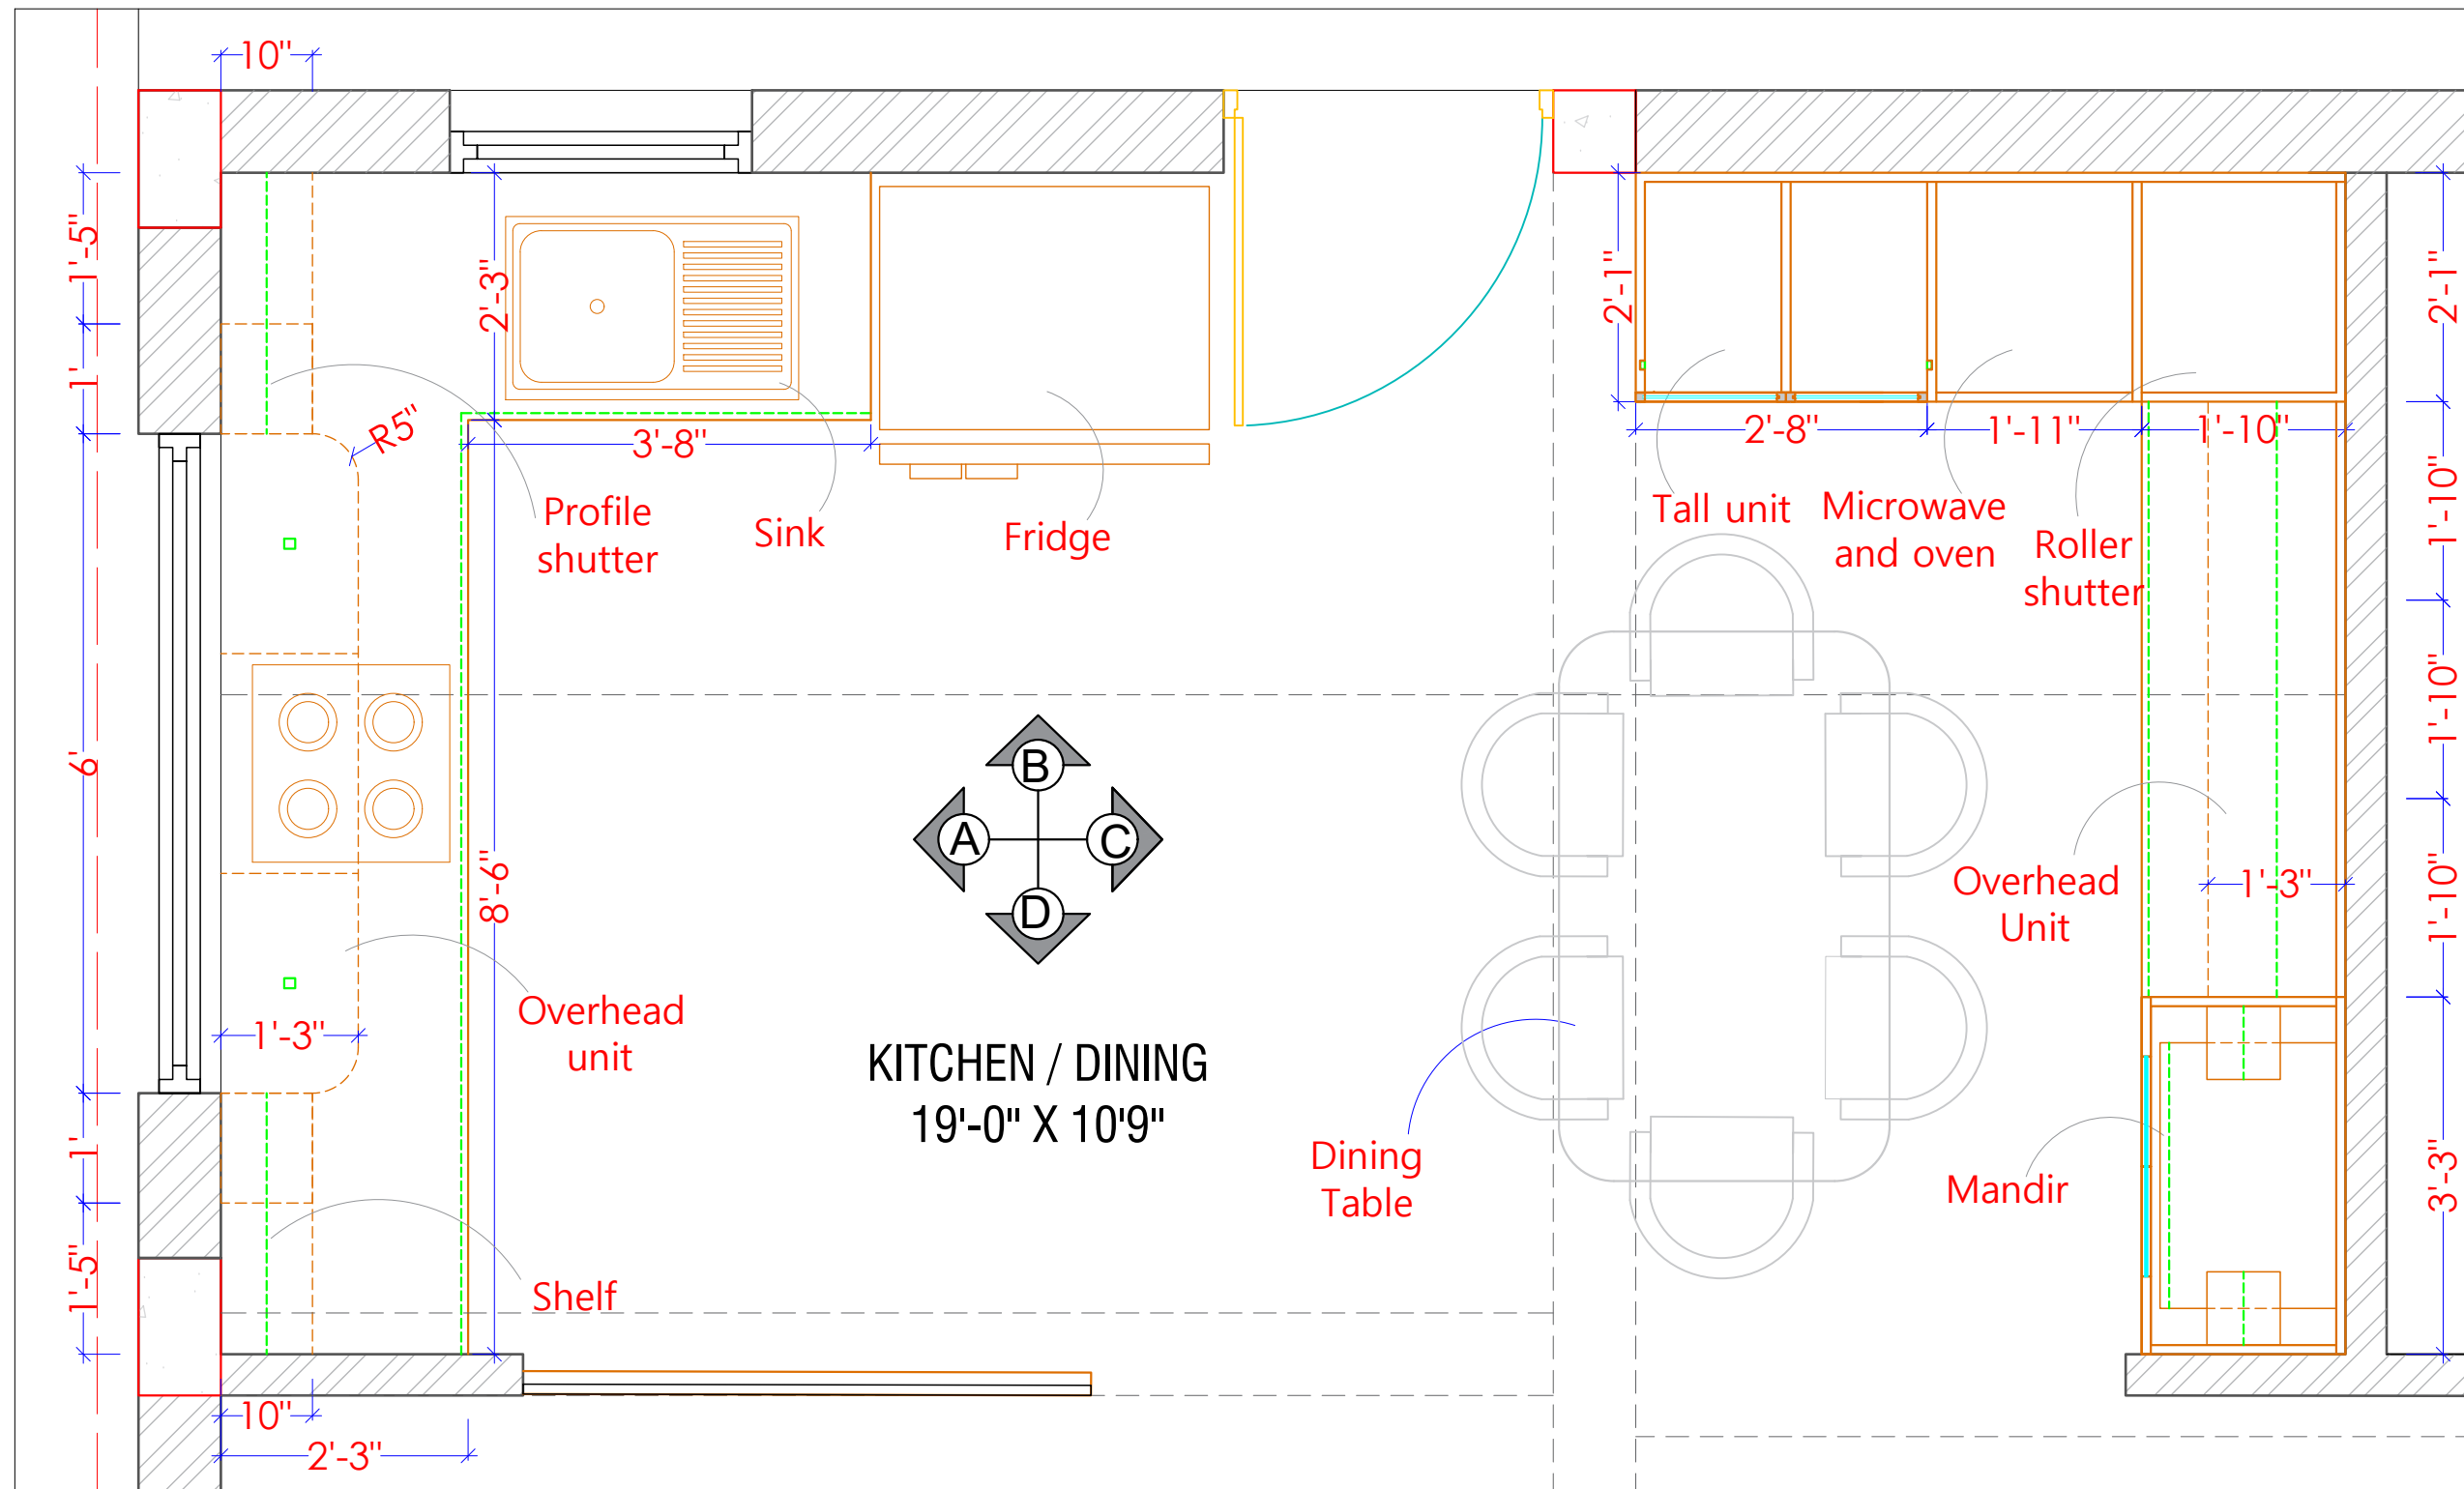

FURNITURE LAYOUT

Provide light point in furniture	
Provide spot point in furniture	

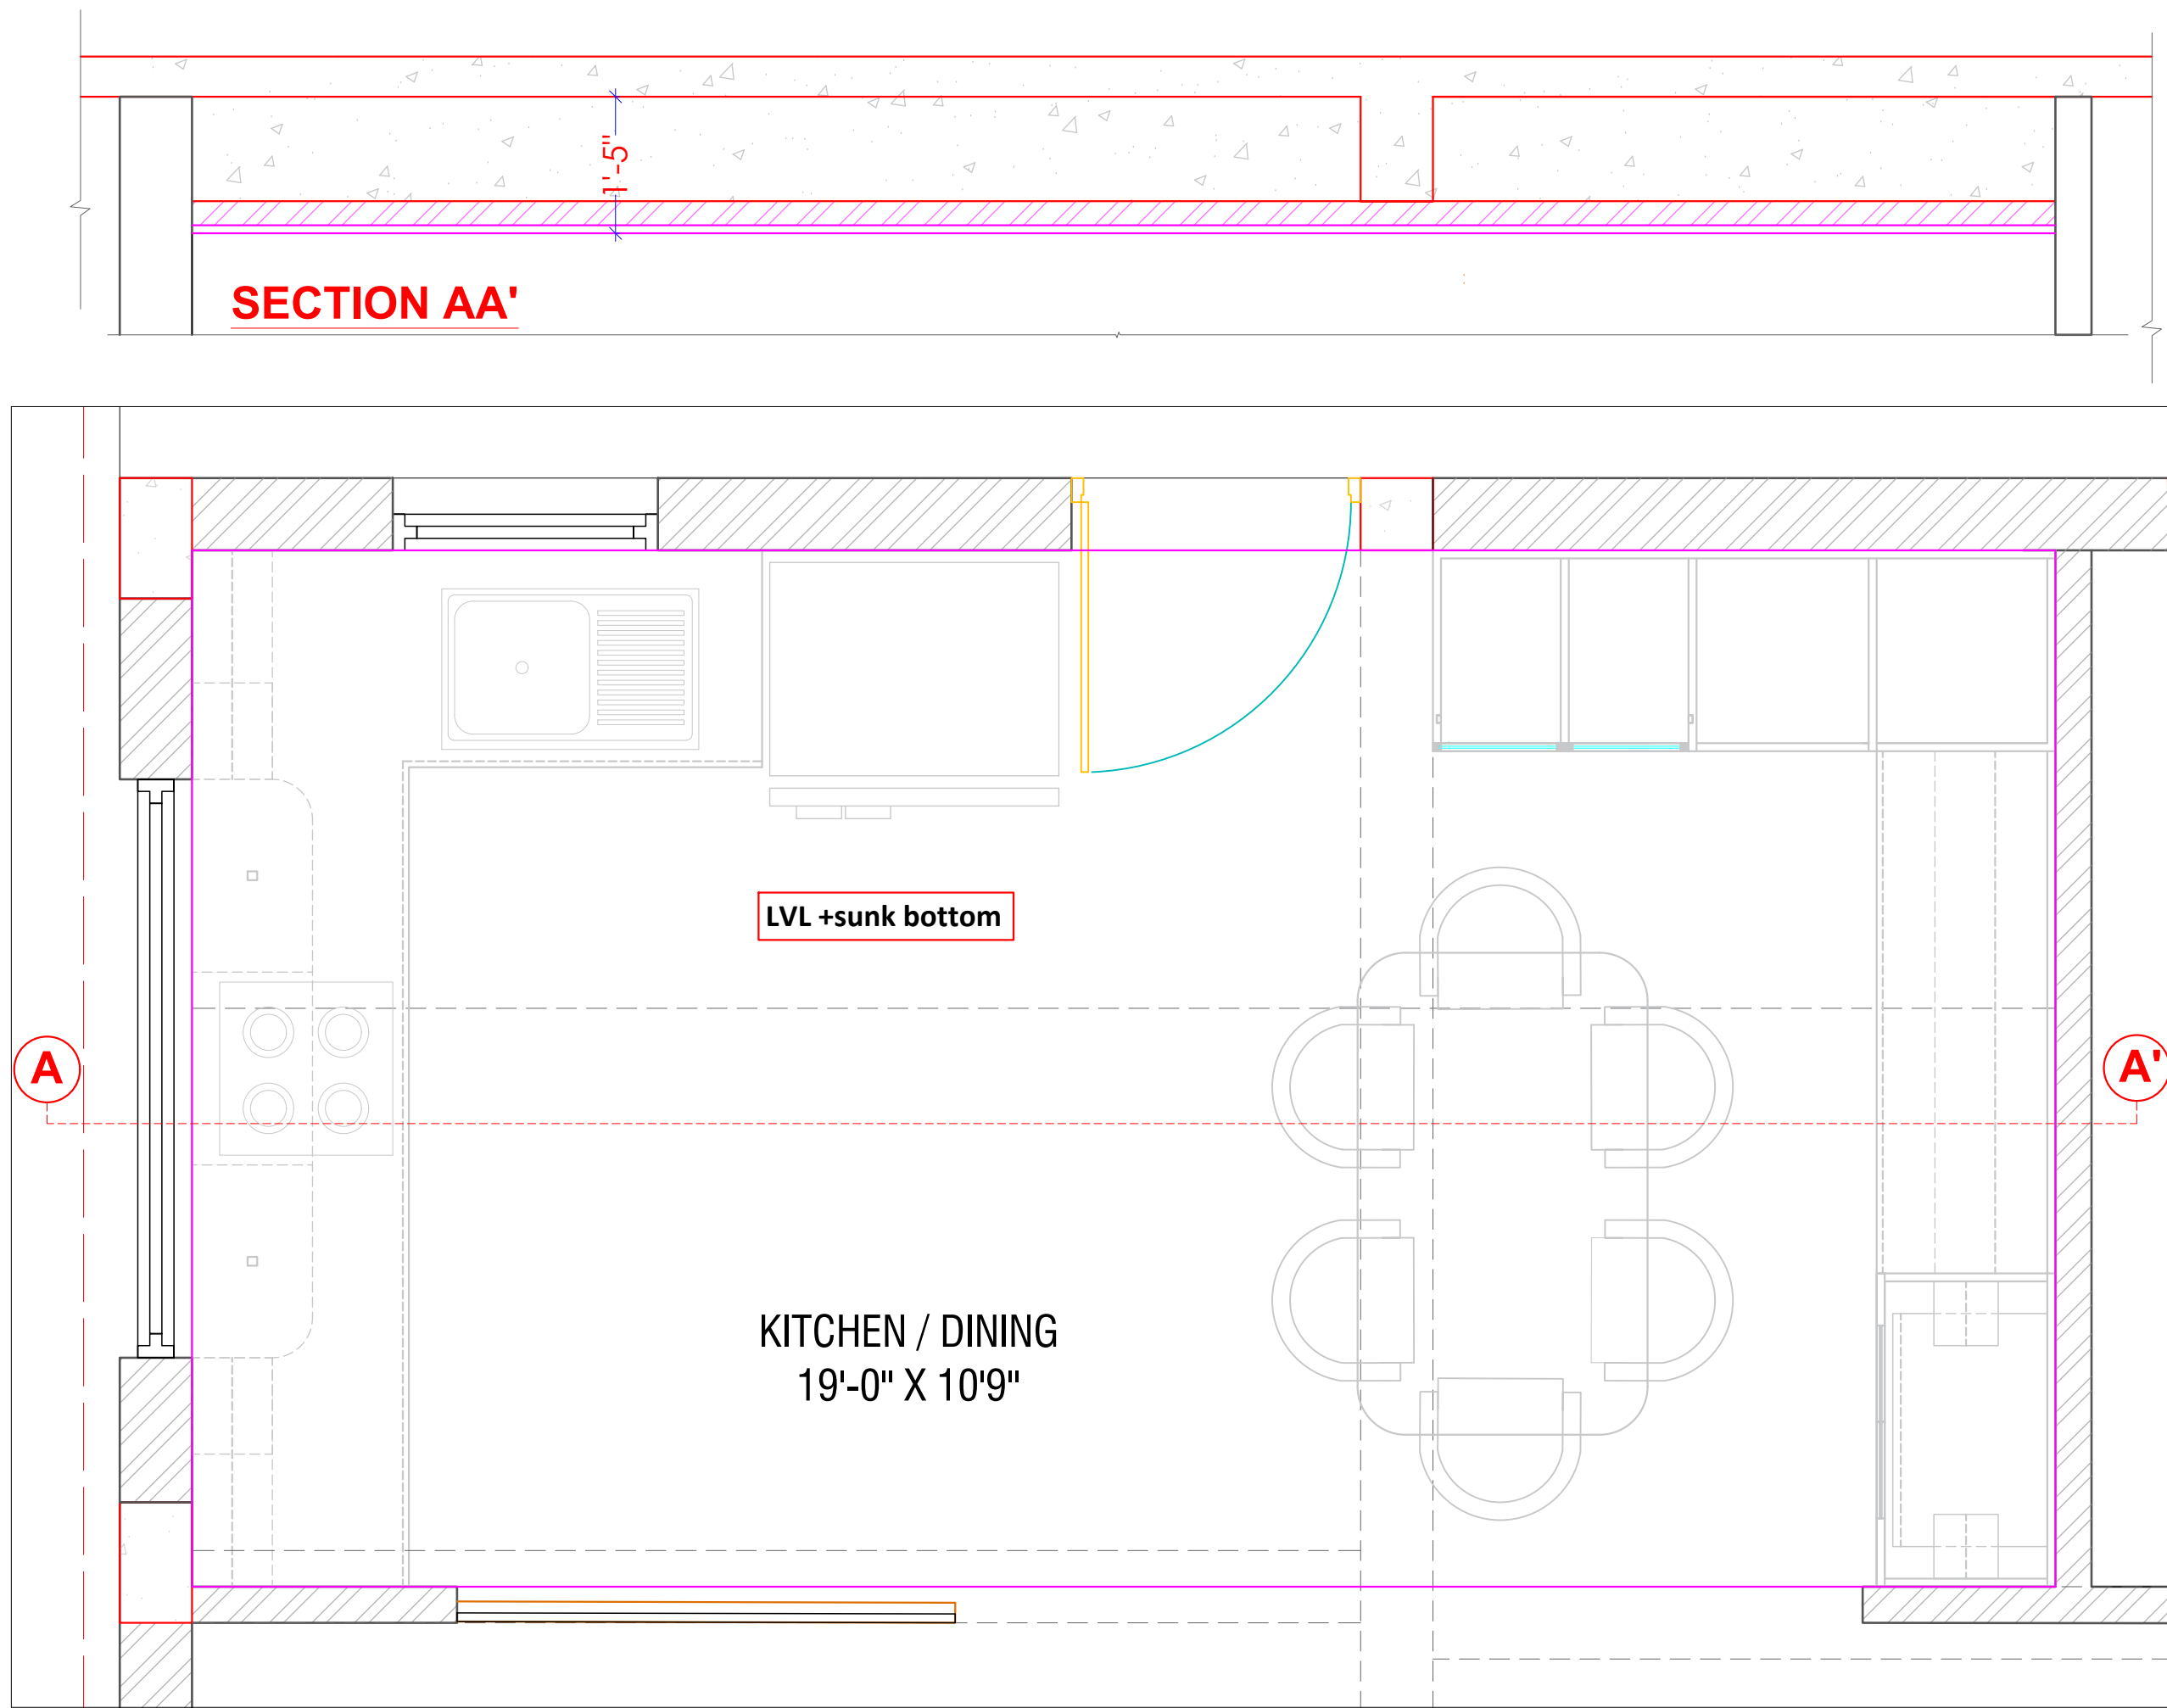

SECTION AA'

LVL +sunk bottom

KITCHEN / DINING
19'-0" X 10'9"

FALSE CEILING LAYOUT

DRAWING TITLE :

KITCHEN
FALSE CEILING LAYOUT

NOTES:

- * DO NOT SCALE THE DRAWING.
- * ALL DIMENSIONS ARE IN FEET \ INCHES.
- * ANY DISCREPENCY IN THE DRAWING TO BE BROUGHT IN THE DESIGNER'S NOTICE BEFORE IMPLEMENTATION ON SITE.

SITE ADDRESS:

SAVAD
VADODARA

CLIENT NAME:

RONAK PANCHOLI

DATE:

02-06-2025

NORTH:



DRAWING DETAIL

REVISION NO.	R1	R2	R3
REVISED DATE:	07/02/26		
SCALE:	N.T.S		
DRAWN BY:	ARCHANA		
CHECKED BY:	MITTAL		

	www.mayaspace.studio
	mayaspace.studio@gmail.com
	+918980144077
	@mayaspace.studio



KITCHEN LIGHTING LAYOUT

- * DO NOT SCALE THE DRAWING.
- * ALL DIMENSIONS ARE IN FEET \ INCHES.
- * ANY DISCREPANCY IN THE DRAWING TO BE BROUGHT IN THE DESIGNER'S NOTICE BEFORE IMPLEMENTATION ON SITE.


SAVAD
VADODARA

RONAK PANCHOLI


NORTH: 

REVISION NO.	R1	R2	R3
REVISED DATE:	07/02/26		
SCALE:	N.T.S		
DRAWN BY:	ARCHANA		
CHECKED BY:	MITTAL		

	www.mayaspace.studio
	mayaspace.studio@gmail.com
	+918980144077
	@mayaspace.studio

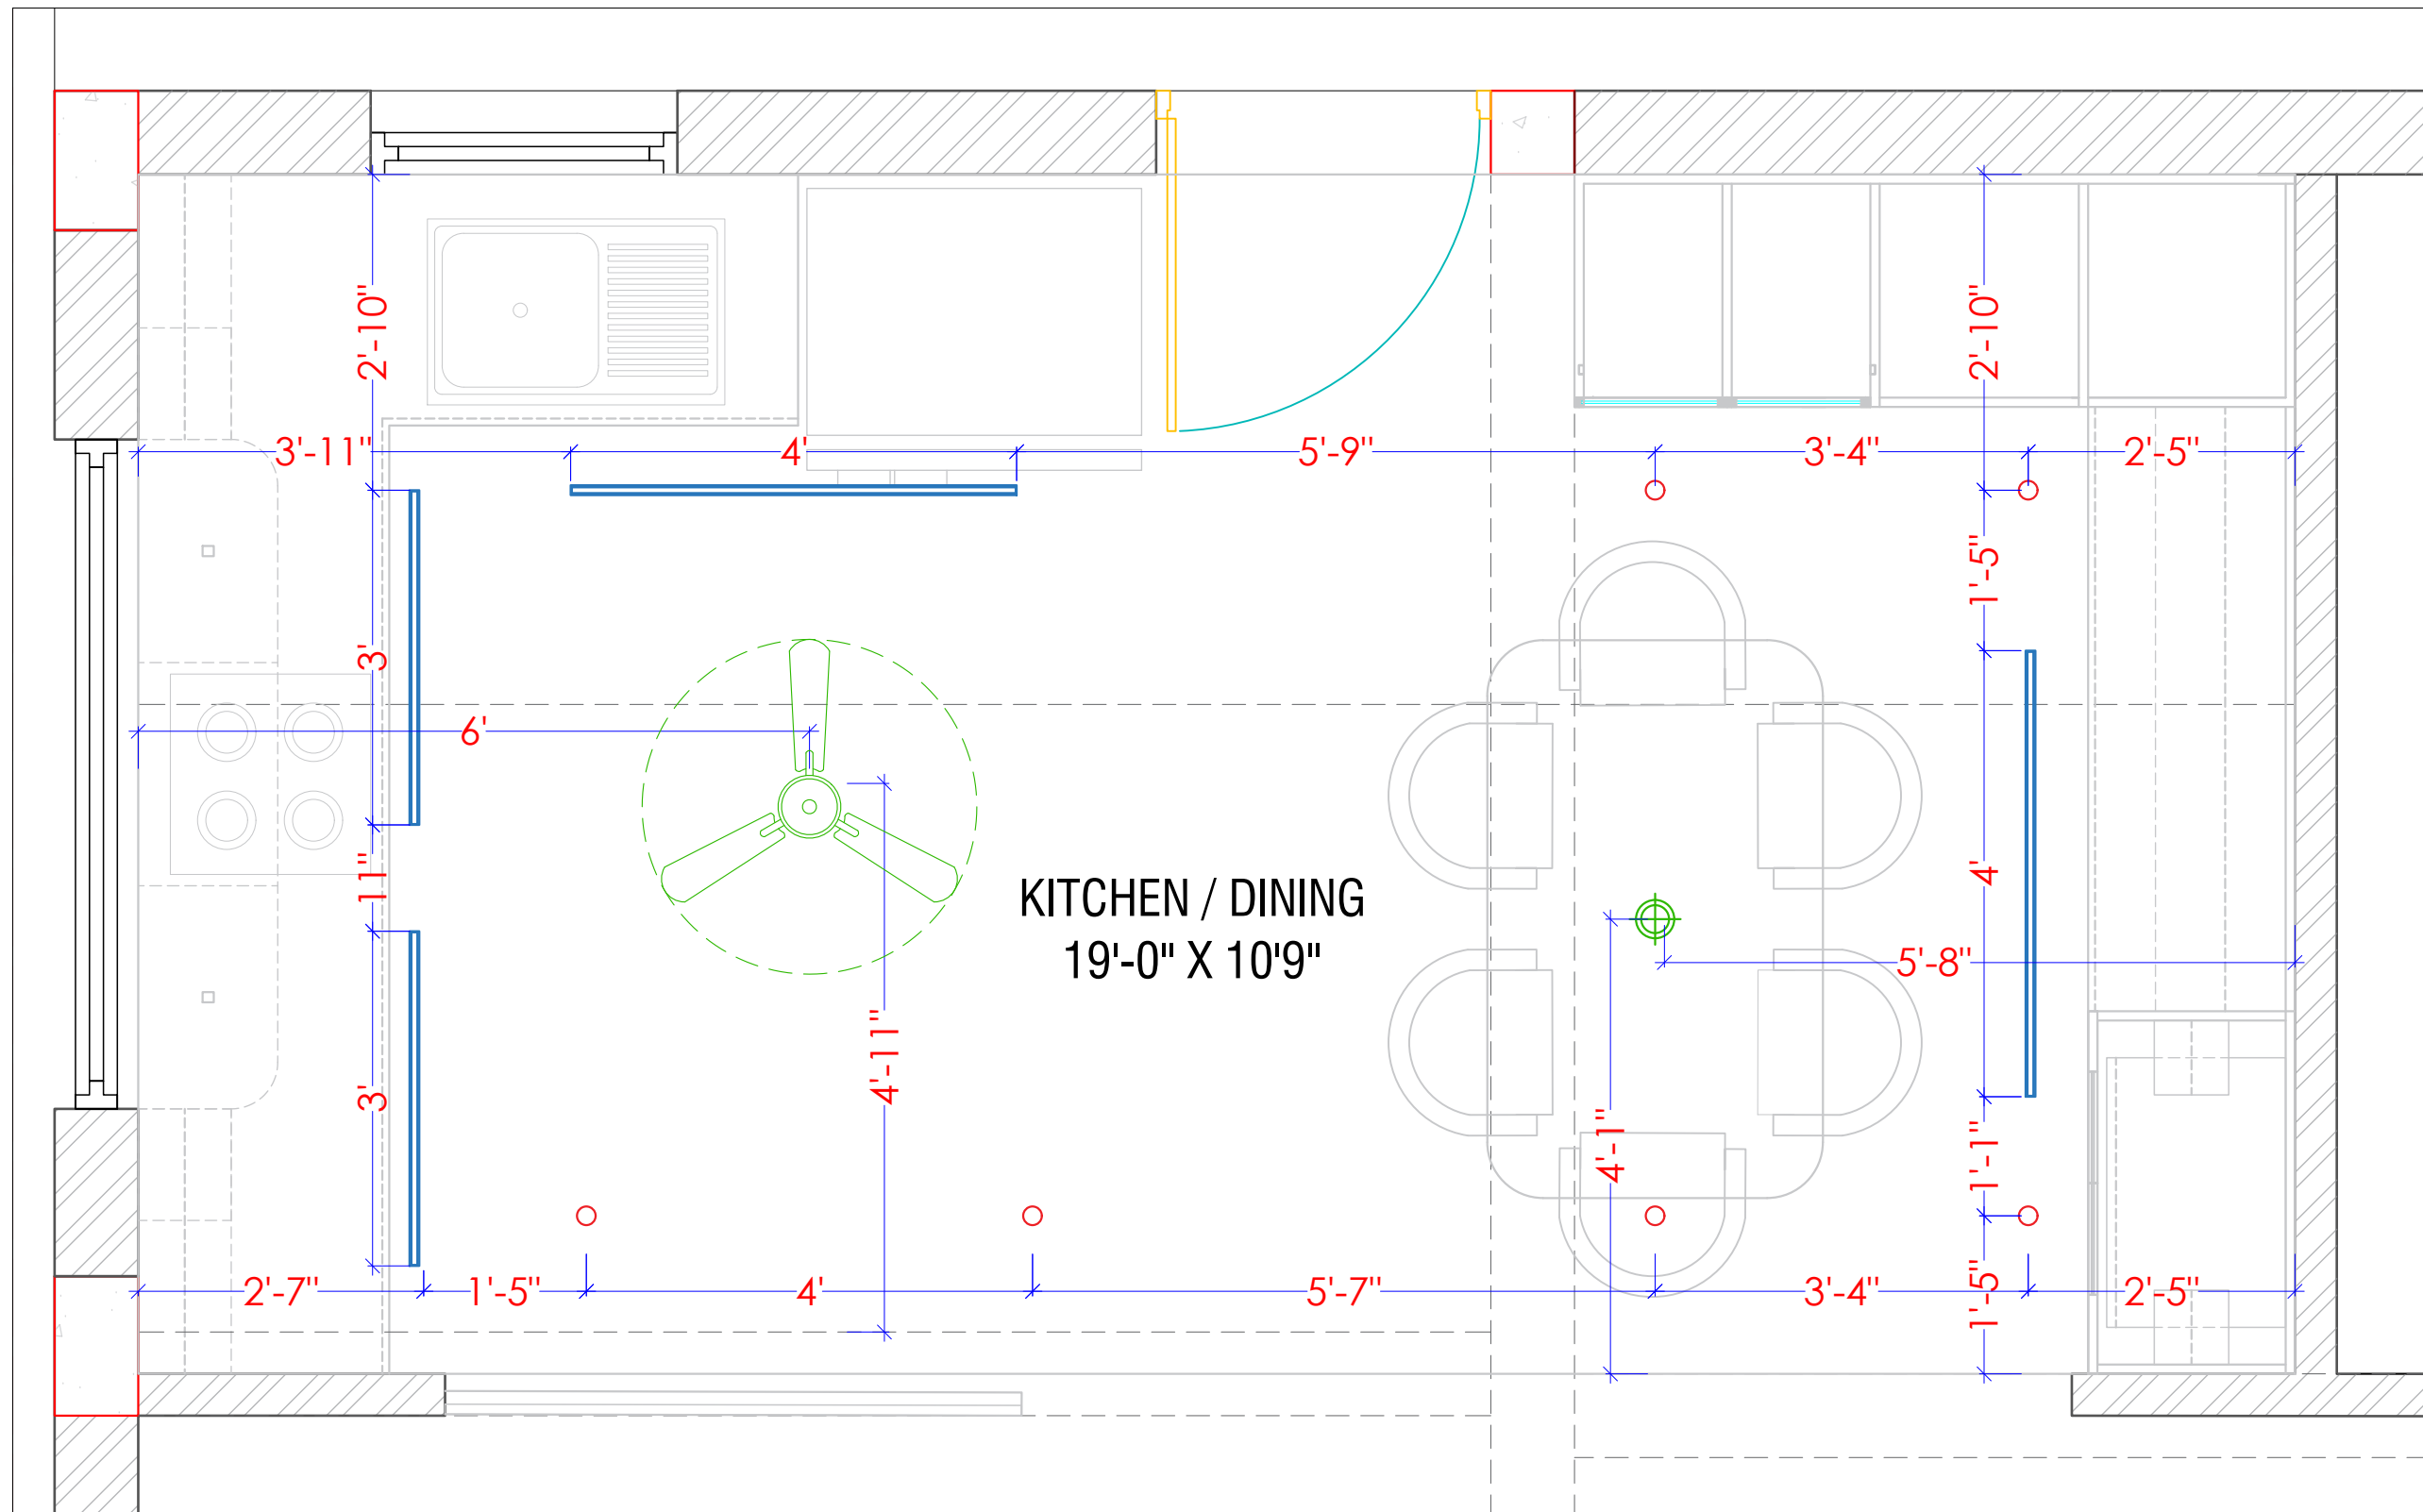

LIGHTING LAYOUT

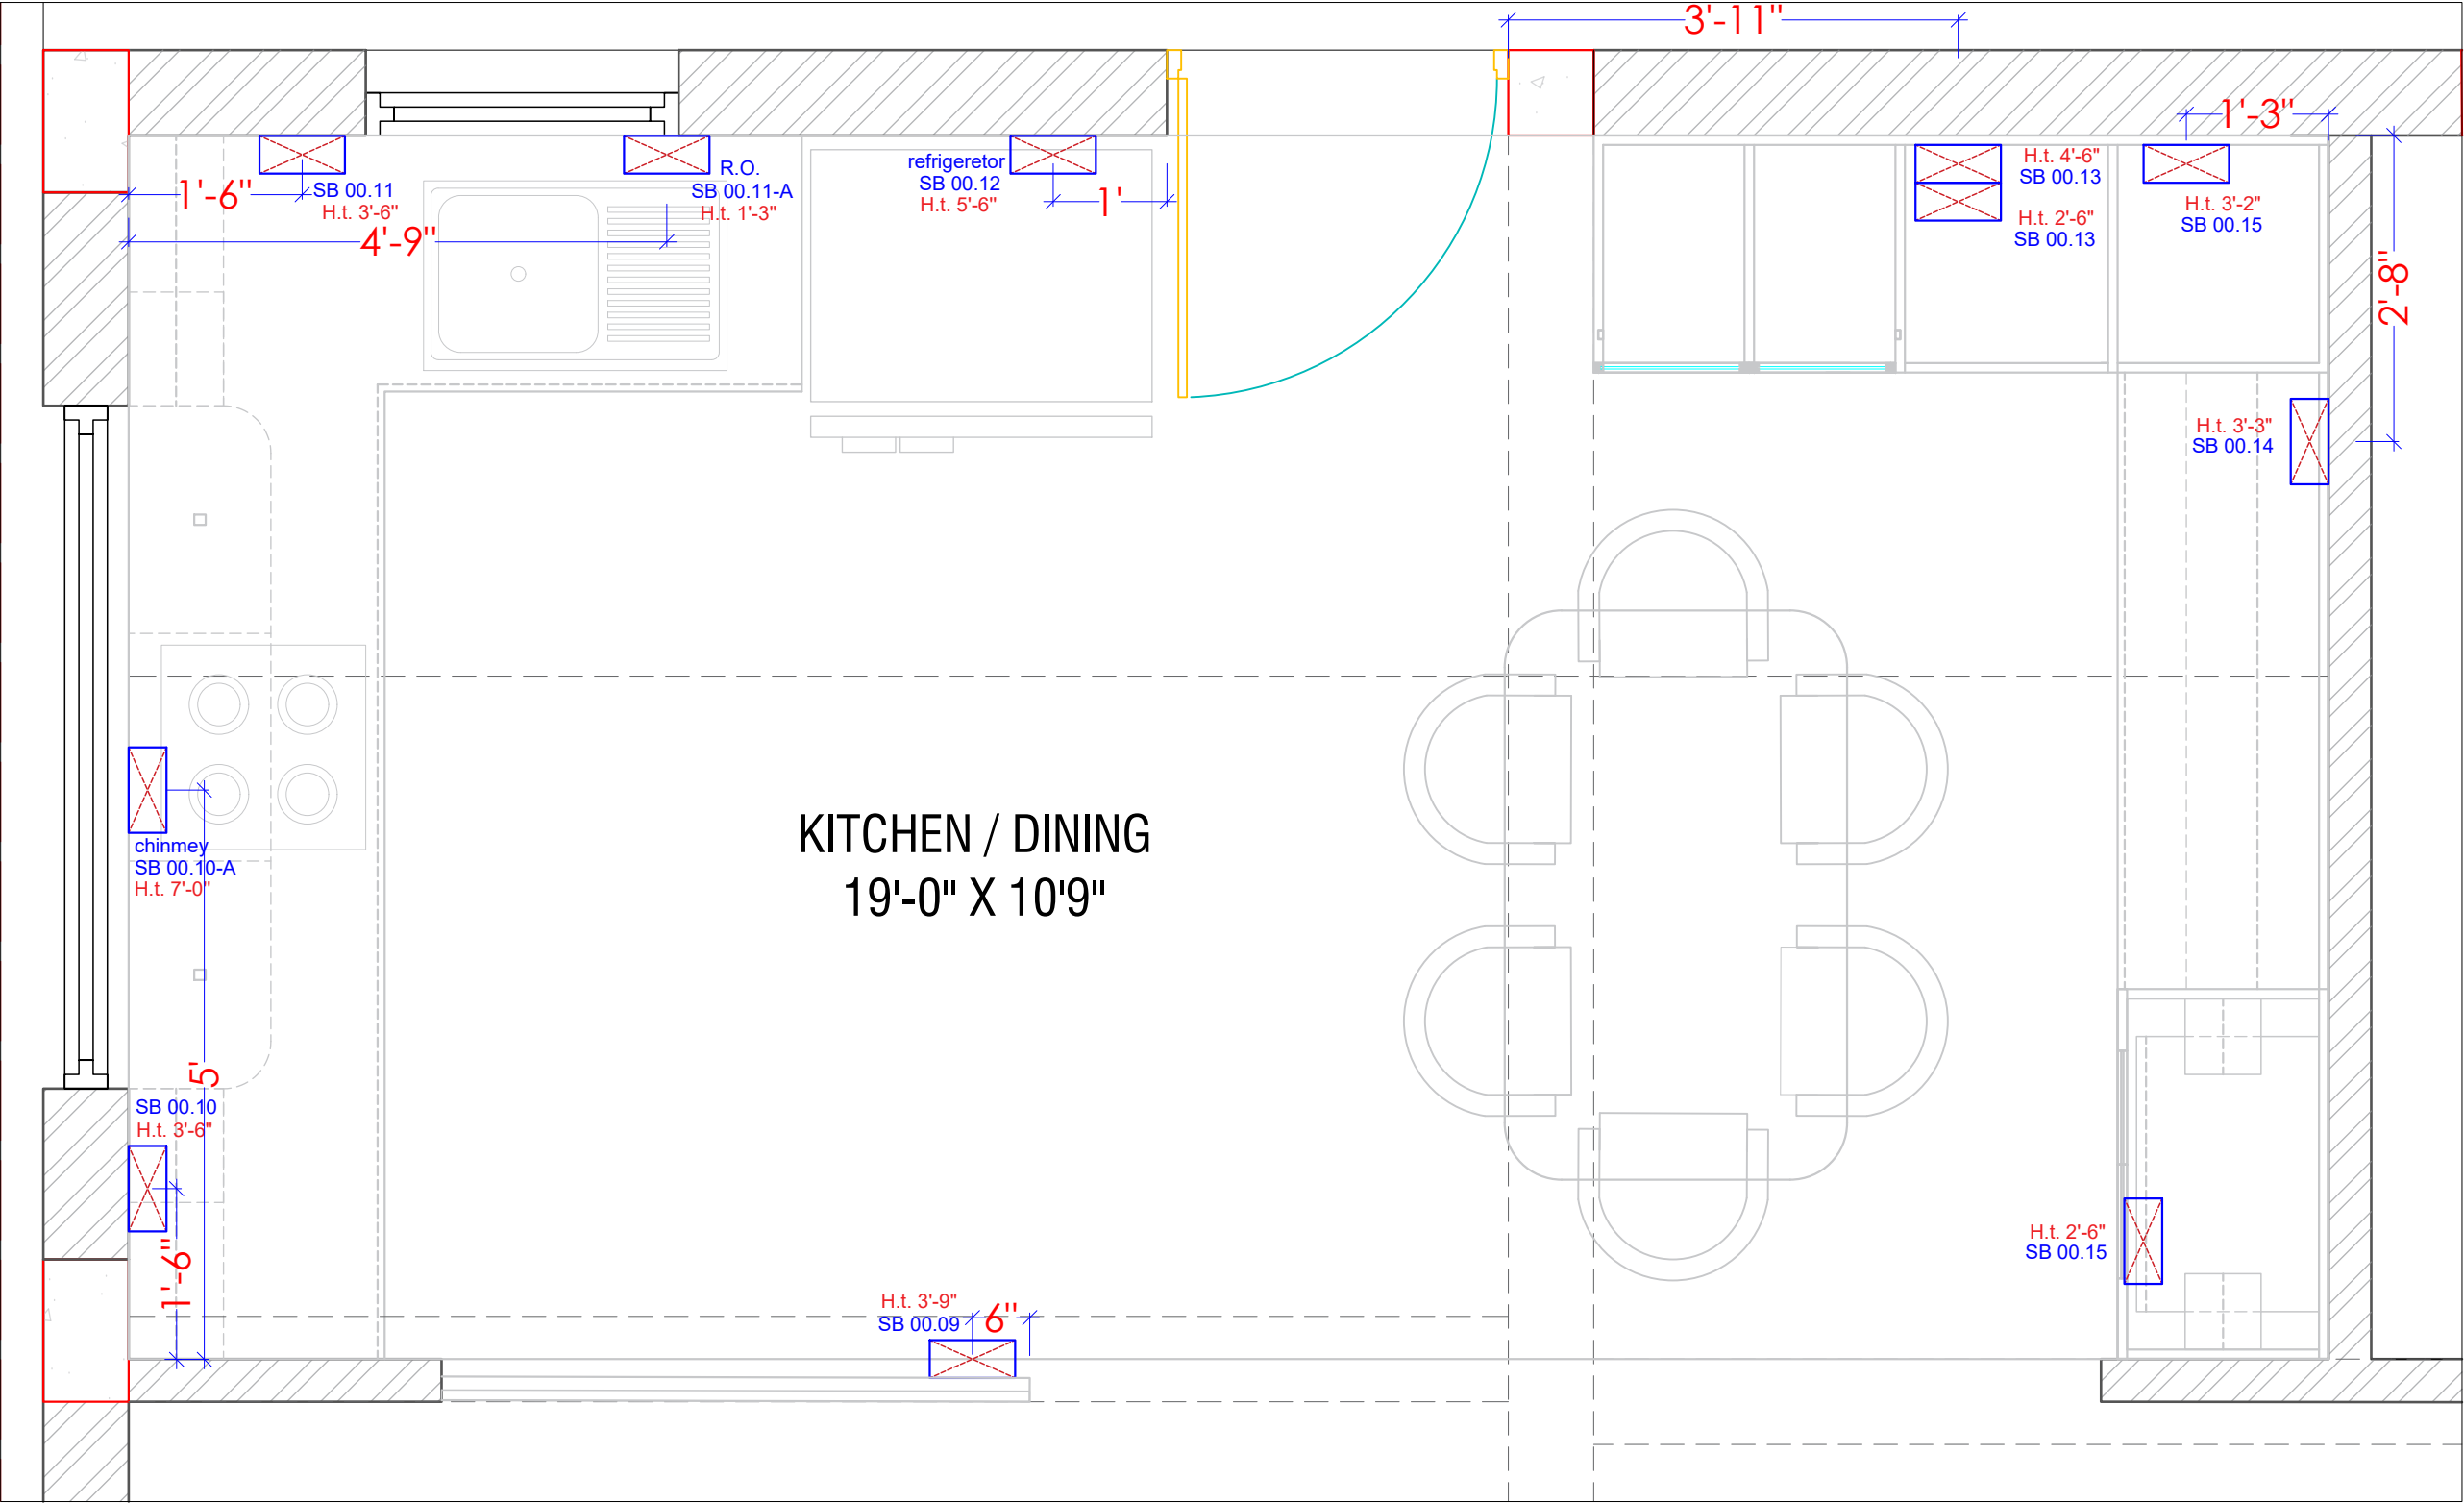

SWITCH BOARD LAYOUT

DRAWING TITLE :

KITCHEN
SB LAYOUT

NOTES:

* DO NOT SCALE THE DRAWING.

* ALL DIMENSIONS ARE IN FEET \ INCHES.

* ANY DISCREPENCY IN THE DRAWING TO BE BROUGHT IN THE DESIGNER'S NOTICE BEFORE IMPLEMENTATION ON SITE.

SITE ADDRESS:

SAVAD
VADODARA

CLIENT NAME:

RONAK PANCHOLI


DATE:	02-06-2025
NORTH:	

DRAWING DETAIL

REVISION NO.	R1 R2 R3
REVISED DATE:	07/02/2026
SCALE:	N.T.S
DRAWN BY:	ARCHANA
CHECKED BY:	MITTAL

	www.mayaspace.studio
	mayaspace.studio@gmail.com
	+918980144077
	@mayaspace.studio

Maya
SPACE STUDIO

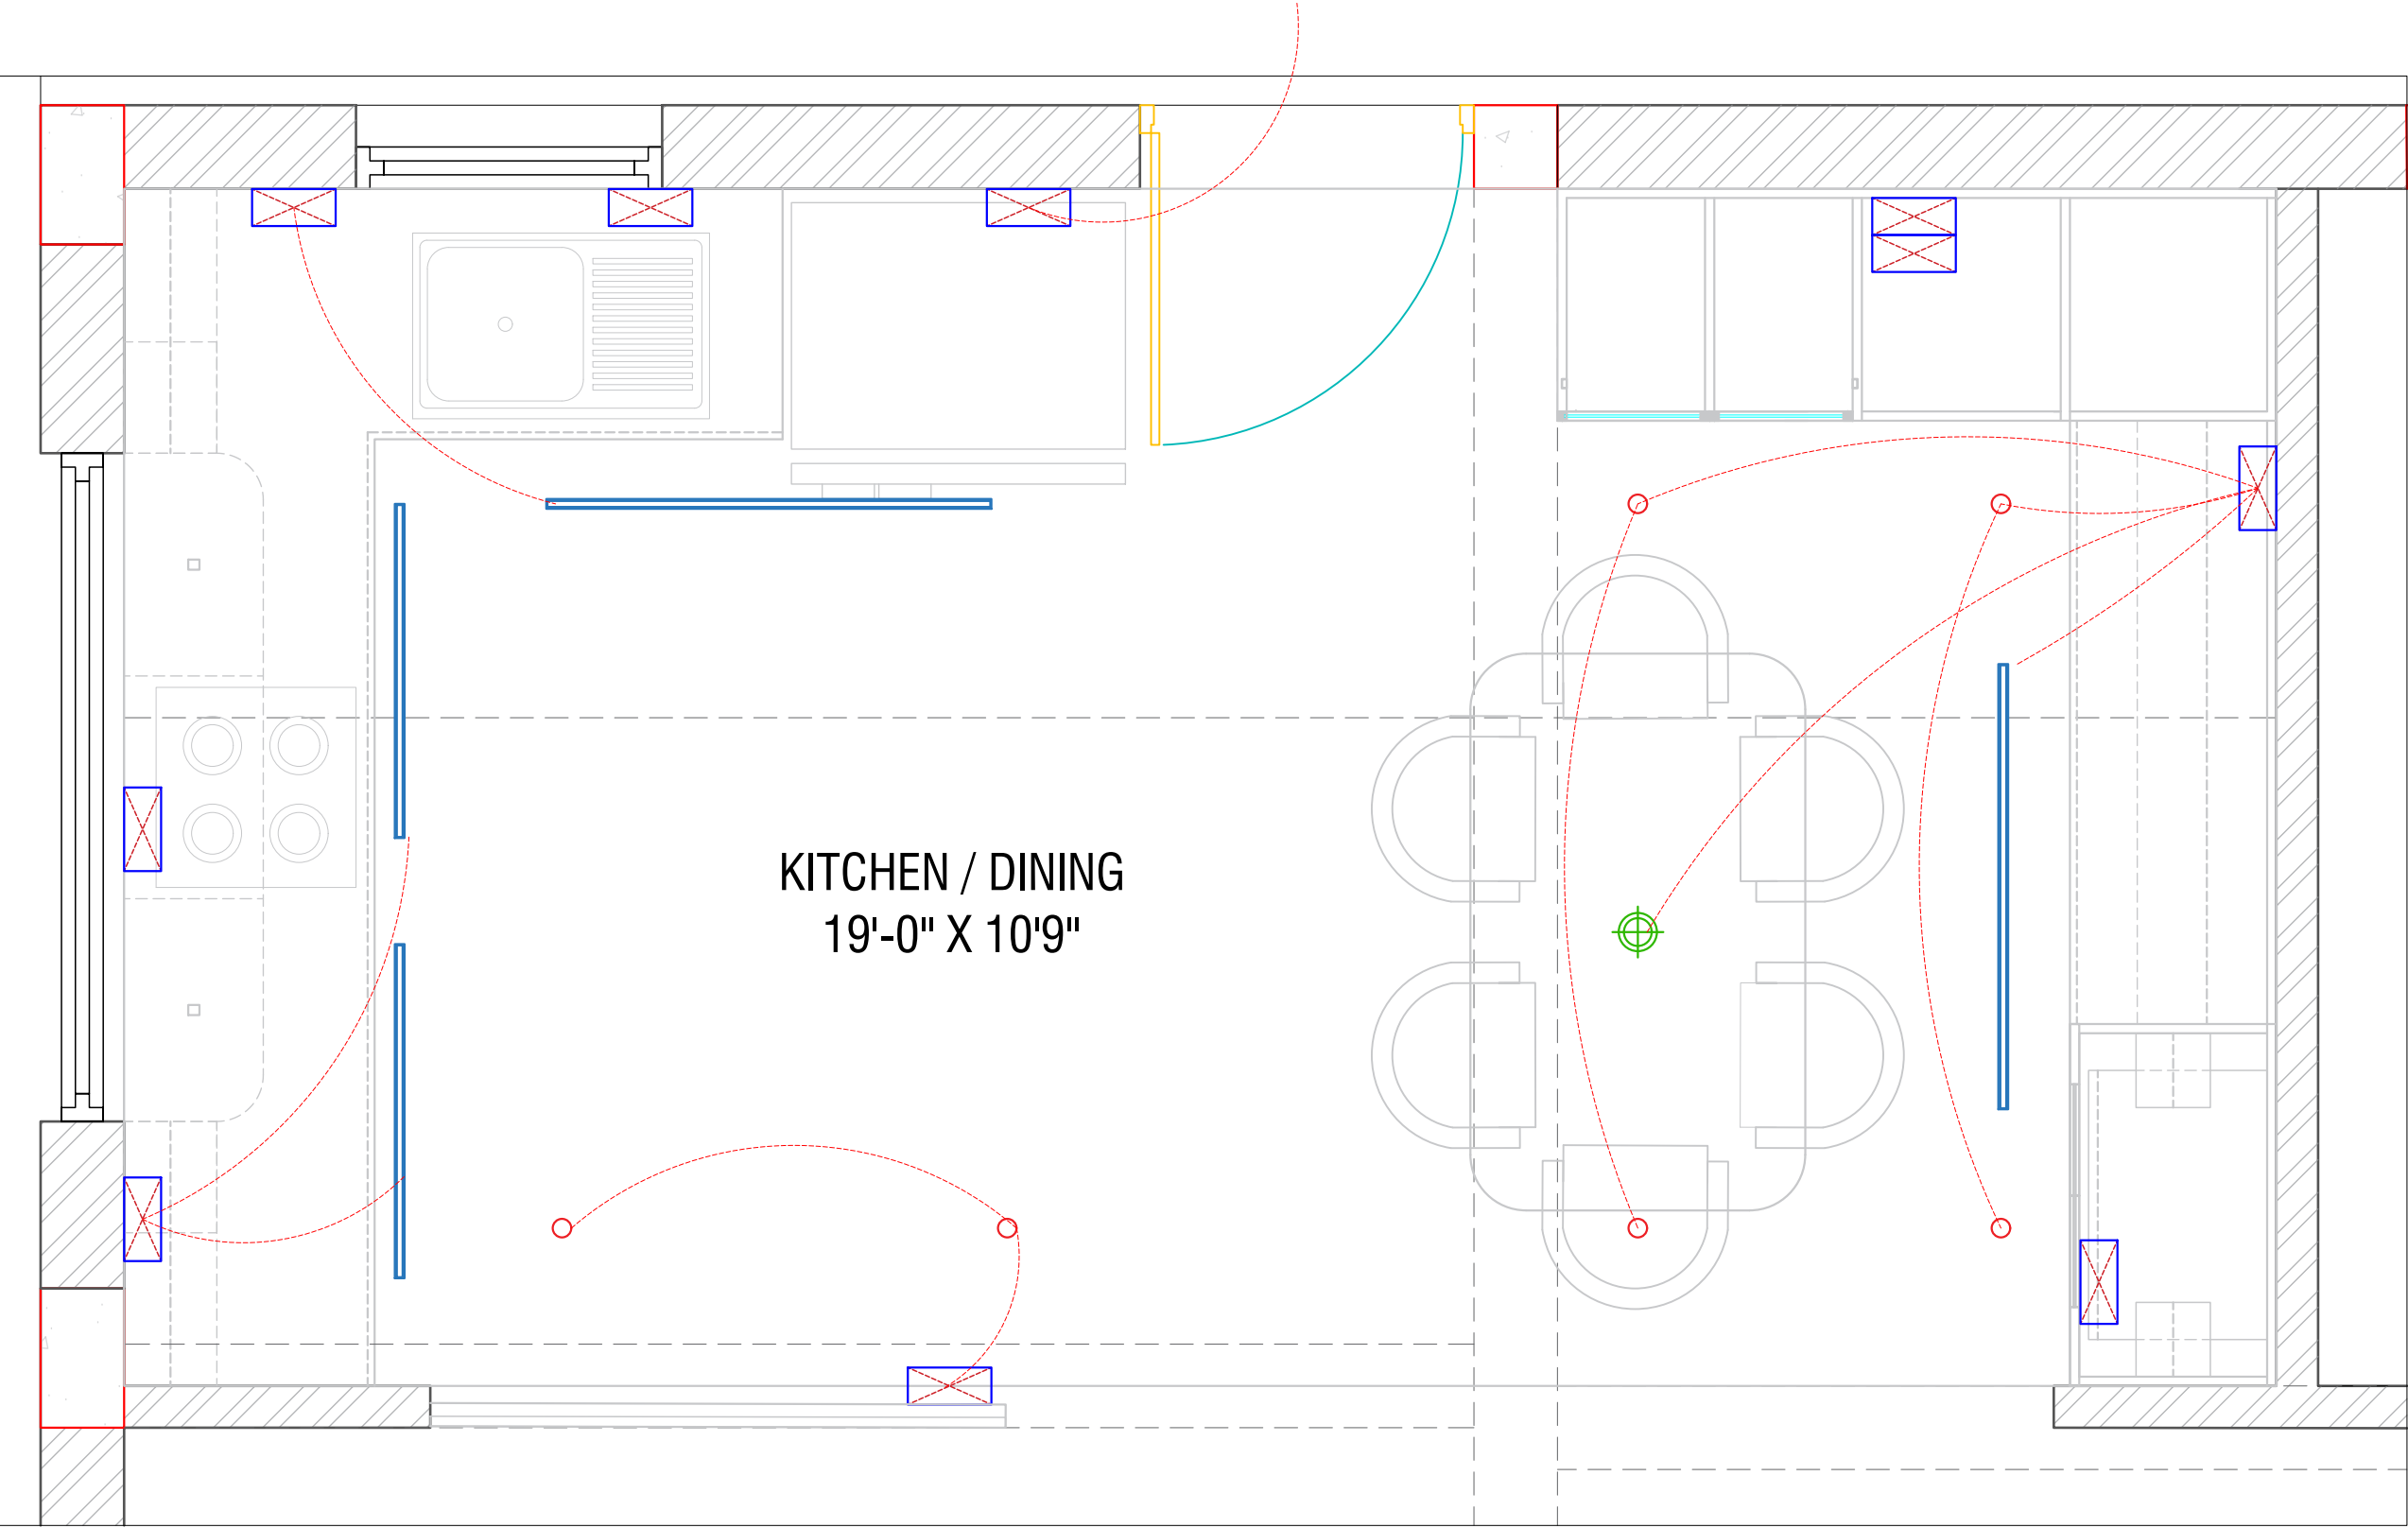

LOOPING LAYOUT

DRAWING TITLE :

KITCHEN
LOOPING LAYOUT

NOTES:

* DO NOT SCALE THE DRAWING.

* ALL DIMENSIONS ARE IN FEET \ INCHES.

* ANY DISCREPANCY IN THE DRAWING TO BE BROUGHT IN THE DESIGNER'S NOTICE BEFORE IMPLEMENTATION ON SITE.

SITE ADDRESS:

SAVAD
VADODARA

CLIENT NAME:

RONAK PANCHOLI

DATE:	02-06-2025
NORTH:	

DRAWING DETAIL

REVISION NO.	R1 R2 R3
REVISED DATE:	07/02/26
SCALE:	N.T.S
DRAWN BY:	ARCHANA
CHECKED BY:	MITTAL

	www.mayaspace.studio
	mayaspace.studio@gmail.com
	+918980144077
	@mayaspace.studio

Maya
SPACE STUDIO

DRAWING TITLE :

KITCHEN ELEVATION- A

NOTES:

- * DO NOT SCALE THE DRAWING.
- * ALL DIMENSIONS ARE IN FEET \ INCHES.
- * ANY DISCREPANCY IN THE DRAWING TO BE BROUGHT IN THE DESIGNER'S NOTICE BEFORE IMPLEMENTATION ON SITE.

SITE ADDRESS:

SAVAD
VADODARA

CLIENT NAME:

RONAK PANCHOLI



DATE: 02-06-2025

NORTH:


DRAWING DETAIL

REVISION NO.	☐ R1 ☐ R2 ☐ R3
REVISED DATE:	07/02/2026
SCALE:	N.T.S
DRAWN BY:	ARCHANA
CHECKED BY:	MITTAL

	www.mayaspace.studio
	mayaspace.studio@gmail.com
	+918980144077
	@mayaspace.studio

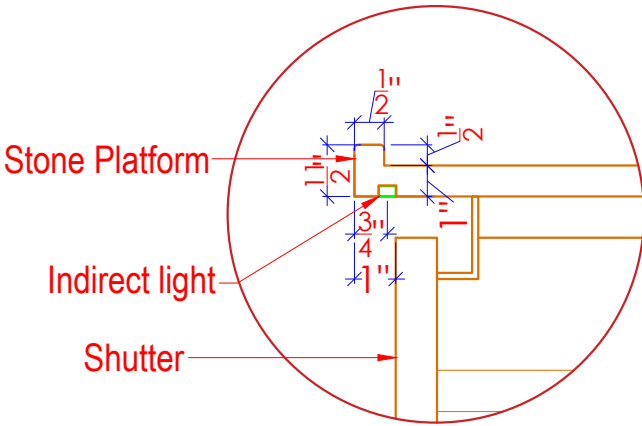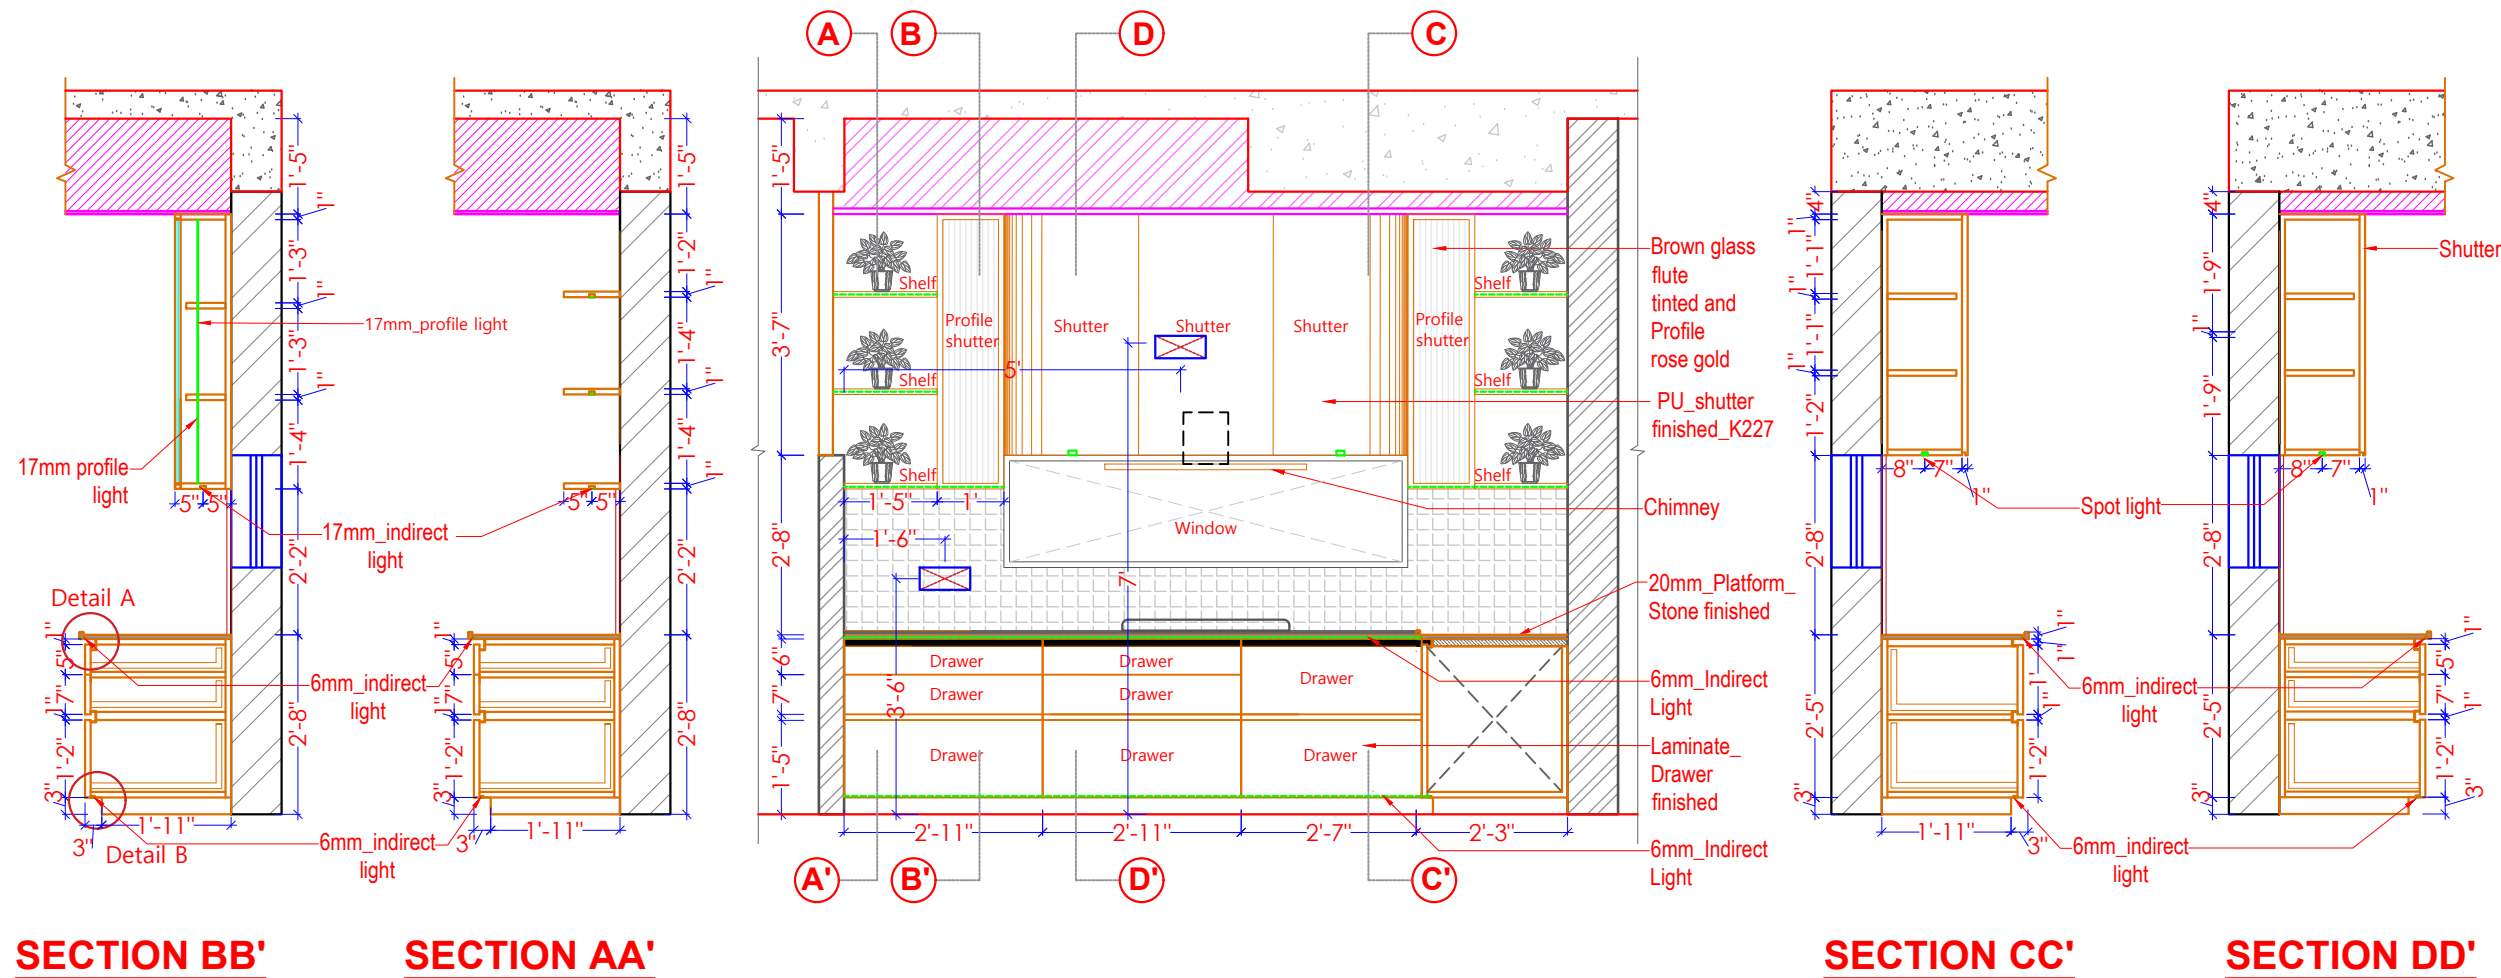

Detail A

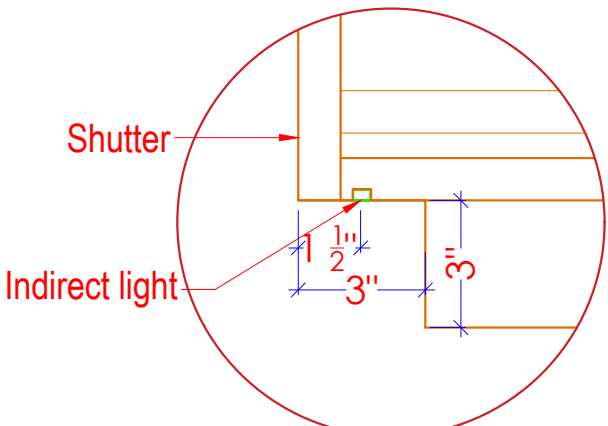

Detail B

ELEVATION - A

DRAWING TITLE :

KITCHEN
ELEVATION- B

NOTES:

- * DO NOT SCALE THE DRAWING.
- * ALL DIMENSIONS ARE IN FEET \ INCHES.
- * ANY DISCREPANCY IN THE DRAWING TO BE BROUGHT IN THE DESIGNER'S NOTICE BEFORE IMPLEMENTATION ON SITE.

SITE ADDRESS:

SAVAD
VADODARA

CLIENT NAME:

RONAK PANCHOLI


DATE: 02-06-2025

NORTH:

DRAWING DETAIL

REVISION NO.	R1	R2	R3
REVISED DATE:	07/02/2026		
SCALE:	N.T.S		
DRAWN BY:	ARCHANA		
CHECKED BY:	MITTAL		

	www.mayaspace.studio
	mayaspace.studio@gmail.com
	+918980144077
	@mayaspace.studio

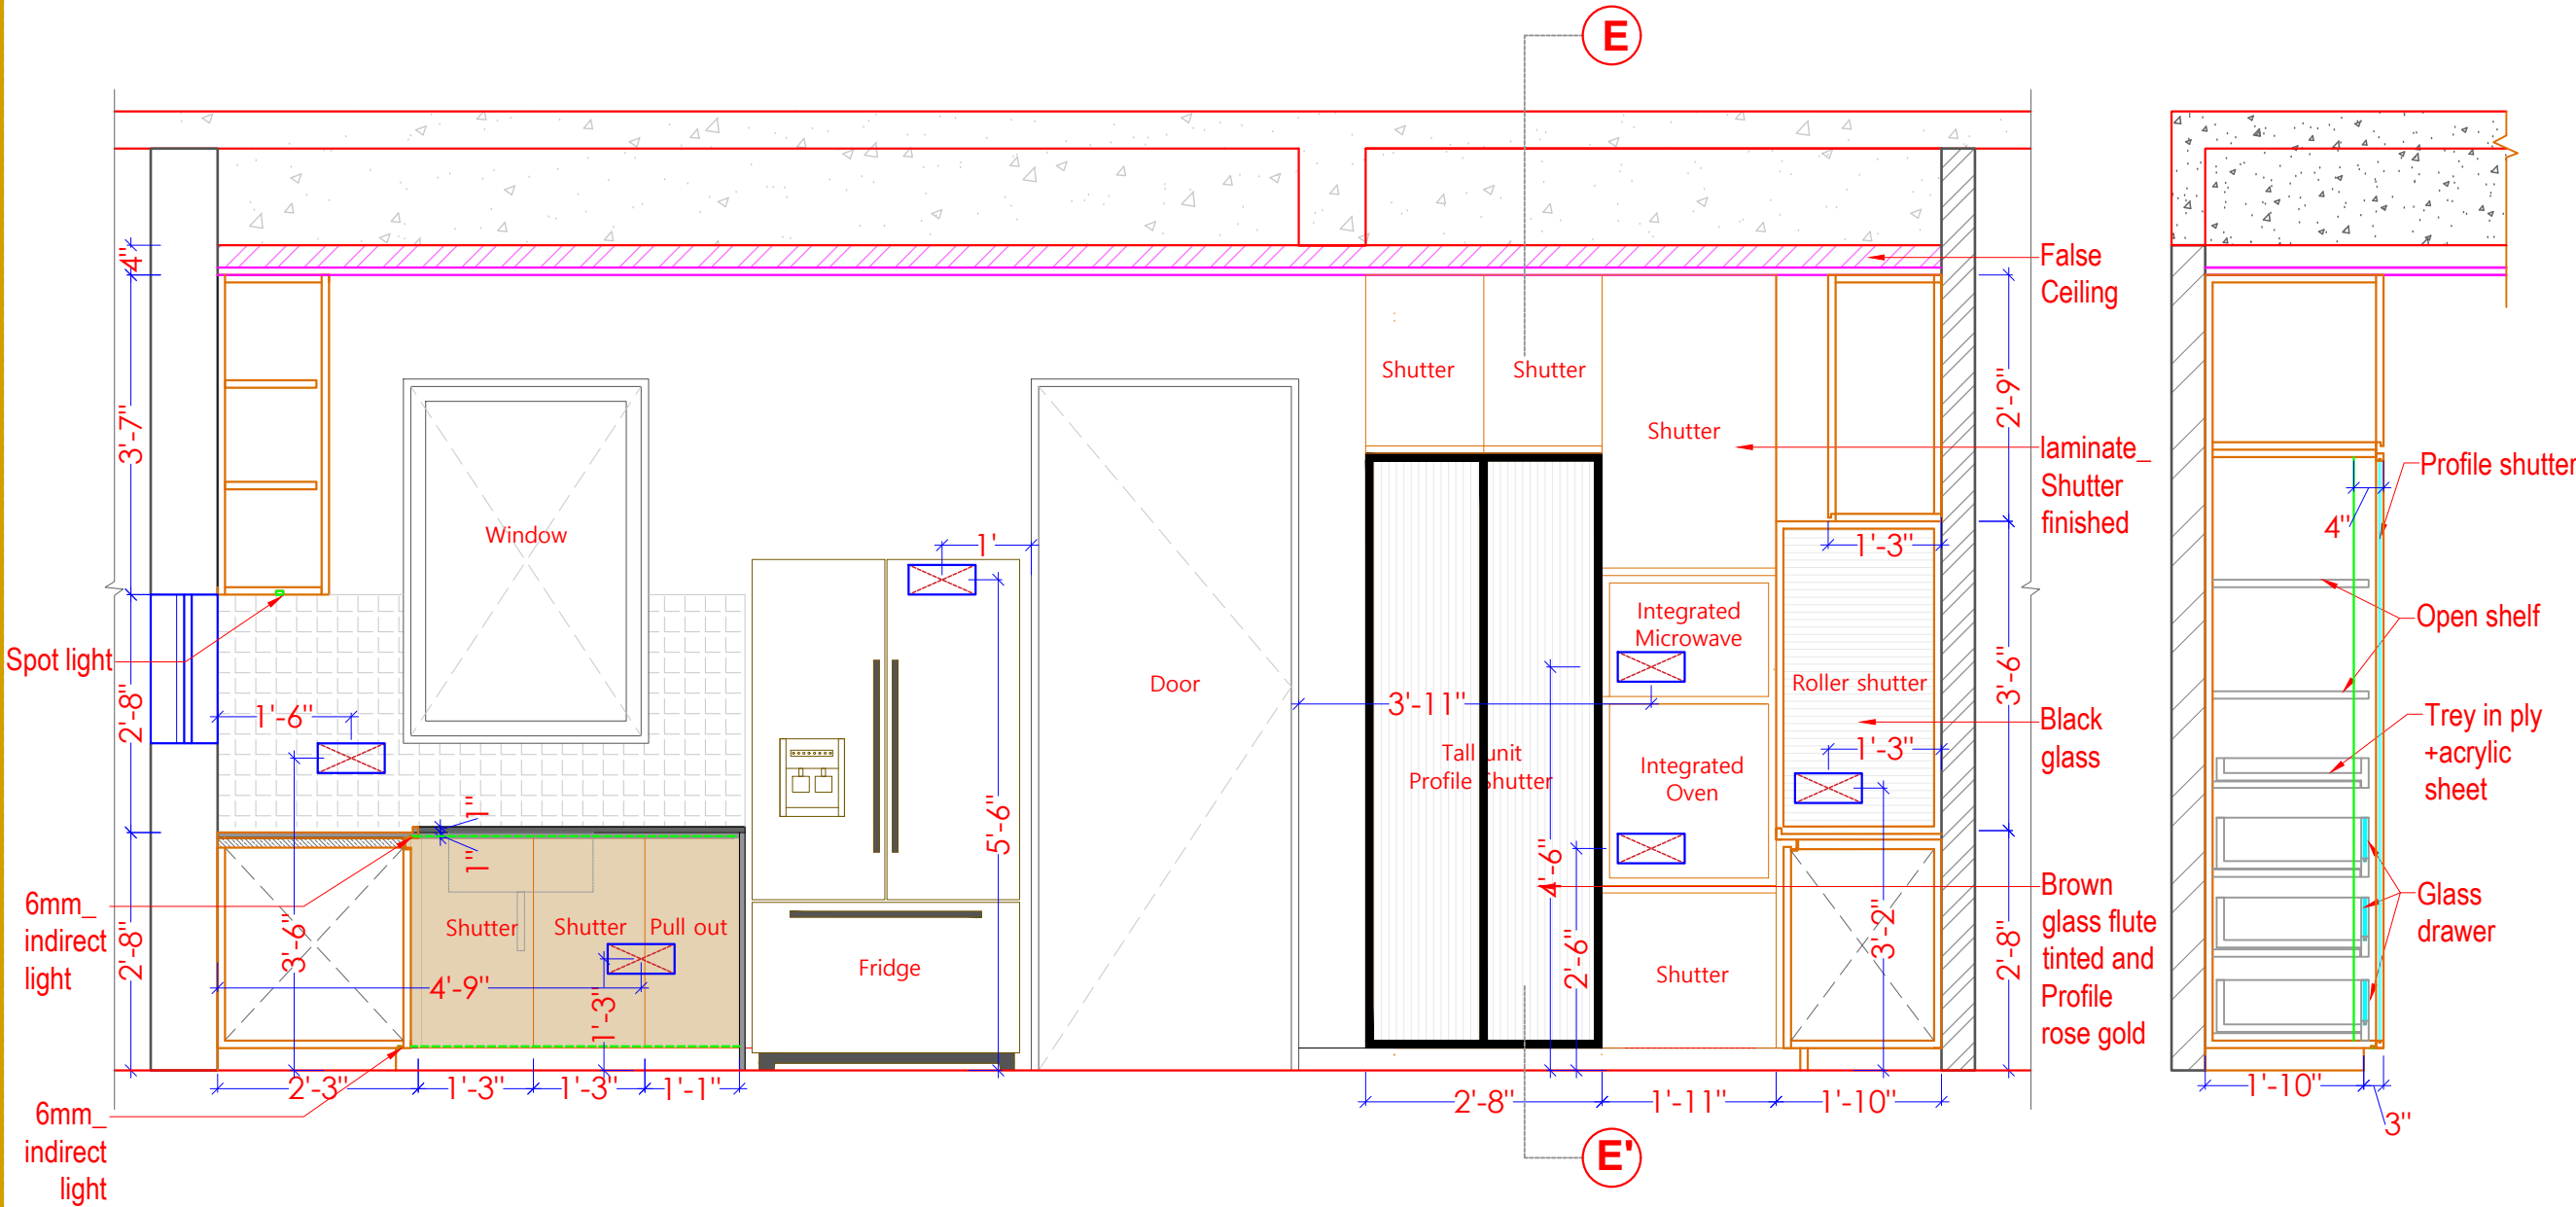

ELEVATION - B

SECTION EE'

DRAWING TITLE :

KITCHEN
ELEVATION- C

NOTES:

* DO NOT SCALE THE DRAWING.

* ALL DIMENSIONS ARE IN FEET \ INCHES.

* ANY DISCREPENCY IN THE DRAWING
TO BE BROUGHT IN THE DESIGNER'S
NOTICE BEFORE IMPLEMENTATION
ON SITE.

SITE ADDRESS:

SAVAD
VADODARA

CLIENT NAME:

RONAK PANCHOLI

DATE:

02-06-2025

NORTH:

DRAWING DETAIL

REVISION NO.

R1 R2 R3

REVISED DATE:

07/02/26

SCALE:

N.T.S

DRAWN BY:

ARCHANA

CHECKED BY:


MITTAL

www.mayaspace.studio

mayaspace.studio@gmail.com

+918980144077

@mayaspace.studio

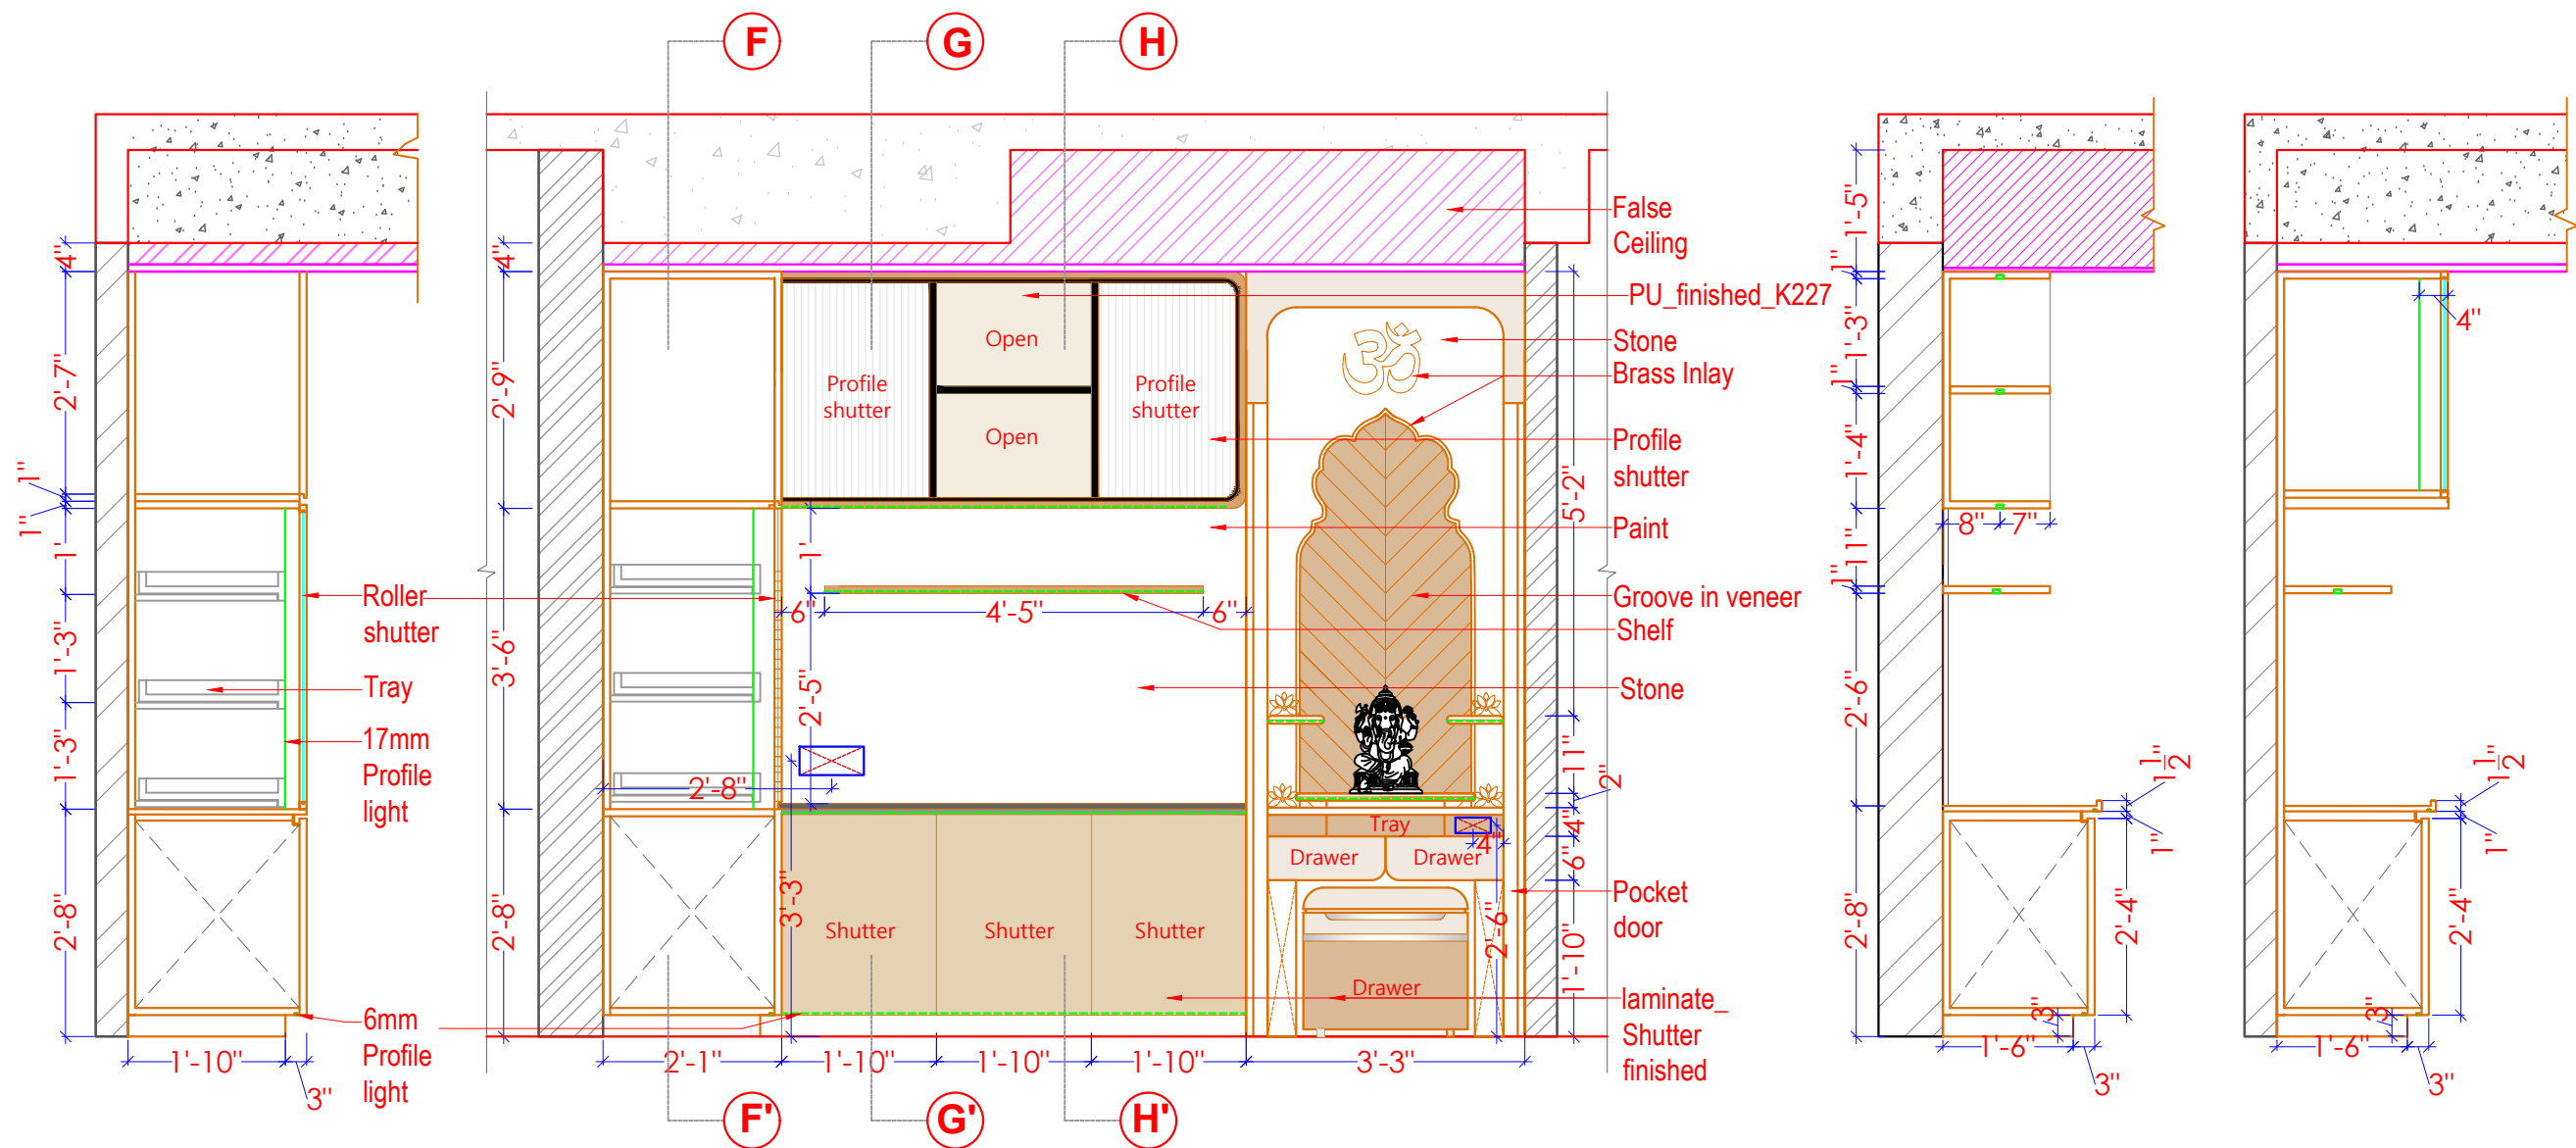

SECTION FF'

SECTION HH'

SECTION GG'

ELEVATION - C

KITCHEN
ELEVATION- D

- * DO NOT SCALE THE DRAWING.
- * ALL DIMENSIONS ARE IN FEET \ INCHES.
- * ANY DISCREPANCY IN THE DRAWING TO BE BROUGHT IN THE DESIGNER'S NOTICE BEFORE IMPLEMENTATION ON SITE.


SAVAD
VADODARA

RONAK PANCHOLI


NORTH:

REVISION NO.	R1	R2	R3
REVISED DATE:	07/02/26		
SCALE:	N.T.S		
DRAWN BY:	ARCHANA		
CHECKED BY:	MITTAL		

	www.mayaspace.studio
	mayaspace.studio@gmail.com
	+918980144077
	@mayaspace.studio

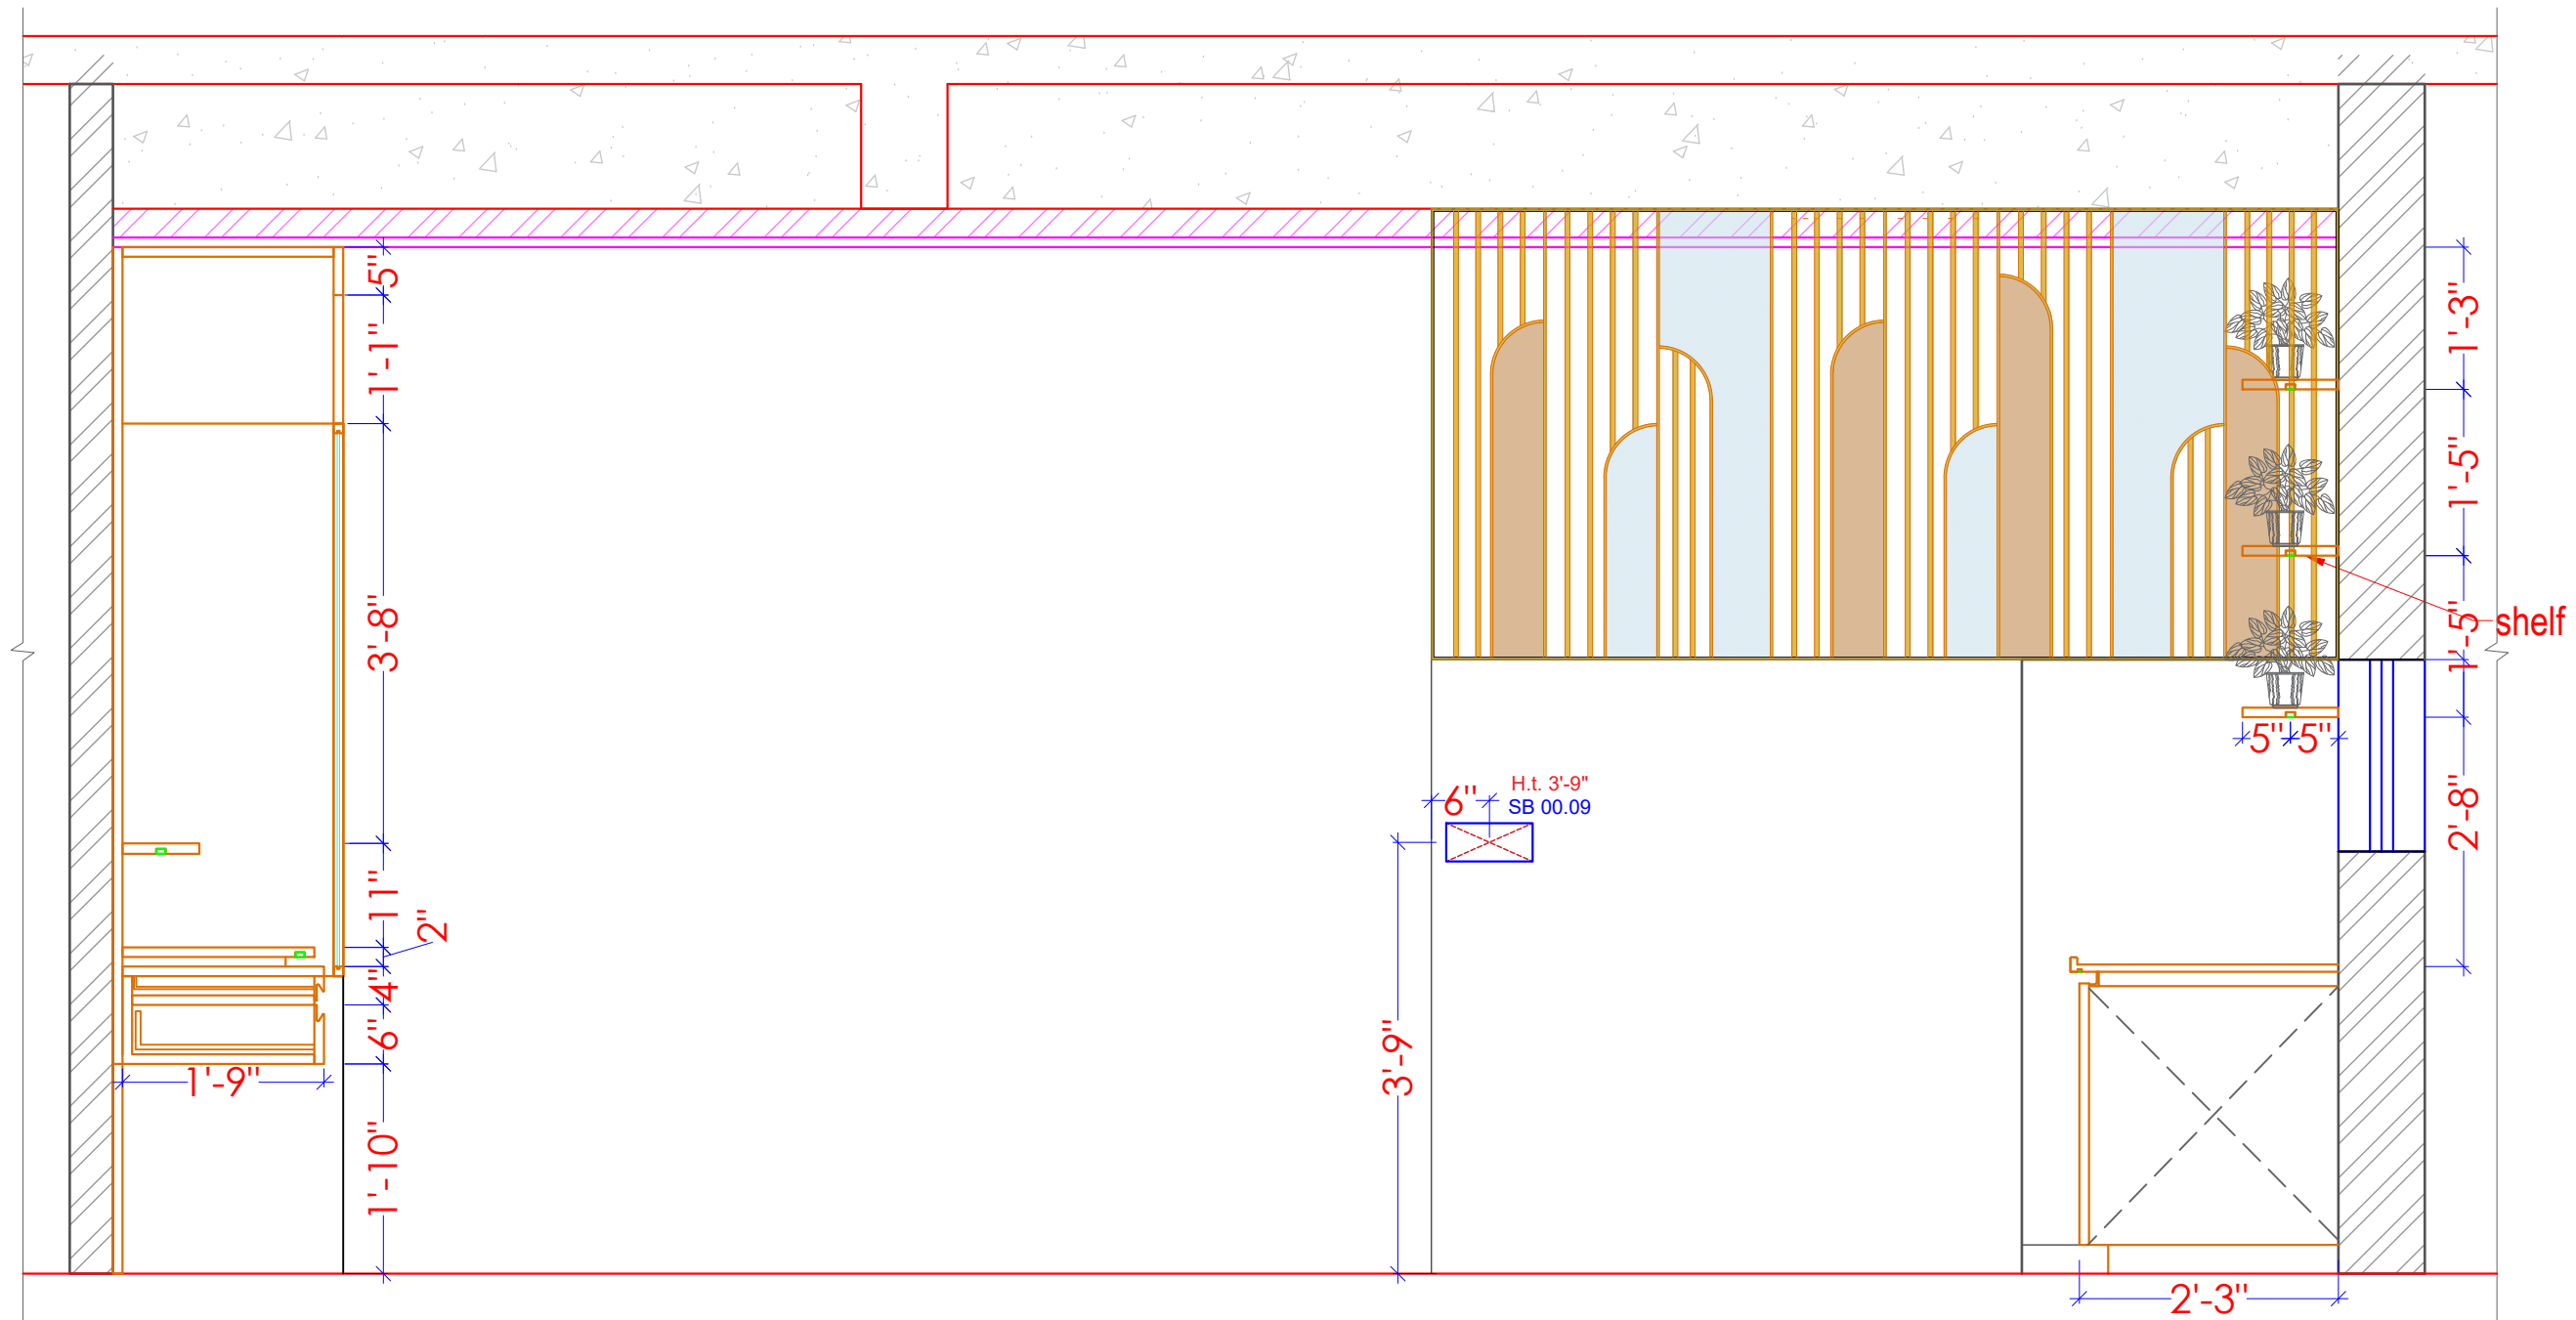

ELEVATION - D

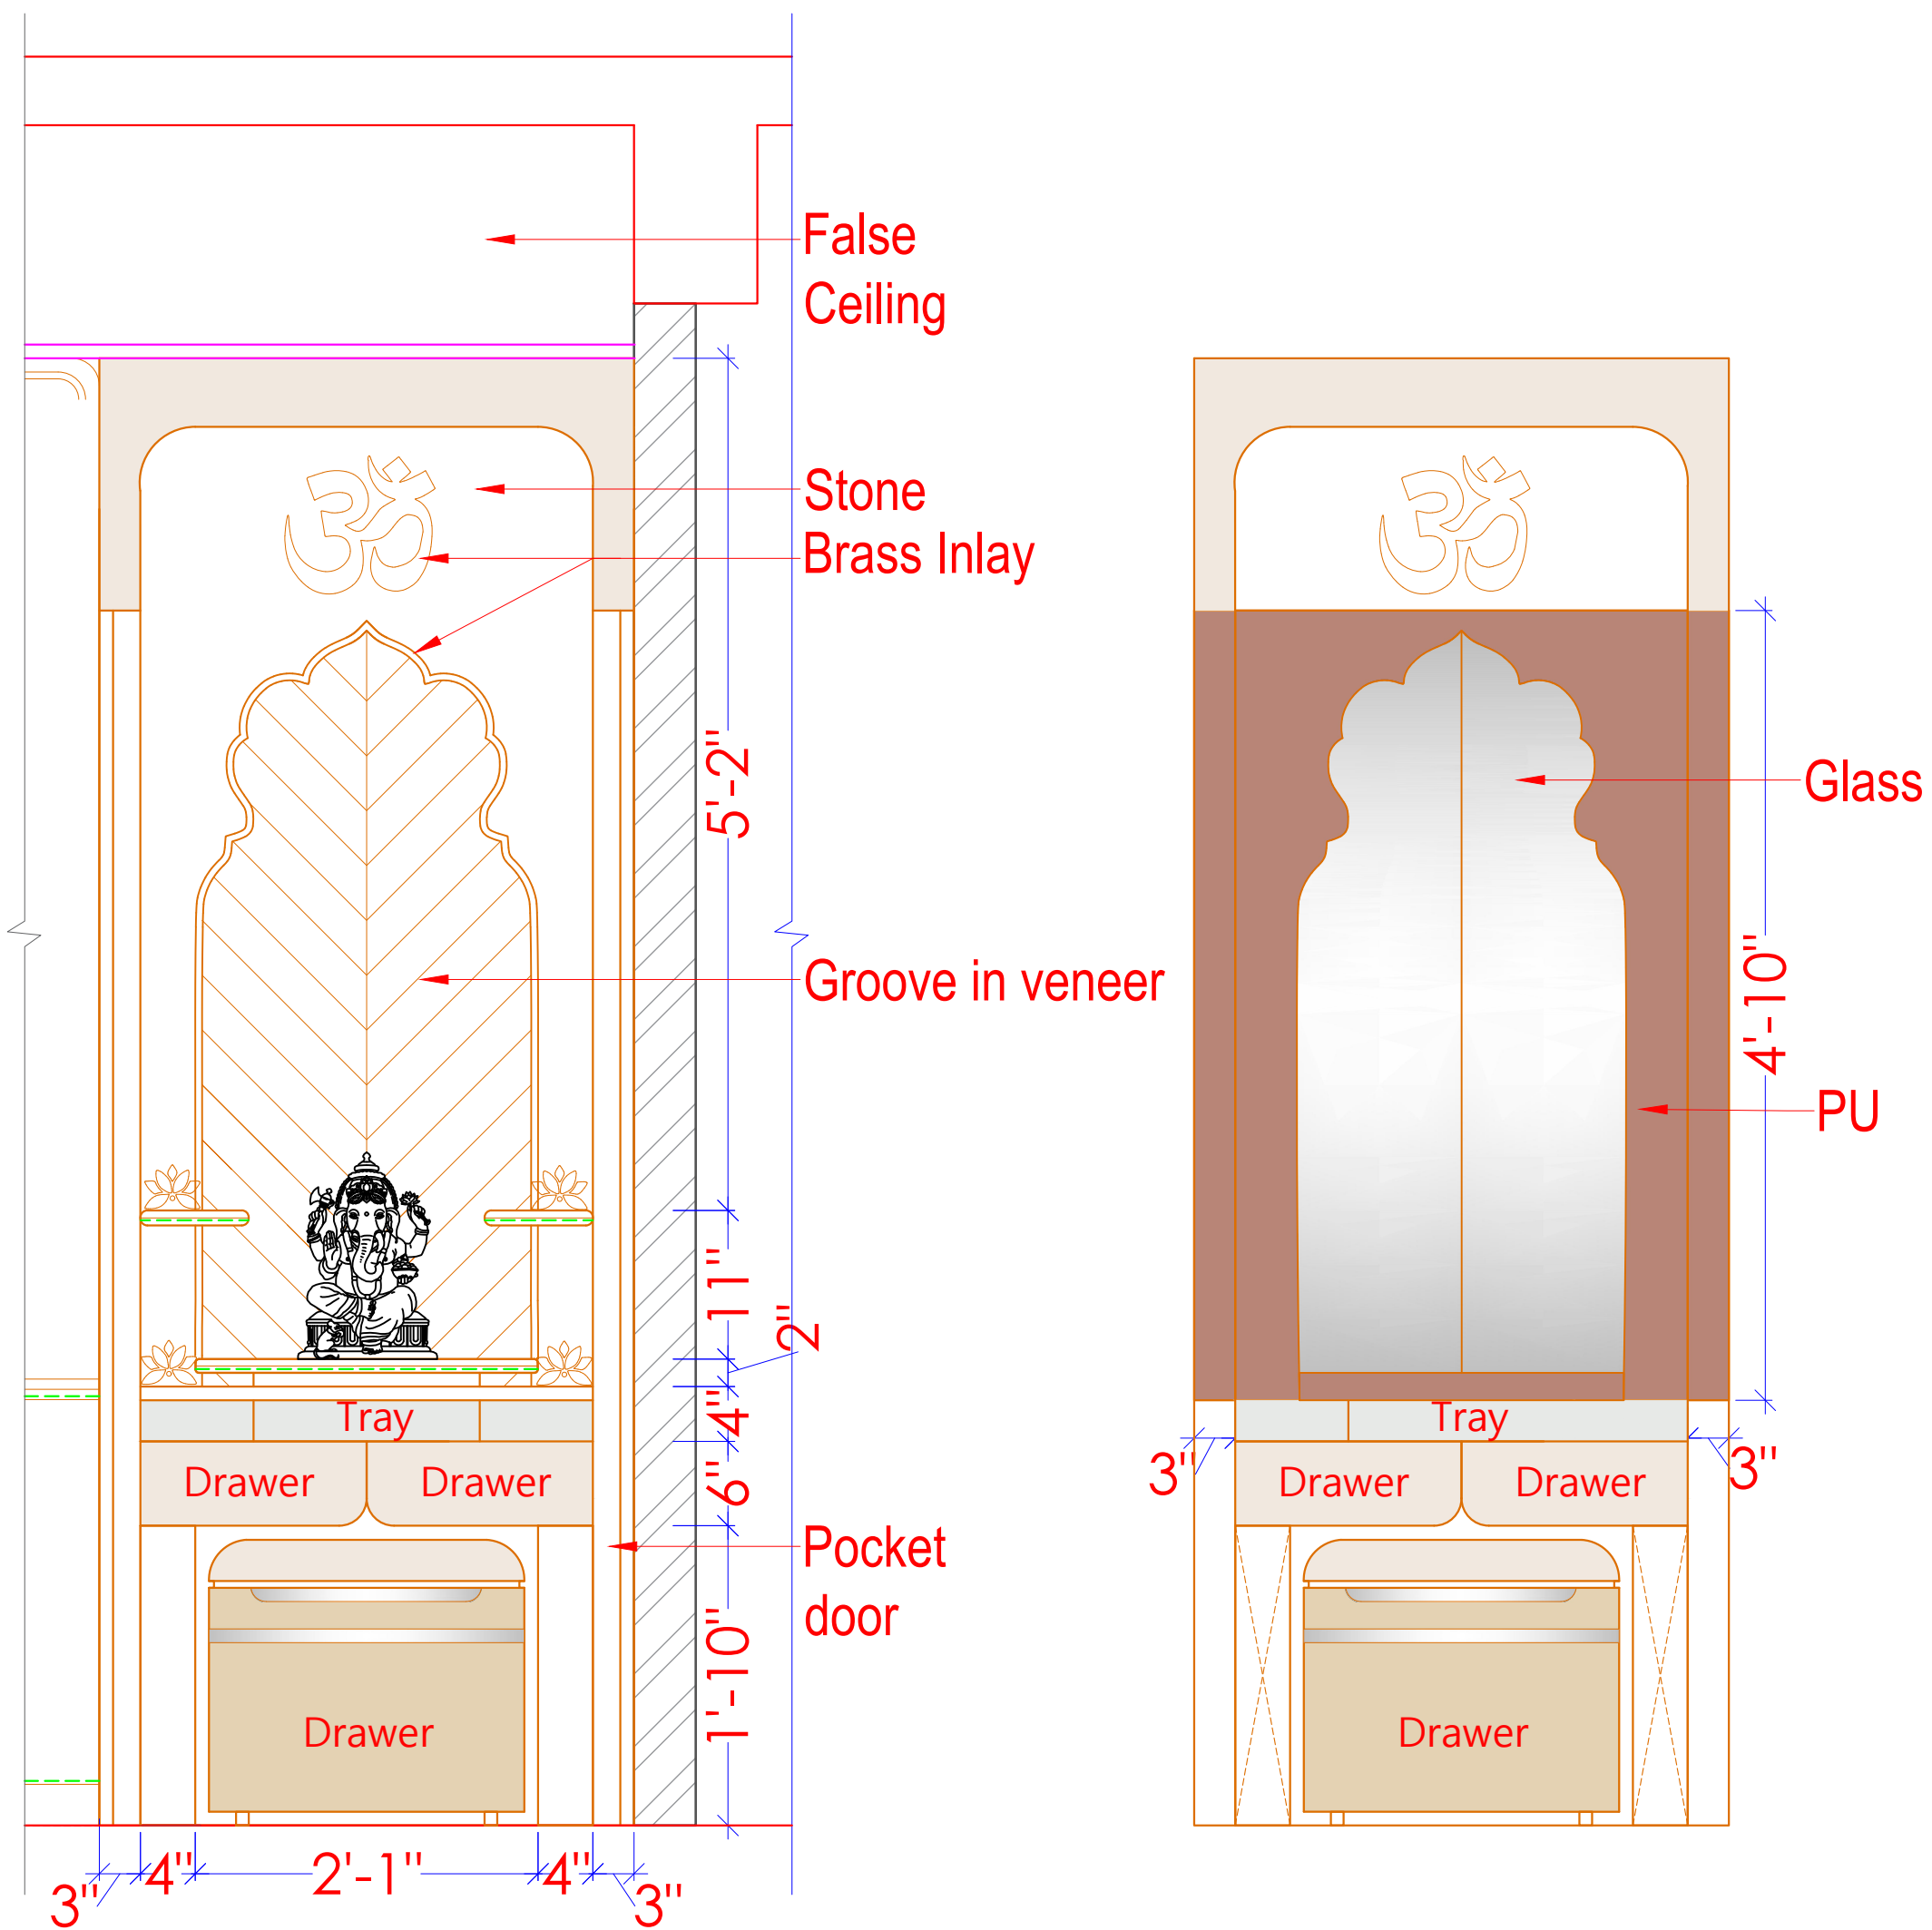

DRAWING TITLE :

KITCHEN
MANDIR DETAIL

NOTES:

- * DO NOT SCALE THE DRAWING.
- * ALL DIMENSIONS ARE IN FEET \ INCHES.
- * ANY DISCREPENCY IN THE DRAWING TO BE BROUGHT IN THE DESIGNER'S NOTICE BEFORE IMPLEMENTATION ON SITE.

SITE ADDRESS:

SAVAD
VADODARA

CLIENT NAME:

RONAK PANCHOLI

DATE:

02-06-2025


NORTH:

DRAWING DETAIL

REVISION NO.	R1	R2	R3
REVISED DATE:	07/02/26		
SCALE:	N.T.S		
DRAWN BY:	ARCHANA		
CHECKED BY:	MITTAL		

	www.mayaspace.studio
	mayaspace.studio@gmail.com
	+918980144077
	@mayaspace.studio



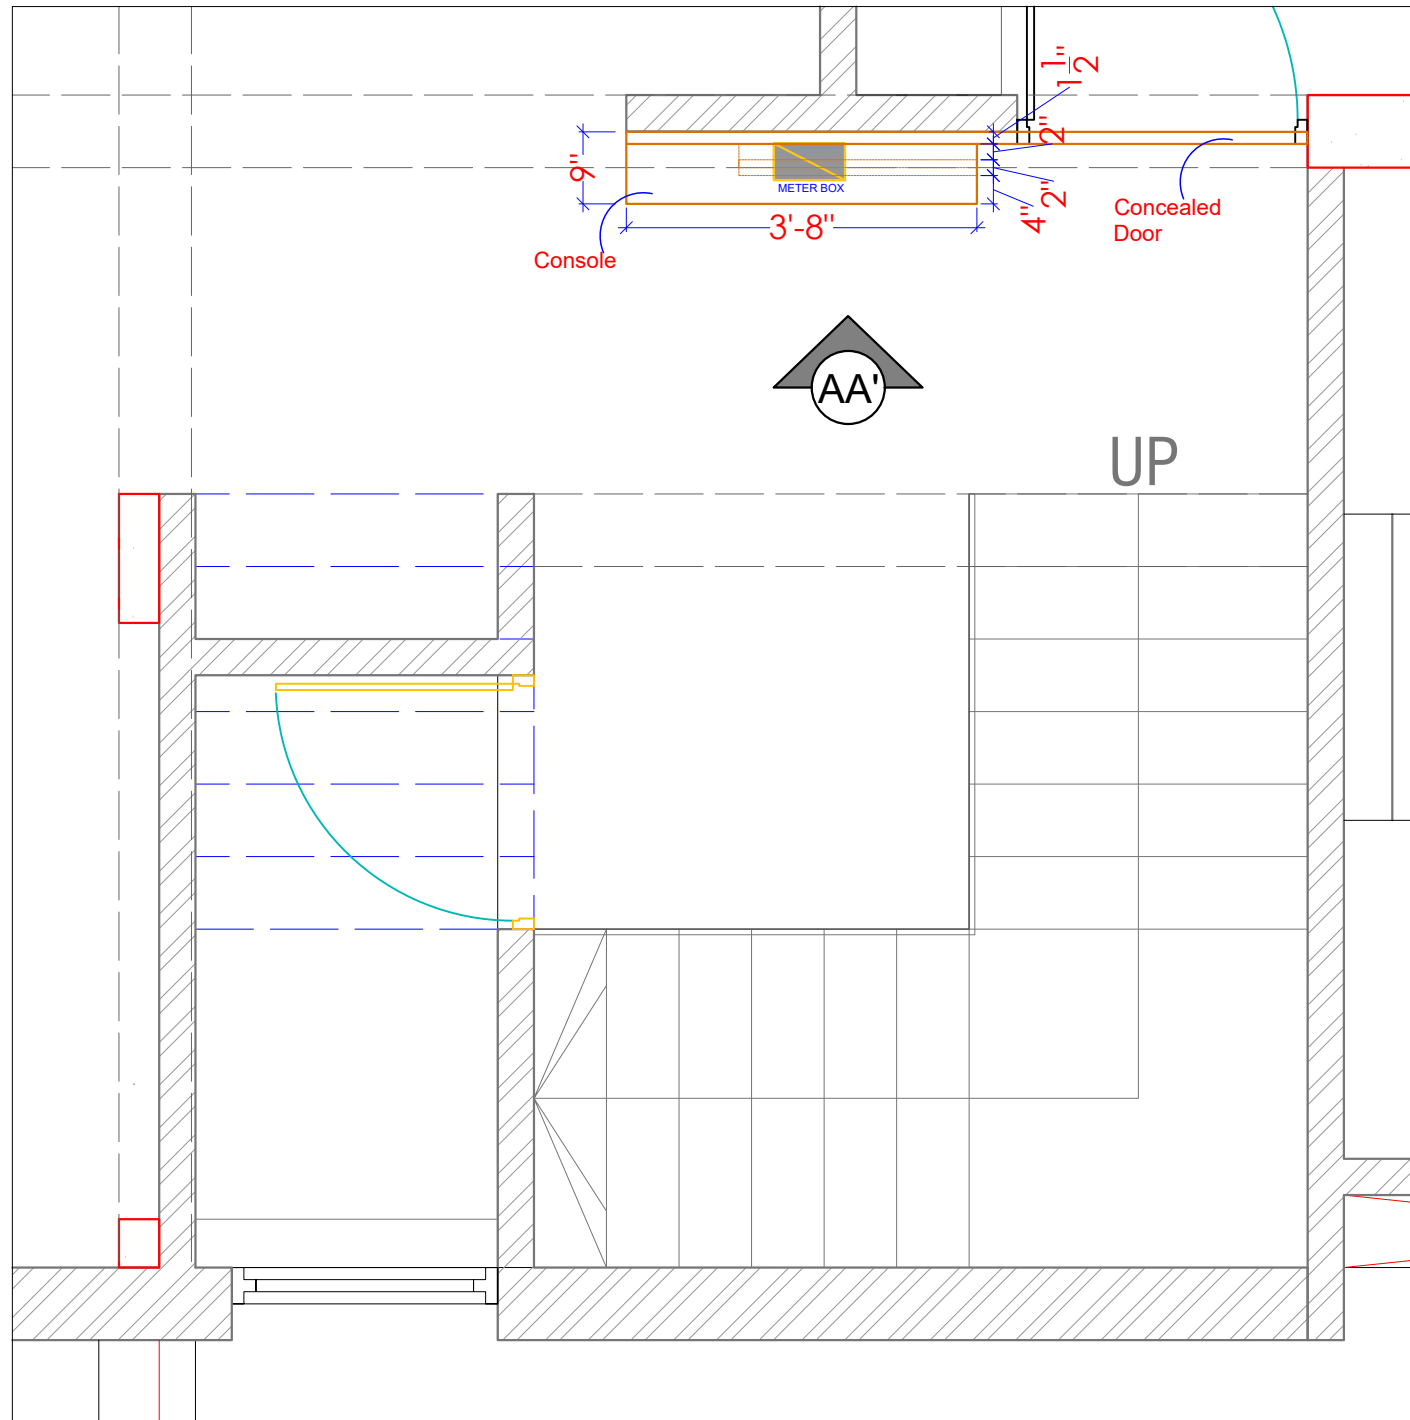

DRAWING TITLE :

LIVING ROOM PASSAGE DESIGN

NOTES:

- * DO NOT SCALE THE DRAWING.
- * ALL DIMENSIONS ARE IN FEET \ INCHES.
- * ANY DISCREPANCY IN THE DRAWING TO BE BROUGHT IN THE DESIGNER'S NOTICE BEFORE IMPLEMENTATION ON SITE.

SITE ADDRESS:

SAVAD
VADODARA

CLIENT NAME:

RONAK PANCHOLI

DATE:

02-06-2025

NORTH:

DRAWING DETAIL

REVISION NO.

R1 R2 R3

REVISED DATE:

07/02/2026

SCALE:

N.T.S

DRAWN BY:

ARCHANA

CHECKED BY:

MITTAL

 www.mayaspace.studio

 mayaspace.studio@gmail.com

 +918980144077

 @mayaspace.studio



DRAWING TITLE :

LIVING ROOM
PASSAGE DESIGN

NOTES:

- * DO NOT SCALE THE DRAWING.
- * ALL DIMENSIONS ARE IN FEET \ INCHES.
- * ANY DISCREPANCY IN THE DRAWING TO BE BROUGHT IN THE DESIGNER'S NOTICE BEFORE IMPLEMENTATION ON SITE.

SITE ADDRESS:

SAVAD
VADODARA

CLIENT NAME:

RONAK PANCHOLI

DATE:

02-06-2025

NORTH:

DRAWING DETAIL

REVISION NO.

R1 R2 R3

REVISED DATE:

07/02/2026

SCALE:

N.T.S


DRAWN BY:

ARCHANA

CHECKED BY:

MITTAL

www.mayaspace.studio
mayaspace.studio@gmail.com
+918980144077
@mayaspace.studio

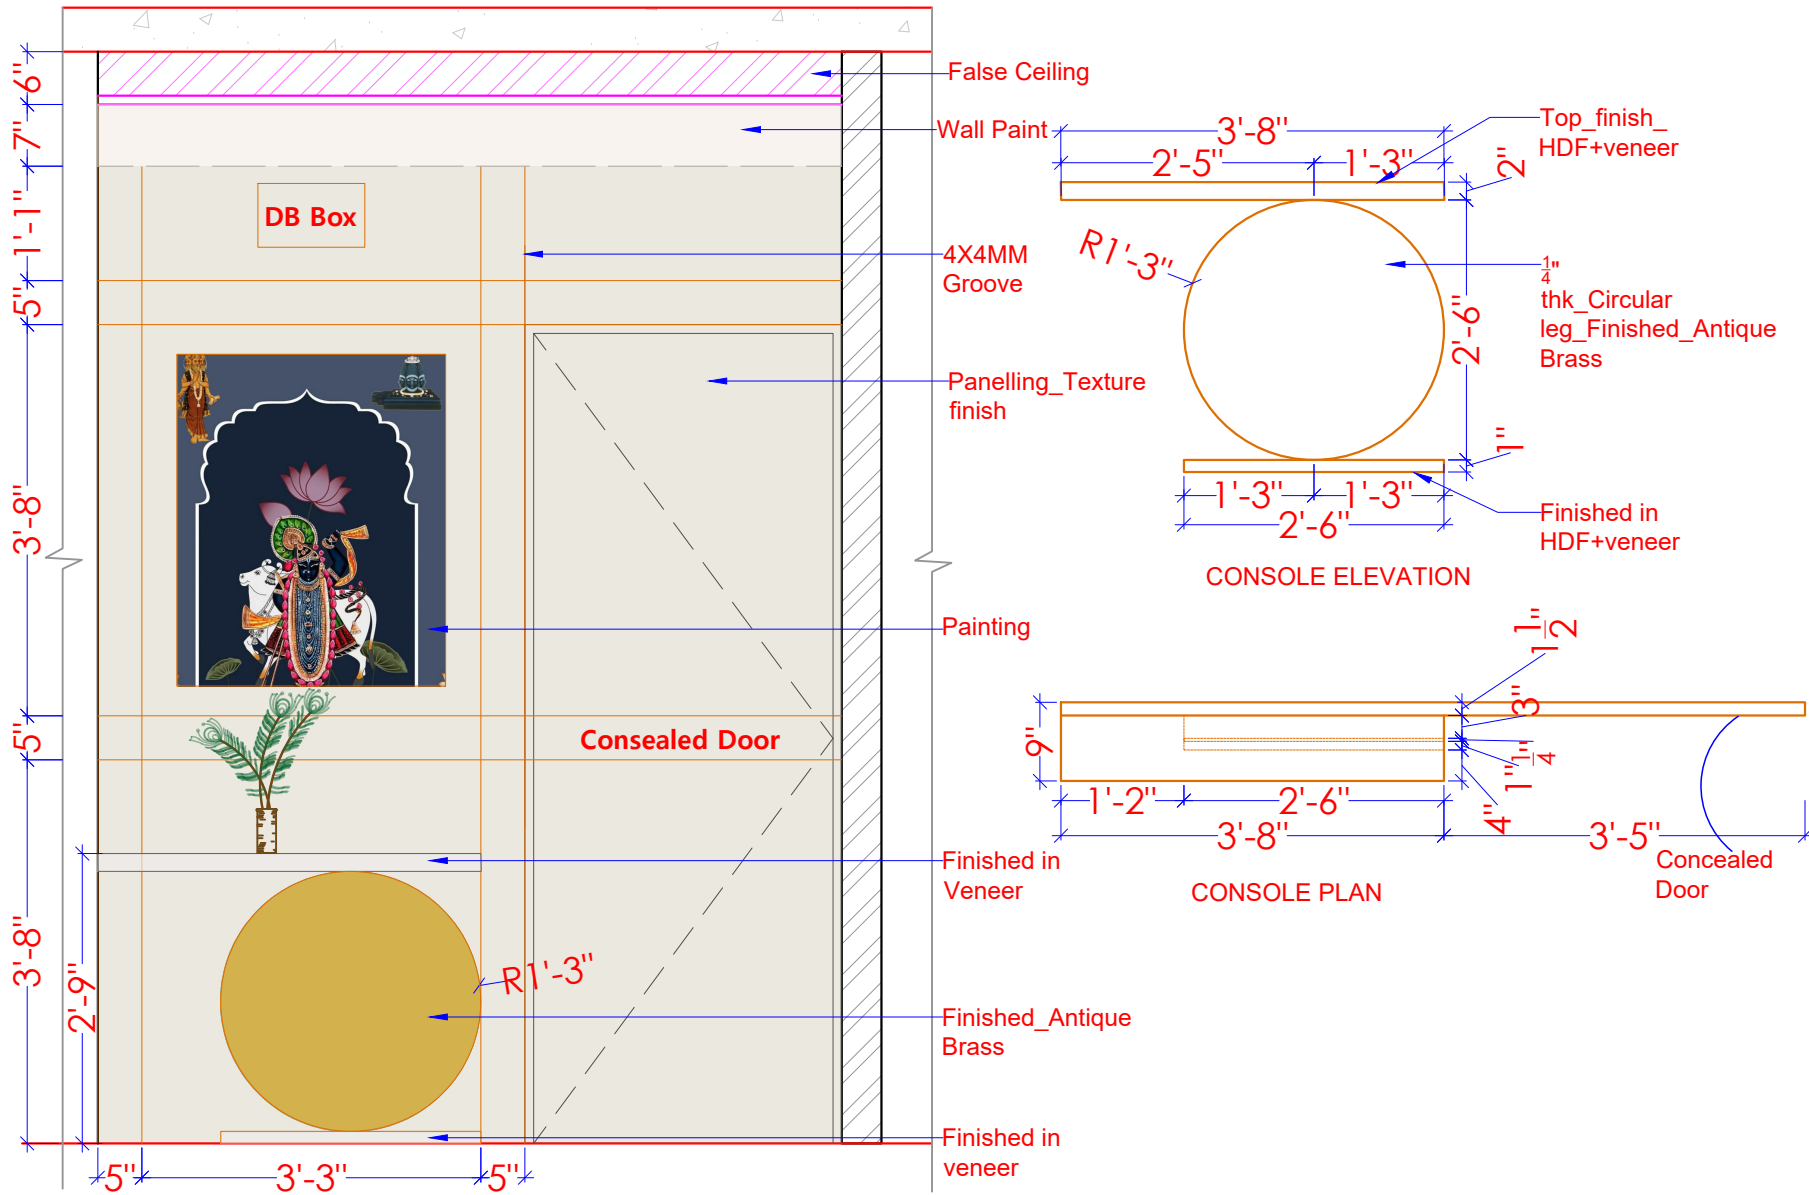

ELEVATION - AA'

DRAWING TITLE :

LIVING ROOM
BASIN AREA

NOTES:

- * DO NOT SCALE THE DRAWING.
- * ALL DIMENSIONS ARE IN FEET \ INCHES.
- * ANY DISCREPENCY IN THE DRAWING TO BE BROUGHT IN THE DESIGNER'S NOTICE BEFORE IMPLEMENTATION ON SITE.

SITE ADDRESS:

SAVAD
VADODARA

CLIENT NAME:

RONAK PANCHOLI

DATE:

02-06-2025

NORTH:

DRAWING DETAIL

REVISION NO.

R1 R2 R3

REVISED DATE:

07/02/2026

SCALE:

N.T.S

DRAWN BY:

ARCHANA

CHECKED BY:


MITTAL

 www.mayaspace.studio


 mayaspace.studio@gmail.com

 +918980144077


 @mayaspace.studio

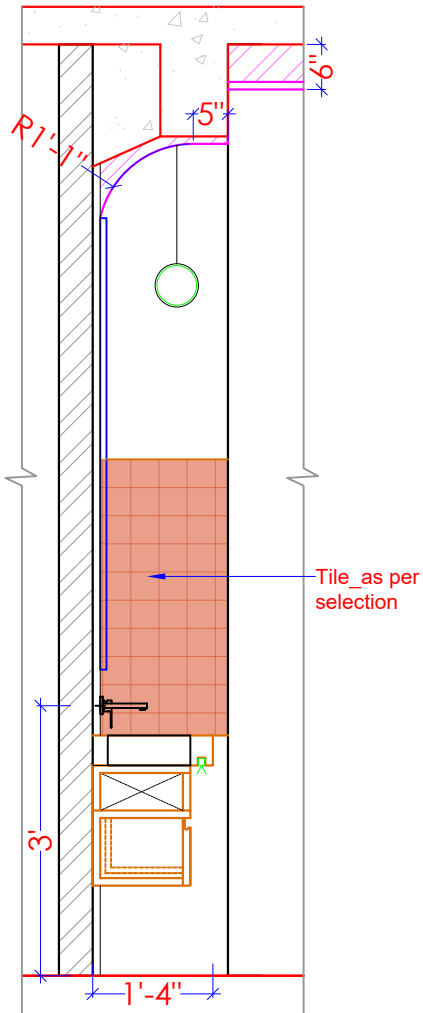



ELEVATION - c

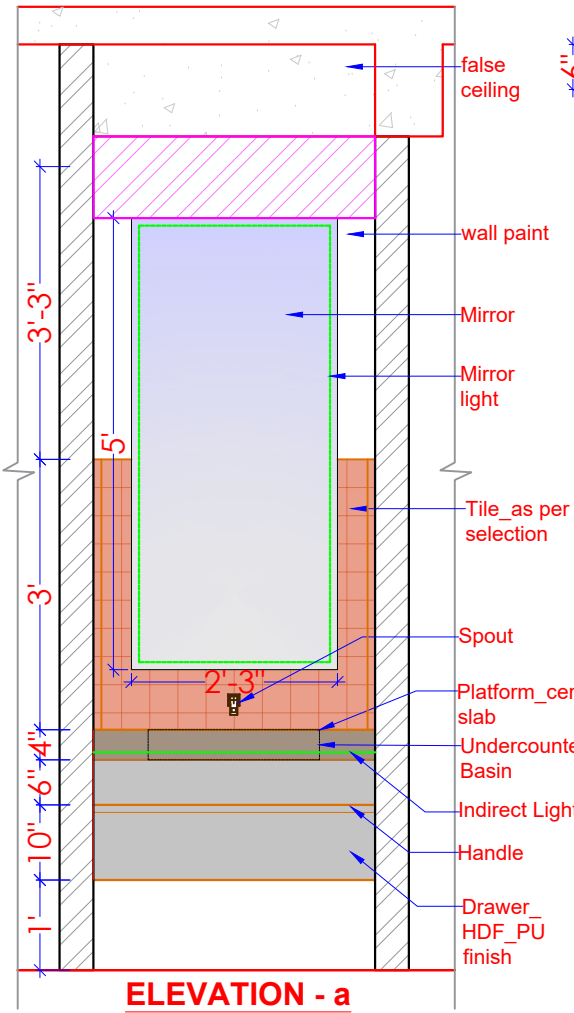


ELEVATION - a

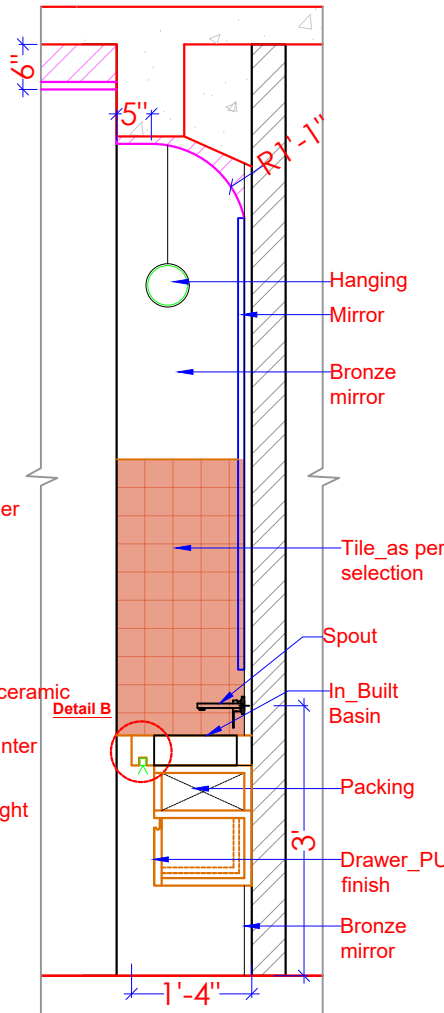

ELEVATION - b

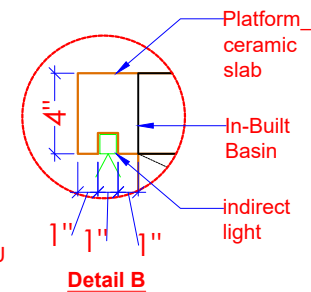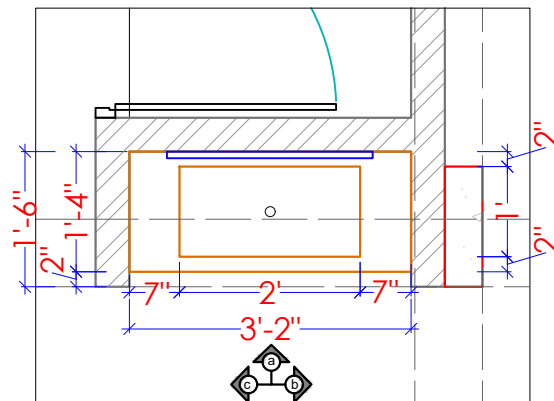

Detail B

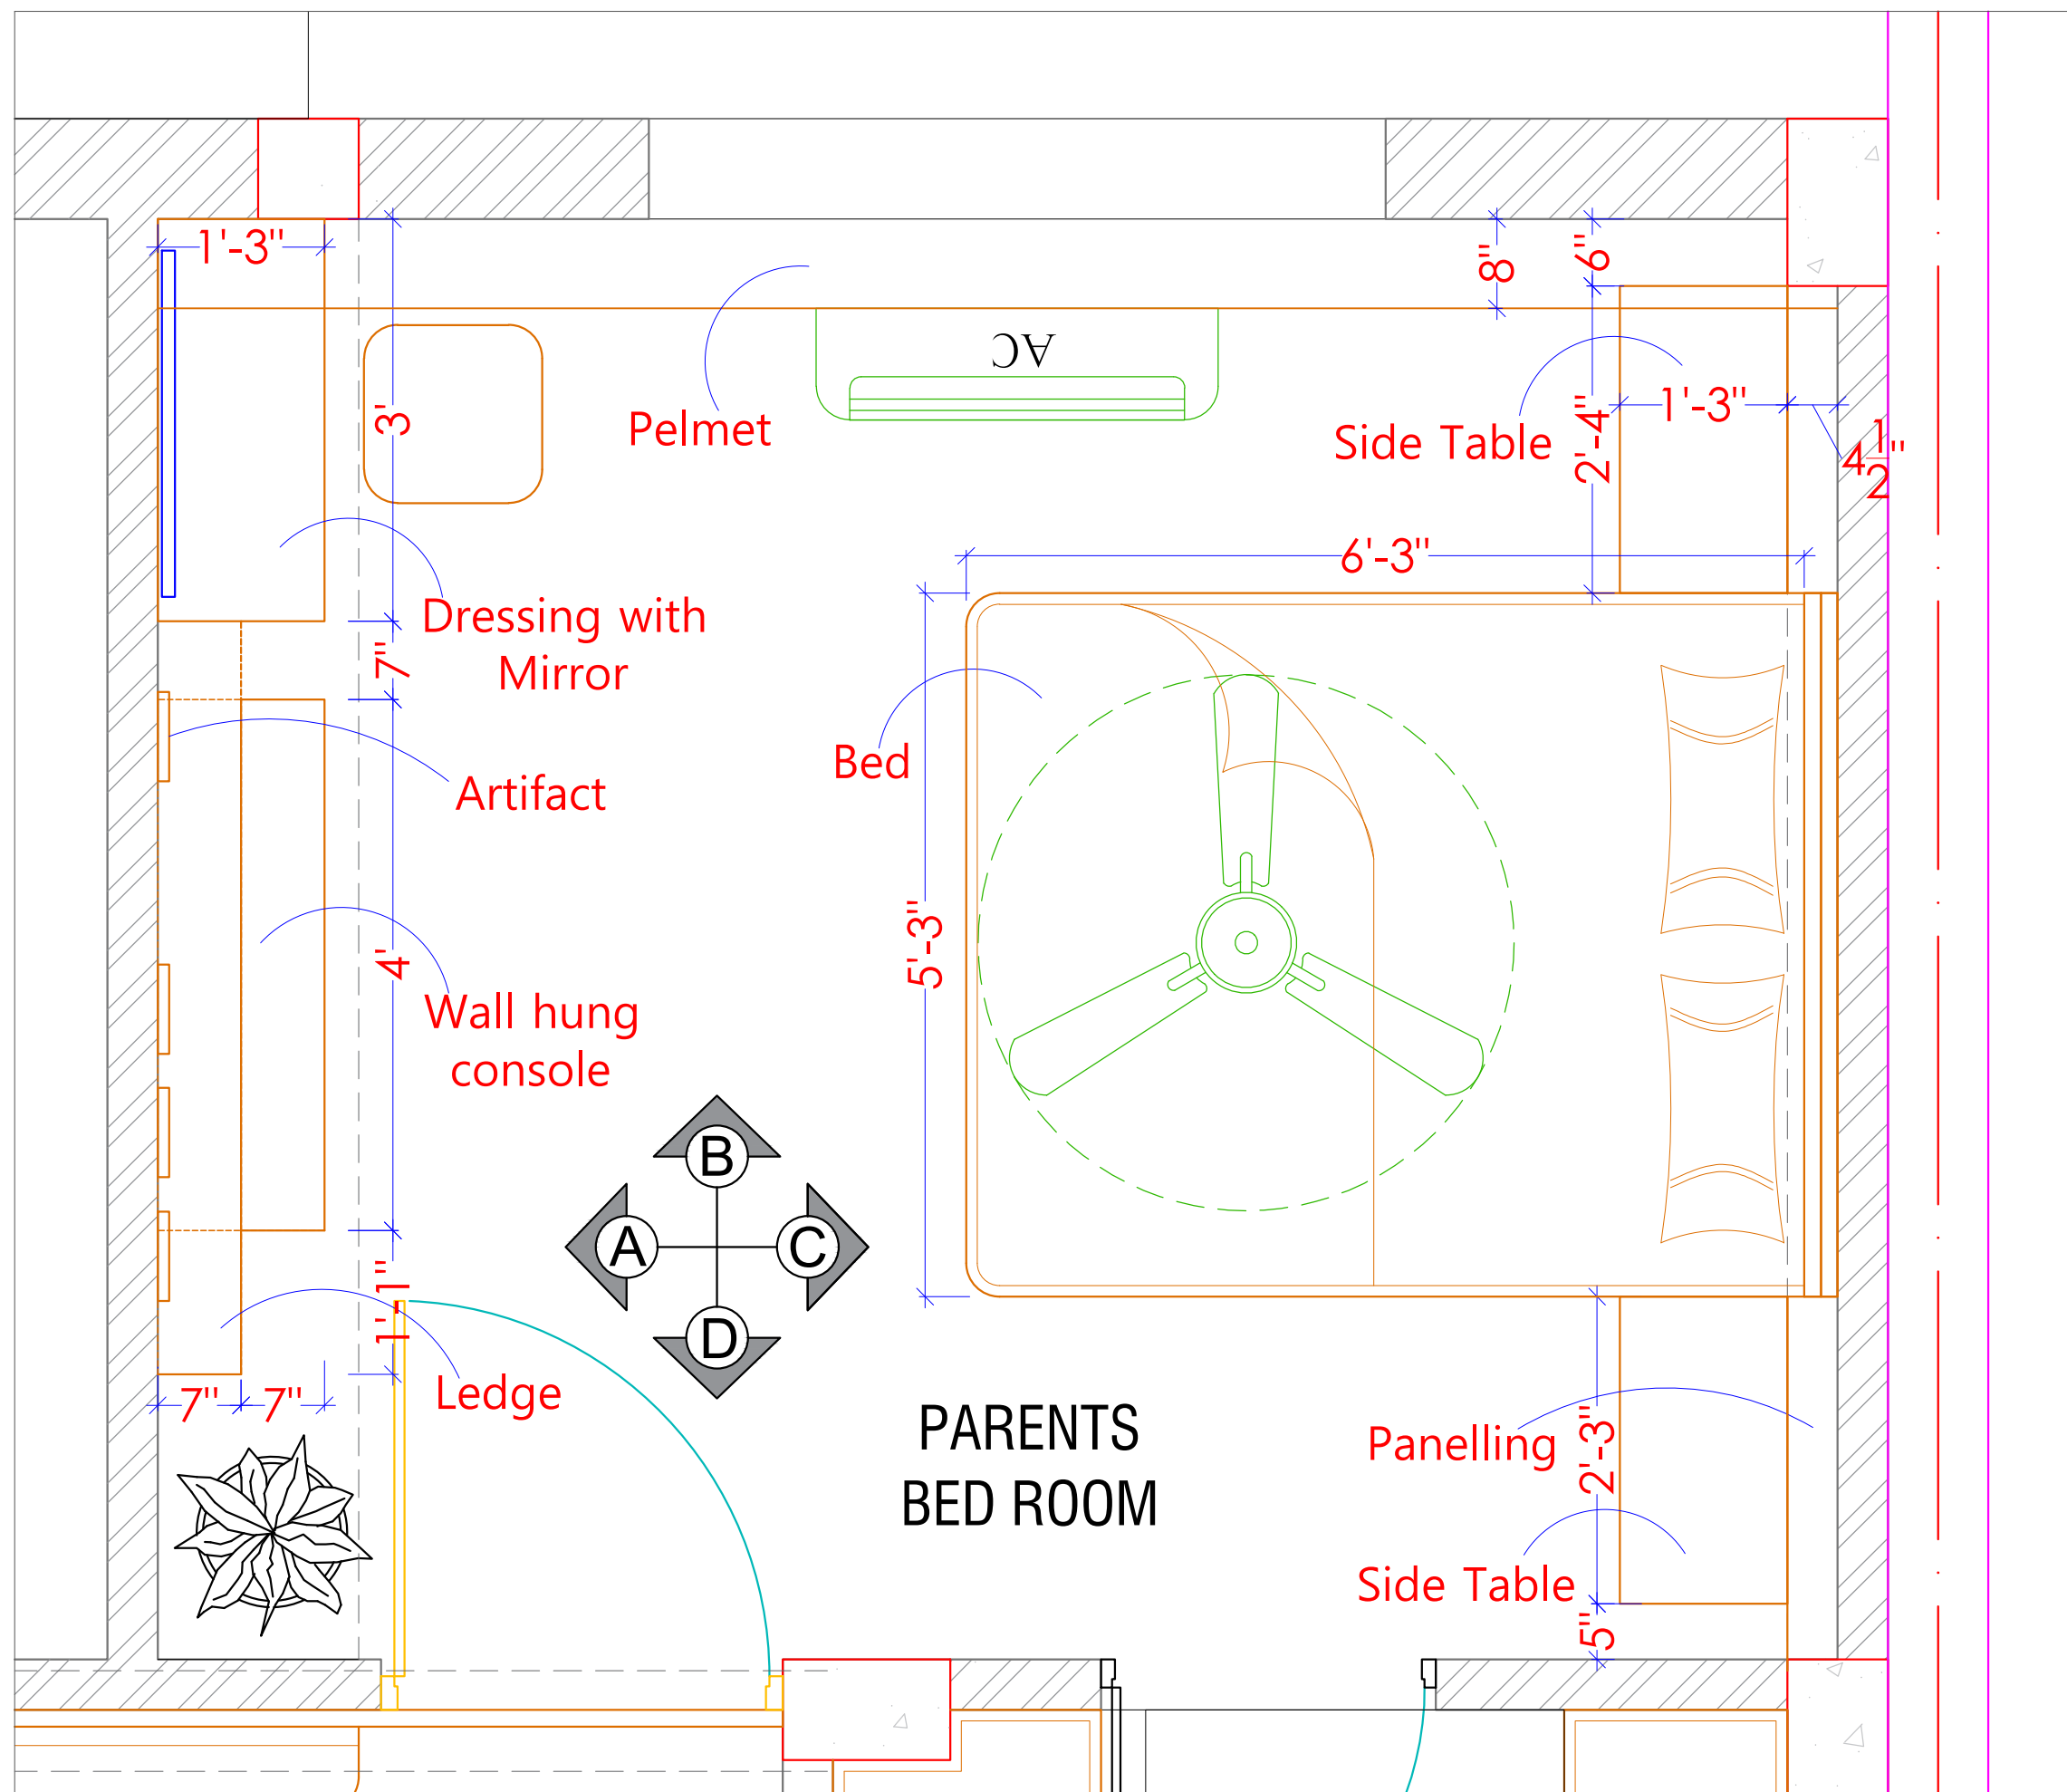

PLAN

DRAWING TITLE :

PARENTS BEDROOM
FURNITURE LAYOUT

NOTES:

- * DO NOT SCALE THE DRAWING.
- * ALL DIMENSIONS ARE IN FEET \ INCHES.
- * ANY DISCREPANCY IN THE DRAWING TO BE BROUGHT IN THE DESIGNER'S NOTICE BEFORE IMPLEMENTATION ON SITE.

SITE ADDRESS:

SAVAD
VADODARA

CLIENT NAME:

RONAK PANCHOLI

DATE:

02-06-2025

NORTH:




DRAWING DETAIL

REVISION NO.	R1	R2	R3
REVISED DATE:	07/02/26		
SCALE:	N.T.S		
DRAWN BY:	ARCHANA		
CHECKED BY:	MITTAL		

	www.mayaspace.studio
	mayaspace.studio@gmail.com
	+918980144077
	@mayaspace.studio



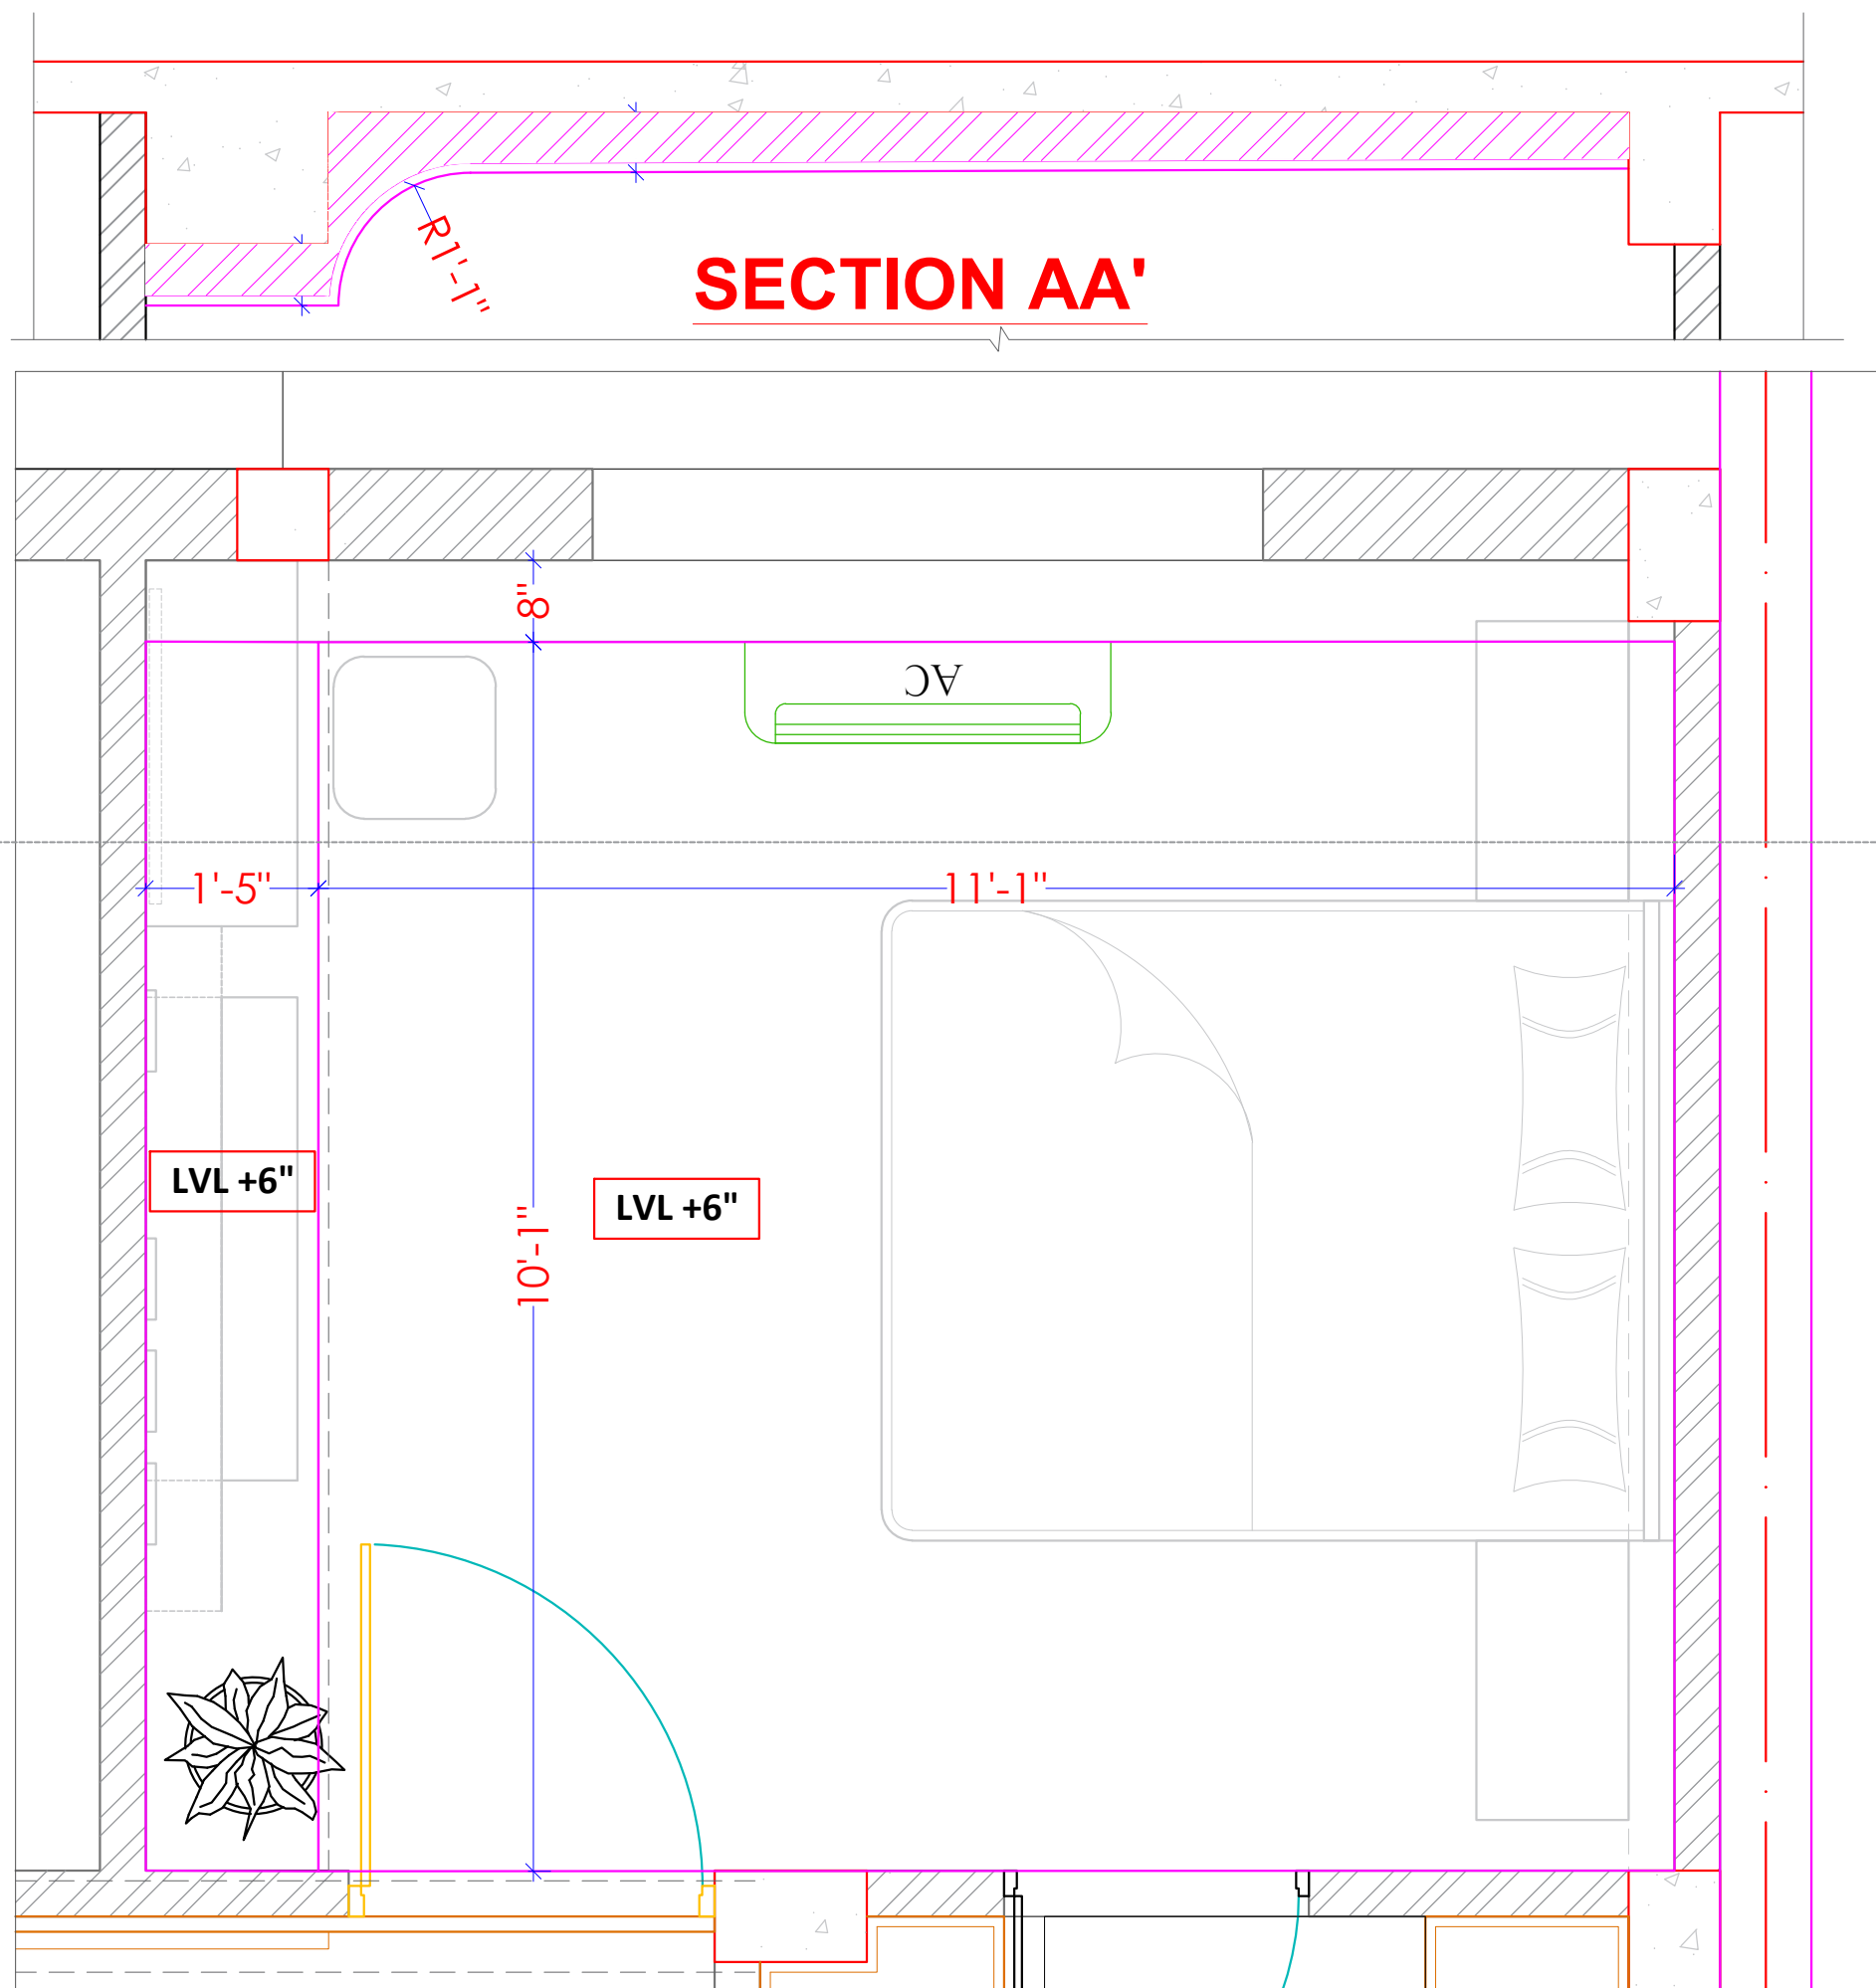

FALSE CEILING LAYOUT

**PARENTS BEDROOM
FALSE CEILING LAYOUT**

NOTES:

- * DO NOT SCALE THE DRAWING.
- * ALL DIMENSIONS ARE IN FEET \ INCHES.
- * ANY DISCREPANCY IN THE DRAWING TO BE BROUGHT IN THE DESIGNER'S NOTICE BEFORE IMPLEMENTATION ON SITE.

SITE ADDRESS:

**SAVAD
VADODARA**

CLIENT NAME:

RONAK PANCHOLI

DATE:

02-06-2025

NORTH:




DRAWING DETAIL

REVISION NO.	R1	R2	R3
REVISED DATE:	07/02/26		
SCALE:	N.T.S		
DRAWN BY:	ARCHANA		
CHECKED BY:	MITTAL		

	www.mayaspace.studio
	mayaspace.studio@gmail.com
	+918980144077
	@mayaspace.studio



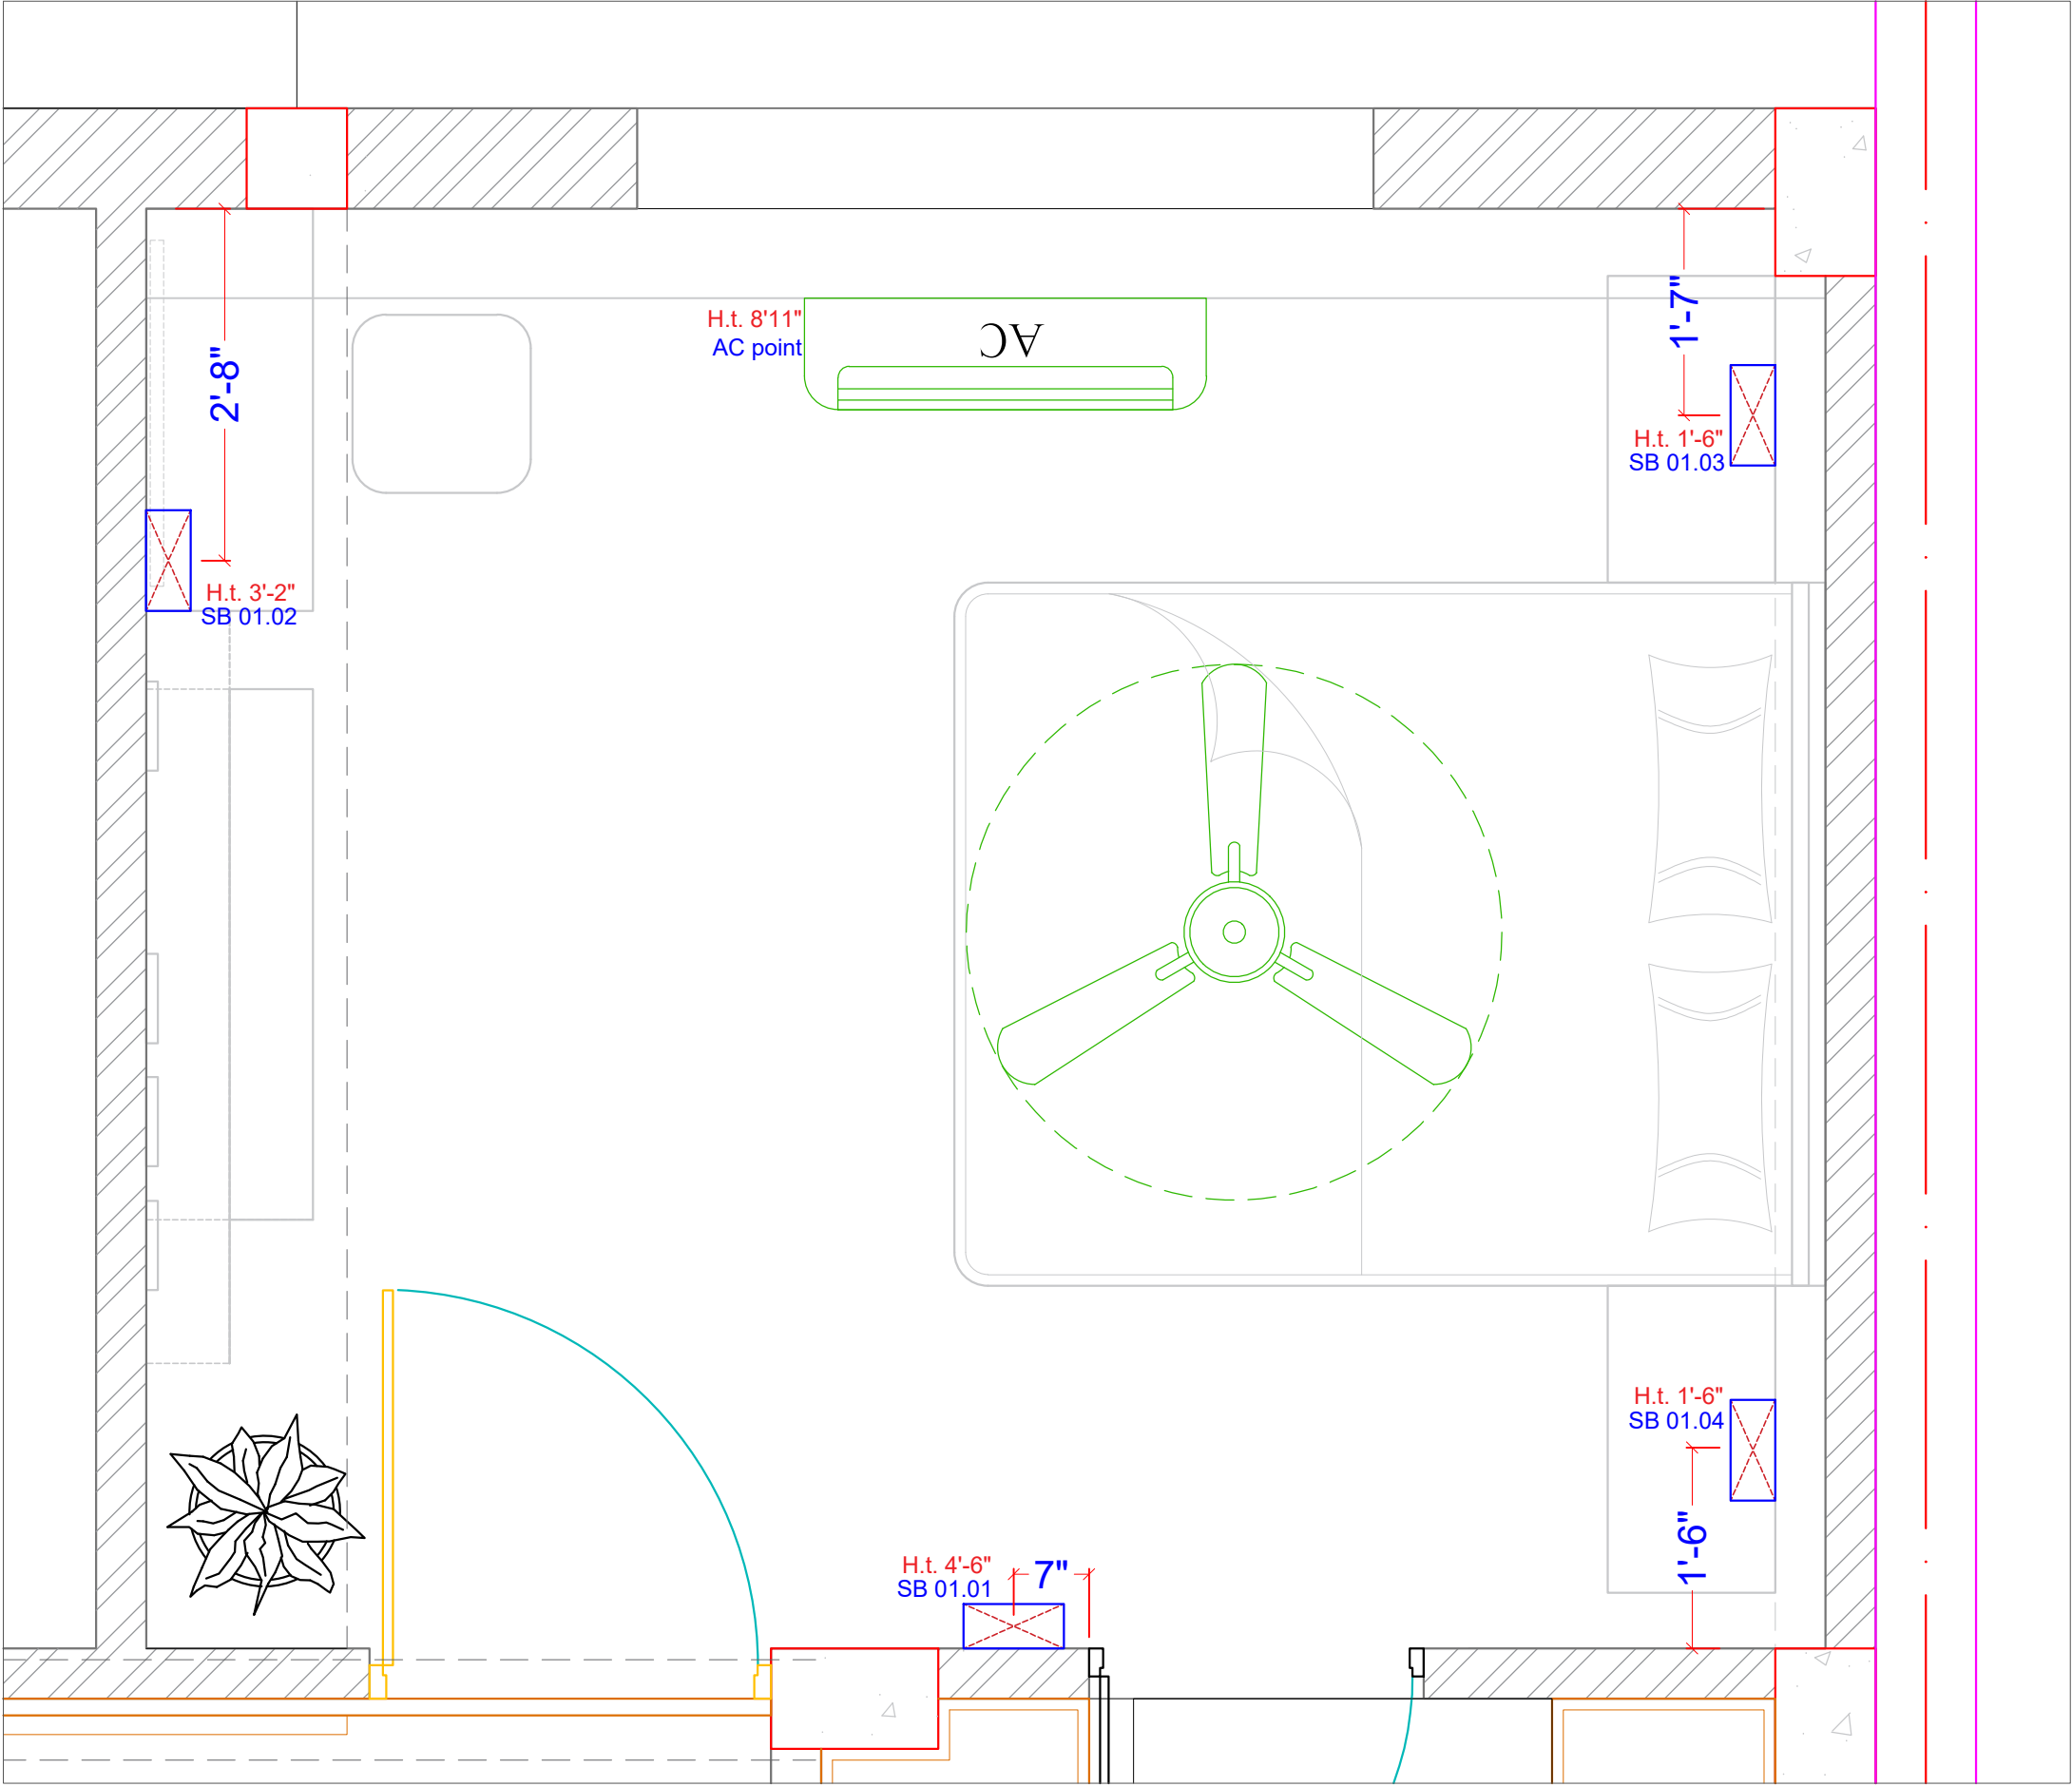

SWITCH BOARD LAYOUT

**PARENTS BEDROOM
SWITCH BOARD LAYOUT**

NOTES:

- * DO NOT SCALE THE DRAWING.
- * ALL DIMENSIONS ARE IN FEET \ INCHES.
- * ANY DISCREPANCY IN THE DRAWING TO BE BROUGHT IN THE DESIGNER'S NOTICE BEFORE IMPLEMENTATION ON SITE.

SITE ADDRESS:

**SAVAD
VADODARA**

CLIENT NAME:

RONAK PANCHOLI

DATE:

02-06-2025

NORTH:




DRAWING DETAIL

REVISION NO.	R1	R2	R3
REVISED DATE:	07/02/26		
SCALE:	N.T.S		
DRAWN BY:	ARCHANA		
CHECKED BY:	MITTAL		

	www.mayaspace.studio
	mayaspace.studio@gmail.com
	+918980144077
	@mayaspace.studio



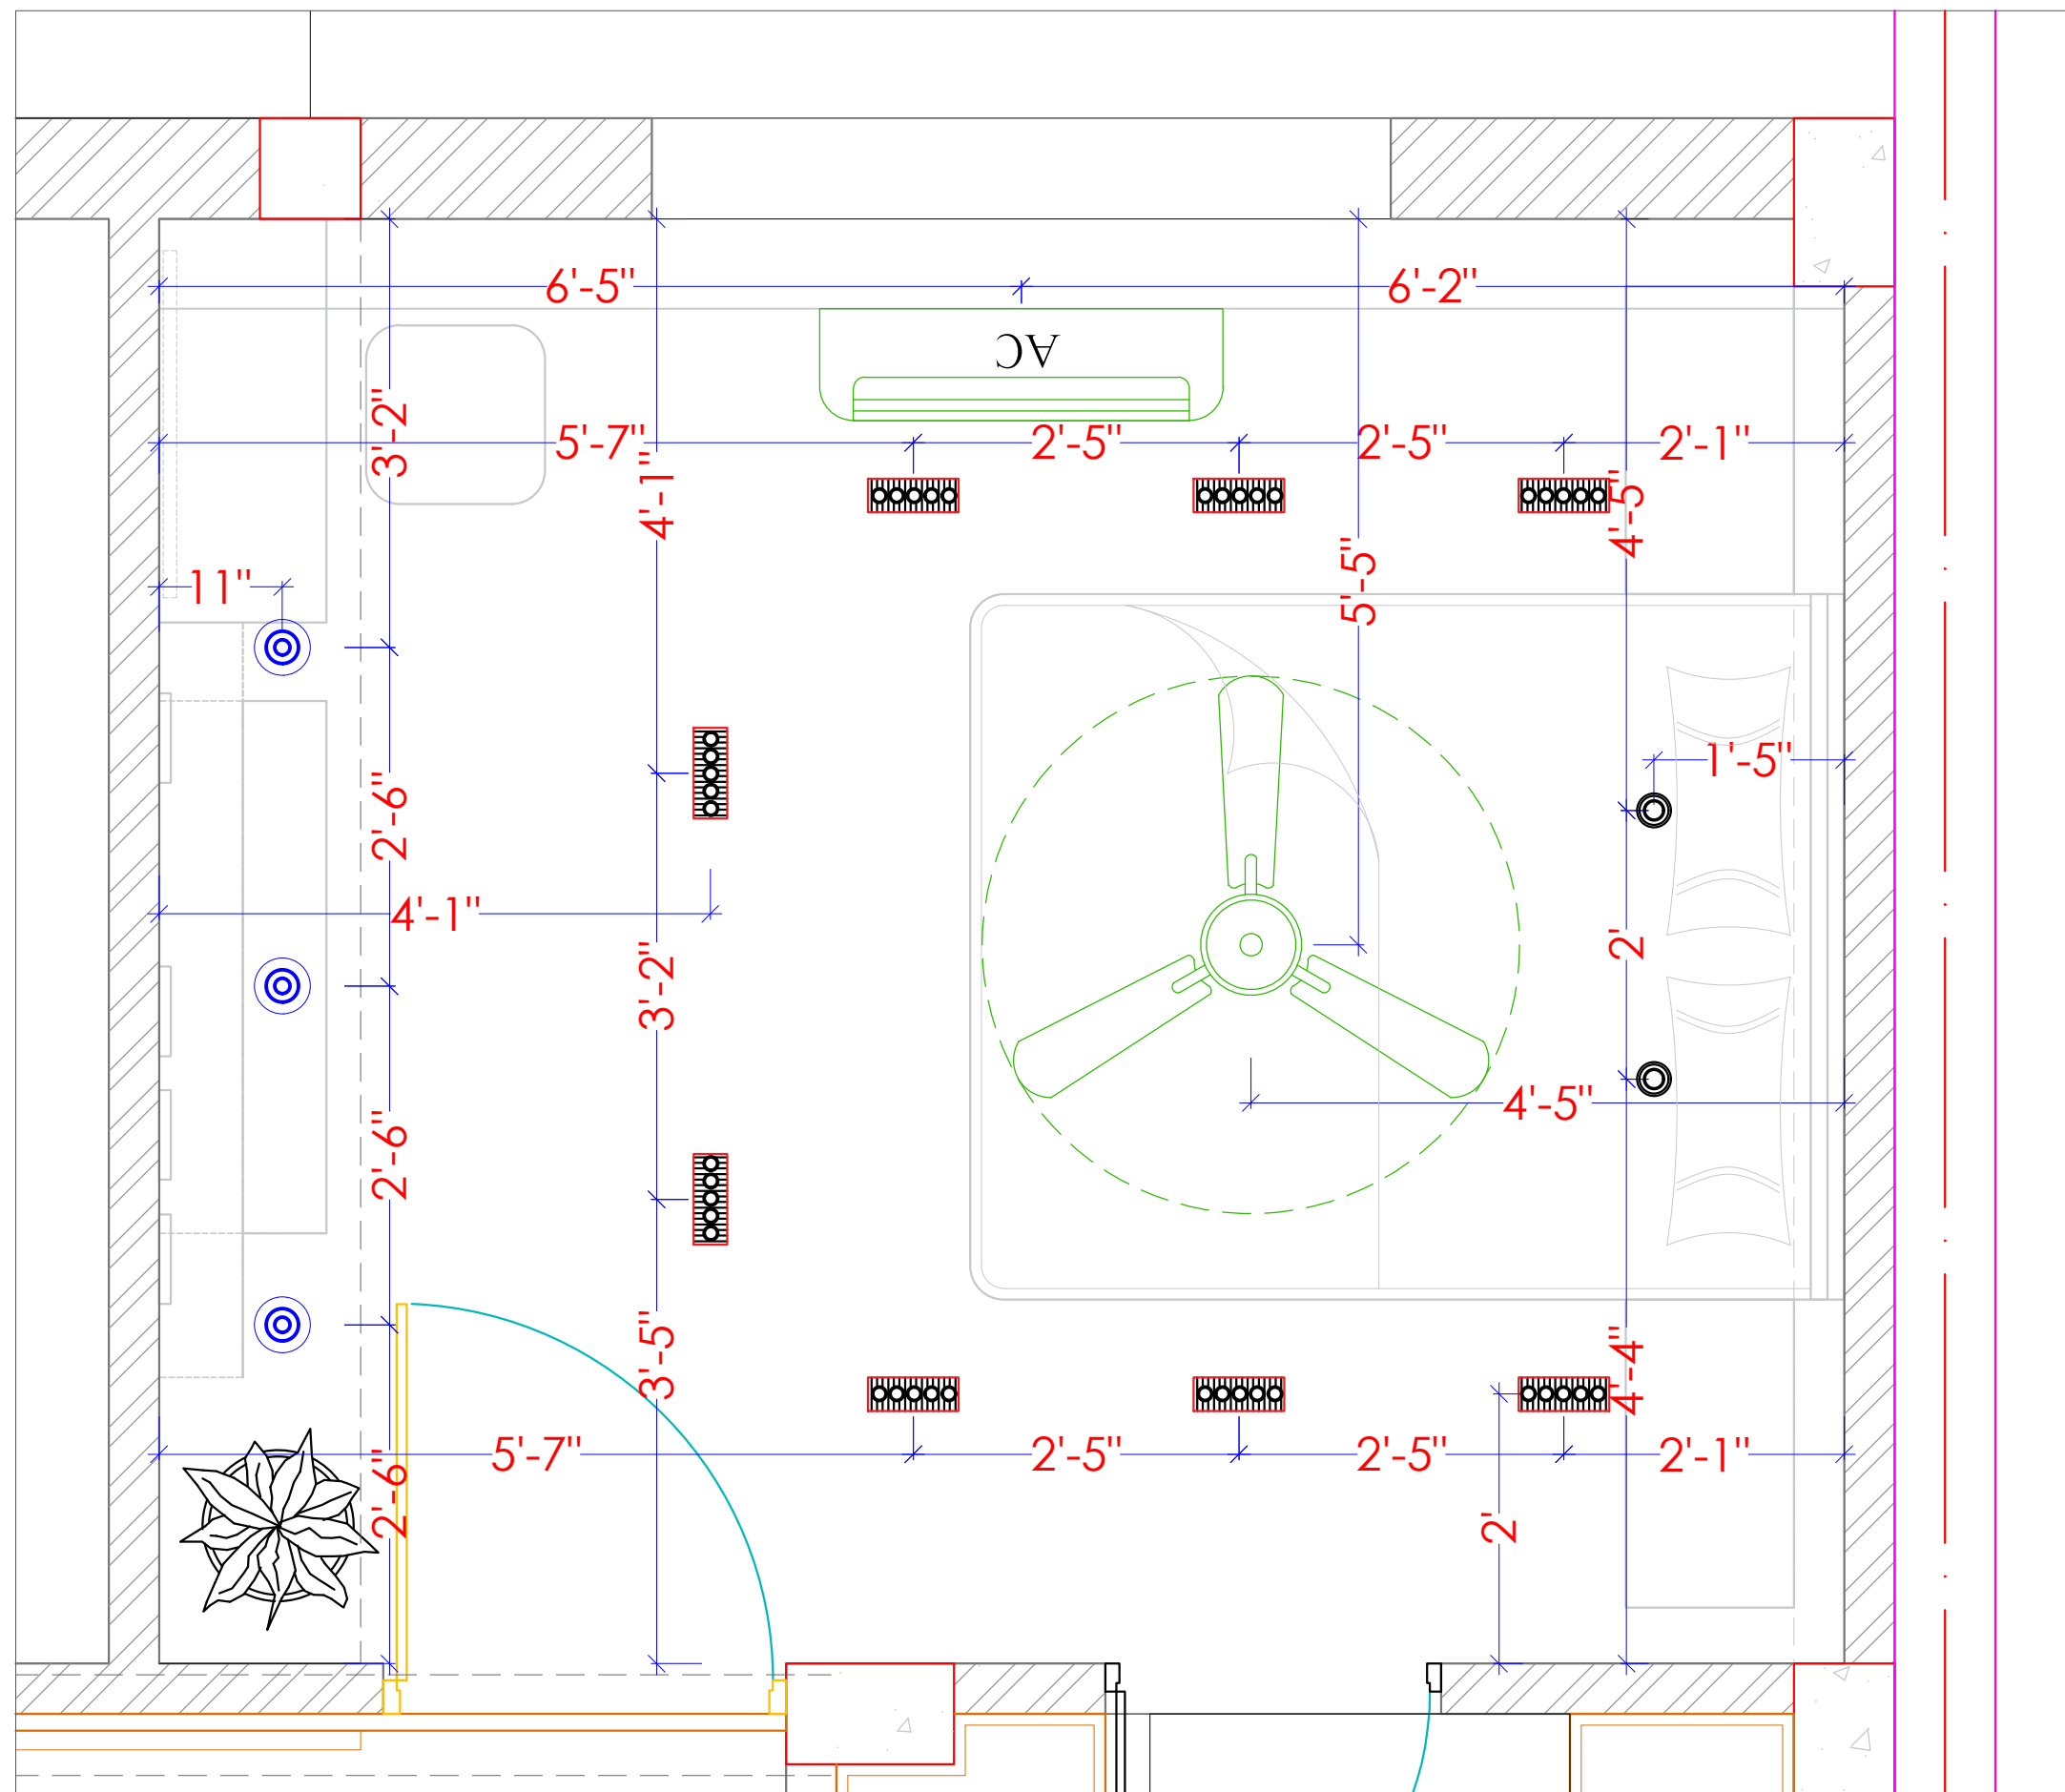

LIGHTING LAYOUT

**PARENTS BEDROOM
LIGHTING LAYOUT**

NOTES:

- * DO NOT SCALE THE DRAWING.
- * ALL DIMENSIONS ARE IN FEET \ INCHES.
- * ANY DISCREPANCY IN THE DRAWING TO BE BROUGHT IN THE DESIGNER'S NOTICE BEFORE IMPLEMENTATION ON SITE.

SITE ADDRESS:

SAVAD
VADODARA

CLIENT NAME:

RONAK PANCHOLI

DATE:

02-06-2025

NORTH:




DRAWING DETAIL

REVISION NO.	R1	R2	R3
REVISED DATE:	07/02/26		
SCALE:	N.T.S		
DRAWN BY:	ARCHANA		
CHECKED BY:	MITTAL		

	www.mayaspace.studio
	mayaspace.studio@gmail.com
	+918980144077
	@mayaspace.studio



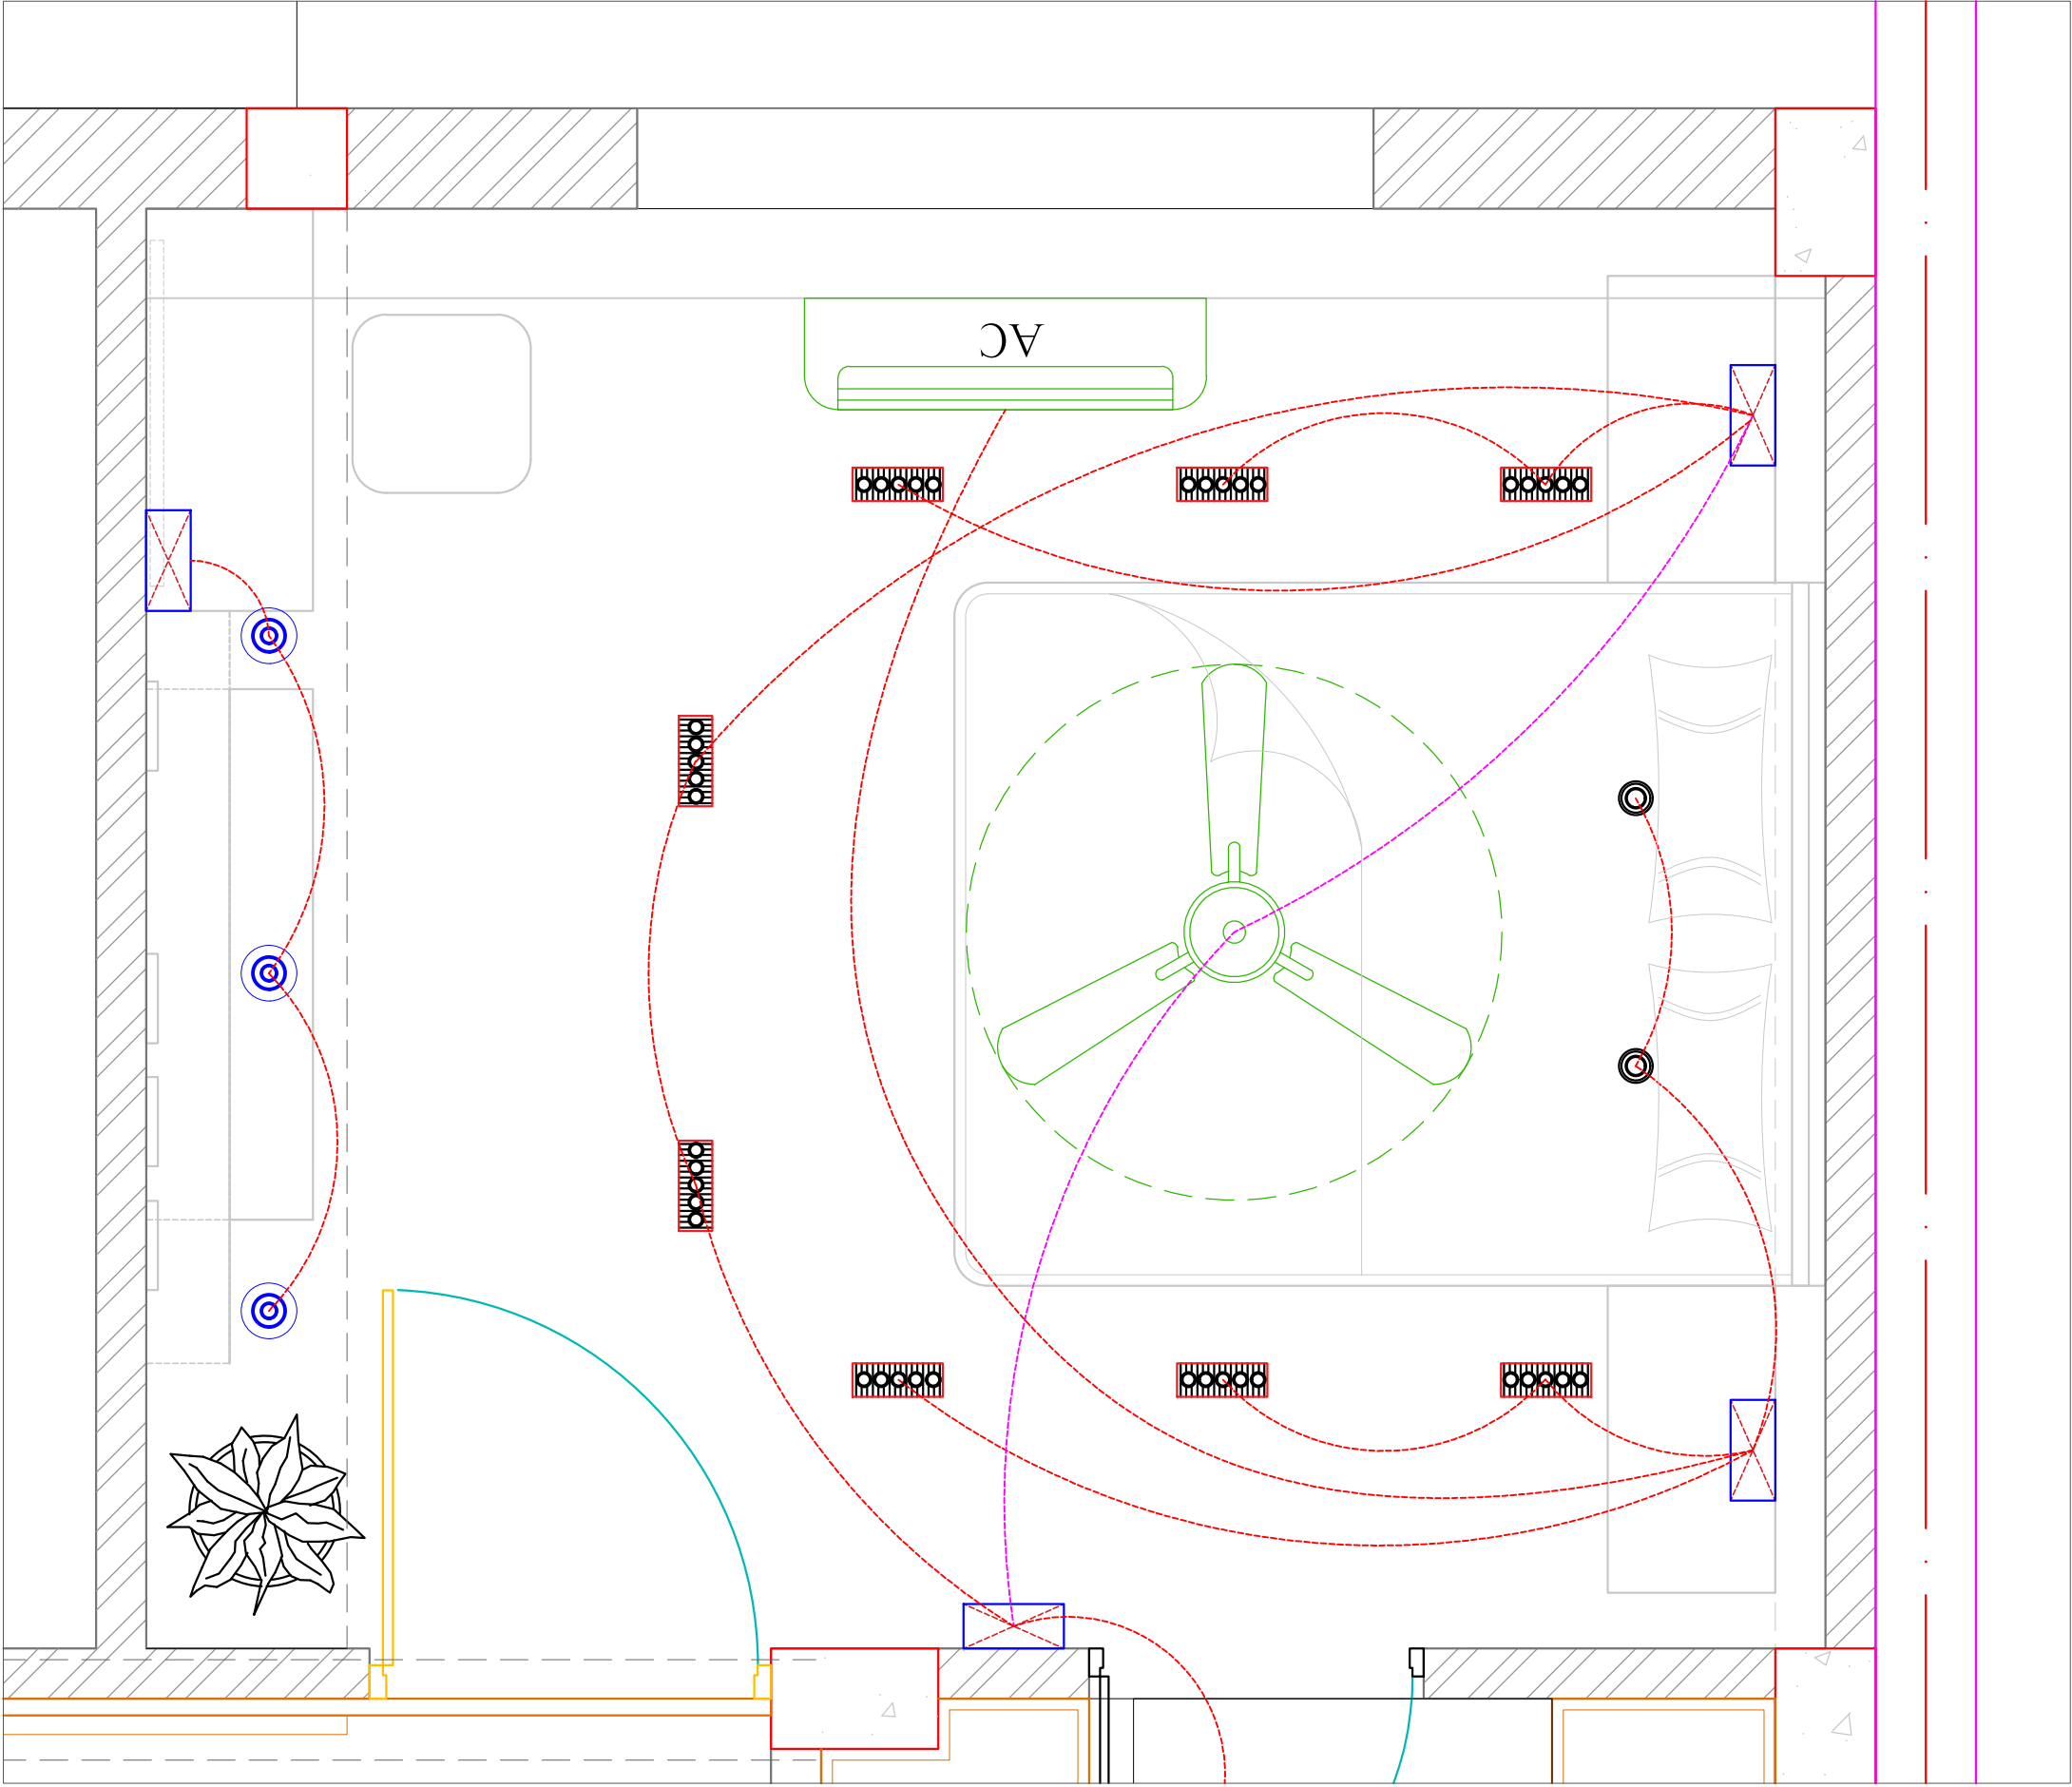

LOOPING LAYOUT

PARENTS BEDROOM LOOPING LAYOUT

NOTES:

- * DO NOT SCALE THE DRAWING.
- * ALL DIMENSIONS ARE IN FEET \ INCHES.
- * ANY DISCREPANCY IN THE DRAWING TO BE BROUGHT IN THE DESIGNER'S NOTICE BEFORE IMPLEMENTATION ON SITE.

SITE ADDRESS:

SAVAD
VADODARA

CLIENT NAME:

RONAK PANCHOLI

DATE:

02-06-2025

NORTH:



DRAWING DETAIL

REVISION NO.	R1	R2	R3
REVISED DATE:	07/02/26		
SCALE:	N.T.S		
DRAWN BY:	ARCHANA		
CHECKED BY:	MITTAL		

	www.mayaspace.studio
	mayaspace.studio@gmail.com
	+918980144077
	@mayaspace.studio



PARENTS BEDROOM ELEVATION A

- * DO NOT SCALE THE DRAWING.
- * ALL DIMENSIONS ARE IN FEET \ INCHES.
- * ANY DISCREPANCY IN THE DRAWING TO BE BROUGHT IN THE DESIGNER'S NOTICE BEFORE IMPLEMENTATION ON SITE.


SAVAD
VADODARA

RONAK PANCHOLI

NORTH:

REVISION NO.	R1	R2	R3
REVISED DATE:	07/02/26		
SCALE:	N.T.S		
DRAWN BY:	ARCHANA		
CHECKED BY:	MITTAL		

	www.mayaspace.studio
	mayaspace.studio@gmail.com
	+918980144077
	@mayaspace.studio

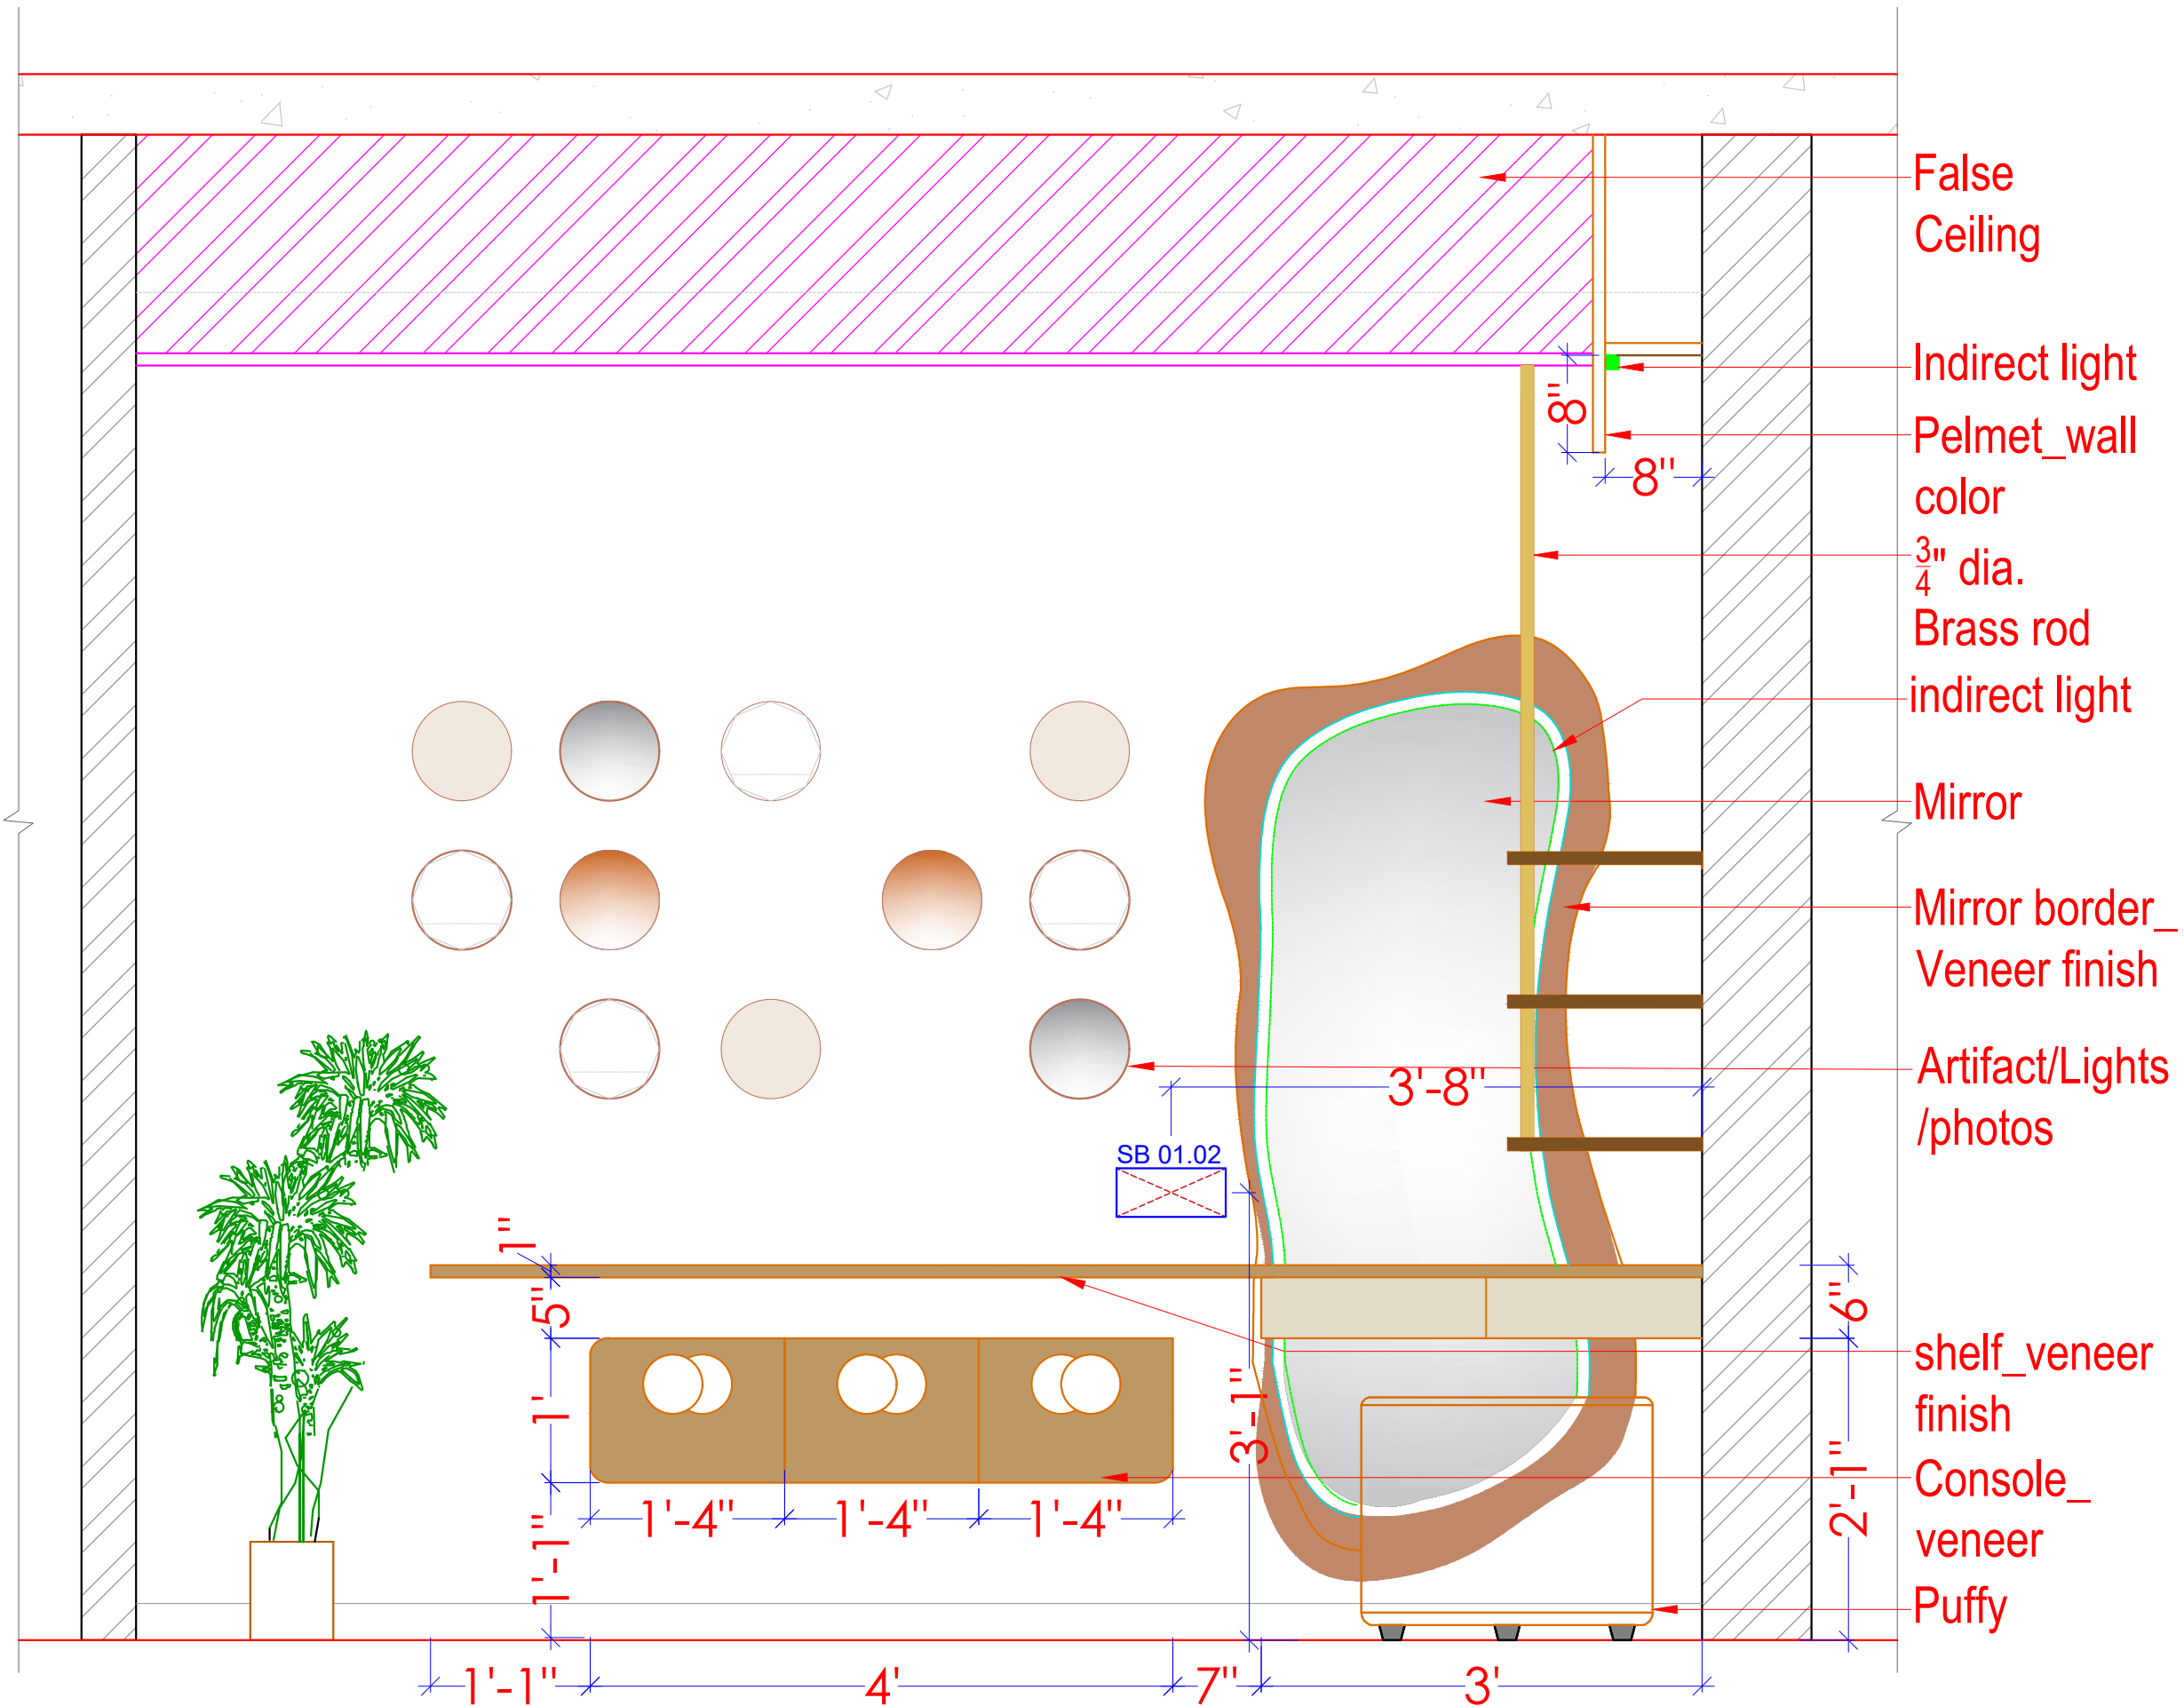

ELEVATION - A

PARENTS BEDROOM ELEVATION B

- * DO NOT SCALE THE DRAWING.
- * ALL DIMENSIONS ARE IN FEET \ INCHES.
- * ANY DISCREPANCY IN THE DRAWING TO BE BROUGHT IN THE DESIGNER'S NOTICE BEFORE IMPLEMENTATION ON SITE.


SAVAD
VADODARA

RONAK PANCHOLI

NORTH:

REVISION NO.	R1 R2 R3
REVISED DATE:	07/02/26
SCALE:	N.T.S
DRAWN BY:	ARCHANA
CHECKED BY:	MITTAL

- www.mayaspace.studio
- mayaspace.studio@gmail.com
- +918980144077
- [@mayaspace.studio](https://www.instagram.com/mayaspace.studio)

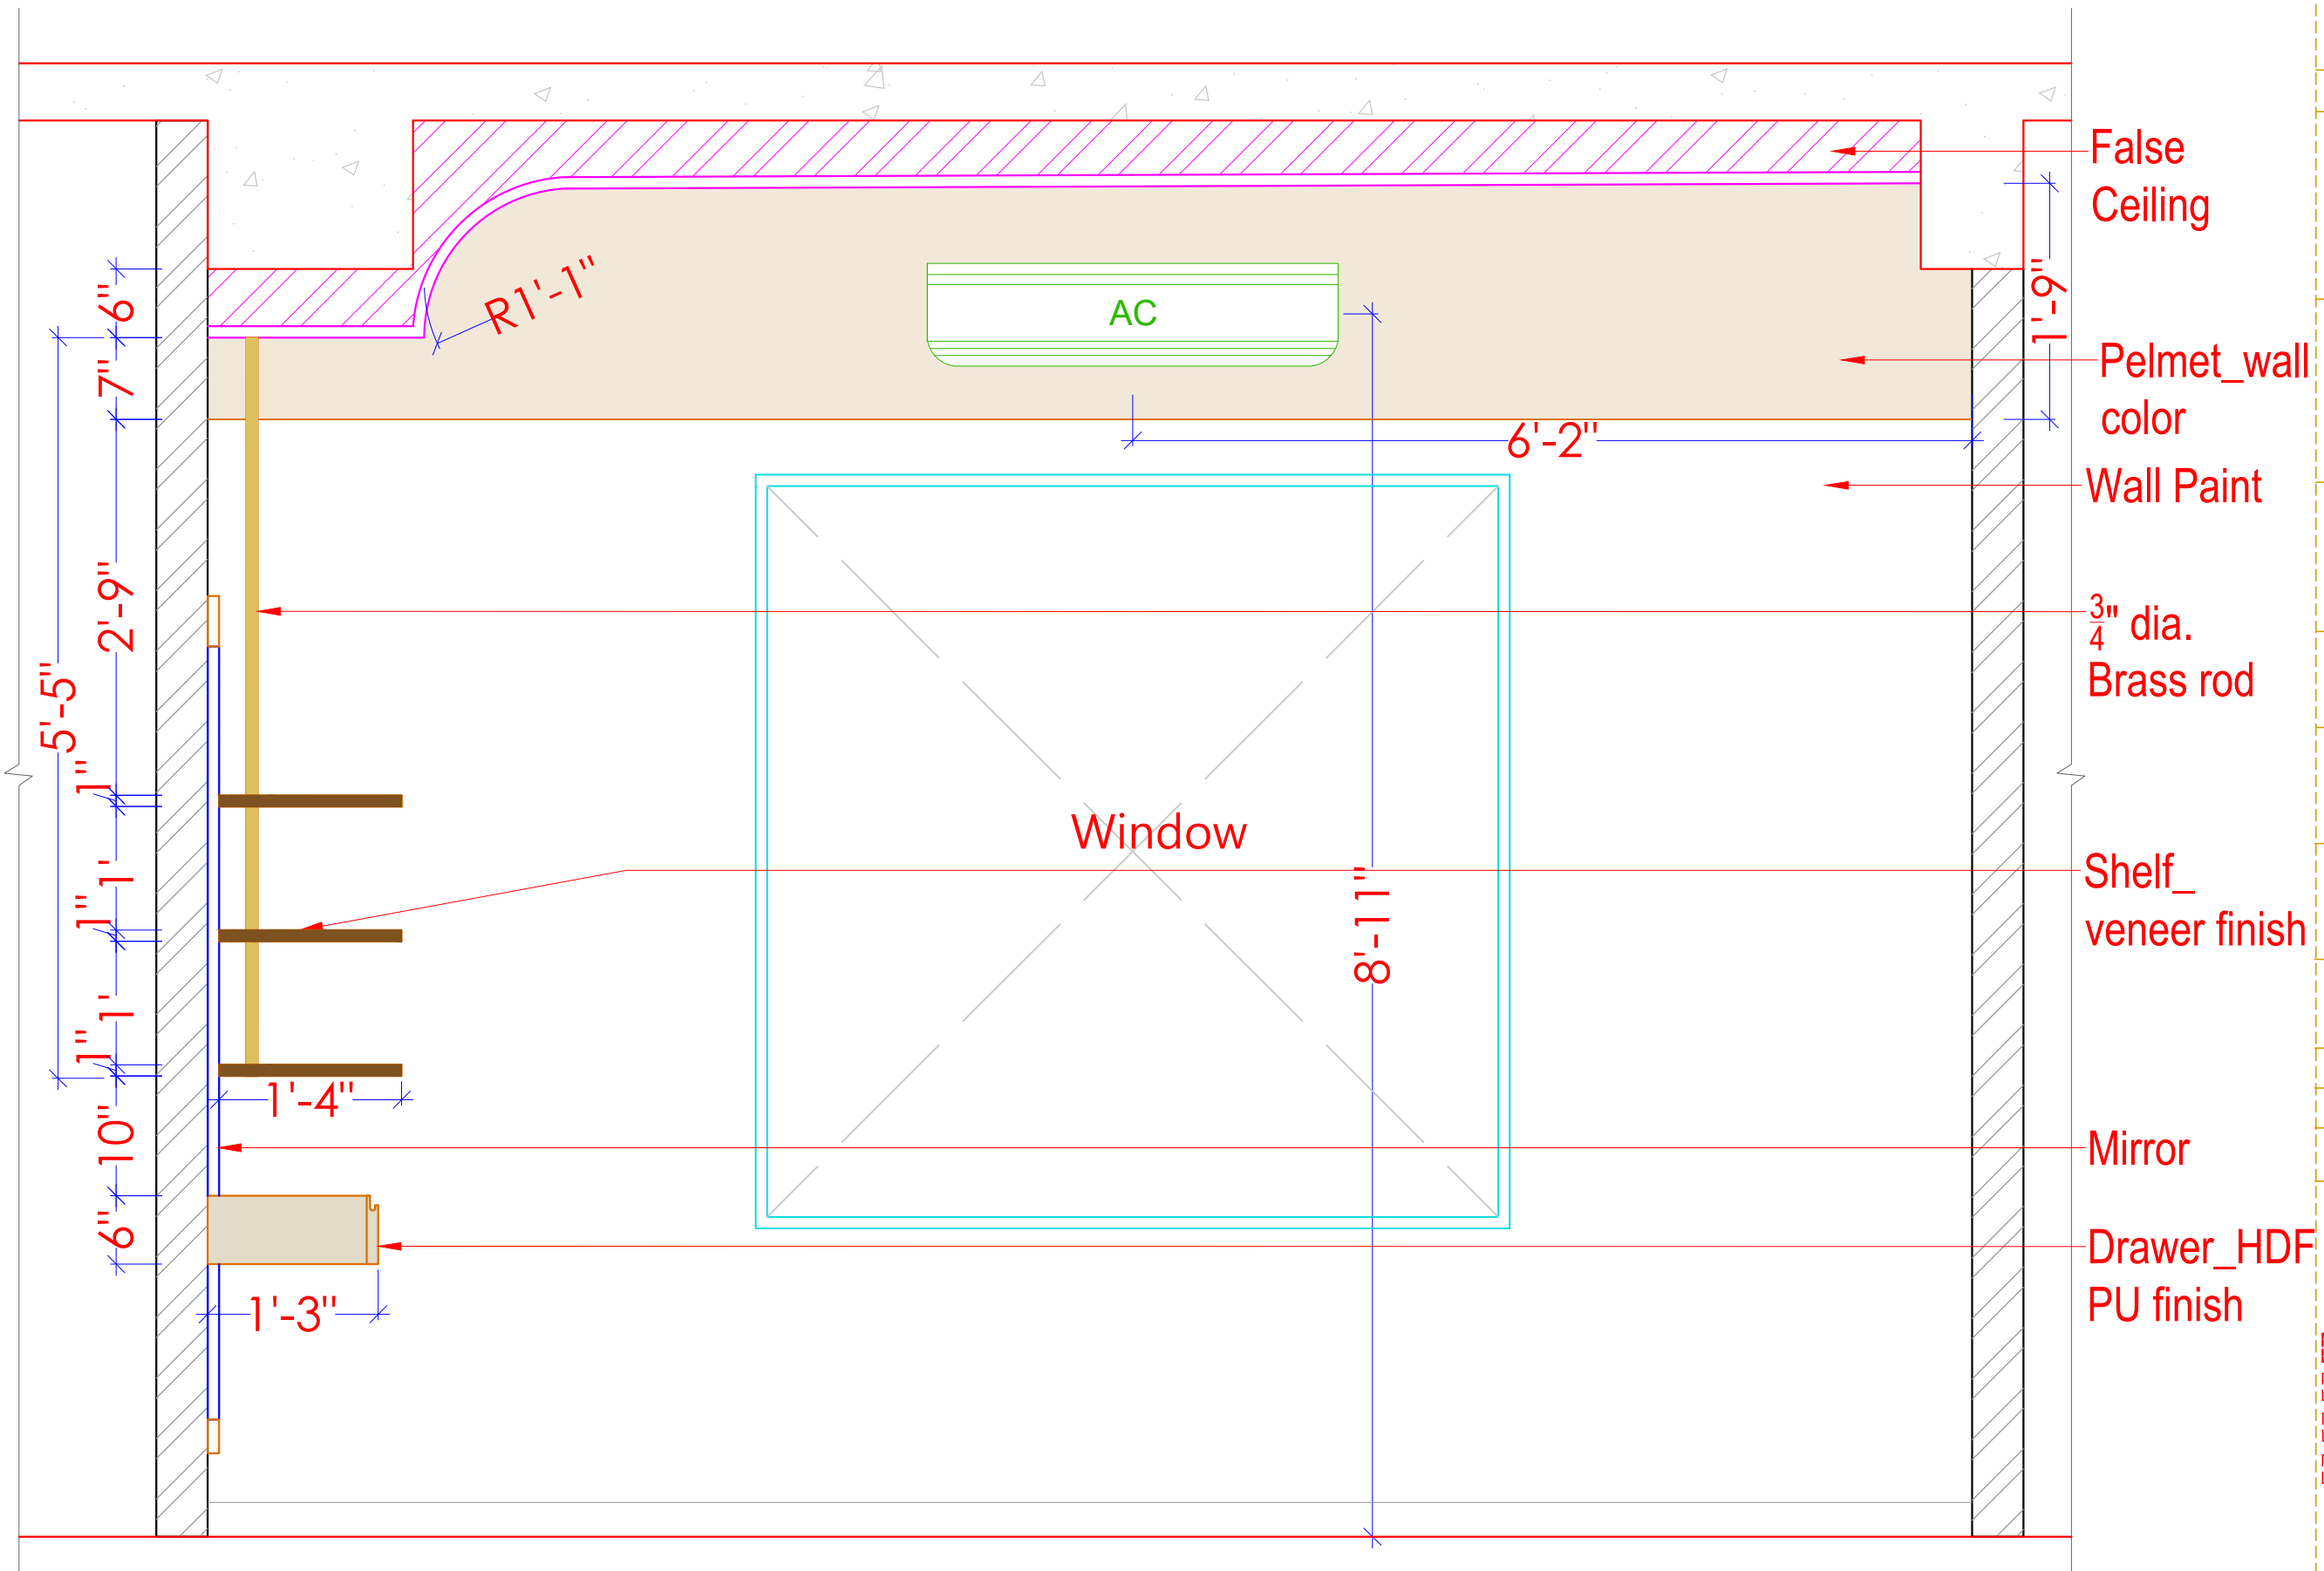

ELEVATION - B

PARENTS BEDROOM ELEVATION C

- * DO NOT SCALE THE DRAWING.
- * ALL DIMENSIONS ARE IN FEET \ INCHES.
- * ANY DISCREPANCY IN THE DRAWING TO BE BROUGHT IN THE DESIGNER'S NOTICE BEFORE IMPLEMENTATION ON SITE.


SAVAD
VADODARA

RONAK PANCHOLI


NORTH:

REVISION NO.	R1	R2	R3
REVISED DATE:	07/02/2025		
SCALE:	N.T.S		
DRAWN BY:	ARCHANA		
CHECKED BY:	MITTAL		

	www.mayaspace.studio
	mayaspace.studio@gmail.com
	+918980144077
	@mayaspace.studio

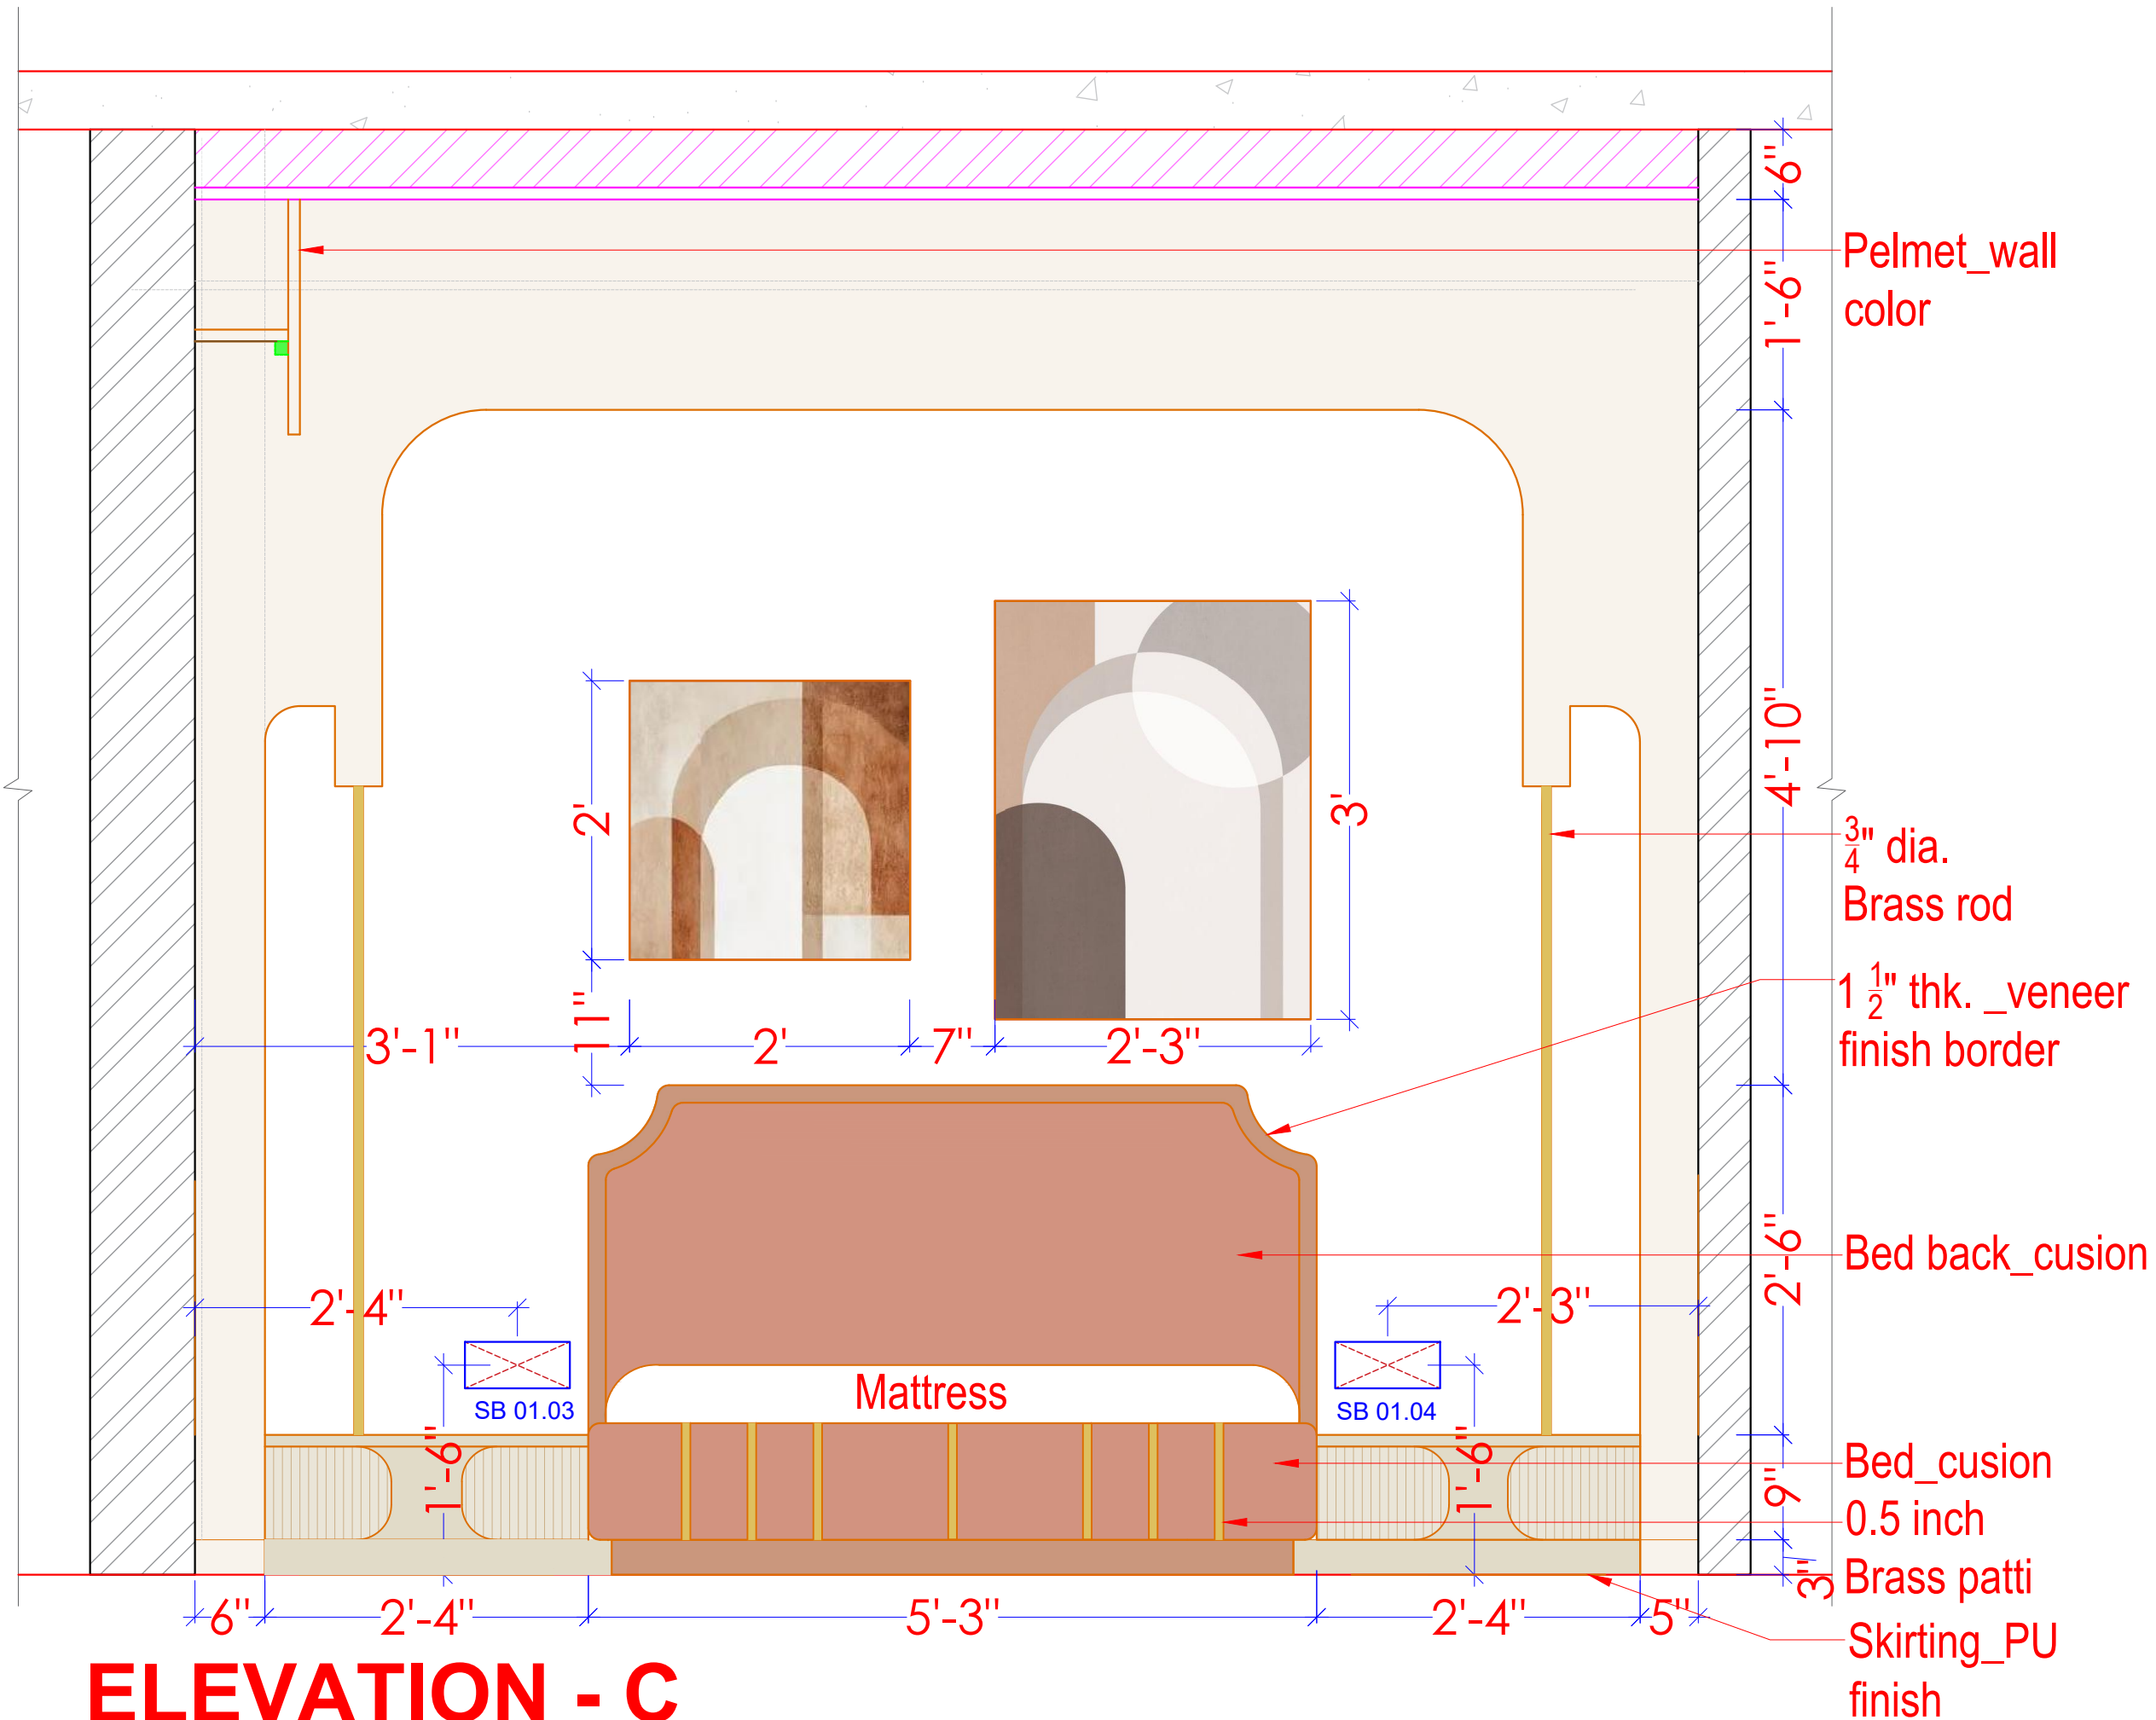

ELEVATION - C

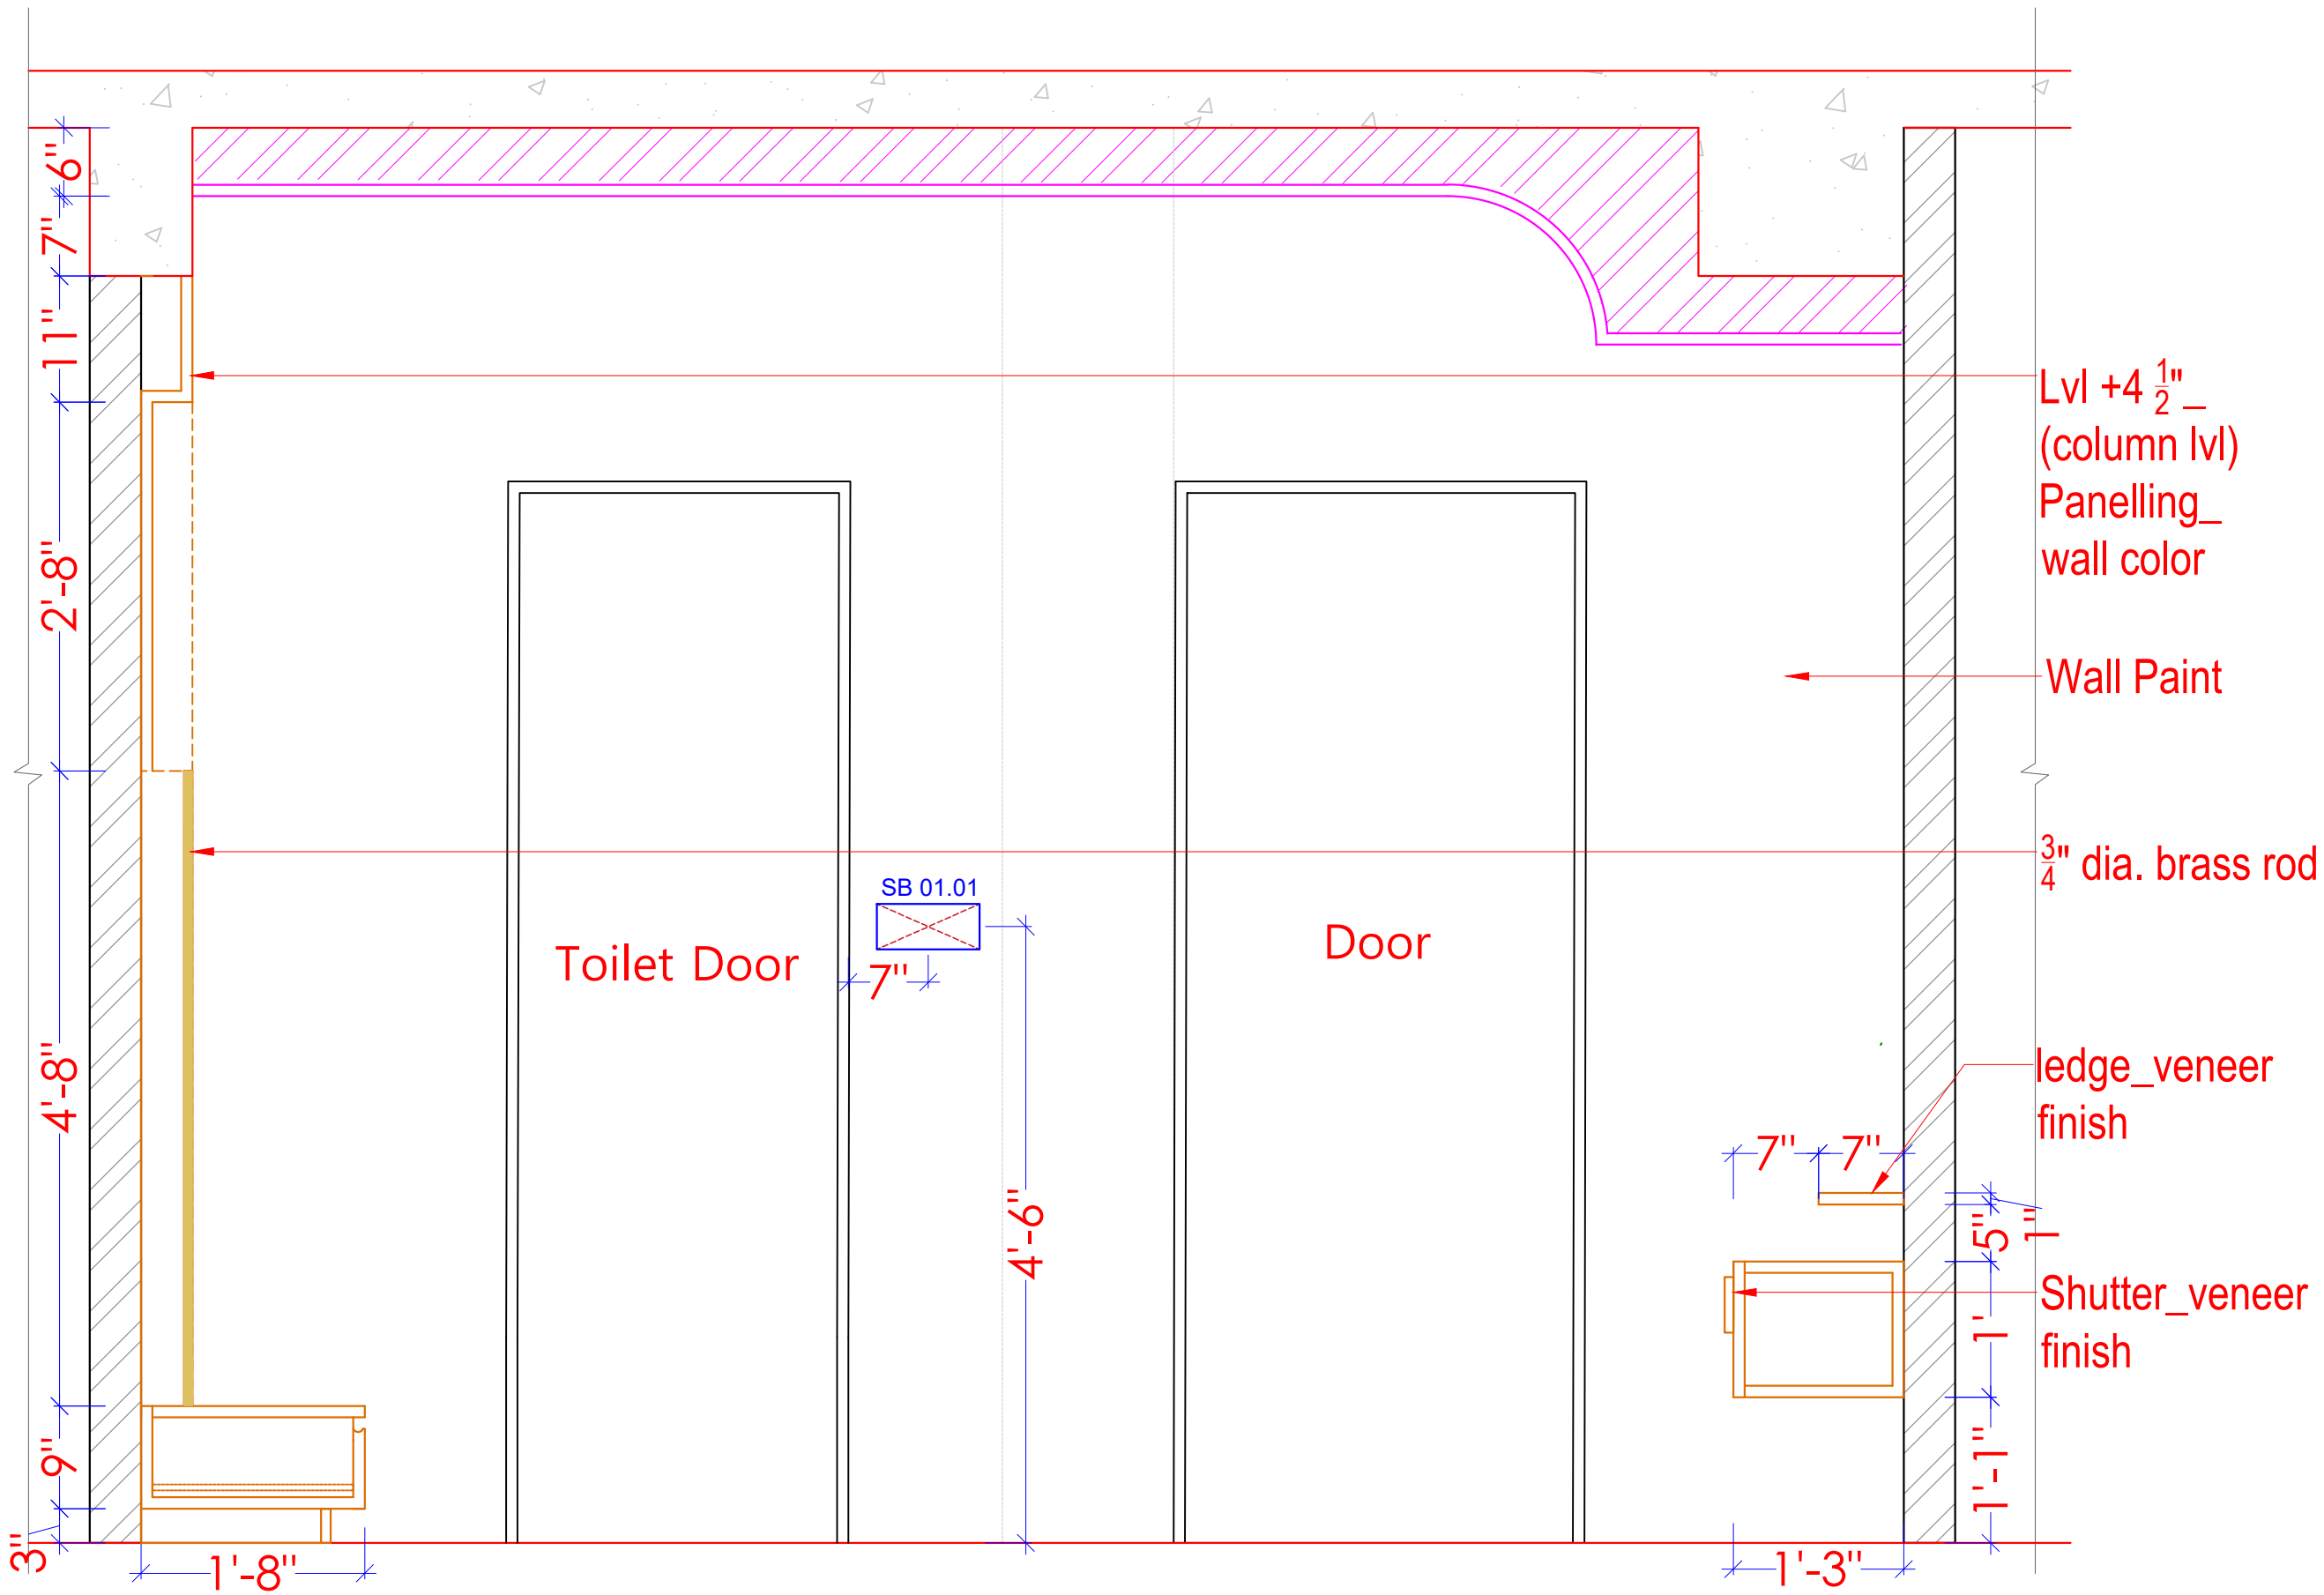

ELEVATION - D

DRAWING TITLE :

PARENTS BEDROOM
ELEVATION D

NOTES:

* DO NOT SCALE THE DRAWING.
* ALL DIMENSIONS ARE IN FEET \ INCHES.
* ANY DISCREPANCY IN THE DRAWING
TO BE BROUGHT IN THE DESIGNER'S
NOTICE BEFORE IMPLEMENTATION
ON SITE.

SITE ADDRESS:

SAVAD
VADODARA

CLIENT NAME:

RONAK PANCHOLI

DATE: 02-06-2025

NORTH:

DRAWING DETAIL

REVISION NO.	R1 R2 R3
REVISED DATE:	07/02/26
SCALE:	N.T.S
DRAWN BY:	ARCHANA
CHECKED BY:	MITTAL



 www.mayaspace.studio

 mayaspace.studio@gmail.com


 +918980144077

 @mayaspace.studio




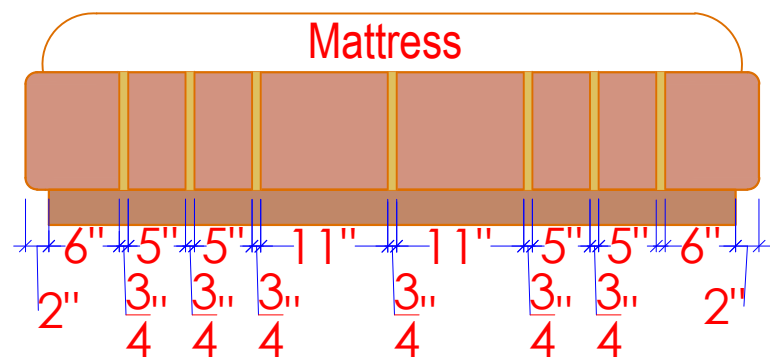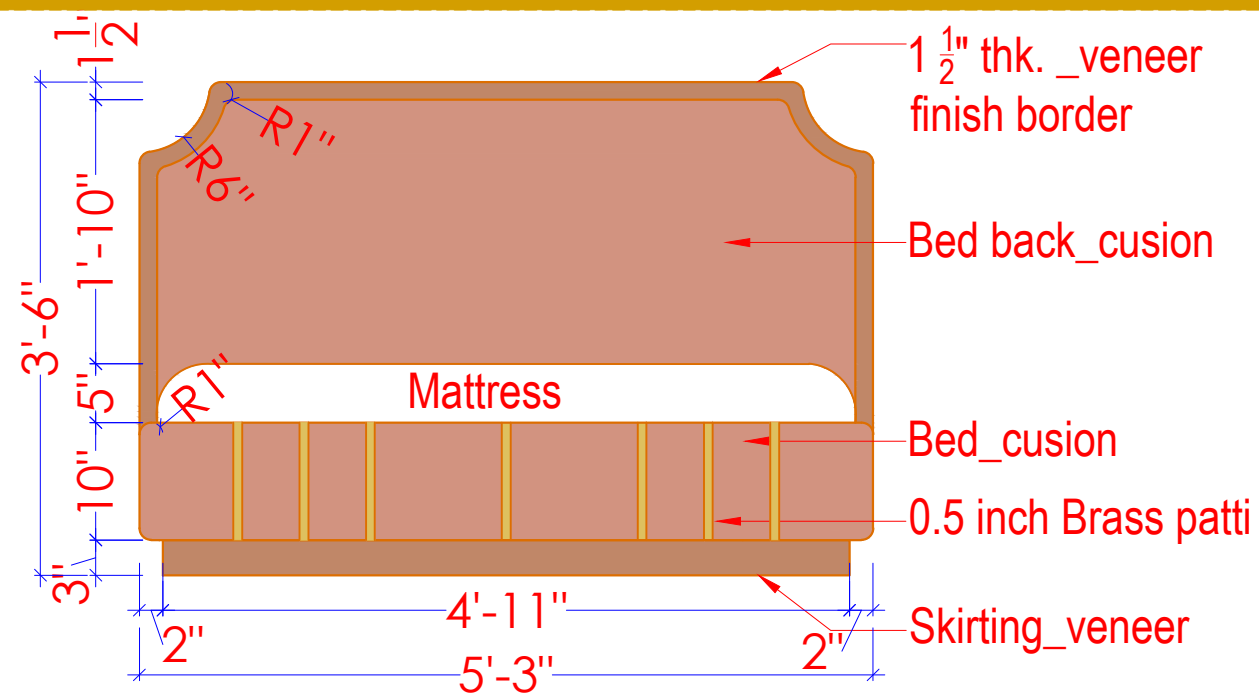


BED ELEVATION

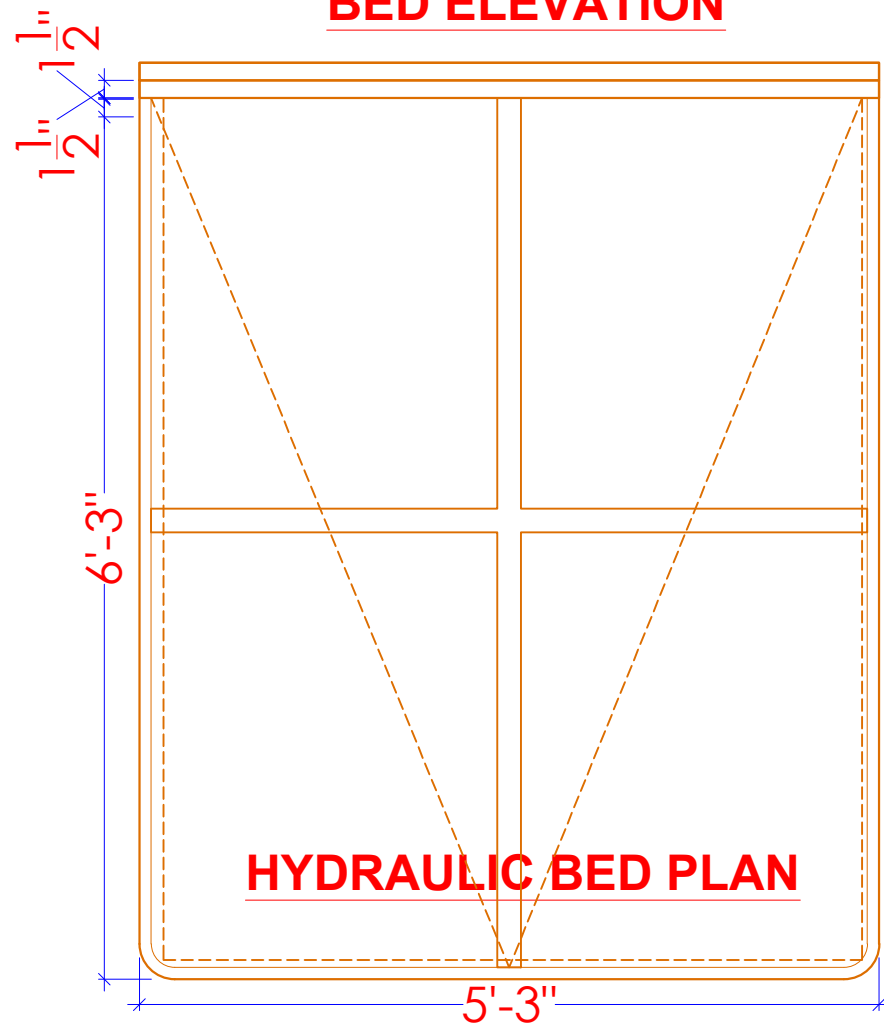


HYDRAULIC BED PLAN

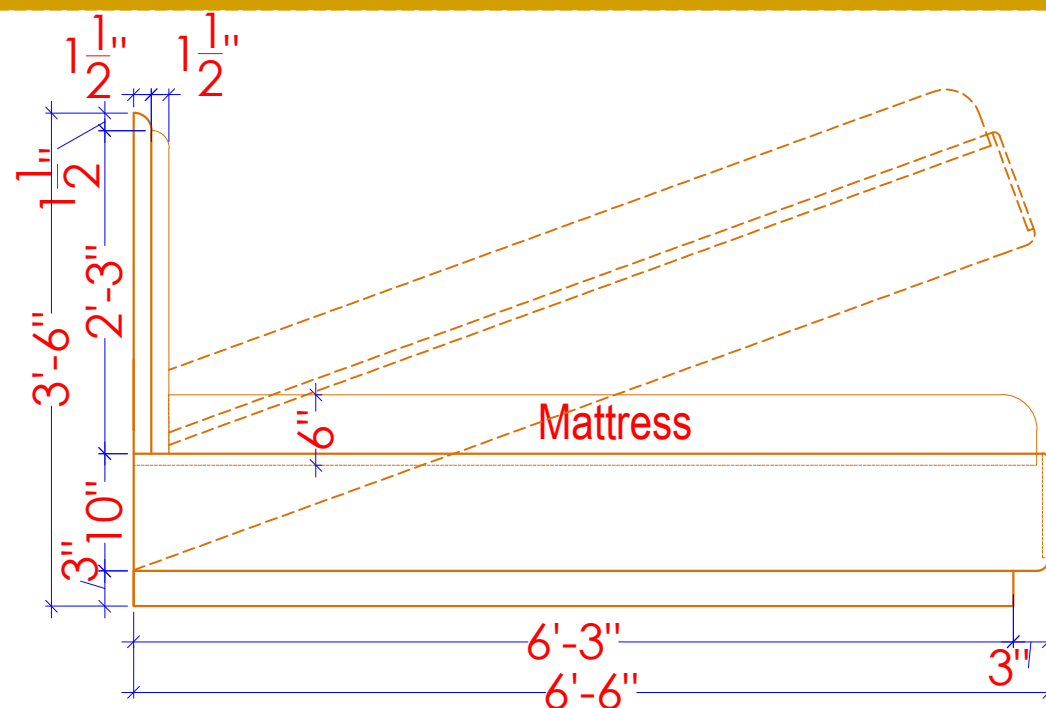


BED SIDE ELEVATION

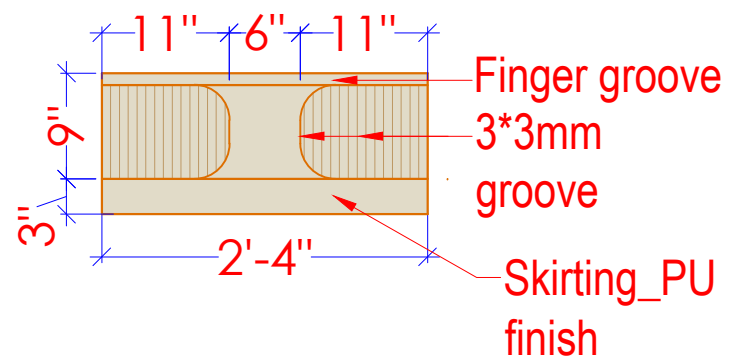


SIDE TABLE ELEVATION

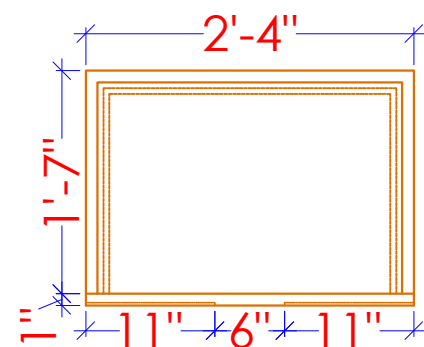

SIDE TABLE PLAN

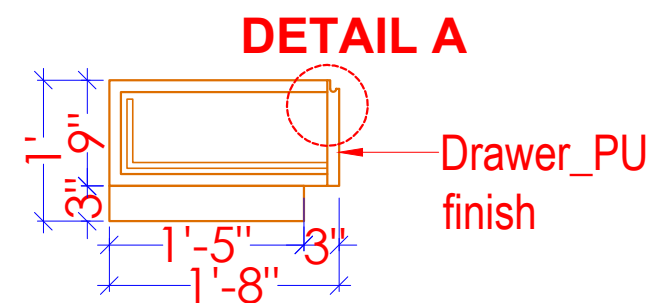

SIDE TABLE SECTION

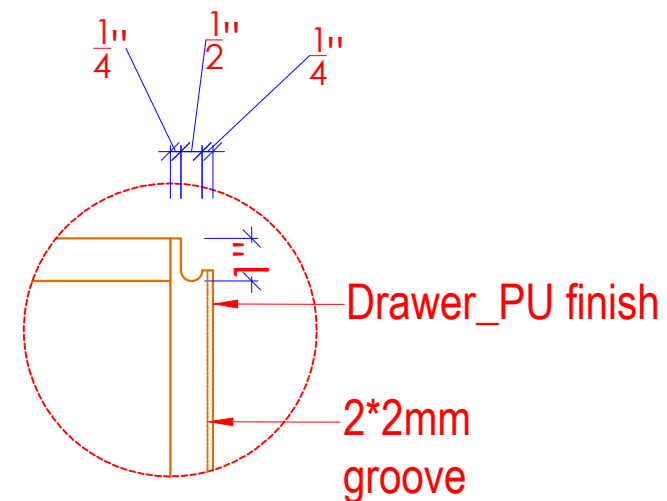

DETAIL A

PARENTS BEDROOM BED DETAIL

NOTES:

- * DO NOT SCALE THE DRAWING.
- * ALL DIMENSIONS ARE IN FEET \ INCHES.
- * ANY DISCREPANCY IN THE DRAWING TO BE BROUGHT IN THE DESIGNER'S NOTICE BEFORE IMPLEMENTATION ON SITE.

SITE ADDRESS:

SAVAD
VADODARA

CLIENT NAME:

RONAK PANCHOLI

DATE:

02-06-2025

NORTH:



DRAWING DETAIL

REVISION NO.

R1 R2 R3

REVISED DATE:

07/02/26

SCALE:

N.T.S

DRAWN BY:

ARCHANA

CHECKED BY:

MITTAL




www.mayaspace.studio

mayaspace.studio@gmail.com



+918980144077

@mayaspace.studio



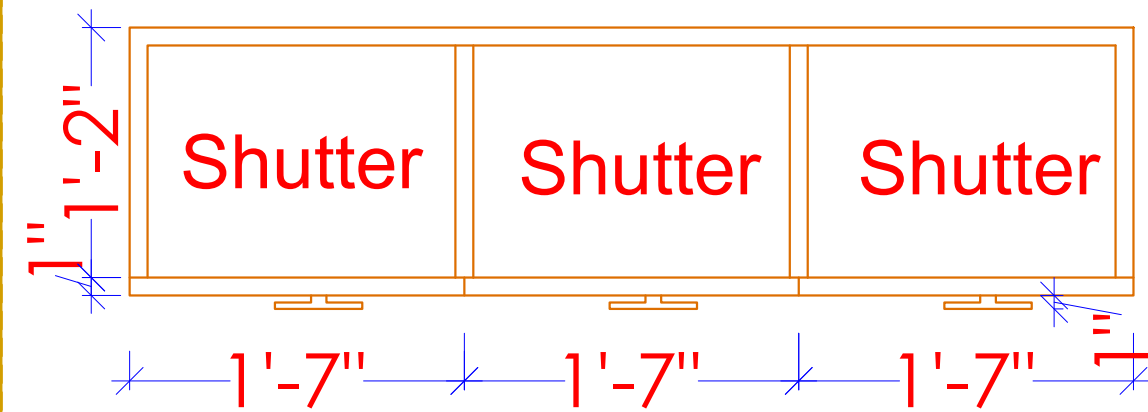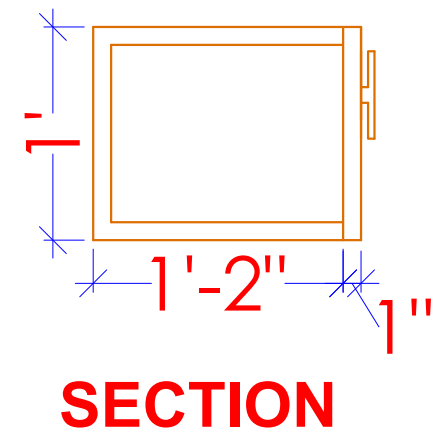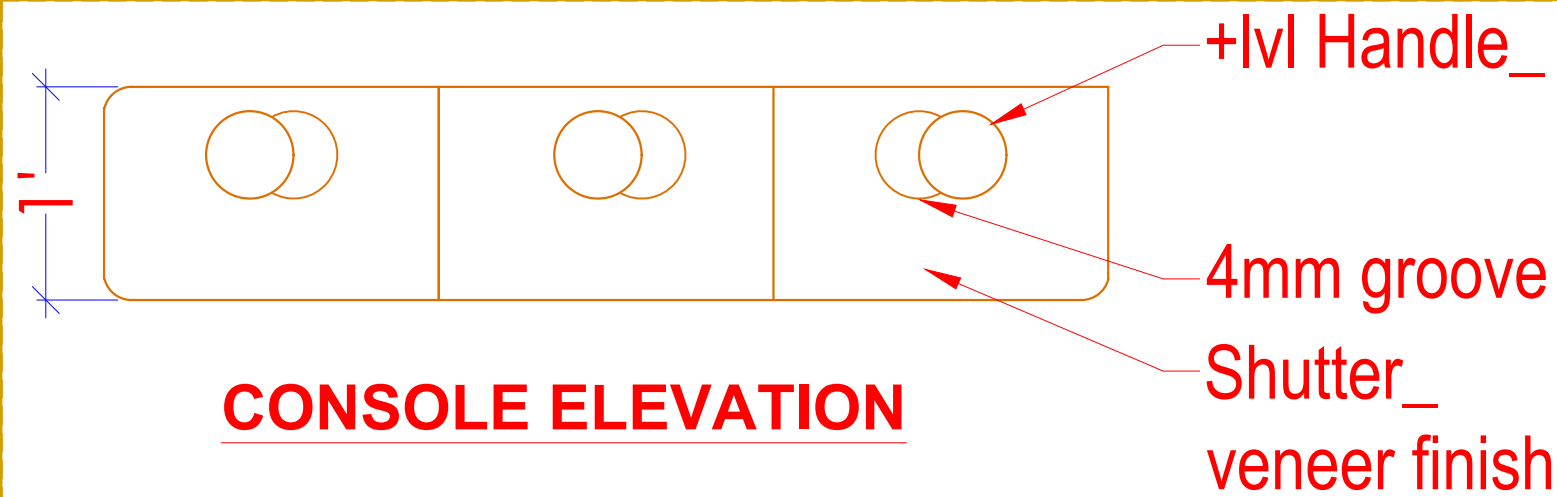


PLAN

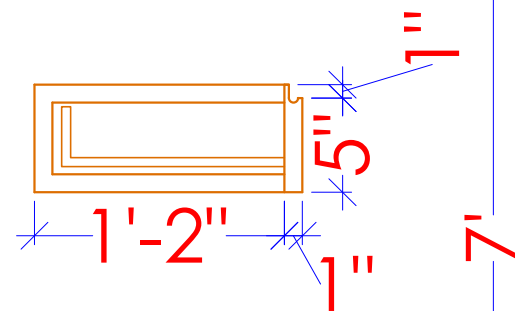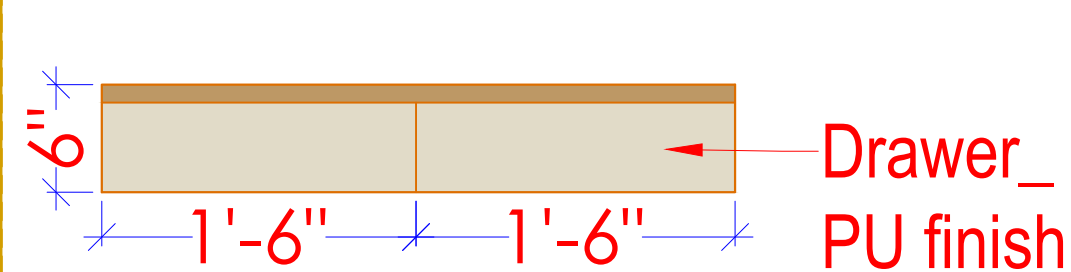


SECTION

DRAWER ELEVATION

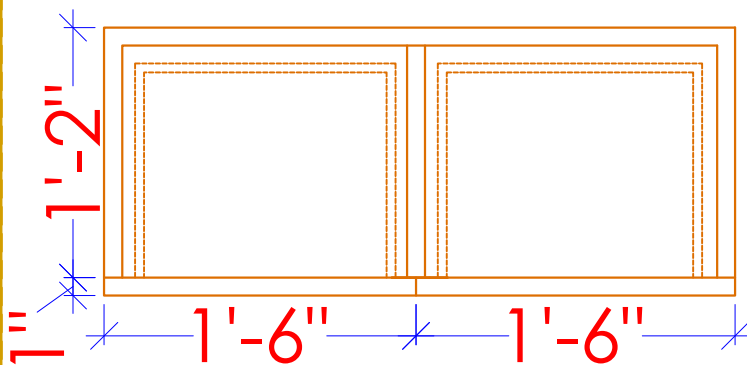

PLAN

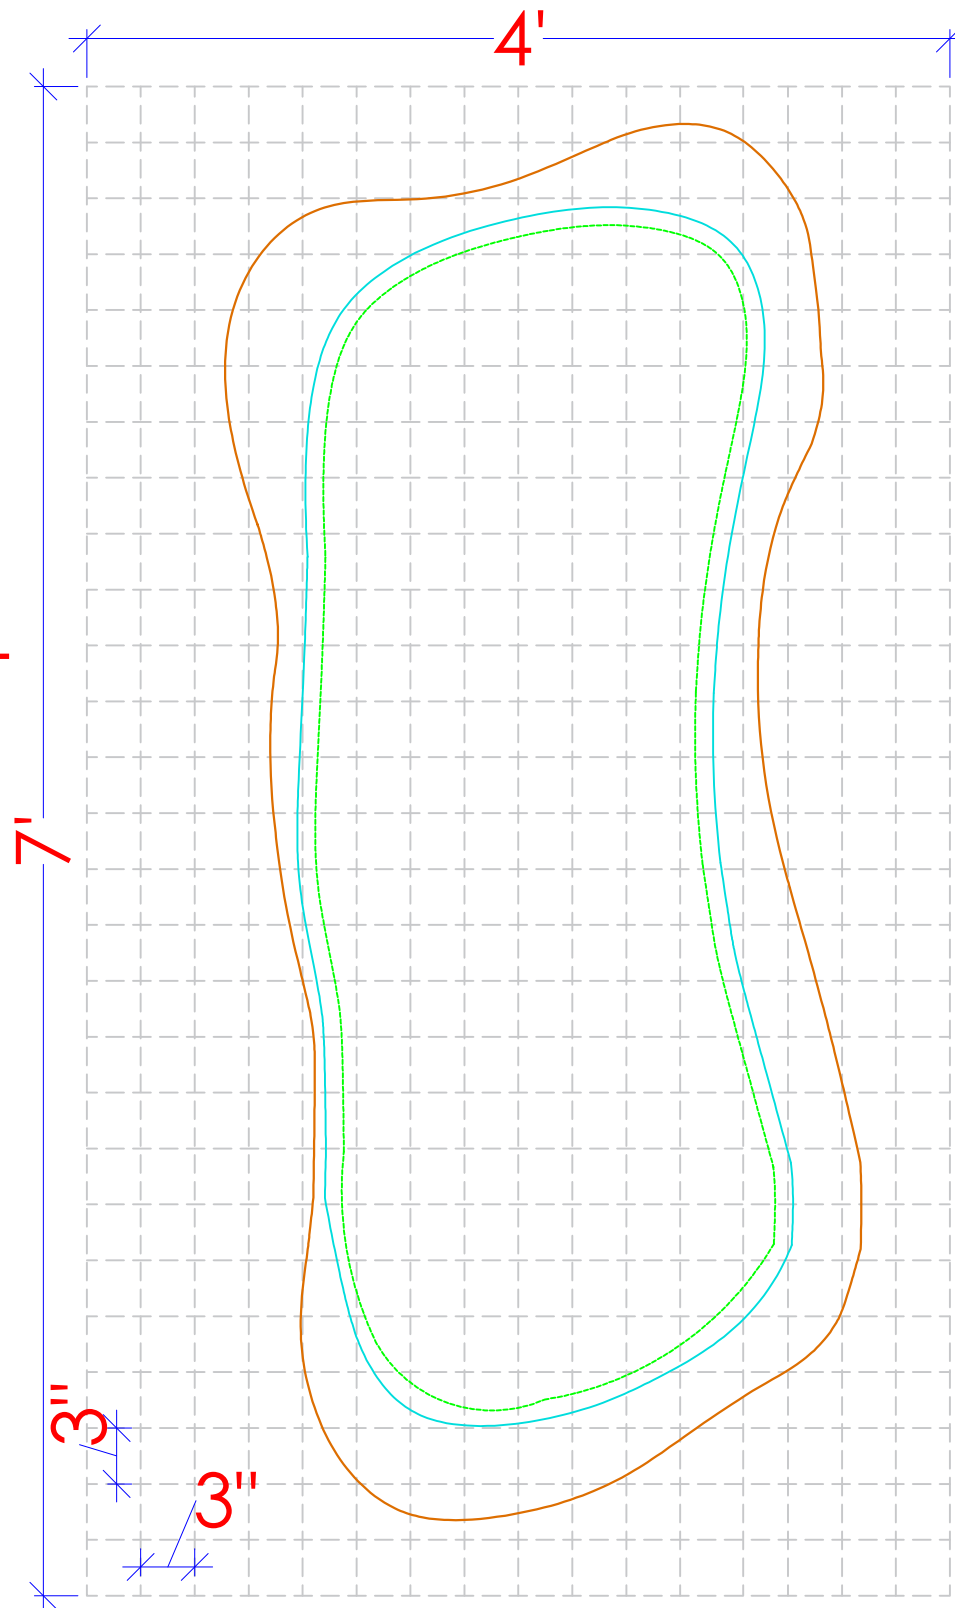

**PARENTS BEDROOM
DRESSING DETAIL**

NOTES:

- * DO NOT SCALE THE DRAWING.
- * ALL DIMENSIONS ARE IN FEET \ INCHES.
- * ANY DISCREPANCY IN THE DRAWING TO BE BROUGHT IN THE DESIGNER'S NOTICE BEFORE IMPLEMENTATION ON SITE.

SITE ADDRESS:

SAVAD
VADODARA

CLIENT NAME:

RONAK PANCHOLI

DATE:

02-06-2025

NORTH:




DRAWING DETAIL

REVISION NO.	R1	R2	R3
REVISED DATE:	07/02/26		
SCALE:	N.T.S		
DRAWN BY:	ARCHANA		
CHECKED BY:	MITTAL		

	www.mayaspace.studio
	mayaspace.studio@gmail.com
	+918980144077
	@mayaspace.studio



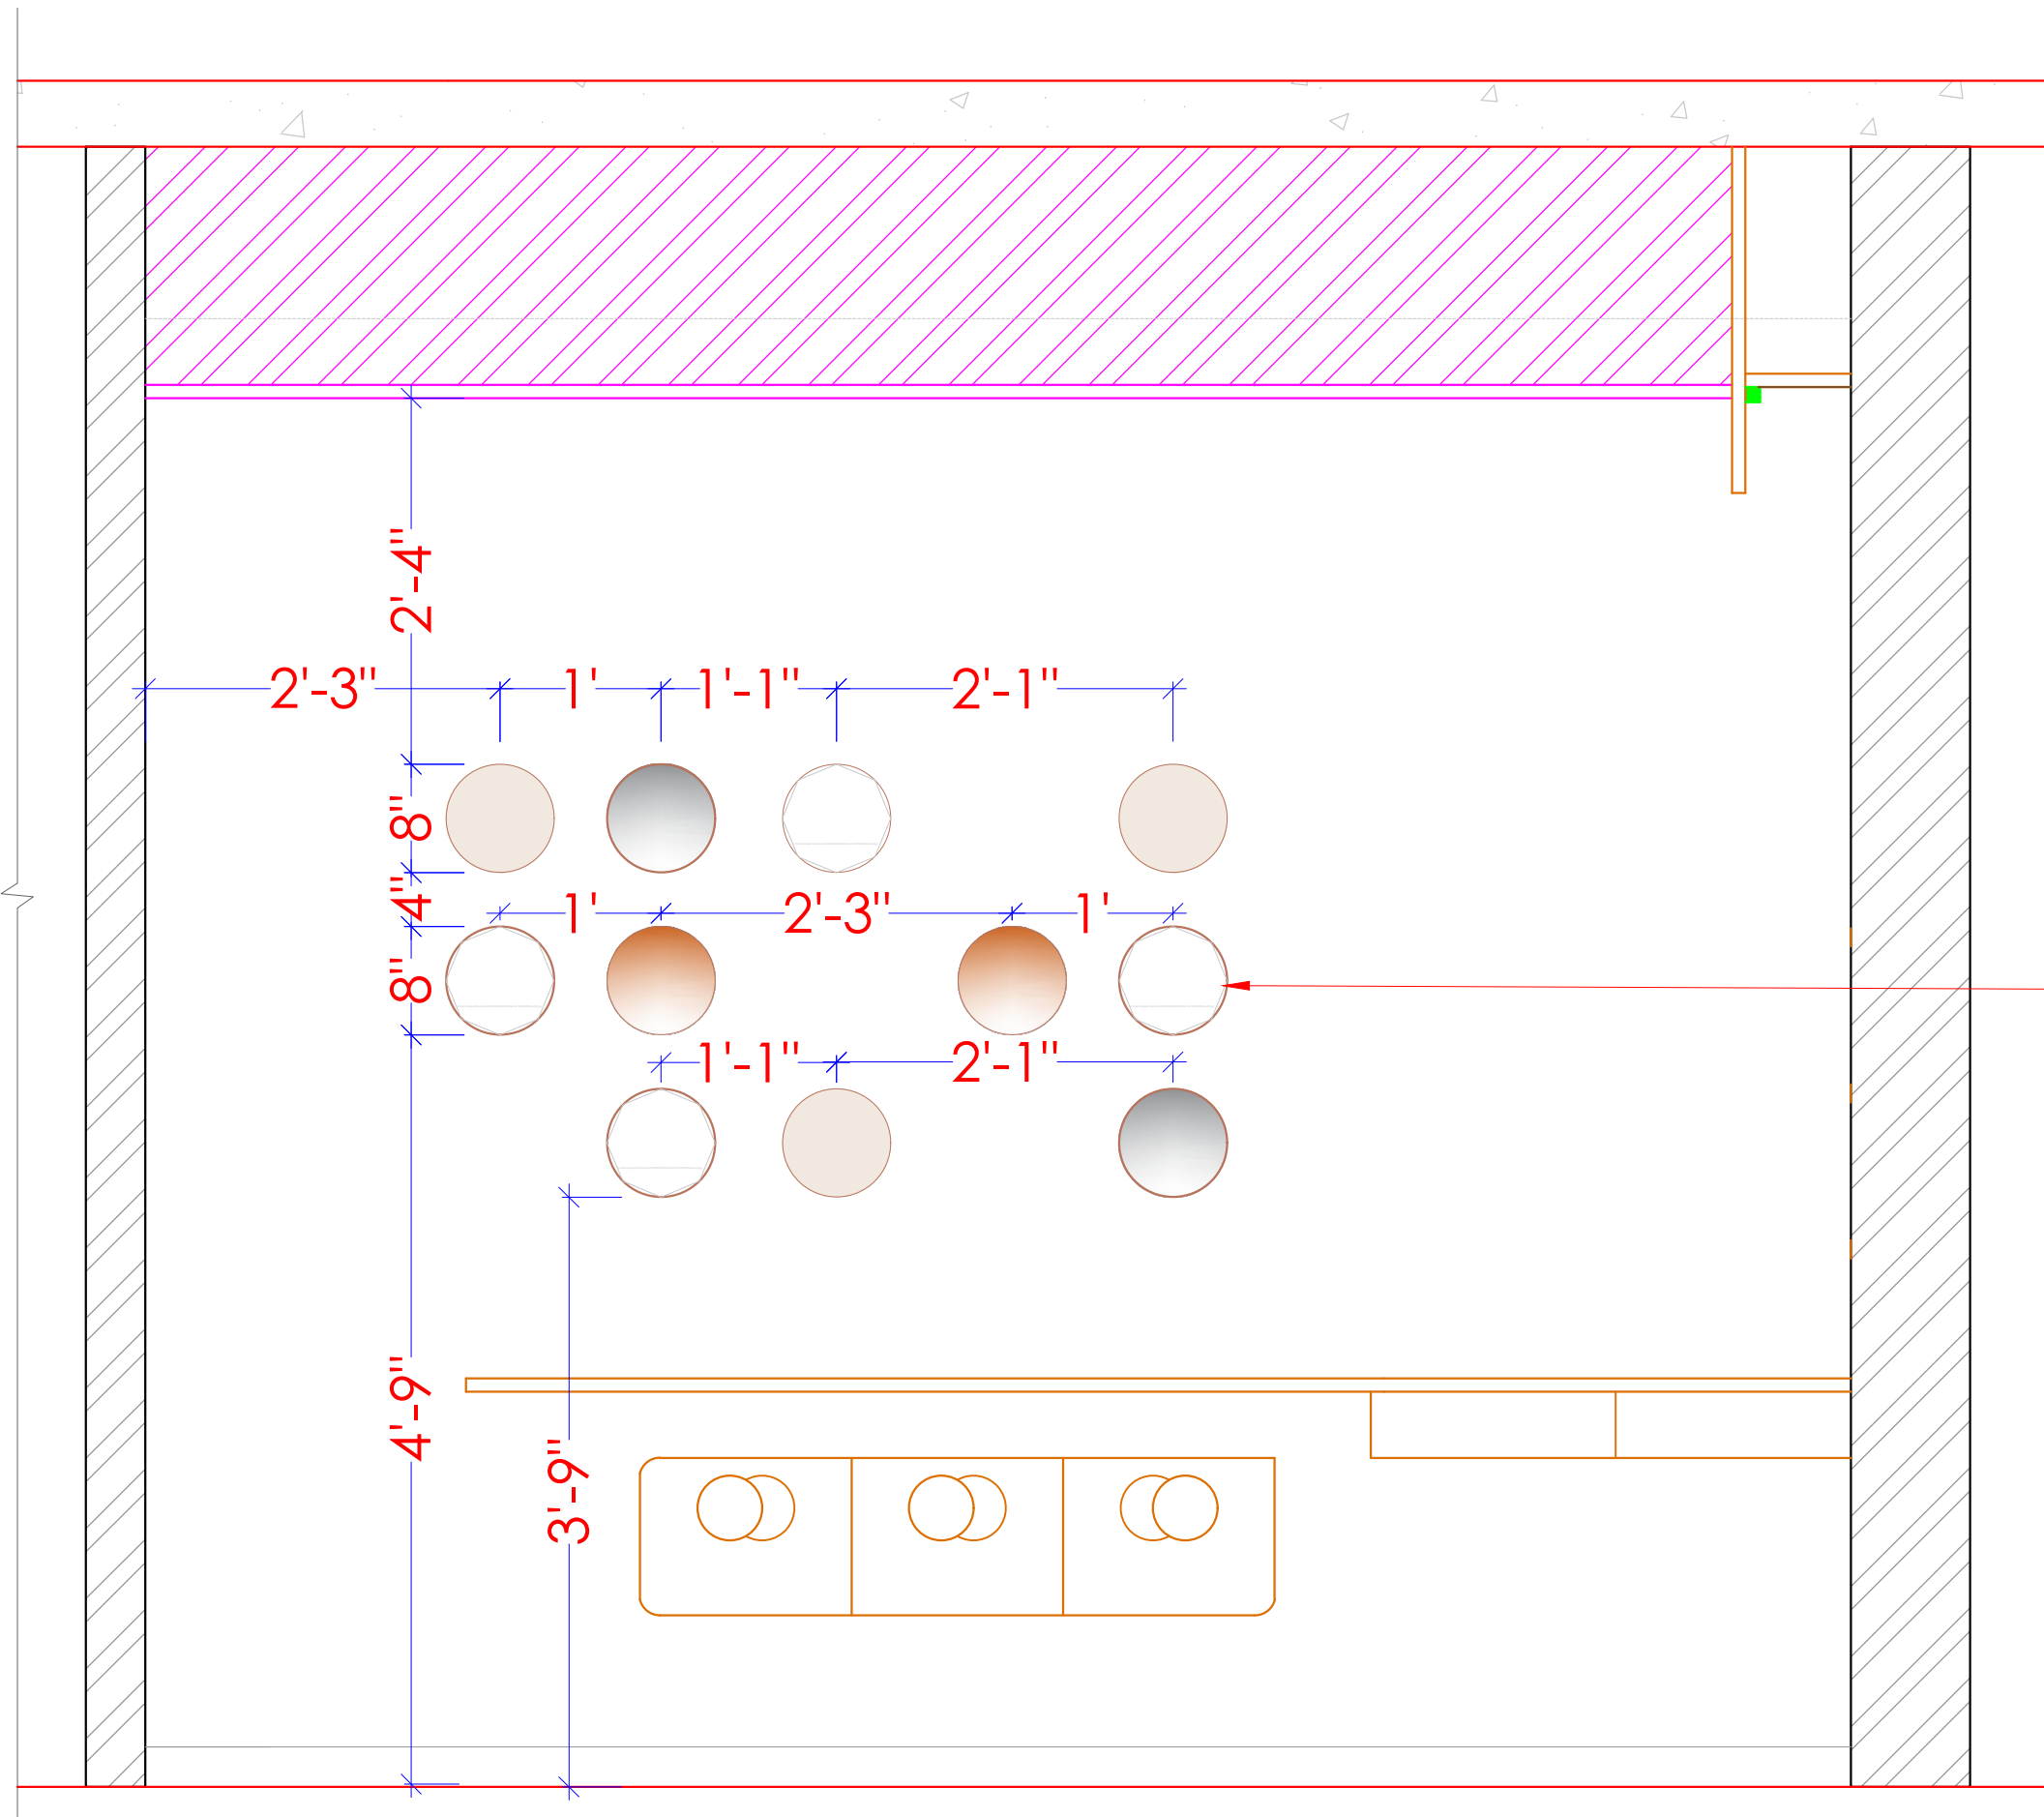

DRAWING TITLE :

PARENTS BEDROOM ARTIFACT WALL

NOTES:

- * DO NOT SCALE THE DRAWING.
- * ALL DIMENSIONS ARE IN FEET \ INCHES.
- * ANY DISCREPANCY IN THE DRAWING TO BE BROUGHT IN THE DESIGNER'S NOTICE BEFORE IMPLEMENTATION ON SITE.

SITE ADDRESS:

SAVAD
VADODARA

CLIENT NAME:

RONAK PANCHOLI

DATE:

02-06-2025


NORTH:

DRAWING DETAIL

REVISION NO.	R1	R2	R3
REVISED DATE:	07/02/26		
SCALE:	N.T.S		
DRAWN BY:	ARCHANA		
CHECKED BY:	MITTAL		

	www.mayaspace.studio
	mayaspace.studio@gmail.com
	+918980144077
	@mayaspace.studio



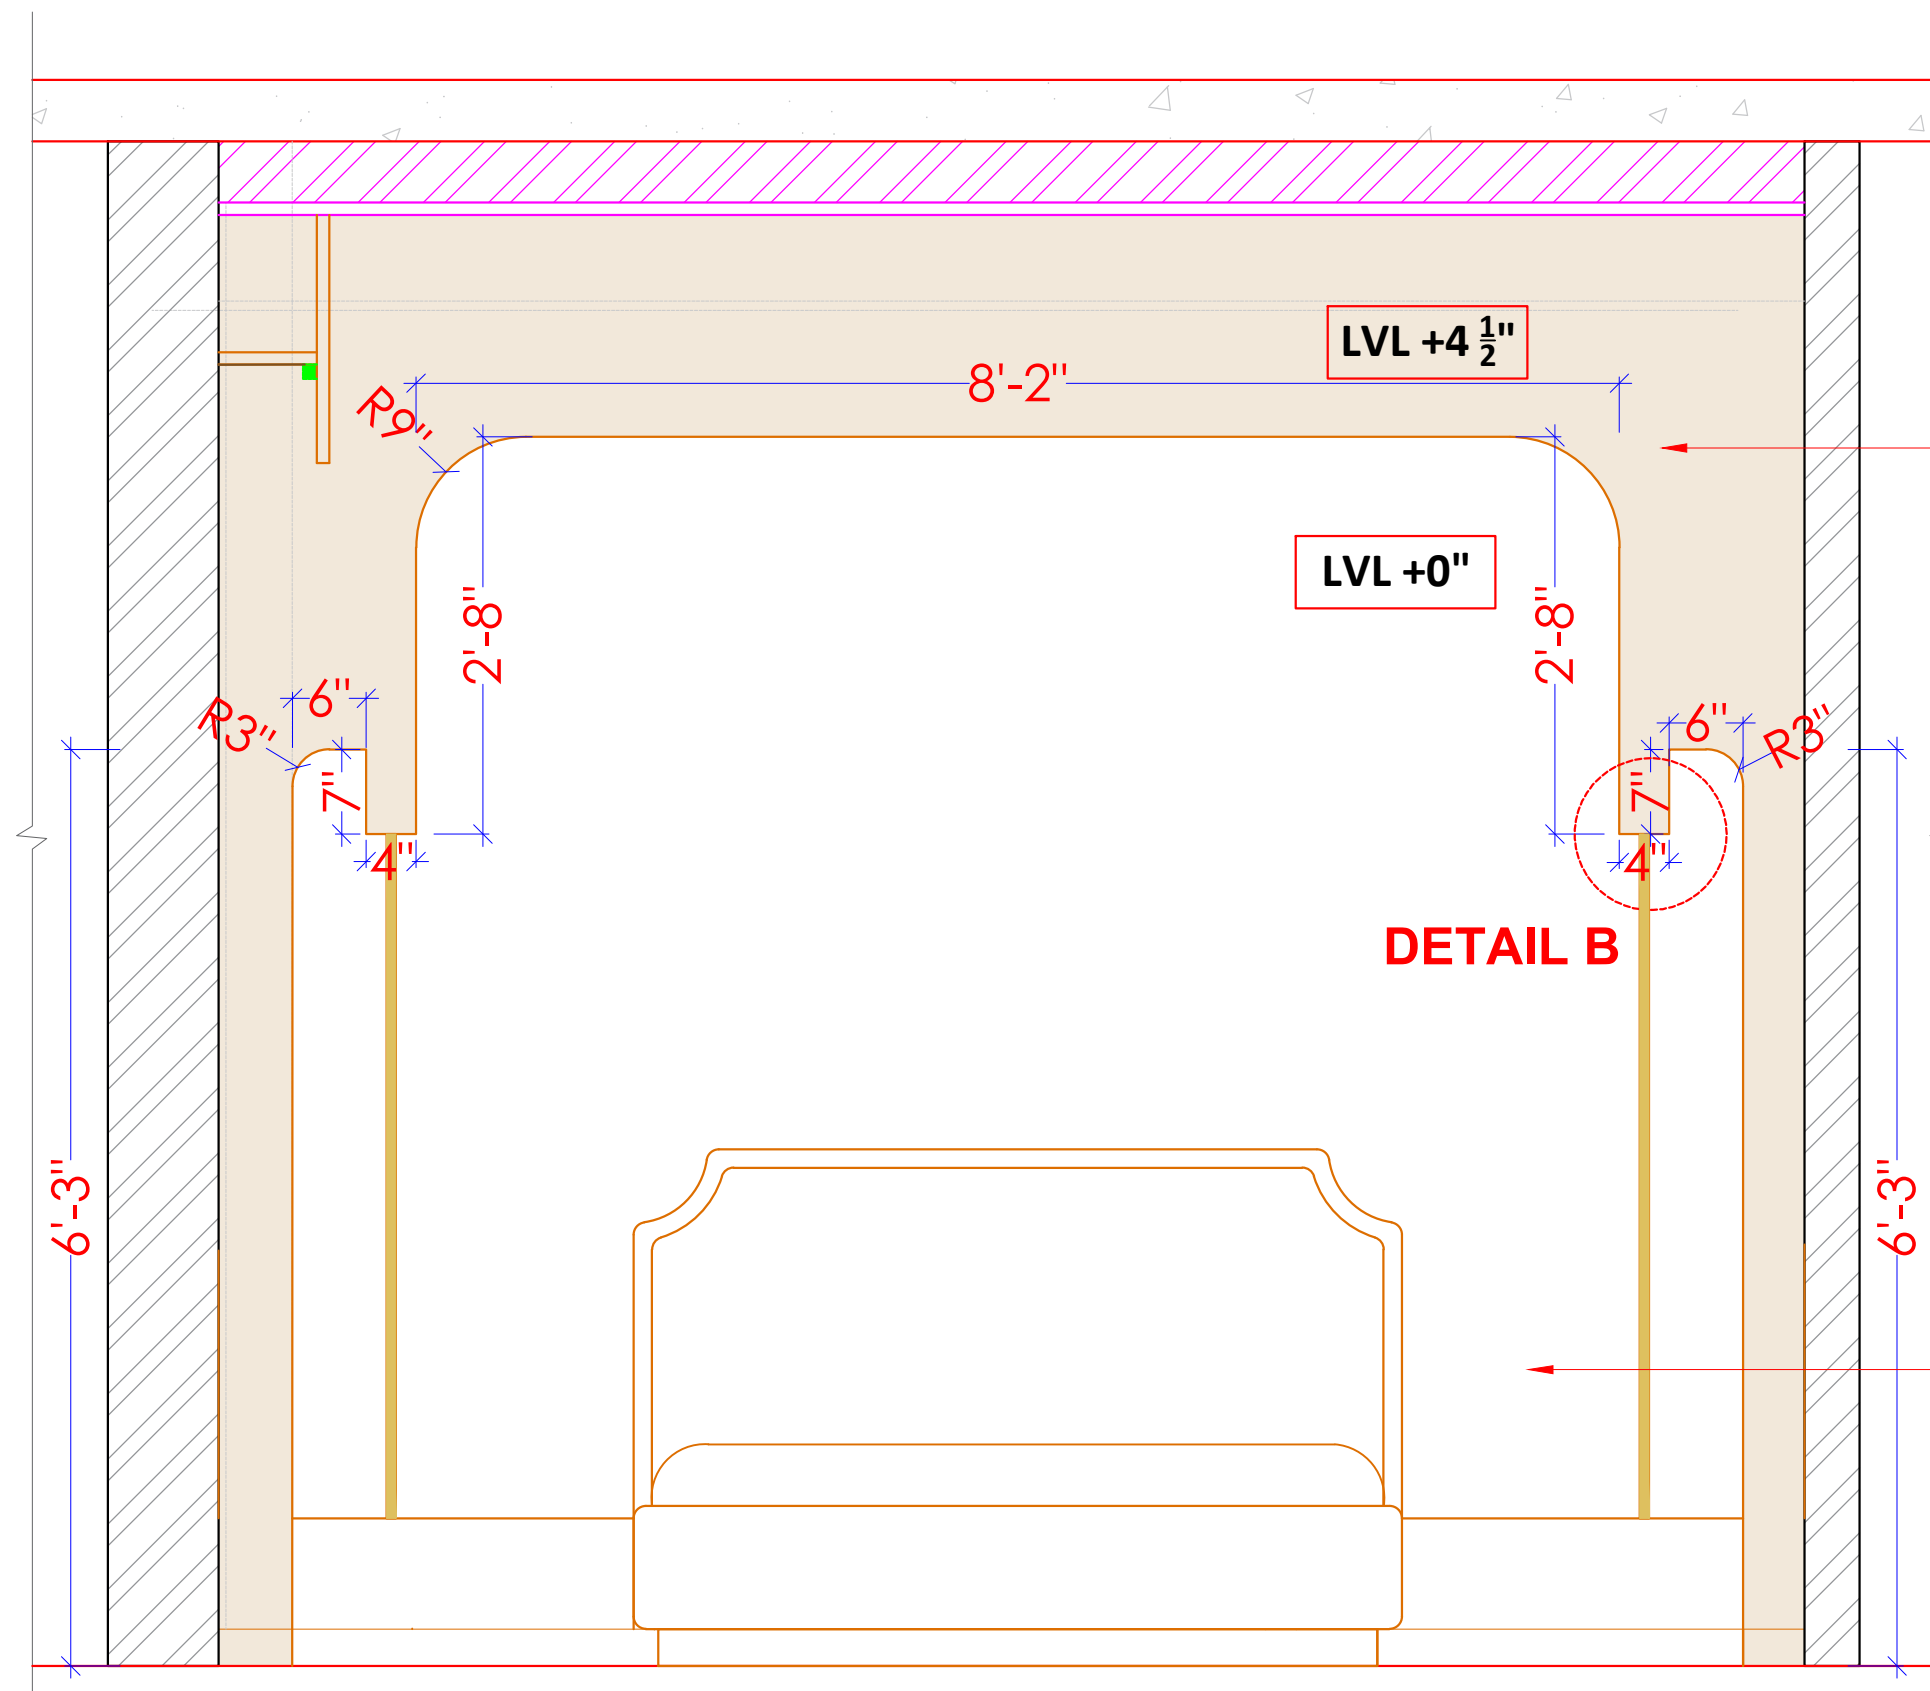

PANELLING DETAIL

DRAWING TITLE :

PARENTS BEDROOM PANELLING DETAIL

NOTES:

- * DO NOT SCALE THE DRAWING.
- * ALL DIMENSIONS ARE IN FEET \ INCHES.
- * ANY DISCREPANCY IN THE DRAWING TO BE BROUGHT IN THE DESIGNER'S NOTICE BEFORE IMPLEMENTATION ON SITE.

SITE ADDRESS:

SAVAD
VADODARA

CLIENT NAME:

RONAK PANCHOLI

DATE:

02-06-2025

NORTH:


DRAWING DETAIL

REVISION NO.	☐ R1	☐ R2	☐ R3
REVISED DATE:	07/02/26		
SCALE:	N.T.S		
DRAWN BY:	ARCHANA		
CHECKED BY:	MITTAL		

	www.mayaspace.studio
	mayaspace.studio@gmail.com
	+918980144077
	@mayaspace.studio



Lvl+4 $\frac{1}{2}$ "
Panelling_
paint finish

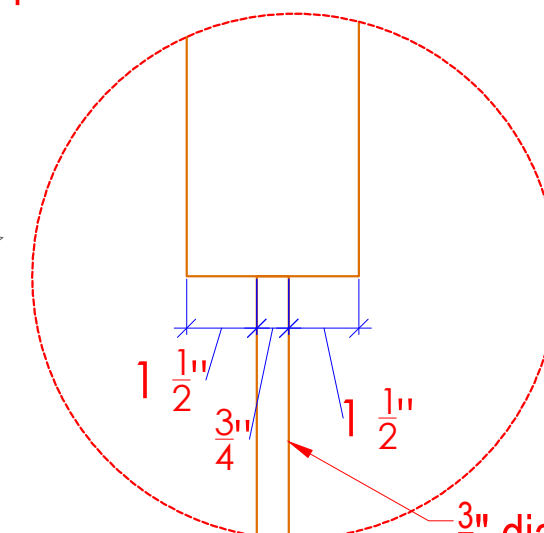

DETAIL B $\frac{3}{4}$ " dia. Brass rod

Texture_
as per
selection