

DRAWING TITLE :

LIVING ROOM
TV UNIT WALL DETAIL

NOTES:

- * DO NOT SCALE THE DRAWING.
- * ALL DIMENSIONS ARE IN FEET \ INCHES.
- * ANY DISCREPANCY IN THE DRAWING TO BE BROUGHT IN THE DESIGNER'S NOTICE BEFORE IMPLEMENTATION ON SITE.

SITE ADDRESS:

SAVAD
VADODARA

CLIENT NAME:

RONAK PANCHOLI


DATE: 02-06-2025

NORTH:

DRAWING DETAIL

REVISION NO.	R1	R2	R3
REVISED DATE:	12/02/26		
SCALE:	N.T.S		
DRAWN BY:	ARCHANA		
CHECKED BY:	MITTAL		

- www.mayaspace.studio
- mayaspace.studio@gmail.com
- +918980144077
- [@mayaspace.studio](#)

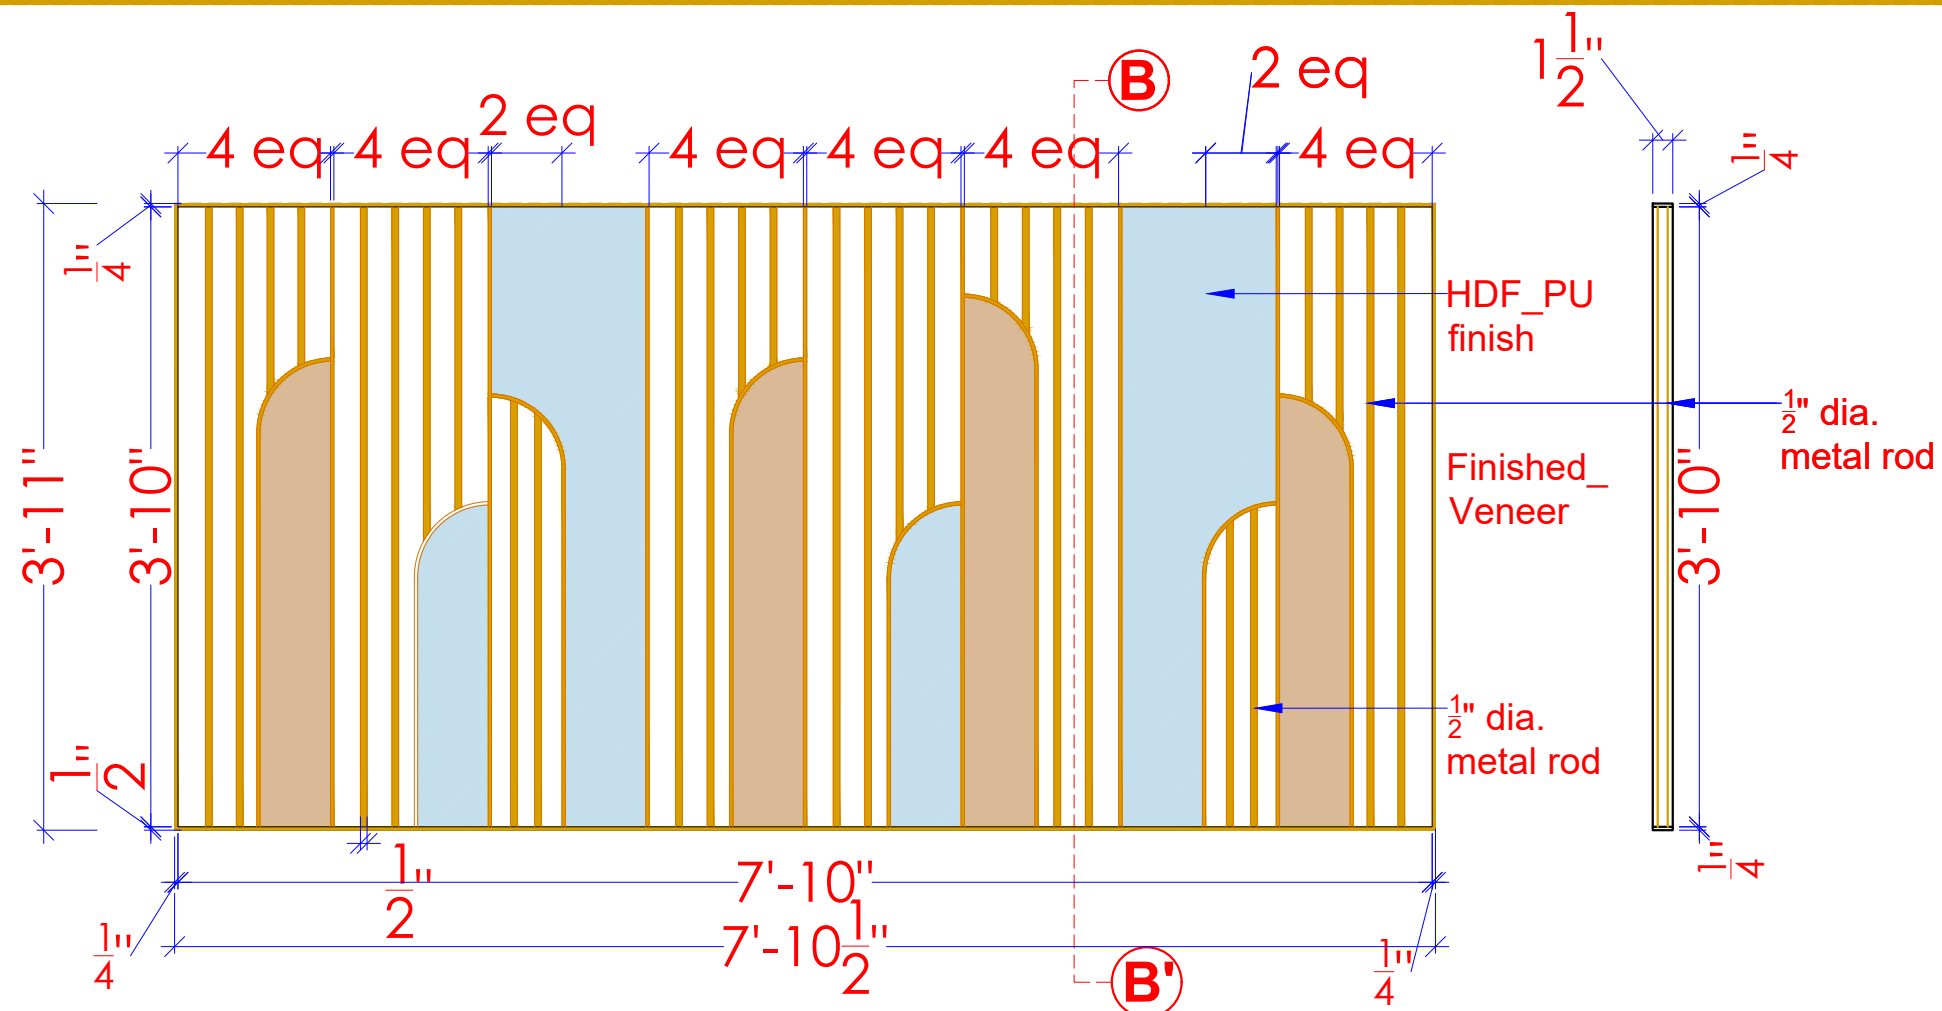

TV WALL ELEVATION

SECTION BB'



TV WALL PLAN

