




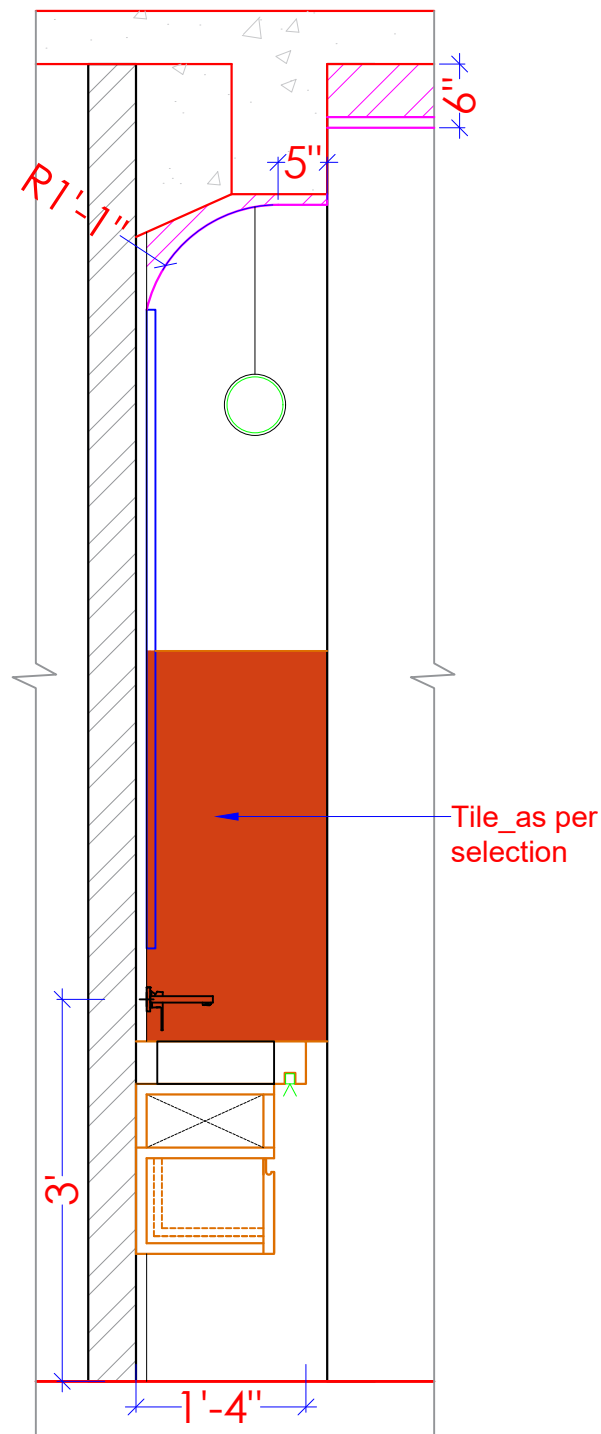


ELEVATION - c

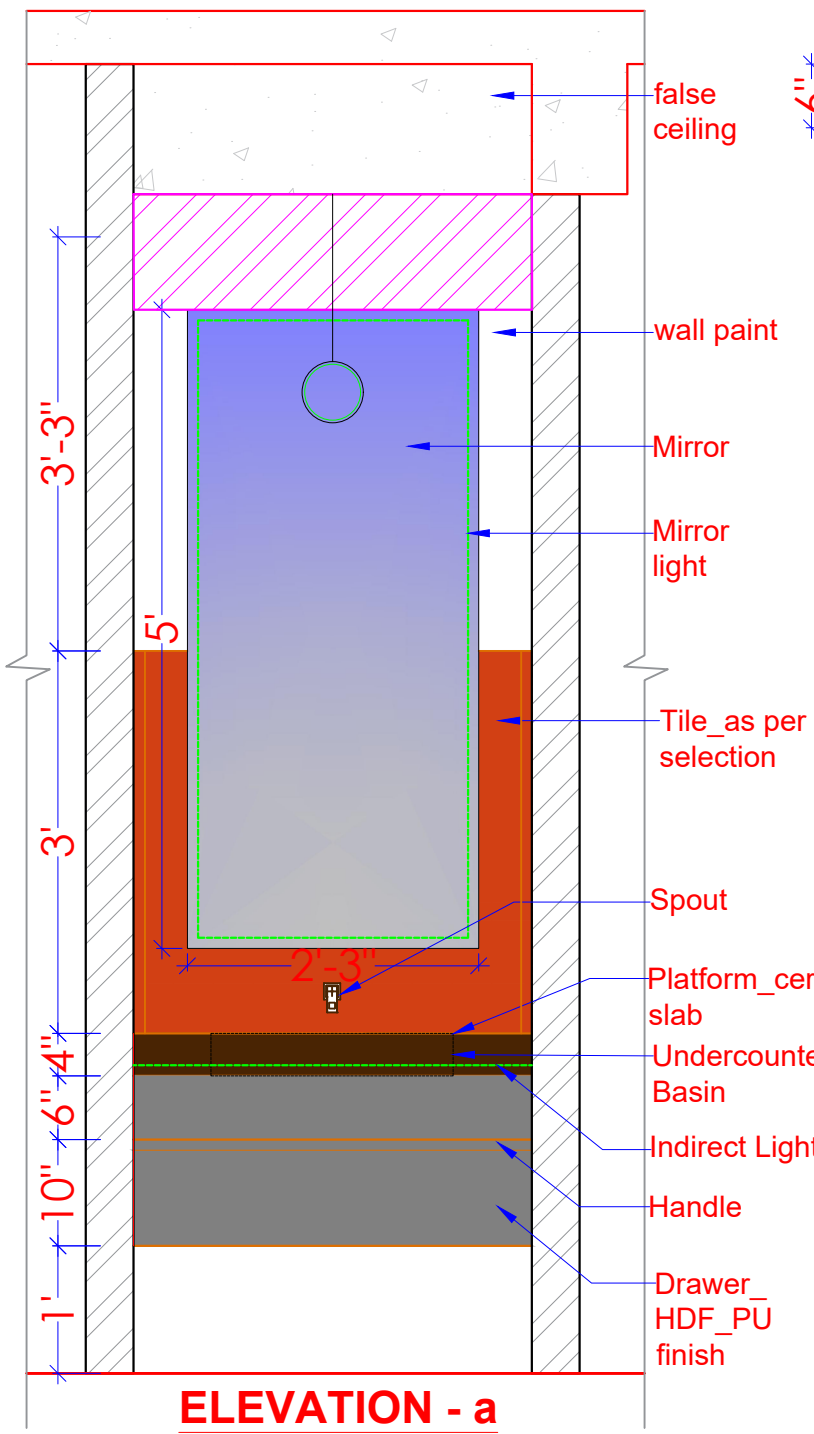


ELEVATION - a

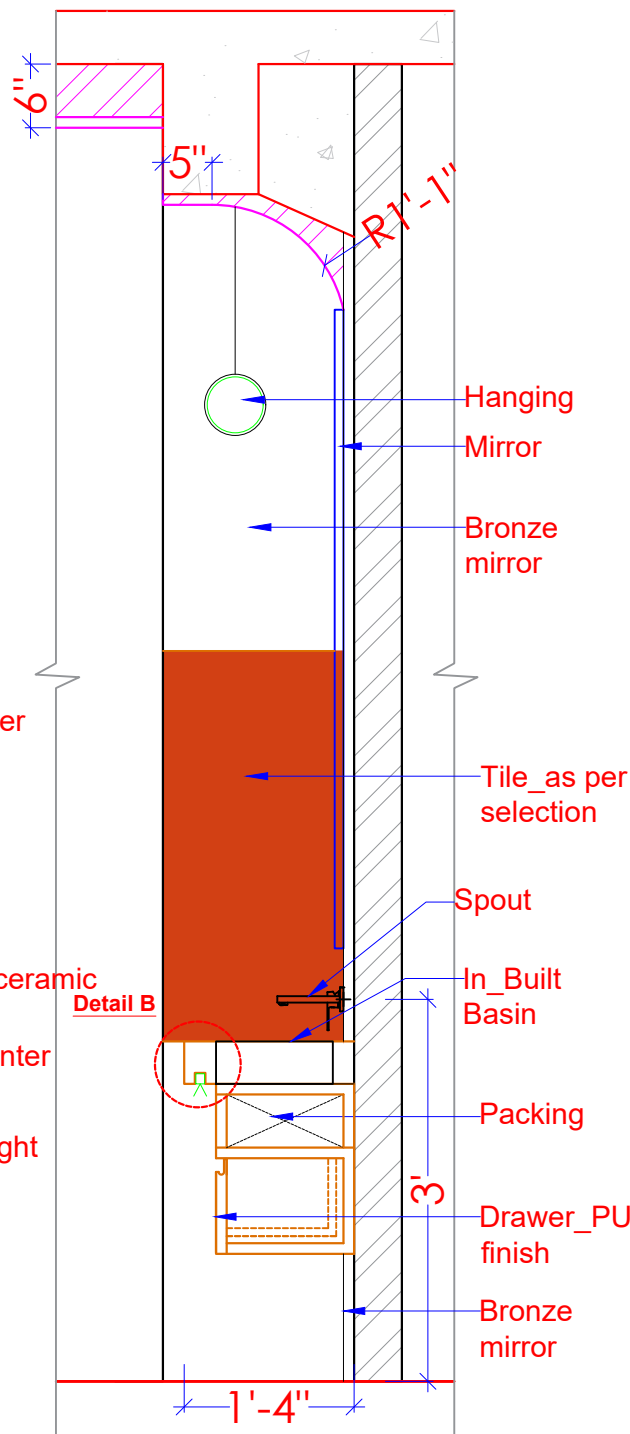

ELEVATION - b

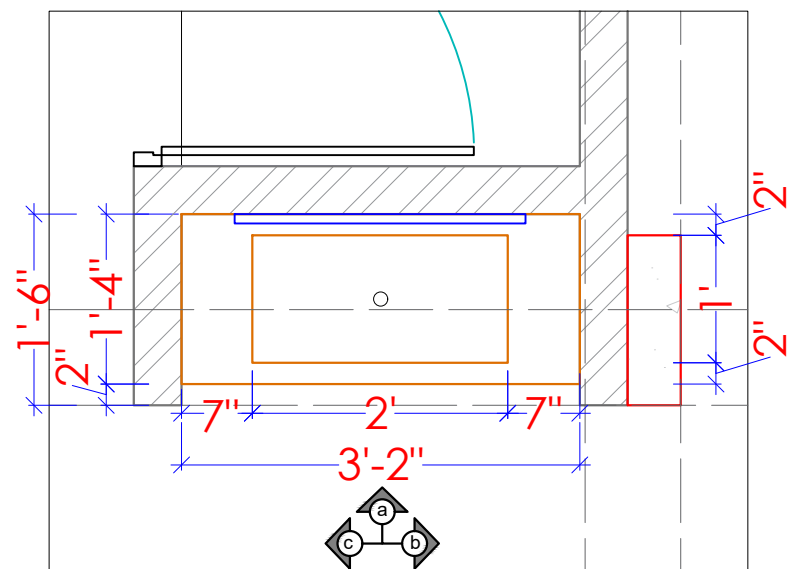

PLAN

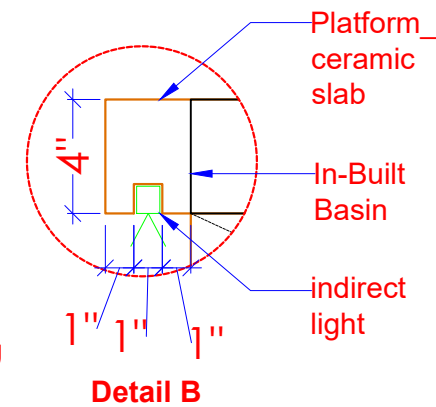

DRAWING TITLE :

LIVING ROOM
BASIN AREA

NOTES:

* DO NOT SCALE THE DRAWING.

* ALL DIMENSIONS ARE IN FEET \ INCHES.

* ANY DISCREPENCY IN THE DRAWING
TO BE BROUGHT IN THE DESIGNER'S
NOTICE BEFORE IMPLEMENTATION
ON SITE.

SITE ADDRESS:

SAVAD
VADODARA

CLIENT NAME:

RONAK PANCHOLI

DATE:

02-06-2025

NORTH:

DRAWING DETAIL

REVISION NO.

R1 R2 R3

REVISED DATE:

12/02/26

SCALE:

N.T.S

DRAWN BY:

ARCHANA

CHECKED BY:

MITTAL

www.mayaspace.studio
mayaspace.studio@gmail.com
+918980144077
@mayaspace.studio

