


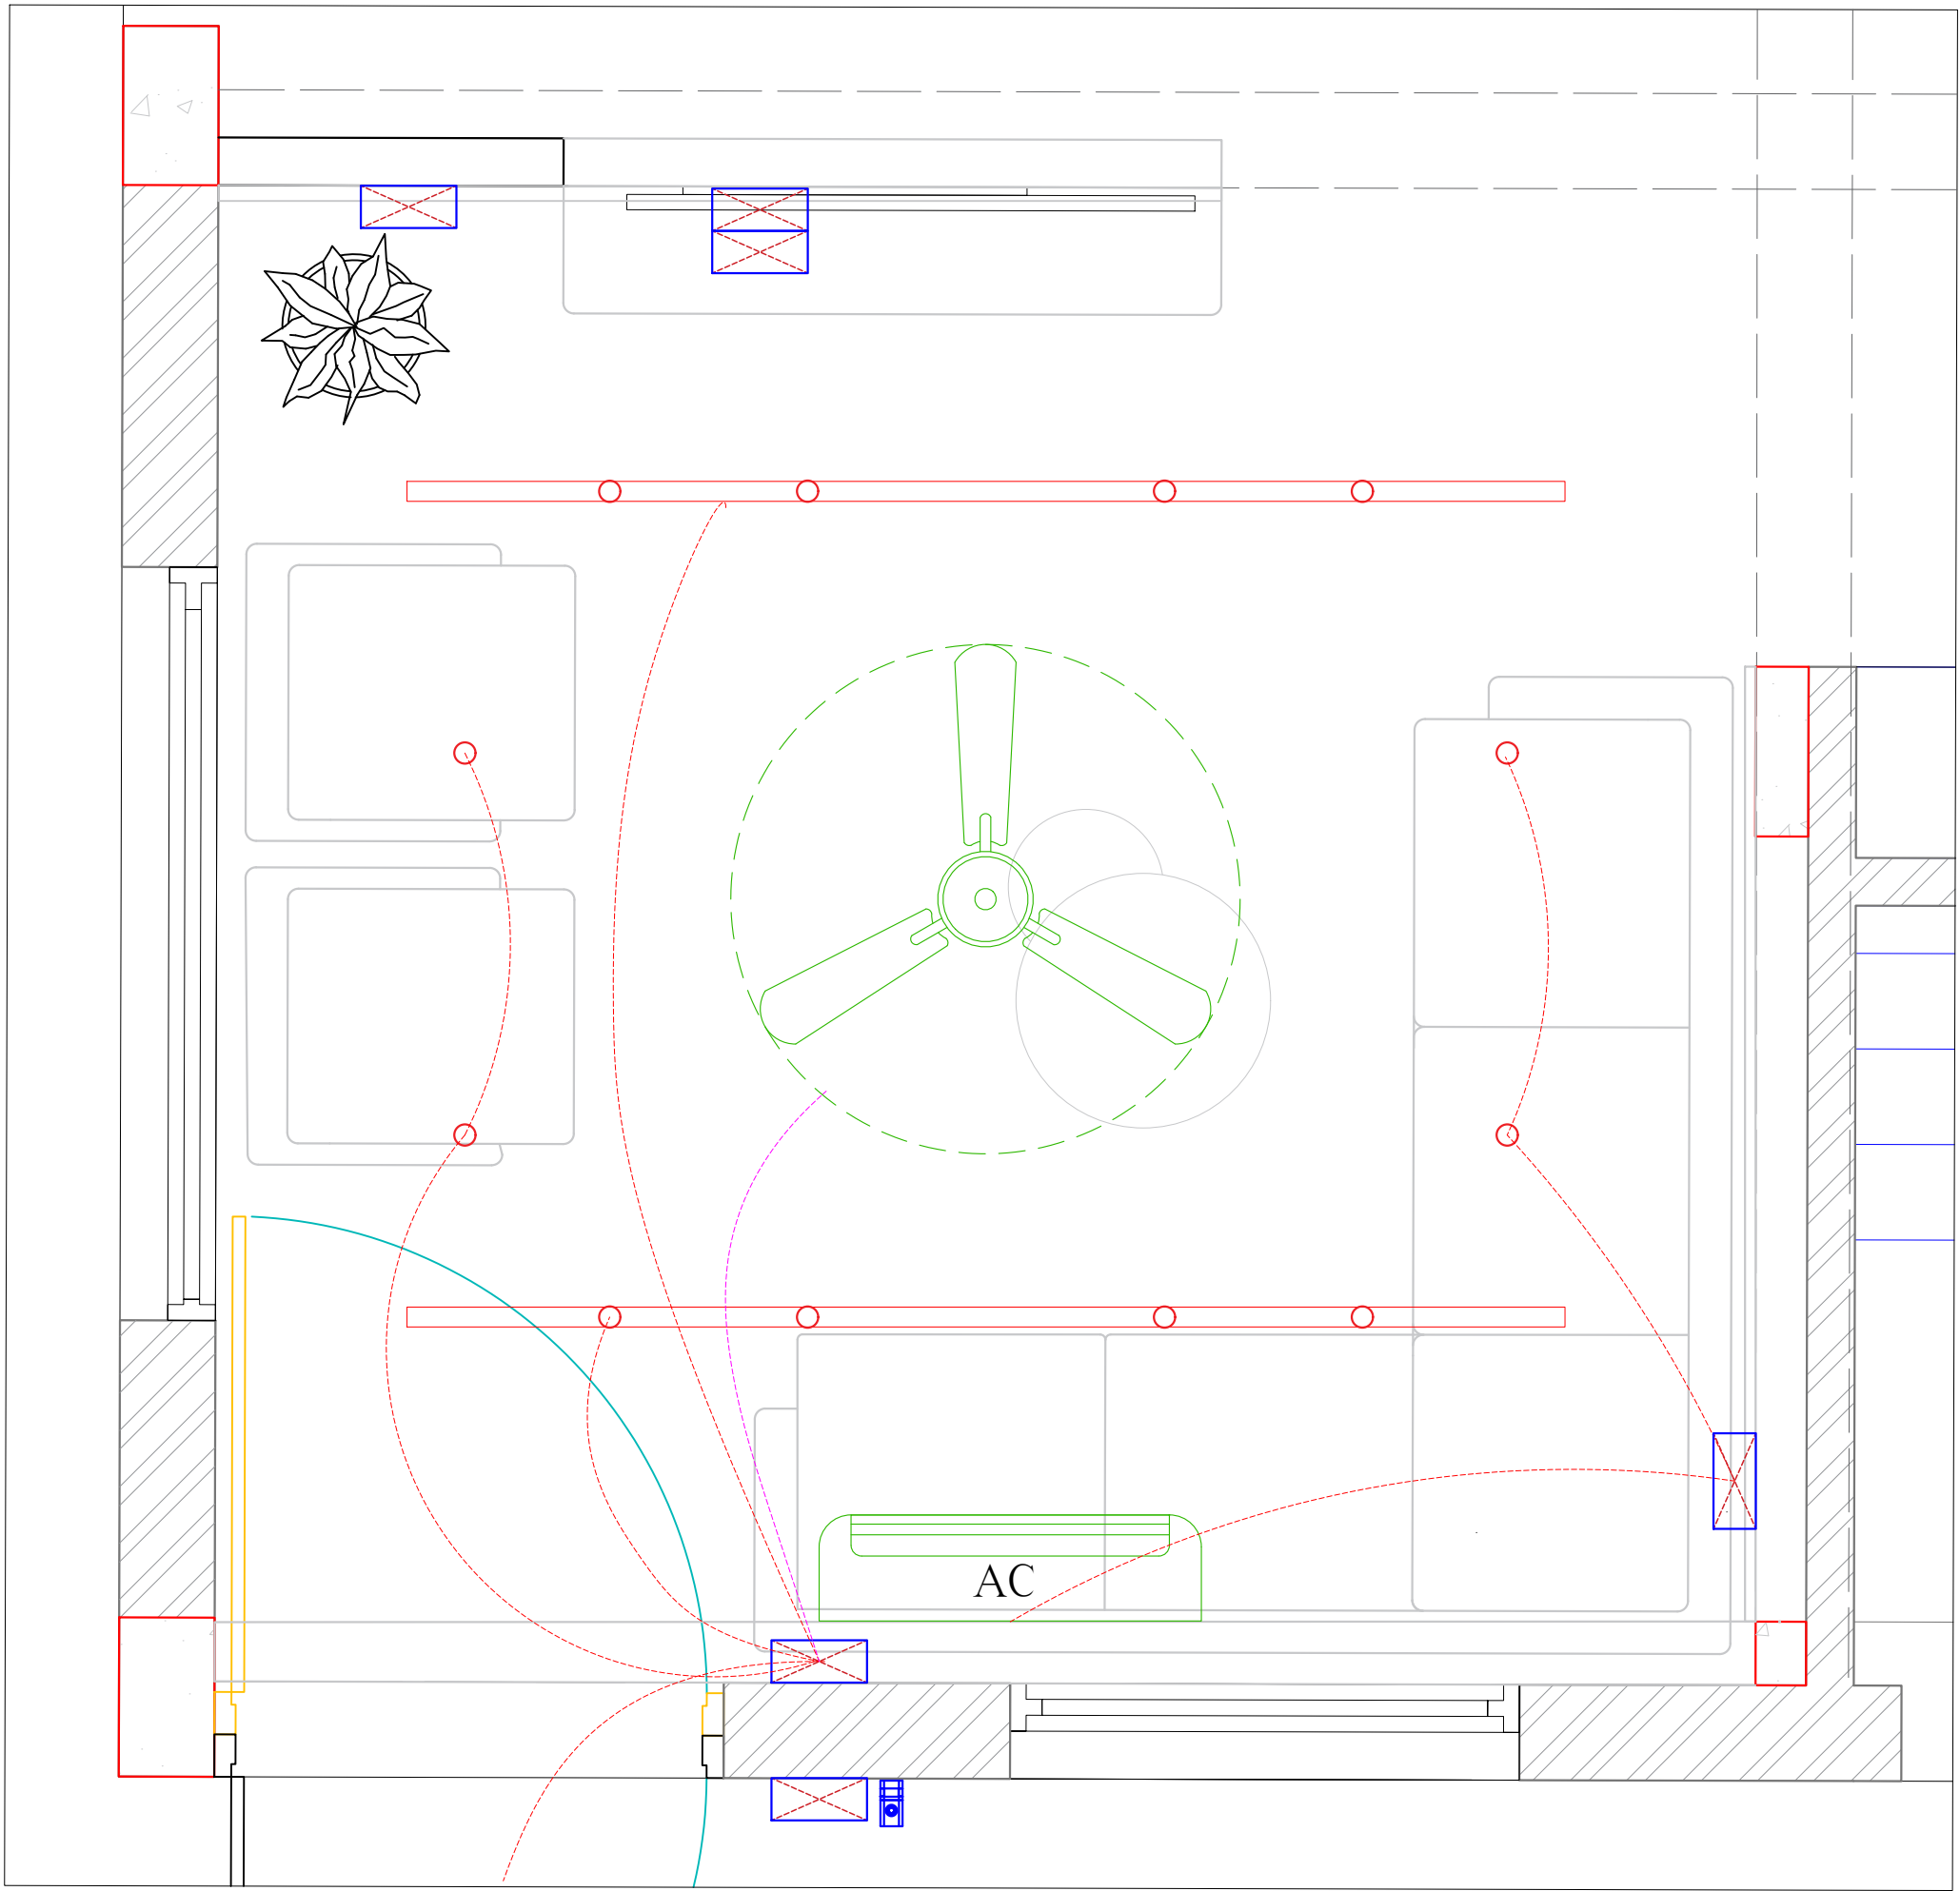

LOOPING LAYOUT

DRAWING TITLE :

LIVING ROOM
LOOPING LAYOUT

NOTES:

- * DO NOT SCALE THE DRAWING.
- * ALL DIMENSIONS ARE IN FEET \ INCHES.
- * ANY DISCREPENCY IN THE DRAWING TO BE BROUGHT IN THE DESIGNER'S NOTICE BEFORE IMPLEMENTATION ON SITE.

SITE ADDRESS:

SAVAD
VADODARA

CLIENT NAME:

RONAK PANCHOLI

DATE: 02-06-2025

NORTH:

DRAWING DETAIL

REVISION NO.	R1	R2	R3
REVISED DATE:	12/02/26		
SCALE:	N.T.S		
DRAWN BY:	ARCHANA		
CHECKED BY:	MITTAL		

	www.mayaspace.studio
	mayaspace.studio@gmail.com
	+918980144077
	@mayaspace.studio

