


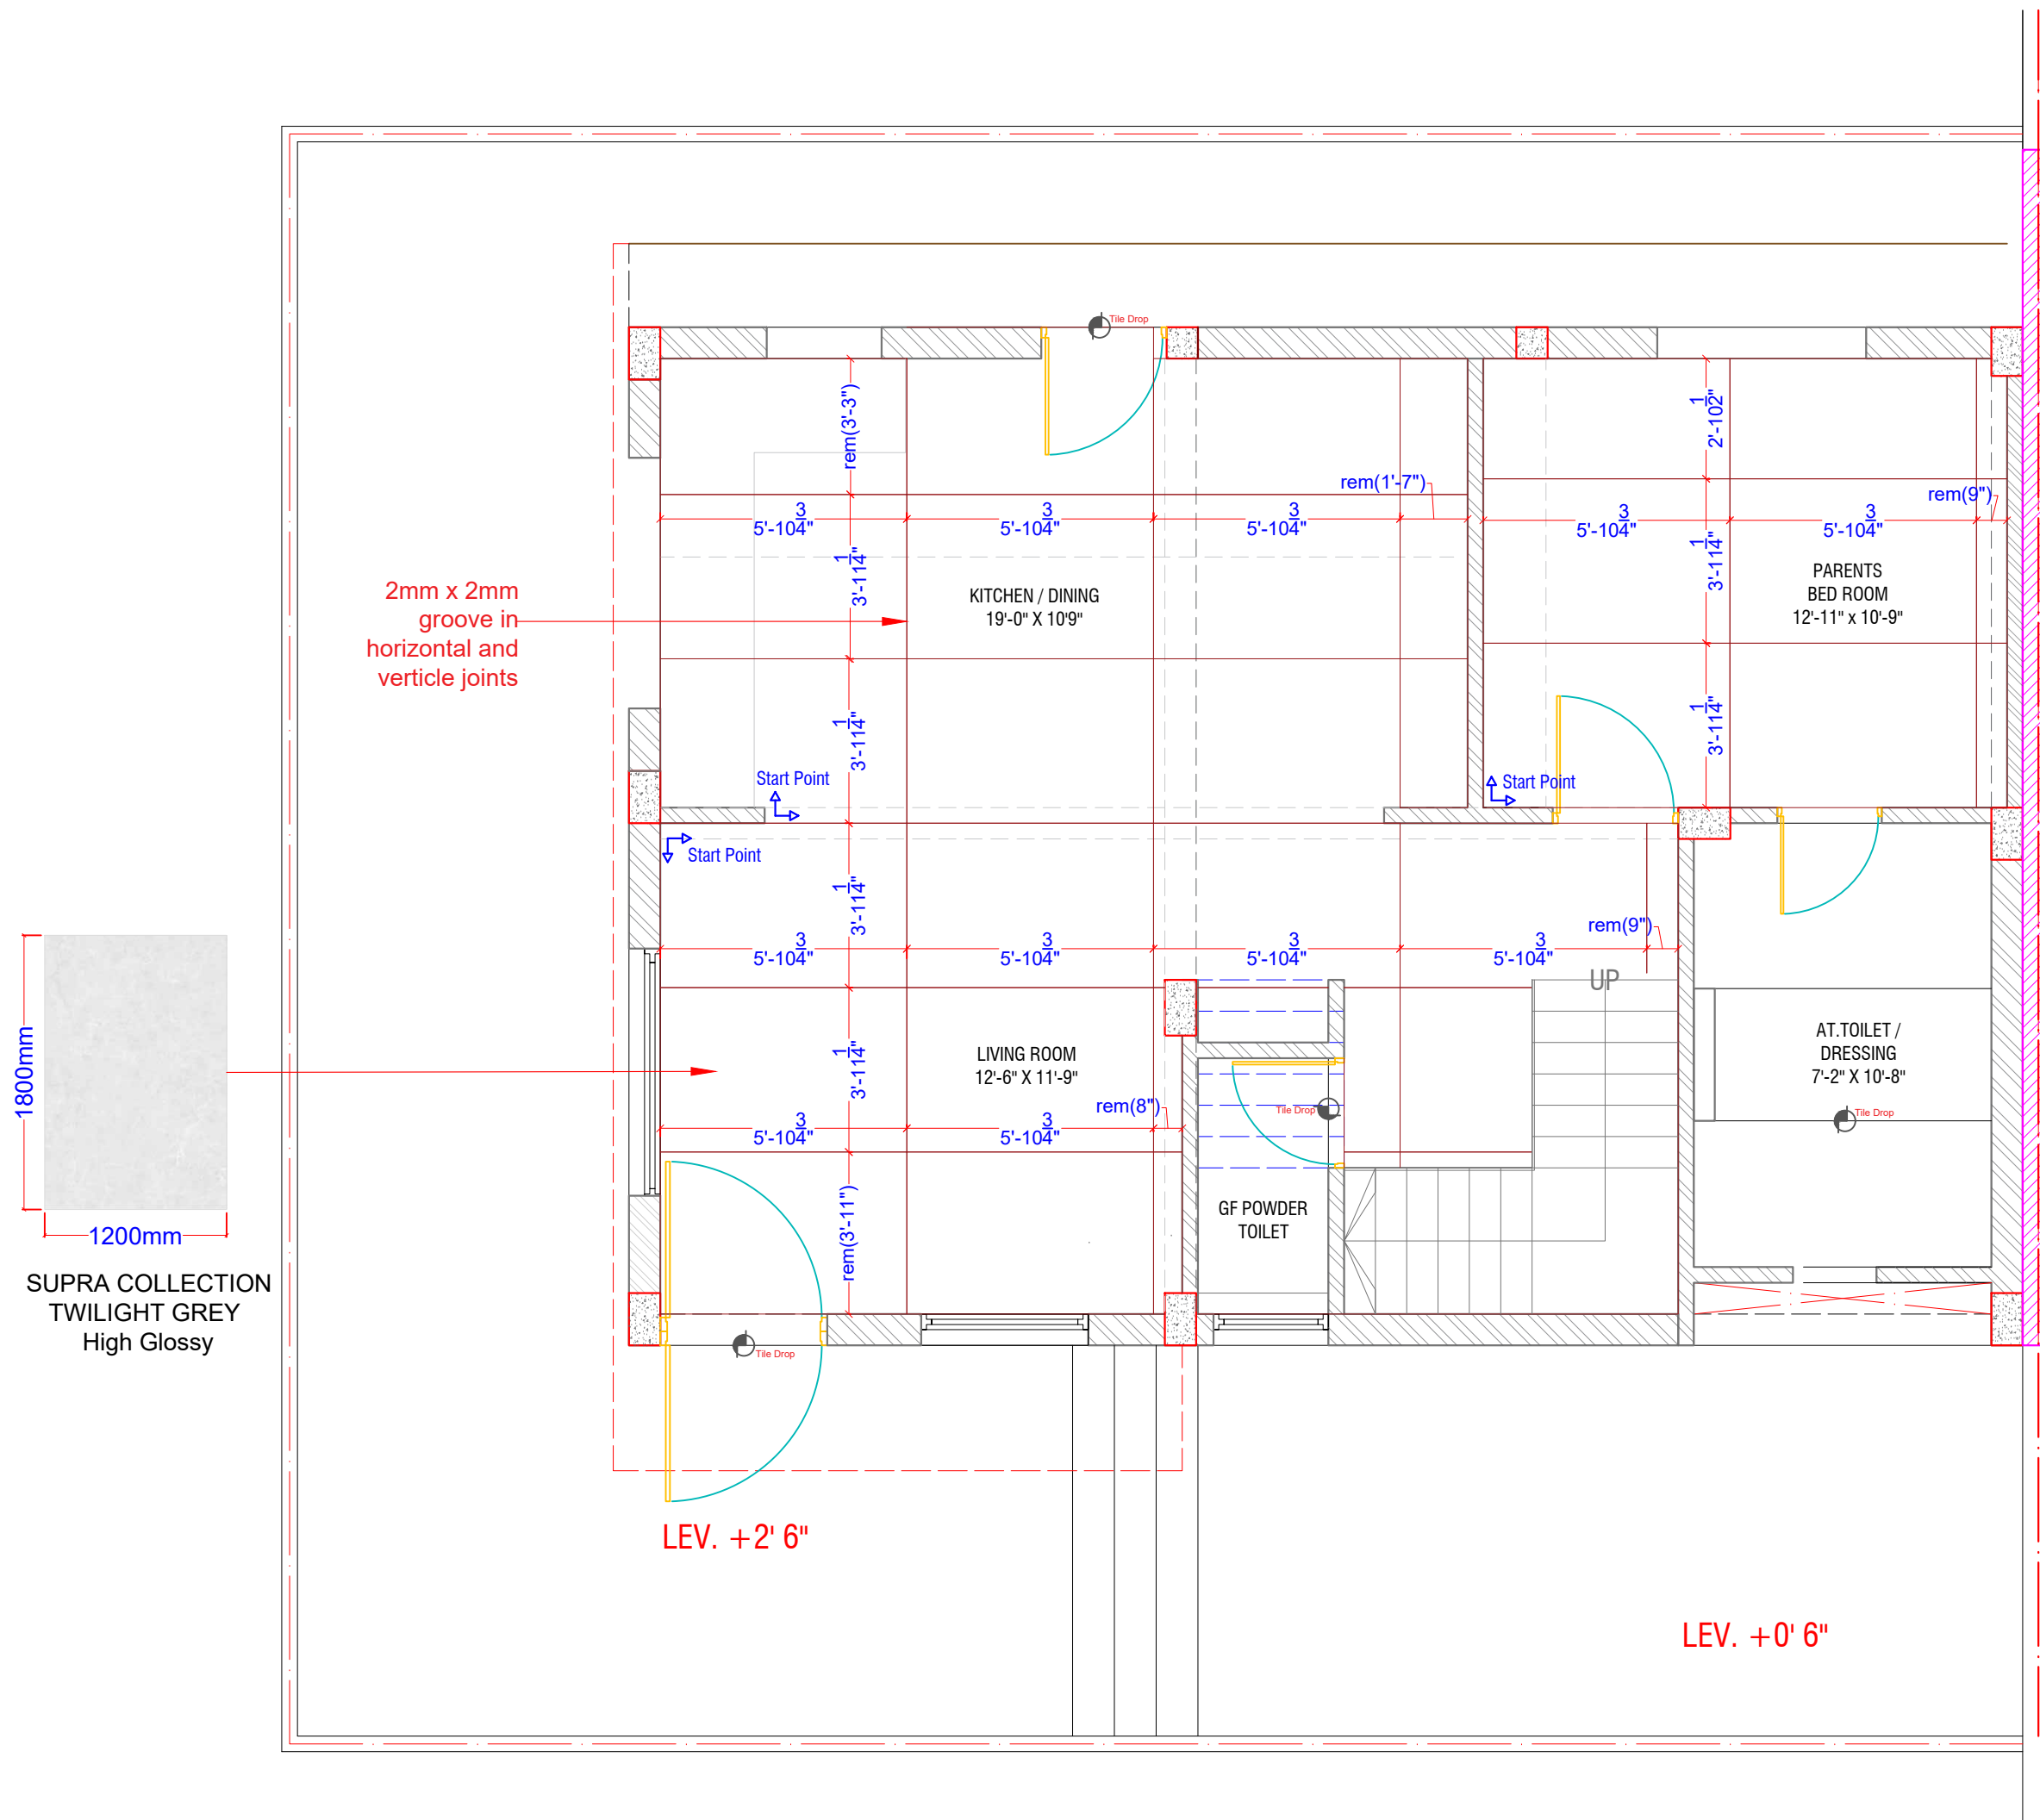

NOTES:

- * DO NOT SCALE THE DRAWING.
- * ALL DIMENSIONS ARE IN FEET \ INCHES.
- * ANY DISCREPANCY IN THE DRAWING TO BE BROUGHT IN THE DESIGNER'S NOTICE BEFORE IMPLEMENTATION ON SITE.

DRAWING TITLE :

GROUND FLOOR
FLOORING LAYOUT

SITE ADDRESS:

SAVAD
VADODARA

CLIENT NAME:

RONAK PANCHOLI

DATE:

02-06-2025

NORTH:




DRAWING DETAIL

REVISION NO.	R1	R2	R3
REVISED DATE:	20-11-2025		
SCALE:	N.T.S		
DRAWN BY:	ARCHANA		
CHECKED BY:	MITTAL		

	www.mayaspace.studio
	mayaspace.studio@gmail.com
	+918980144077
	@mayaspace.studio



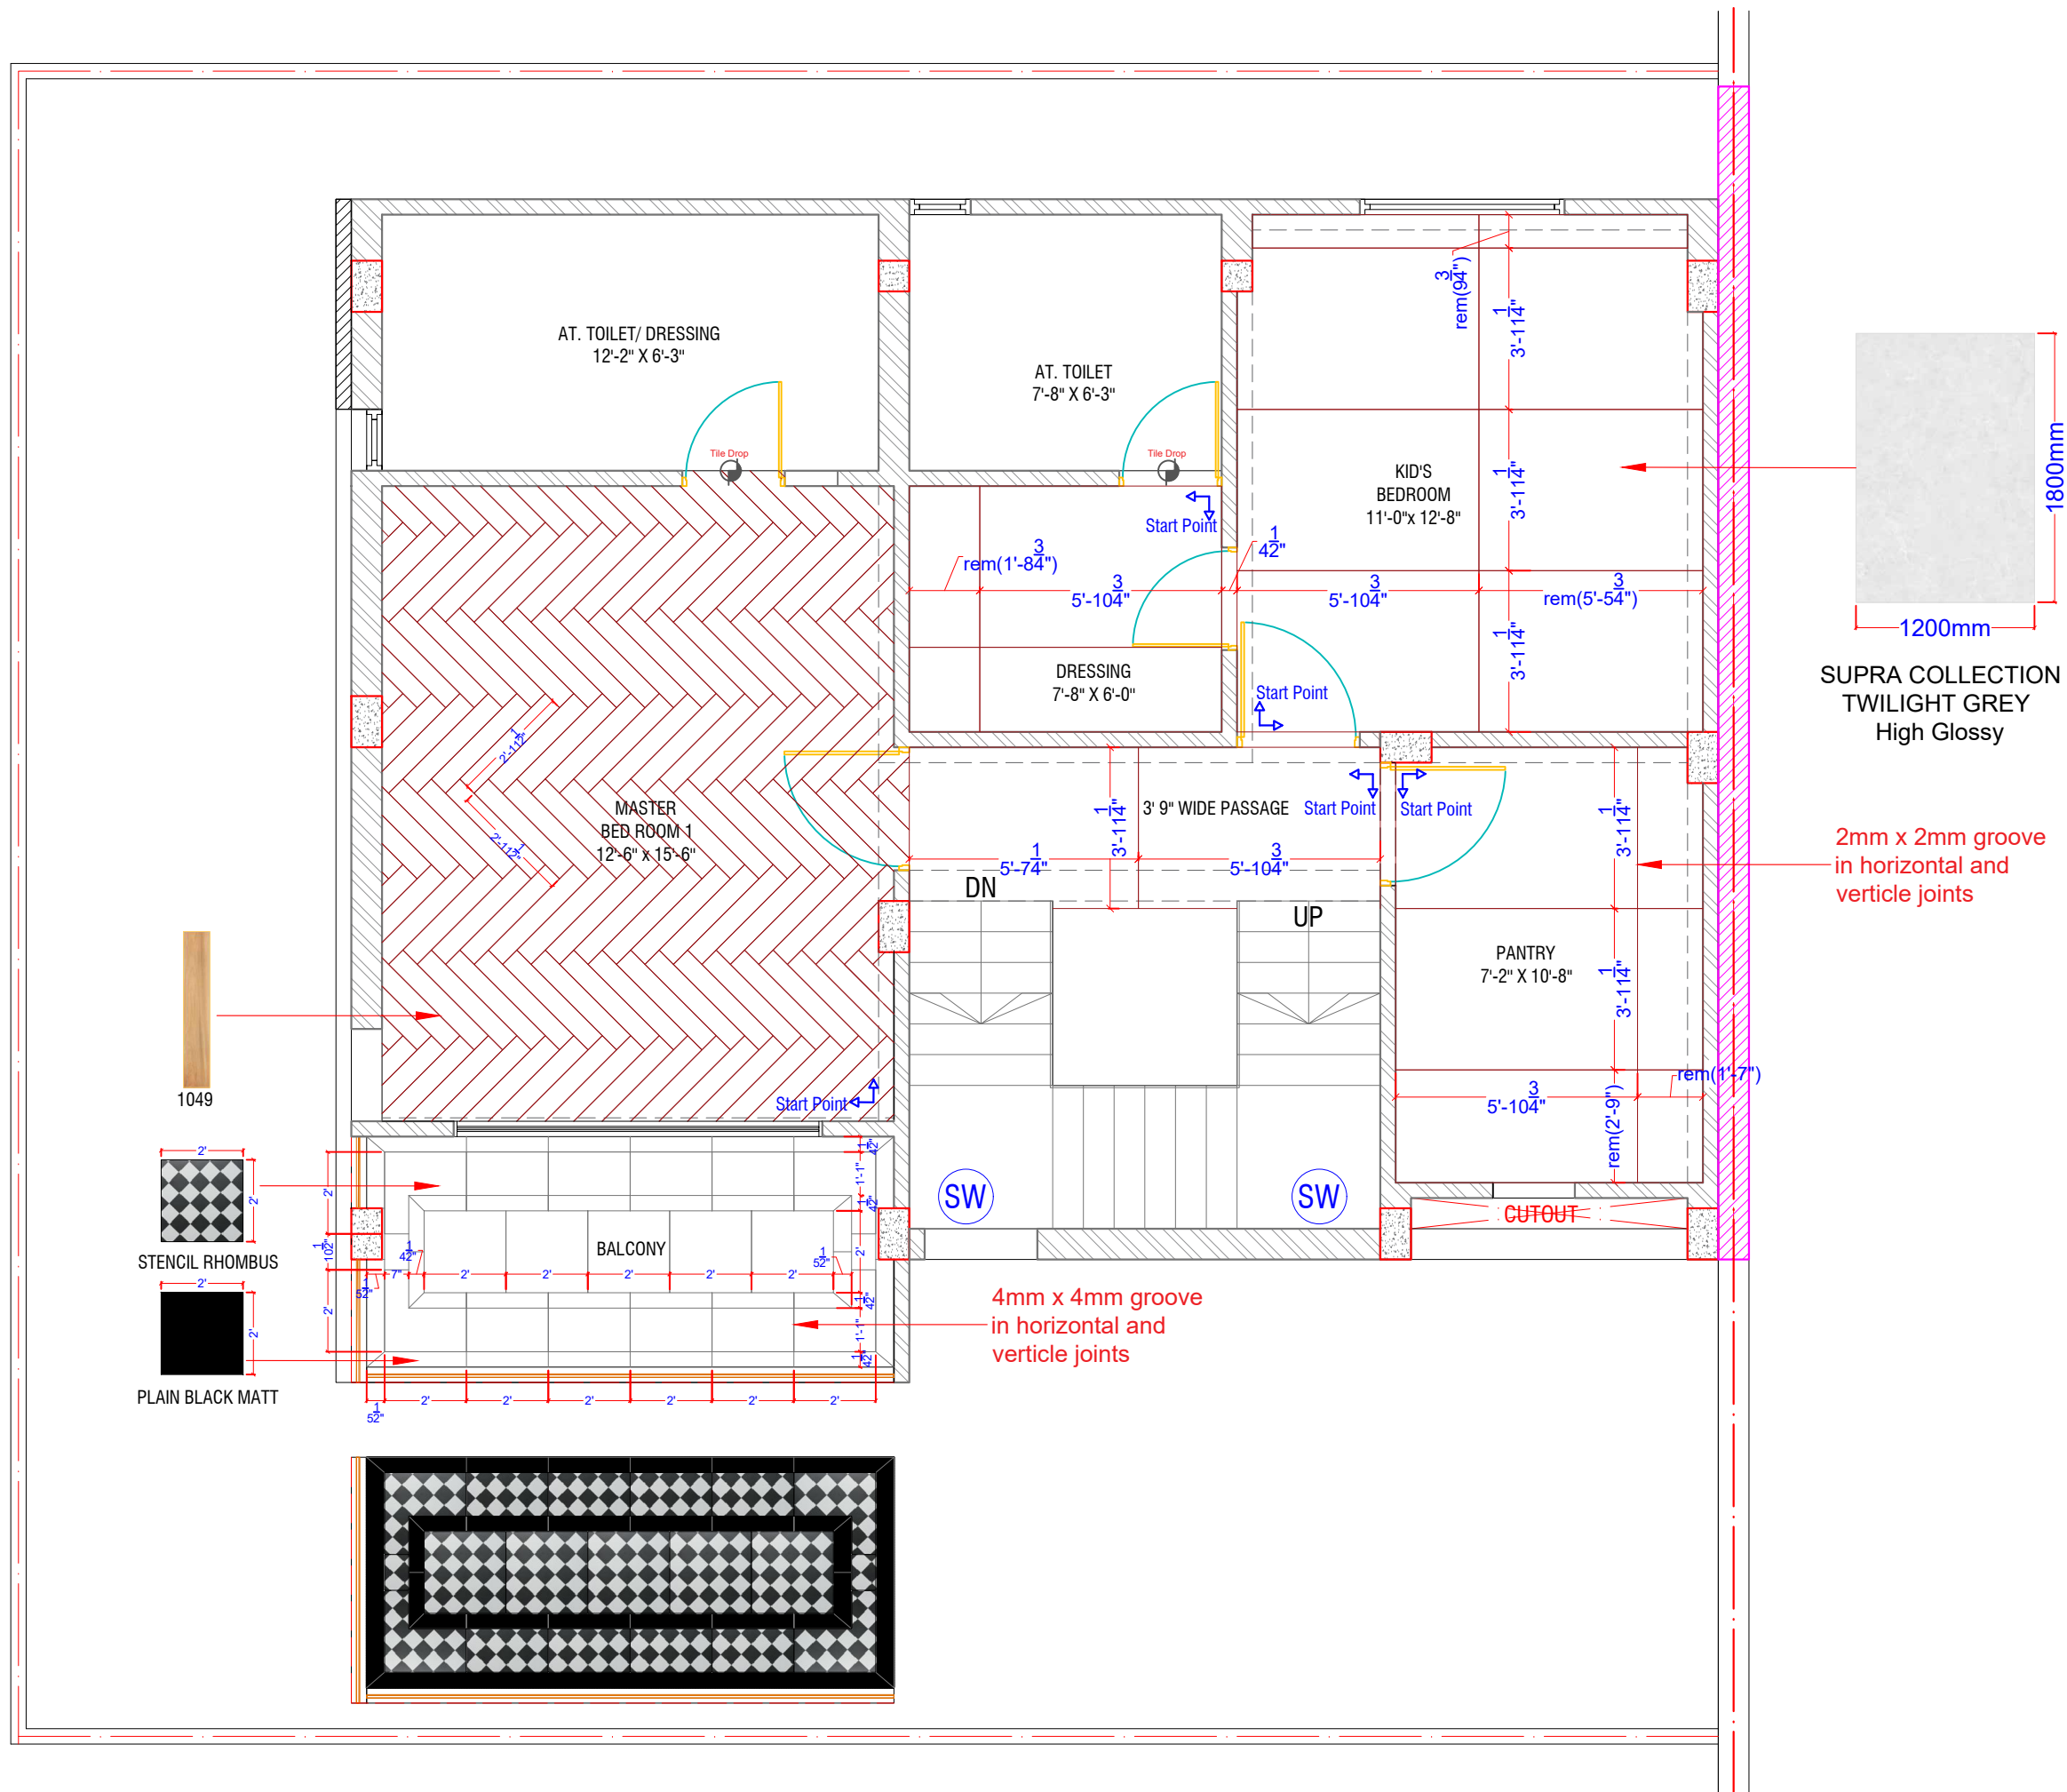

NOTES:

- * DO NOT SCALE THE DRAWING.
- * ALL DIMENSIONS ARE IN FEET \ INCHES.
- * ANY DISCREPENCY IN THE DRAWING TO BE BROUGHT IN THE DESIGNER'S NOTICE BEFORE IMPLEMENTATION ON SITE.

DRAWING TITLE :

FLOORING LAYOUT
FIRST FLOOR

SITE ADDRESS:

SAVAD
VADODARA

CLIENT NAME:

RONAK PANCHOLI

DATE:

02-06-2025

NORTH:




DRAWING DETAIL

REVISION NO.	R1	R2	R3
REVISED DATE:	20-11-2025		
SCALE:	N.T.S		
DRAWN BY:	ARCHANA		
CHECKED BY:	MITTAL		

	www.mayaspace.studio
	mayaspace.studio@gmail.com
	+918980144077
	@mayaspace.studio



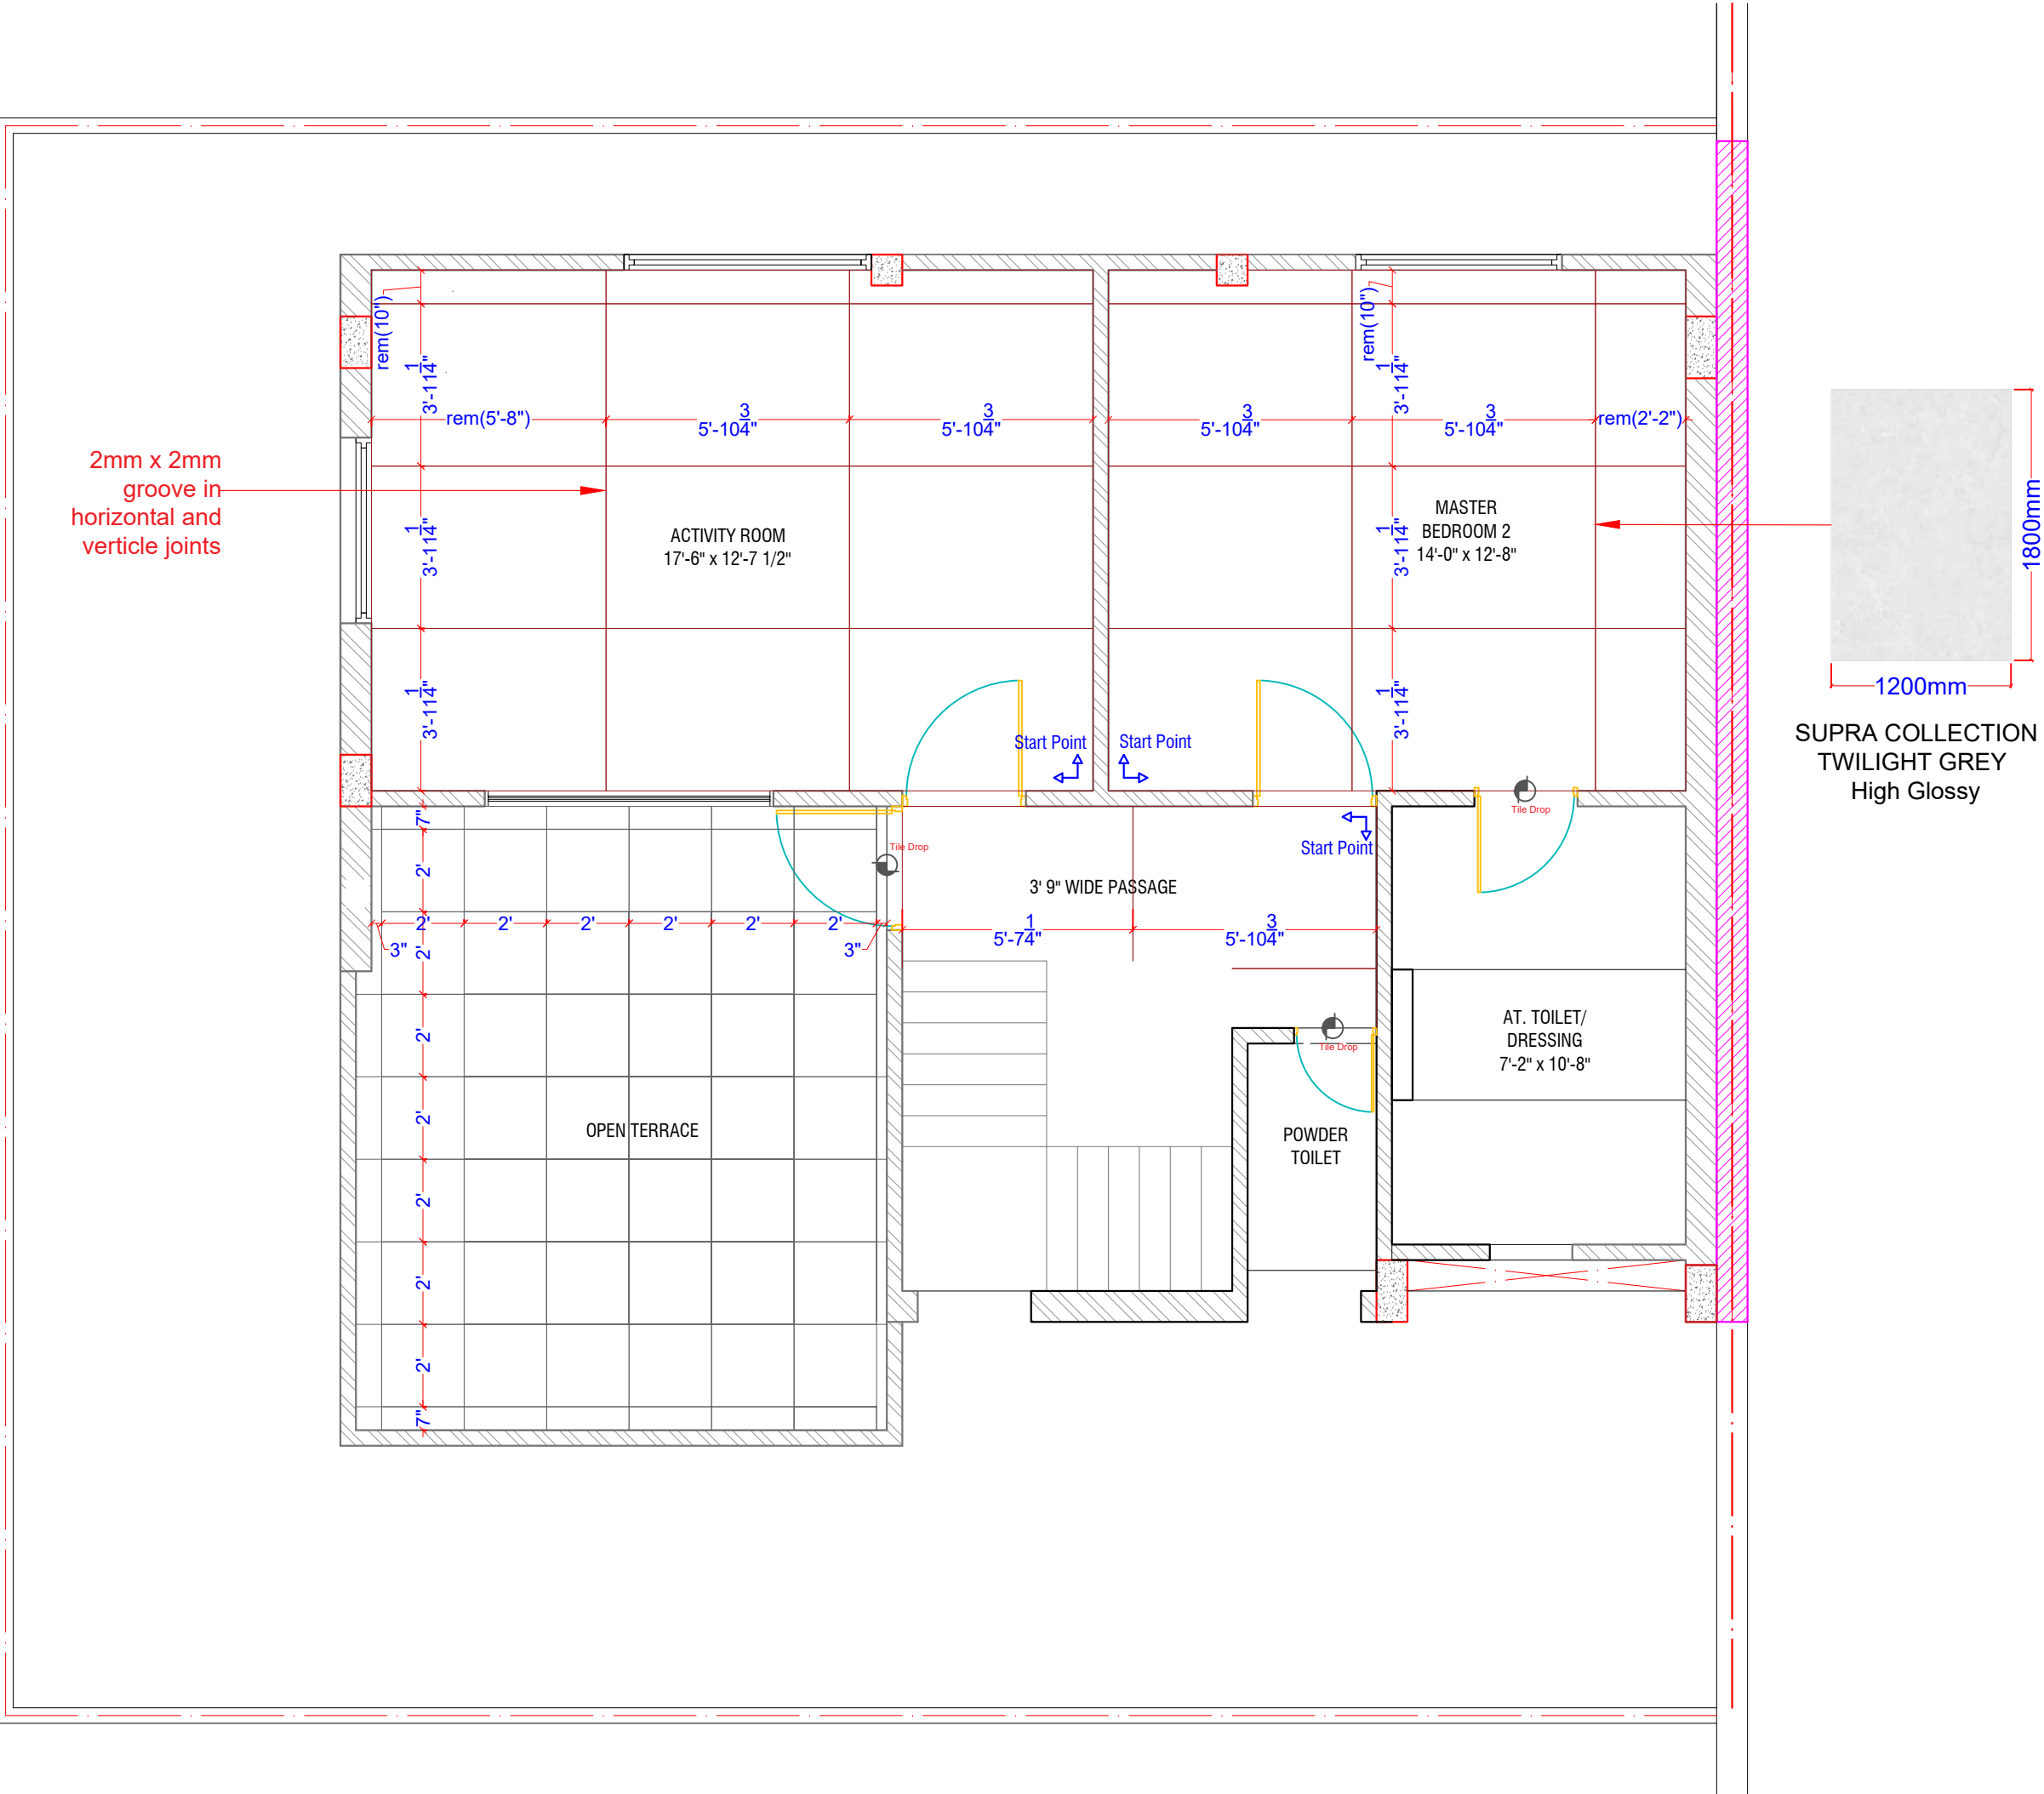

NOTES:

- * DO NOT SCALE THE DRAWING.
- * ALL DIMENSIONS ARE IN FEET \ INCHES.
- * ANY DISCREPENCY IN THE DRAWING TO BE BROUGHT IN THE DESIGNER'S NOTICE BEFORE IMPLEMENTATION ON SITE.

DRAWING TITLE :

FLOORING LAYOUT
SECOND FLOOR

SITE ADDRESS:

SAVAD
VADODARA

CLIENT NAME:

RONAK PANCHOLI



DATE:	02-06-2025
NORTH:	

DRAWING DETAIL


REVISION NO.	R1 R2 R3
REVISED DATE:	20-11-2025
SCALE:	N.T.S
DRAWN BY:	ARCHANA
CHECKED BY:	MITTAL

	www.mayaspace.studio
	mayaspace.studio@gmail.com
	+918980144077
	@mayaspace.studio




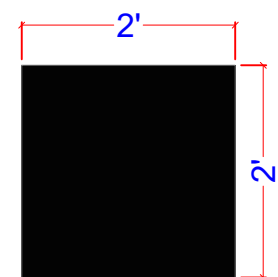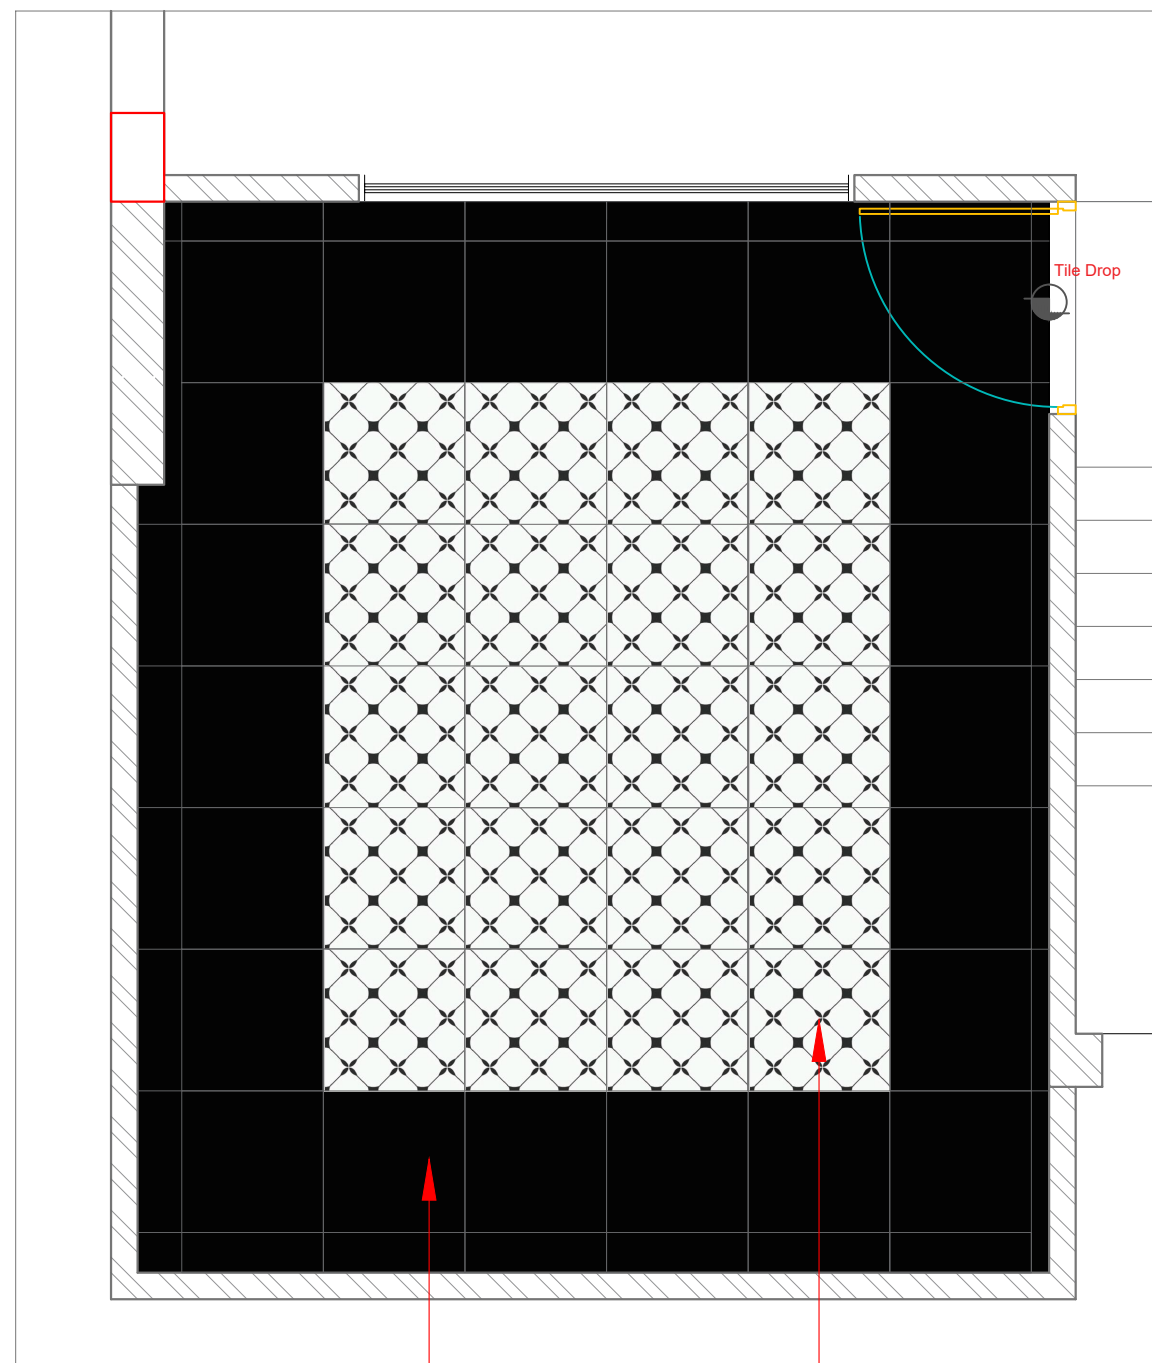

PLAIN BLACK MATT

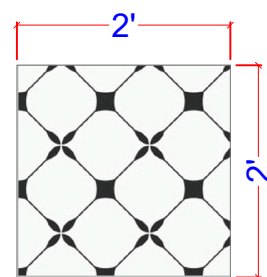

STENCIL CLASSIC

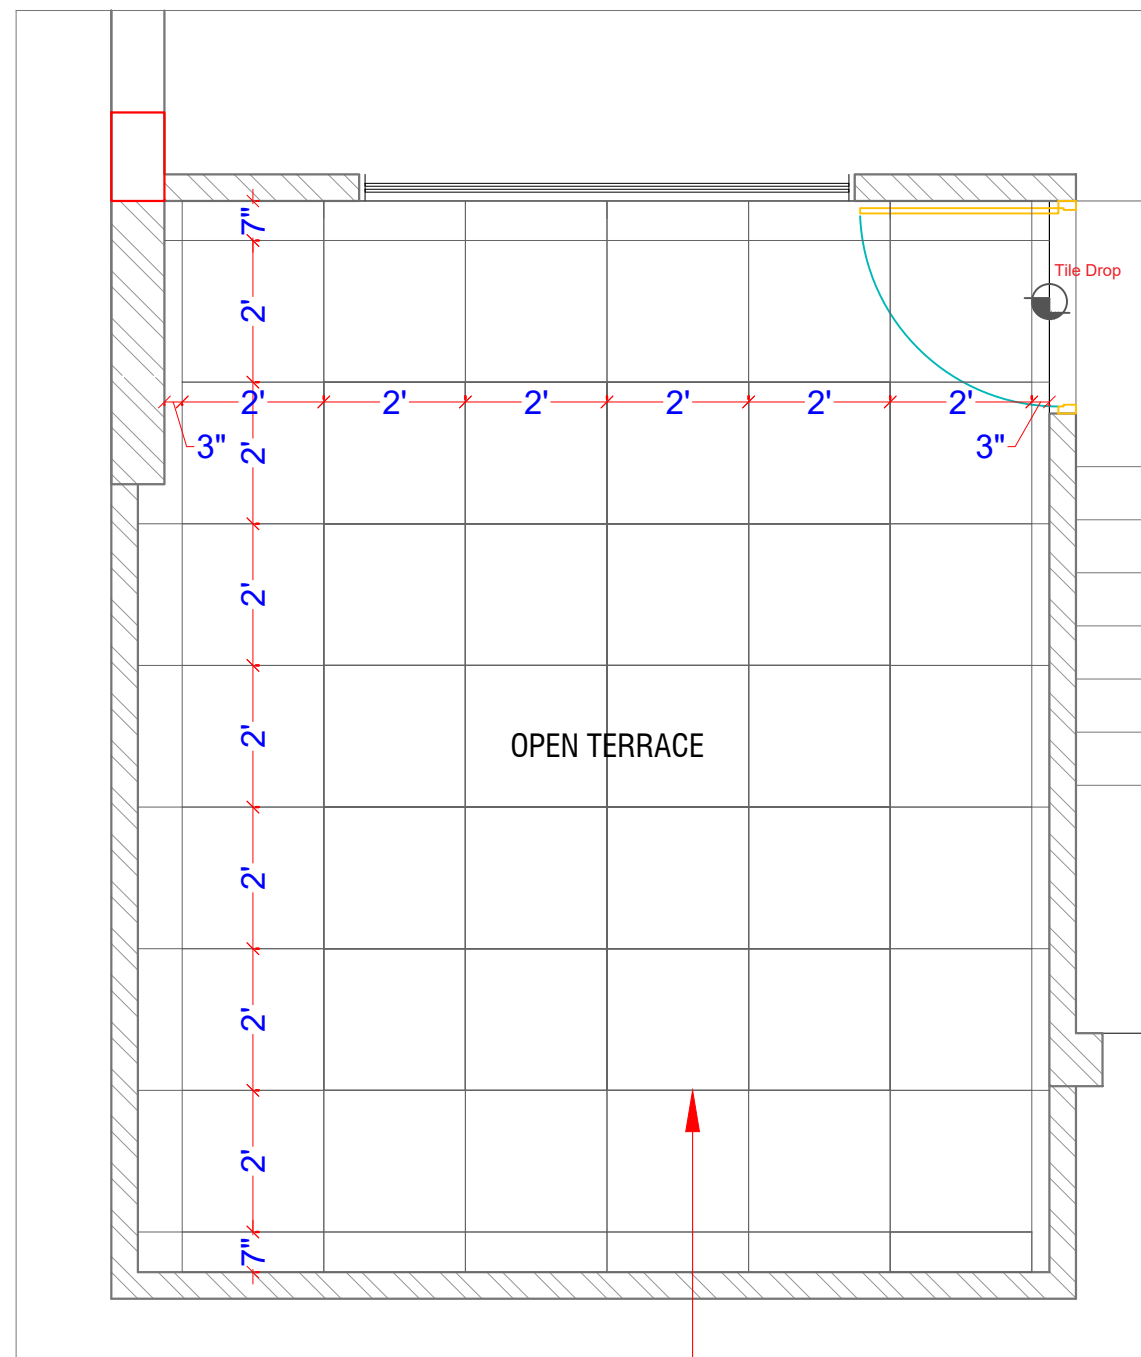

4mm x 4mm groove
in horizontal and
verticle joints

NOTES:

- * DO NOT SCALE THE DRAWING.
- * ALL DIMENSIONS ARE IN FEET \ INCHES.
- * ANY DISCREPENCY IN THE DRAWING TO BE BROUGHT IN THE DESIGNER'S NOTICE BEFORE IMPLEMENTATION ON SITE.

DRAWING TITLE :

SECOND FLOOR
TERRACE FLOORING LAYOUT

SITE ADDRESS:

SAVAD
VADODARA

CLIENT NAME:

RONAK PANCHOLI

DATE:

02-06-2025

NORTH:



DRAWING DETAIL

REVISION NO.	R1	R2	R3
REVISED DATE:	20-11-2025		
SCALE:	N.T.S		
DRAWN BY:	ARCHANA		
CHECKED BY:	MITTAL		

	www.mayaspace.studio
	mayaspace.studio@gmail.com
	+918980144077
	@mayaspace.studio

