

NOTES:

- DO NOT SCALE THE DRAWING.
- ALL DIMENSIONS ARE IN FEET \ INCHES.
- ANY DISCREPANCY IN THE DRAWING TO BE BROUGHT IN THE DESIGNERS NOTICE BEFORE IMPLEMENTATION ON SITE.

DRAWING TITLE :

MASTER 1 ATT,
TOILET DETAILS

SITE ADDRESS:

VADODARA

CLIENT NAME:

MR. PARTH GANDHI

DATE:

02-06-2025

NORTH:



DRAWING DETAIL

REVISION NO.

R1 R2 R3

REVISED DATE:

06-09-2025

SCALE:

N.T.S

DRAWN BY:

PRASANNA

CHECKED BY:


MITTAL

www.mayaspace.studio

mayaspace.studio@gmail.com

+918980144077

@mayaspace.studio

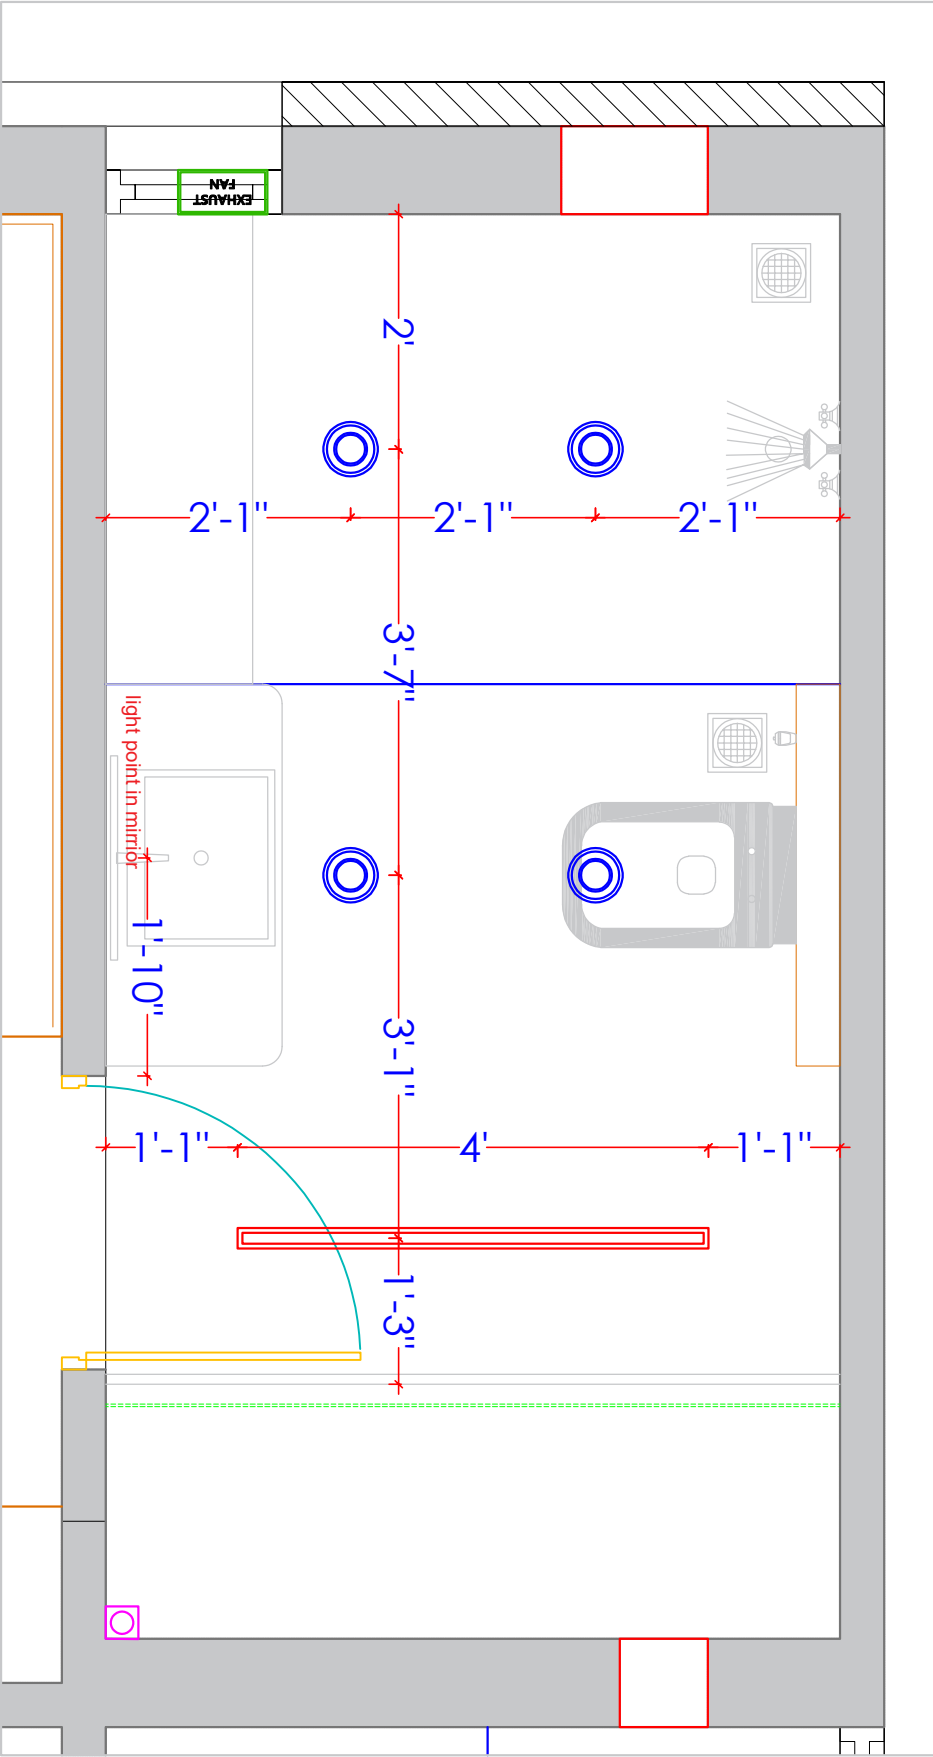

PULMBING LAYOUT

MASTER ROOM ATT. TOILET